SMOKE VENT CALCULATION (NOT FOR FSD APPROVAL) :

(COMPARTMENT (B3–1) + (B2–1))

AREA REFER DWG. NO. A/GBP/35)

NO.	SIZE		TOTAL
VB3–1	1.000 X 2.180	= 2.180 s.m.	17.788 s.m.
VB3–2	1.000 X 1.455	= 1.455 s.m.	
VB3–3	1.100 X 1.600	= 1.760 s.m.	
VB3–4	5.300 X 1.025	= 5.433 s.m.	
VB3–5	1.200 X 2.250	= 2.700 s.m.	
VB3–6	2.130 X 1.000	= 2.130 s.m.	
VB3–7	2.130 X 1.000	= 2.130 s.m.	

CAR PARK SPACE (2.5mx5.0mx2.4m HEADROOM)		PROVIDE			
RESIDENTIAL	R01 – R102	102	122 Nos.	M–EV	EV
VISITOR	V01 – V20*	20##		3#	71
				6#	14
MOTOR CYCLE PARKING SPACE (1.0mx2.4mx2.4m HEADROOM)					
RESIDENTIAL	RM01 – RM13	13 Nos.			

(NOT LESS THAN 30% OF THE PARKING SPACES PROVIDED)
(CARPARK NO. V18, V19 & V20 PROVIDED AT BASEMENT 2 CARPARK)
* V01 – V20 SHALL BE DESIGNATED AS "COMMON AREA" IN DEED OF MUTUAL COVENANT "DMC" OR SUB–DEED OF MUTUAL COVENANT "SUB–DMC" (IF ANY)

SMOKE VENT AREA CALCULATION :

COMPARTMENT FLOOR AREA = 3533.488 m²
SMOKE OUTLET AREA REQ. = 3533.489 x 0.5% = 17.667 m²
SMOKE OUTLET AREA PROV. = 17.788 m² > 17.667 m²

NOTES:

ALL SMOKE VENT ENCLOSURE TO BE –/240/240 FRR

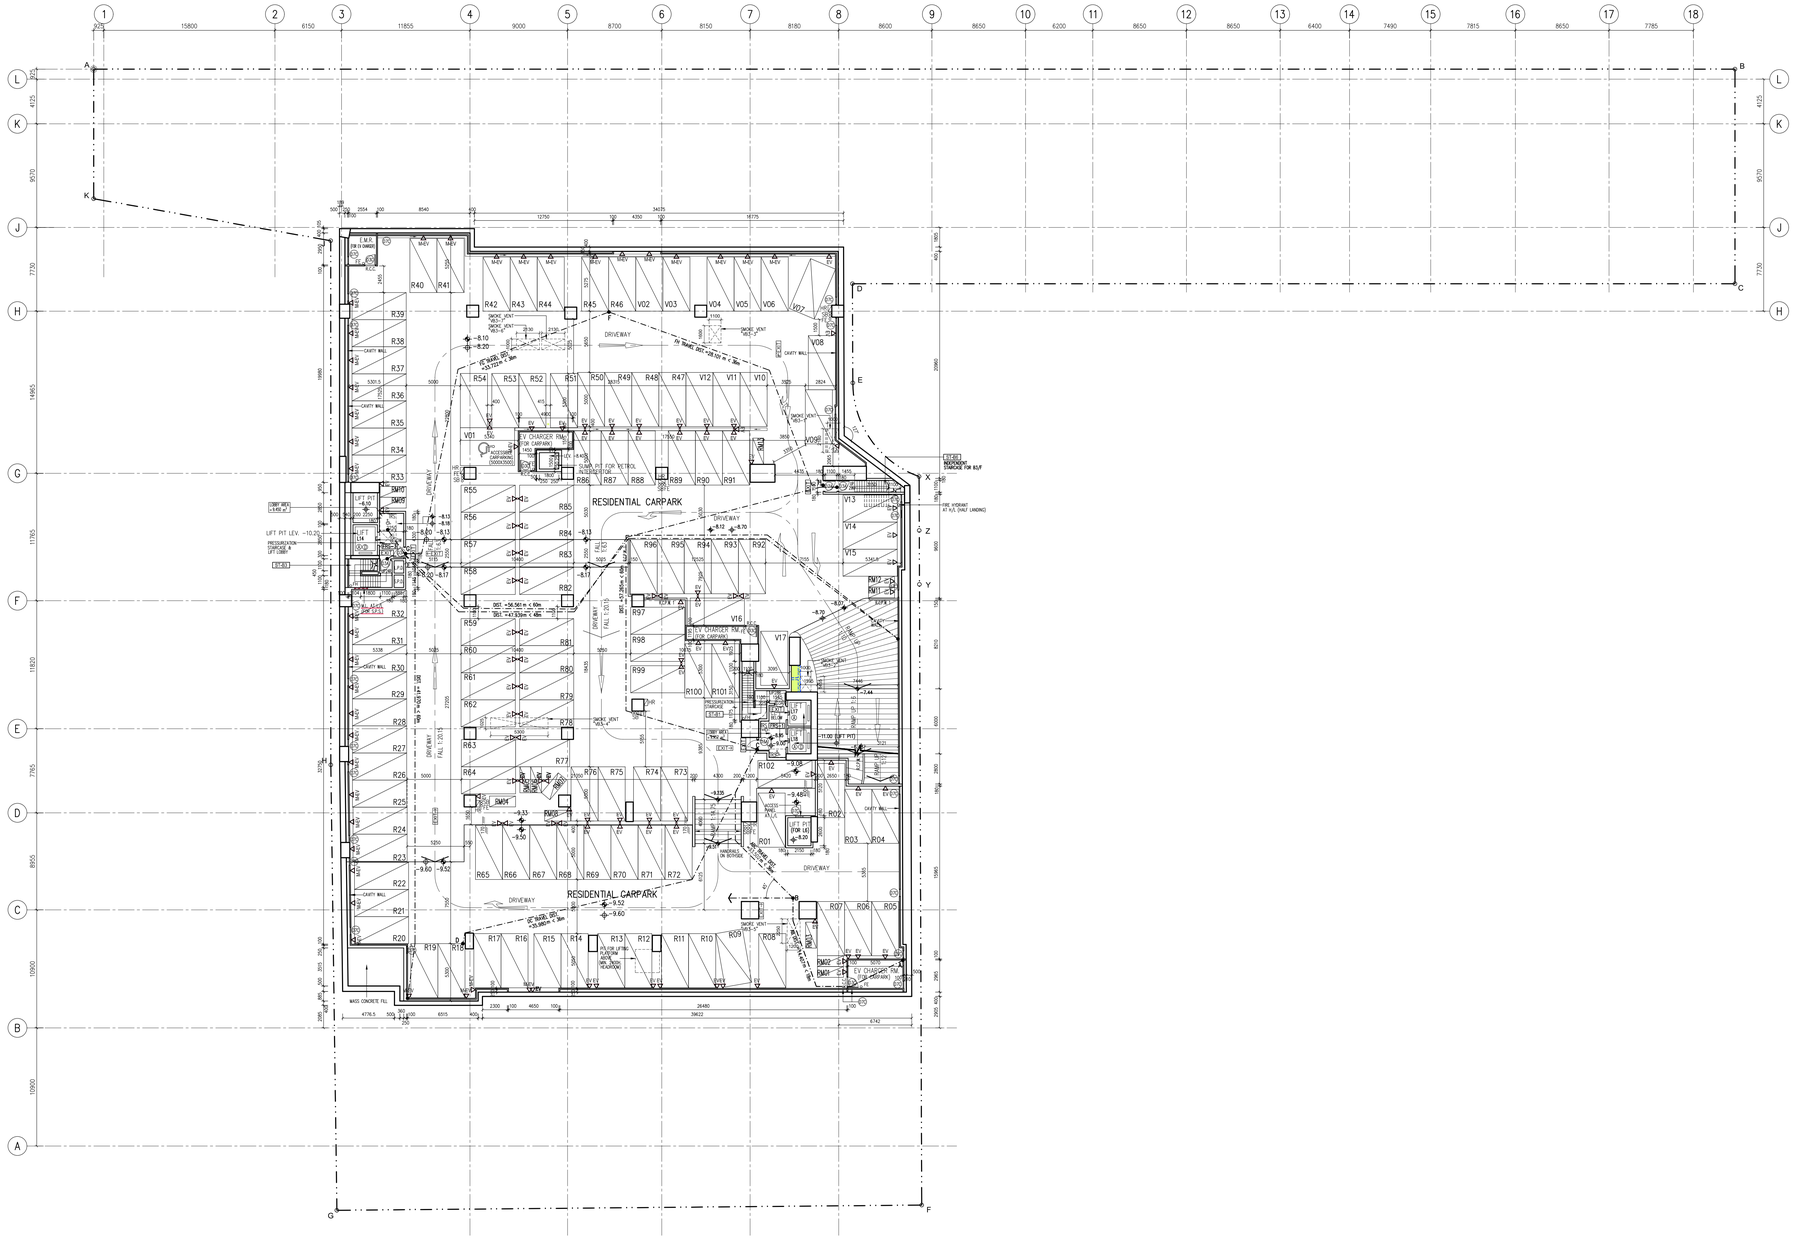

SMOKE VENT CALCULATION (NOT FOR FSD APPROVAL) :

(COMPARTMENT (B2-3) + (B1-1))

AREA REFER DWG. NO. A/GBP/35)

NO.	SIZE		TOTAL
VB2-1	2.130 X 1.100	= 2.343 s.m.	23.628
VB2-2	2.535 X 1.000	= 2.535 s.m.	
VB2-3	2.000 X 1.000	= 2.000 s.m.	
VB2-4	4.000 X 1.000	= 4.000 s.m.	
VB2-5	4.000 X 1.000	= 4.000 s.m.	
VB2-6	3.650 X 1.000	= 3.650 s.m.	
VB2-7	1.000 X 1.000	= 1.000 s.m.	
VB2-8	1.000 X 1.000	= 1.000 s.m.	
VB2-9	1.000 X 1.000	= 1.000 s.m.	
VB2-10	2.100 X 1.000	= 2.100 s.m.	

COMPARTMENT FLOOR AREA = 4693.743 m²
SMOKE OUTLET AREA REQ. = 4693.743 x 0.5% = 23.469 m²
SMOKE OUTLET AREA PROV. = 23.628 m² > 23.469 m²

(COMPARTMENT (B2-2)

AREA REFER DWG. NO. A/GBP/35)

NOTE : DYNAMIC SMOKE EXTRACTION TO BE PROVIDED.

NO.	SIZE		TOTAL
VB2-11	1.000 X 1.000	= 1.000 s.m.	2
VB2-12	1.000 X 1.000	= 1.000 s.m.	

FIRE COMPARTMENT VOLUME = 3773.697 m³
SMOKE OUTLET Nos. REQ. = 3773.697 / 3500 = 1.078
SMOKE OUTLET Nos. PROV. = 2 Nos.

NOTES:
ALL SMOKE VENT ENCLOSURE TO BE -/240/240 FRR
ALL S.E.S. A.D. WITHIN THE SAME COMPARTMENT.

PUBLIC PARKING SPACE (2.5mx5.0mx2.4m HEADROOM)		PROVIDE		
	P001 – P100	100* Nos.	M-EV	EV
			30#	70
PUBLIC MOTOR CYCLE PARKING SPACE (1.0mx2.4mx2.4m HEADROOM)				
	PM01 – PM20	20 Nos.	6#	14

* (INCLUDED 2 NOS. ACCESSIBLE PARKING SPACE CARPARK WHICH SHALL BE DESIGNATED AS "COMMON AREA" IN DEED OF MUTUAL COVENANT "DMC" OR SUB-DEED OF MUTUAL COVENANT "SUB-DMC" (IF ANY)

(NOT LESS THAN 30% OF THE PARKING SPACES PROVIDED)

RETAIL CAR PARK SPACE (2.5mx5.0mx2.4m HEADROOM)		PROVIDE		
	C201 – C246	46* Nos.	M-EV	EV
			14#	32
LOADING/UNLOADING ** (7mx3.5mx3.6m HEADROOM)				
RESIDENTIAL	LG01 – LG04	4 Nos.		
NON-INDUSTRIAL	LG05 – LG11	7 Nos.		

* (INCLUDED 2 NOS. ACCESSIBLE PARKING SPACE CARPARK WHICH SHALL BE DESIGNATED AS "COMMON AREA" IN DEED OF MUTUAL COVENANT "DMC" OR SUB-DEED OF MUTUAL COVENANT "SUB-DMC" (IF ANY)

(NOT LESS THAN 30% OF THE PARKING SPACES PROVIDED)

** LOADING/UN-LOADING SPACE WHICH SHALL BE DESIGNATED AS "COMMON AREA" IN DEED OF MUTUAL COVENANT "DMC" OR SUB-DEED OF MUTUAL CONVENT "SUB-DMC" (IF ANY)

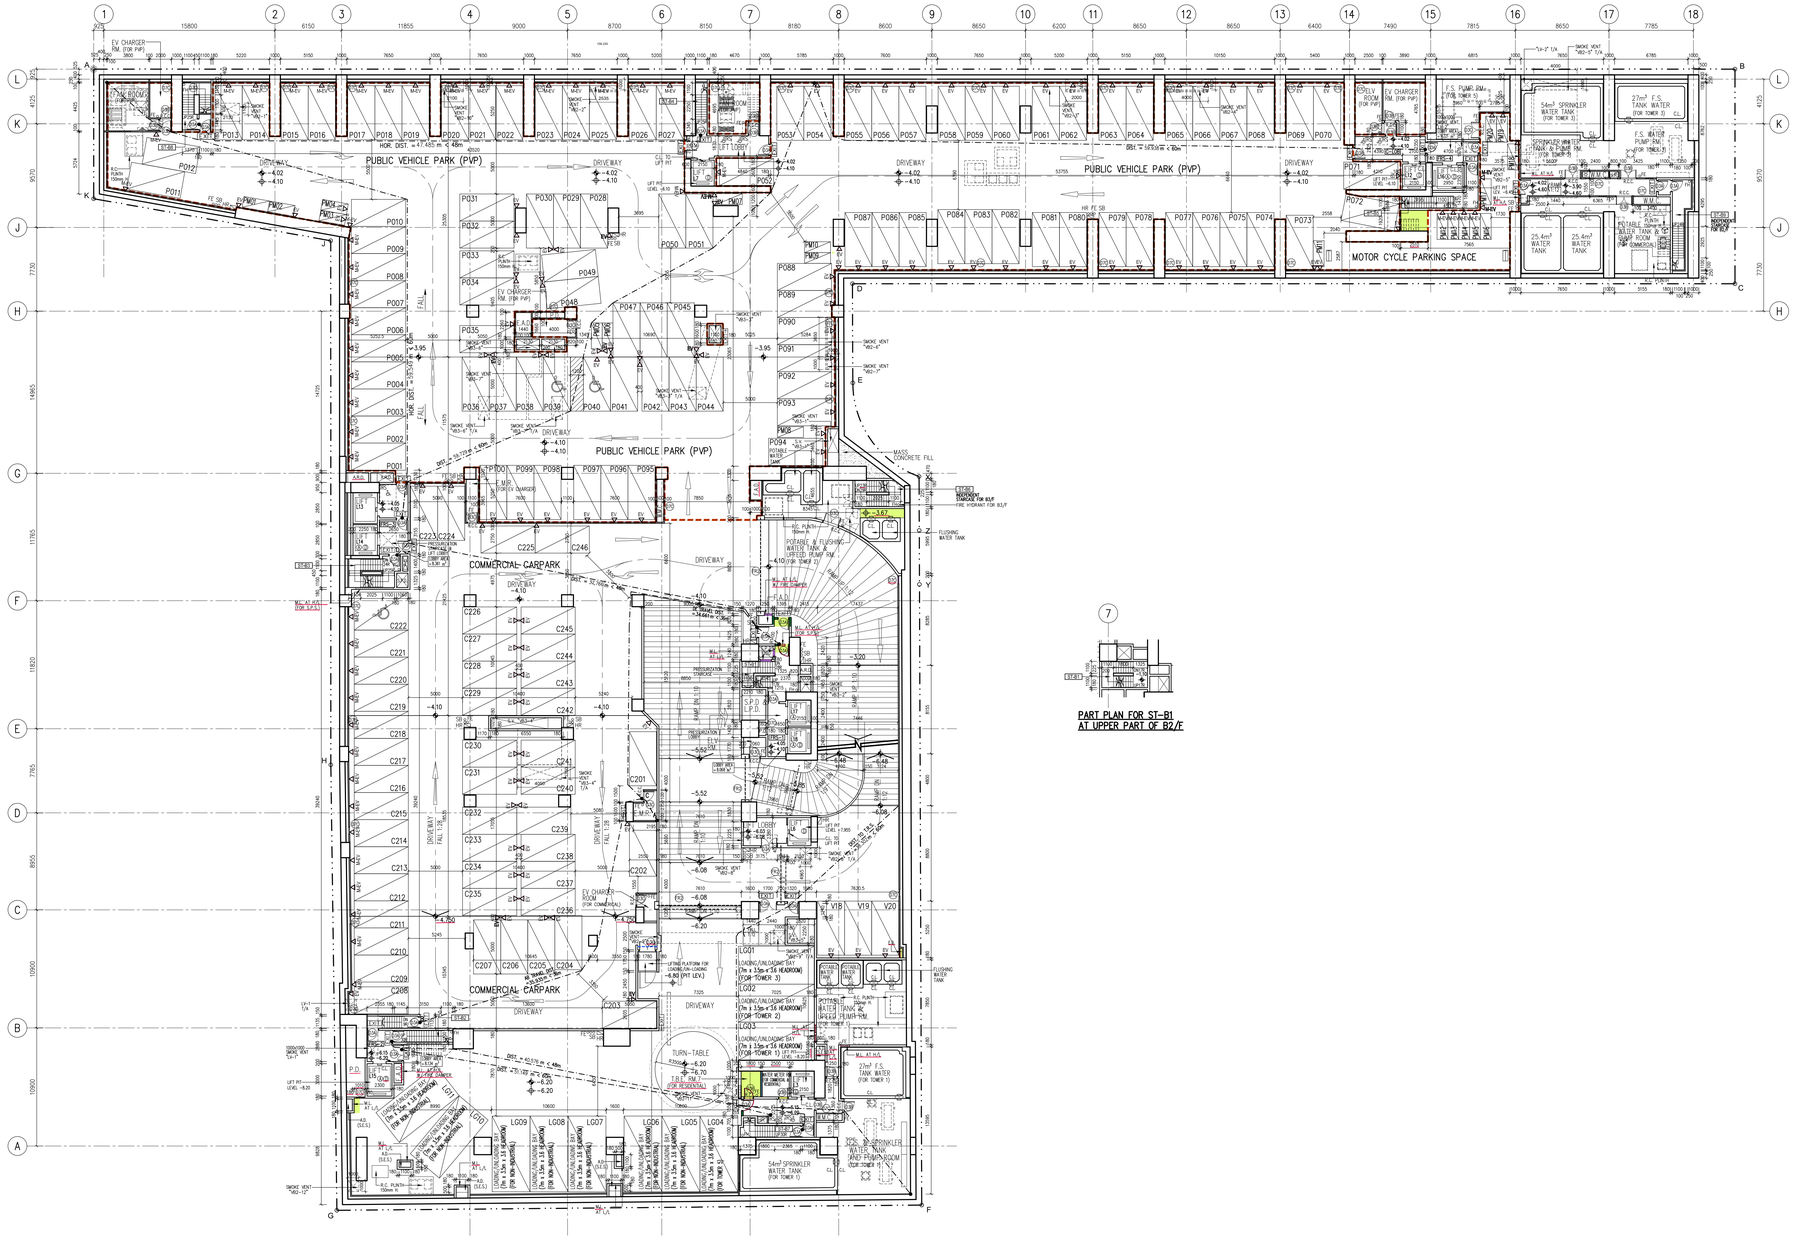

7

PART PLAN FOR ST-B1 AT UPPER PART OF B2/F

BASEMENT 2 FLOOR PLAN

LEGEND :

△ EV — CARPARKING SPACES & MOTORCYCLE PARKING SPACES TO BE PROVIDED AND INSTALLED CHARGING FACILITIES FOR ELECTRIC VEHICLES

△ M-EV — CARPARKING SPACES TO BE PROVIDE AND INSTALL ELECTRIC VEHICLE MEDIUM CHARGER

- - - EXTENT OF "PUBLIC VEHICLE PARK"

PVP PUBLIC VEHICLE PARK

B.D. Ref : 80 2/4024/21

BIM Ref : - --

F.S.D. Ref : - --

D.L.O. Ref : - --

Rev.	Description	Drawn	Checked	Approved	Date
-	1st Submission	WY	AW	AL	07/2022
A	2nd Submission	WY	AW	AL	11/2022
B	1st Amendment	TWM	AW	AL	04/2023
C	2nd Amendment	TWM	AW	AL	12/2023
D	3rd Amendment	TWM	AW	AL	04/2024
D	3rd Amendment (Re-submission)	TWM	AW	AL	05/2024
E	5th Amendment	TWM	AW	AL	12/2024
E	5th Amendment (Re-submission)	TWM	AW	AL	02/2025
F	7th Amendment	LKM	AW	AL	03/2025
G	8th Amendment	TWM	AW	AL	05/2025
H	9th Amendment	TWM	AW	AL	08/2025
H	9th Amendment (Re-submission)	TWM	AW	AL	10/2025
I	11th Amendment	TWM	AW	AL	2/2026

Type II works
The works shown on these plans are Type II works (Building Amendment) in respect of which consent is applied for the purpose of Fast Track consent application under regulation 33 of the Building (Administration) Regulations.

RONALD LU & PARTNERS

呂元祥建築師事務所

Check all measurements on site. Do not scale off drawings.
This drawing is to be read in conjunction with the specification and any other relevant drawings and documentation for the project.
This drawing remains the copyright property of the Architect and is not to be reproduced in whole or in part without permission of the Architect.

Project Title :
PROPOSED DEVELOPMENT
AT BAILEY STREET
& WING KWONG STREET
TO KWA WAN, KOWLOON

Drawing Title :
BASEMENT 2 FLOOR PLAN

Drawn By	TWM	Date	08/2025
Checked By	AW	Date	08/2025
Approved By	AL	Date	08/2025
Project No.	21163KL	Issue Date	08/2025

File Path : J:\Bim Proj\21163KL\Bim Sheet\01 Proj Area\Dwg\BASEMENT 2 FLOOR.dwg

Scale 1:200 By CAD

Drawing Number : A/GBP/04

Revision Number : I

Drawing Purpose

Buildings Department
Amended Plan

Digitally signed by LEUNG Kit Man Andy
APCA (BOR)
16 March 2026

Received on
16 March 2026

Plan Approved
(Digitally Signed)
TSOI Lap-san, Lapson
Senior Building Surveyor
for BUILDING AUTHORITY
17 March 2026

Note: This plan has been processed on a curtailed check basis under the centralized processing system as promulgated in PNAP ADM-19. The duties of the authorized person, registered structural engineer and/or registered geotechnical engineer concerned as specified under section 4(3)(b) and the provision of section 14(2)(c) of the Buildings Ordinance are of particular relevance in this regard.

SMOKE VENT CALCULATION (NOT FOR FSD APPROVAL):

(COMPARTMENT (B1-4))

AREA REFER DWG. NO. A/GBP/35)

NOTE : DYNAMIC SMOKE EXTRACTION TO BE PROVIDED.

NO.	SIZE		TOTAL
VB1-1	1.000 X 1.000	= 1.000 s.m.	4
VB1-2	1.000 X 1.000	= 1.000 s.m.	
VB1-3	1.000 X 1.000	= 1.000 s.m.	
VB1-4	1.000 X 1.000	= 1.000 s.m.	

SMOKE VENT AREA CALCULATION :

FIRE COMPARTMENT VOLUME = 11185.375 m^3

SMOKE OUTLET Nos. REQ. = 11185.375 / 3500 = 3.196

SMOKE OUTLET Nos. PROV. = 4 Nos.

(COMPARTMENT (B2-4) + (B1-6) + (G-9) + (B1-2))

AREA REFER DWG. NO. A/GBP/35)

NO.	SIZE		TOTAL
VB1-11	1.000 X 2.150	= 2.150 s.m.	9.050
VB1-12	1.900 X 1.000	= 1.900 s.m.	
VB1-13	1.000 X 1.000	= 1.000 s.m.	
VB1-14	1.000 X 1.500	= 1.500 s.m.	
VB1-15	1.000 X 1.000	= 1.000 s.m.	
VB1-16	1.000 X 1.500	= 1.500 s.m.	

SMOKE VENT AREA CALCULATION :

COMPARTMENT FLOOR AREA = 1699.560 m^2

SMOKE OUTLET AREA REQ. = 1699.560 x 0.5% = 8.498 m^2

SMOKE OUTLET AREA PROV. = 9.050 m^2 > 8.498 m^2

(COMPARTMENT (B1-3))

AREA REFER DWG. NO. A/GBP/35)

NOTE : DYNAMIC SMOKE EXTRACTION TO BE PROVIDED.

NO.	SIZE		TOTAL
VB1-21	1.000 X 1.000	= 1.000 s.m.	2
VB1-22	1.000 X 1.000	= 1.000 s.m.	

SMOKE VENT AREA CALCULATION :

FIRE COMPARTMENT VOLUME = 3716.416 m^3

SMOKE OUTLET Nos. REQ. = 3716.416 / 3500 = 1.062

SMOKE OUTLET Nos. PROV. = 2 Nos.

(COMPARTMENT (B1-5)

AREA REFER DWG. NO. A/GBP/35)

NO.	SIZE		TOTAL
VB1-31	4.000 X 1.000	= 4.000 s.m.	5.595 s.m.
VB1-32	1.595 X 1.000	= 1.595 s.m.	

SMOKE VENT AREA CALCULATION :

COMPARTMENT FLOOR AREA = 1086.560 m^2

SMOKE OUTLET AREA REQ. = 1086.560 x 0.5% = 5.433 m^2

SMOKE OUTLET AREA PROV. = 5.595 m^2 > 5.433 m^2

NOTES:

ALL SMOKE VENT ENCLOSURE TO BE -/240/240 FRR

ALL S.E.S. A.D. WITHIN THE SAME COMPARTMENT.

			M-EV	EV
COMMERCIAL CAR PARKING SPACE (2.5mx5.0mx2.4m HEADROOM)	C101 – C112	12 Nos.	4 #	8
COMMERCIAL MOTOR CYCLE PARKING SPACE (1.0mx2.4mx2.4m HEADROOM)	CM01 – CM06	6 Nos.	–	6
LOADING/UN-LOADING ** (11mx3.5mx4.7m HEADROOM) / (7mx3.5mx3.6m HEADROOM)				
NON-INDUSTRIAL	HG01 – HG06	6 Nos.	–	
NON-INDUSTRIAL	LG012	1 Nos.	–	

(NOT LESS THAN 30% OF THE PARKING SPACES PROVIDED)

** LOADING/UN-LOADING SPACE WHICH SHALL BE DESIGNATED AS "COMMON AREA" IN DEED OF MUTUAL COVENANT "DMC" OR SUB-DEED OF MUTUAL CONVENT "SUB-DMC" (IF ANY)

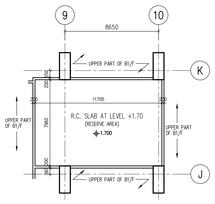

PART PLAN FOR RC SLAB AT LEVEL +1.70 & +0.80

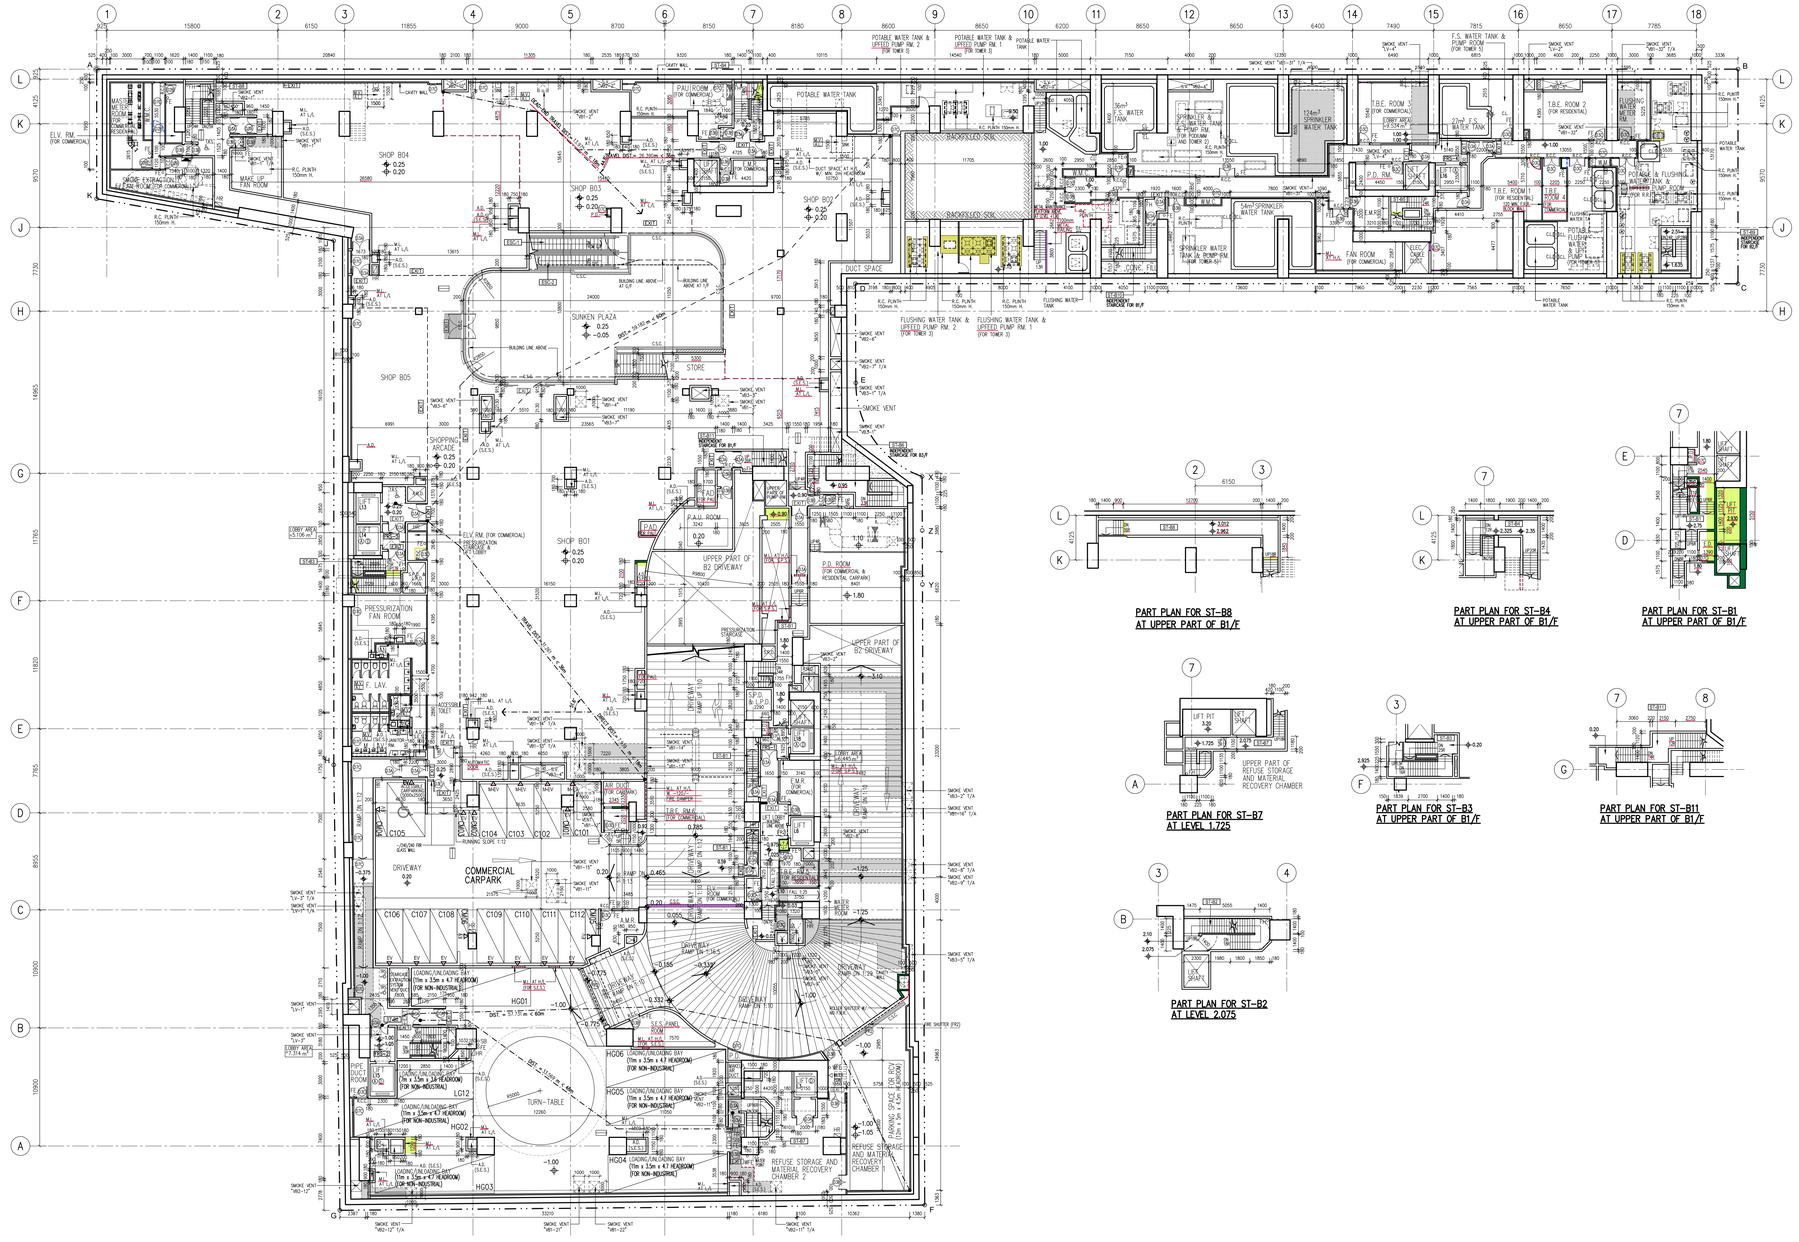
SHOP B04
SHOP B03
SHOP B02
SHOP B05
SHOP B01
SUNKEN PLAZA
SHOPPING ARCADE
P.A.U. ROOM
UPPER PART OF B2 DRIVEWAY
P.D. ROOM (FOR COMMERCIAL & RESIDENTIAL CARPARK)
ELV. RM. (FOR COMMERCIAL)
PRESSURIZATION FAN ROOM
COMMERCIAL CARPARK
DRIVEWAY
DUCT SPACE
STORE
POTABLE WATER TANK
BACKWASH SUMP
SPRINKLER & WATER-TANK PUMP RM. (FOR PODIUM AND TOWER 5)
124m³ SPRINKLER WATER TANK
36m³ F.S. WATER TANK
27m³ F.S. WATER TANK
T.B.E. ROOM 3 (FOR COMMERCIAL)
T.B.E. ROOM 2 (FOR RESIDENTIAL)
T.B.E. ROOM 1 (FOR RESIDENTIAL)
T.B.E. ROOM 4 (FOR COMMERCIAL)
54m³ SPRINKLER WATER TANK
SPRINKLER WATER TANK & PUMP RM. (FOR TOWER 5)
FAN ROOM (FOR COMMERCIAL)
P.D. RM.
FLUSHING WATER TANK & PUMP ROOM (FOR PODIUM)
POTABLE & FLUSHING WATER TANK & PUMP ROOM (FOR PODIUM)
FLUSHING WATER TANK & UPFEED PUMP RM. 2 (FOR TOWER 3)
FLUSHING WATER TANK & UPFEED PUMP RM. 1 (FOR TOWER 3)
SHUTTER
LIFT SHAFT
SMOKE VENT
R.C. PLINTH 150mm H.
A.D. (S.E.S.)
W.L. AT L/A
GANTRY WALL
BUILDING LINE ABOVE
BUILDING LINE ABOVE AT G/F
DUCT SPACE AT W.L. MIN. 2m HEADROOM
LEVEL SLOPED
RUNNING SLOPE 1:12
TURN-TABLE
REFUSE STORAGE AND MATERIAL RECOVERY CHAMBER 1
REFUSE STORAGE AND MATERIAL RECOVERY CHAMBER 2
PARKING SPACE FOR R/V
HG01
HG02
HG03
HG04
HG05
HG06
LG12
C101
C102
C103
C104
C105
C106
C107
C108
C109
C110
C111
C112
V101
V102
LOADING/UNLOADING BAY (11m x 3.5m x 4.7 HEADROOM) [FOR NON-INDUSTRIAL]
LOADING/UNLOADING BAY (7m x 3.5m x 3.6 HEADROOM) [FOR NON-INDUSTRIAL]
LOADING/UNLOADING BAY (7m x 3.5m x 4.7 HEADROOM) [FOR NON-INDUSTRIAL]
LOADING/UNLOADING BAY (7m x 3.5m x 4.7 HEADROOM) [FOR NON-INDUSTRIAL]
LOADING/UNLOADING BAY (7m x 3.5m x 4.7 HEADROOM) [FOR NON-INDUSTRIAL]
LOADING/UNLOADING BAY (7m x 3.5m x 4.7 HEADROOM) [FOR NON-INDUSTRIAL]
SLOPE 1:10
SLOPE 1:8
SLOPE 1:12
SLOPE 1:6.5
SLOPE 1:7
SLOPE 1:8.5
SLOPE 1:10
SLOPE 1:12
SLOPE 1:6
SLOPE 1:7
SLOPE 1:8

WING KWONG STREET
(12.28m WIDTH APPROX.)

MA TAU WAI ROAD
(30.65m WIDTH APPROX.)

BAILEY STREET
(25.82m WIDTH APPROX.)
(MEAN STREET LEVEL +4.650)

WAN ON STREET
(12.17m WIDTH APPROX.)

ADJOINING BUILDING

ADJOINING LOT
(1.1m WIDTH APPROX.)

ADJOINING LOT
(10m WIDTH APPROX.)

PROFILE OF FOOTBRIDGE SUPPORTS AND CONNECTIONS FOR FUTURE FOOTBRIDGE ABOVE (UNDER SEPARATE SUBMISSION)

PUBLIC LANE

PAVEMENT (2.0m WIDTH APPROX.)

PAVEMENT (1.3m WIDTH APPROX.)

PAVEMENT (VAL WIDTH APPROX.)

EXISTING S.T.F.H.

GROUND FLOOR PLAN

LEGEND (UNDER LEASE)

- P – PINK HATCHED BLACK
- G – GREEN
- COVERED LANDSCAPED AREA

LEGEND

- EXIT ROUTE OF REQUIRED STAIRCASE / COVERED PASSAGE OF F.S.A.P.
- TACTILE DIRECTIONAL TILE/BLOCKS
- TACTILE POSITIONAL TILE/BLOCKS
- TACTILE WARNING TILE/BLOCKS

NOTE :

ROOM SHALL BE DESIGNATED AS "COMMON AREA" IN DEED OF MUTUAL COVENANT "DMC"

* HOLD OPEN DOOR DEVICE SHALL COMPLY TO CLAUSE B13.8 OF COP FOR FIRE SAFETY IN BUILDINGS AND TO THE SATISFACTION OF THE DIRECTOR OF FIRE SERVICES.

PART PLAN FOR ST-07 AT UPPER PART OF G/F

PART PLAN FOR ST-11 AT UPPER PART OF G/F

PART PLAN FOR ST-04 & ST-10 AT UPPER PART OF G/F

PART PLAN FOR ST-01 & ST-12 AT UPPER PART OF G/F

PART PLAN FOR ST-02 & ST-03 AT UPPER PART OF G/F

PART PLAN FOR ST-05 AT UPPER PART OF G/F

PART PLAN FOR ST-06 AT UPPER PART OF G/F

PART PLAN FOR ST-09 AT UPPER PART OF G/F

PART PLAN FOR ST-11 AT UPPER PART OF G/F

B.D. Ref : BD 2/4024/21

BIM Ref : - --

F.S.D. Ref : - --

D.L.O. Ref : - --

Rev.	Description	Drawn	Checked	Approved	Date
-	1st Submission	WY	AW	AL	07/2022
A	2nd Submission	WY	AW	AL	11/2022
B	1st Amendment	TWM	AW	AL	04/2023
C	2nd Amendment	TWM	AW	AL	12/2023
D	3rd Amendment	TWM	AW	AL	04/2024
D	3rd Amendment (Re-submission)	TWM	AW	AL	05/2024
E	5th Amendment	TWM	AW	AL	12/2024
E	5th Amendment (Re-submission)	TWM	AW	AL	02/2025
F	8th Amendment	TWM	AW	AL	05/2025
G	9th Amendment	TWM	AW	AL	08/2025
G	9th Amendment (Re-submission)	TWM	AW	AL	10/2025
H	10th Amendment	TWM	AW	AL	12/2025
I	11th Amendment	TWM	AW	AL	02/2026

Type II works
The works shown on these plans are Type II works (Building Amendment) in respect of which consent is applied for the purpose of Fast Track consent application under regulation 33 of the Building (Administration) Regulations.

RONALD LU & PARTNERS

呂元祥建築師事務所

Check all measurements on site. Do not scale off drawings.
This drawing is to be read in conjunction with the specification and any
relevant drawings and other consultants' drawings.
This drawing remains the copyright property of the Architect and is not
to be reproduced in whole or in part without permission of the Architect.

Project Title :
PROPOSED DEVELOPMENT
AT BAILEY STREET
& WING KWONG STREET
TO KIVA WAN, KOWLOON

Drawing Title :
GROUND FLOOR PLAN

Drawn By	TWM	Date	08/2025
Checked By	AW	Date	08/2025
Approved By	AL	Date	08/2025
Project No.	21163KL	Issue Date	08/2025

File Path :
C:\BIM 3Ps_Site\21163KL Bailie Street & Wing Kwong Street\DWG\BASE\GF-1.0-Ground Floor_New Entrance\GF-1.0a GF Bldg

Scale 1:200 By CAD

Drawing Number : A/GBP/06
Revision Number : I

Drawing Purpose
Buildings Department
Amended Plan

Digitally signed by LEUNG Kit Man Andy
APLA | BORD
16 March 2026

Received on
16 March 2026

Plan Approved
(Digitally Signed)
TSOI Lap-san, Lapson
Senior Building Surveyor
for BUILDING AUTHORITY
17 March 2026

Note: This plan has been processed on a curtailed check basis under the centralized processing system as promulgated in PNAP ADM-19. The duties of the authorized person, registered structural engineer and/or registered geotechnical engineer concerned as specified under section 4(3)(b) and the provision of section 14(2)(c) of the Buildings Ordinance are of particular relevance in this regard.

PART PLAN FOR ST-05
AT UPPER PART OF 1/F

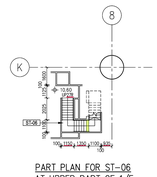

PART PLAN FOR ST-06
AT UPPER PART OF 1/F

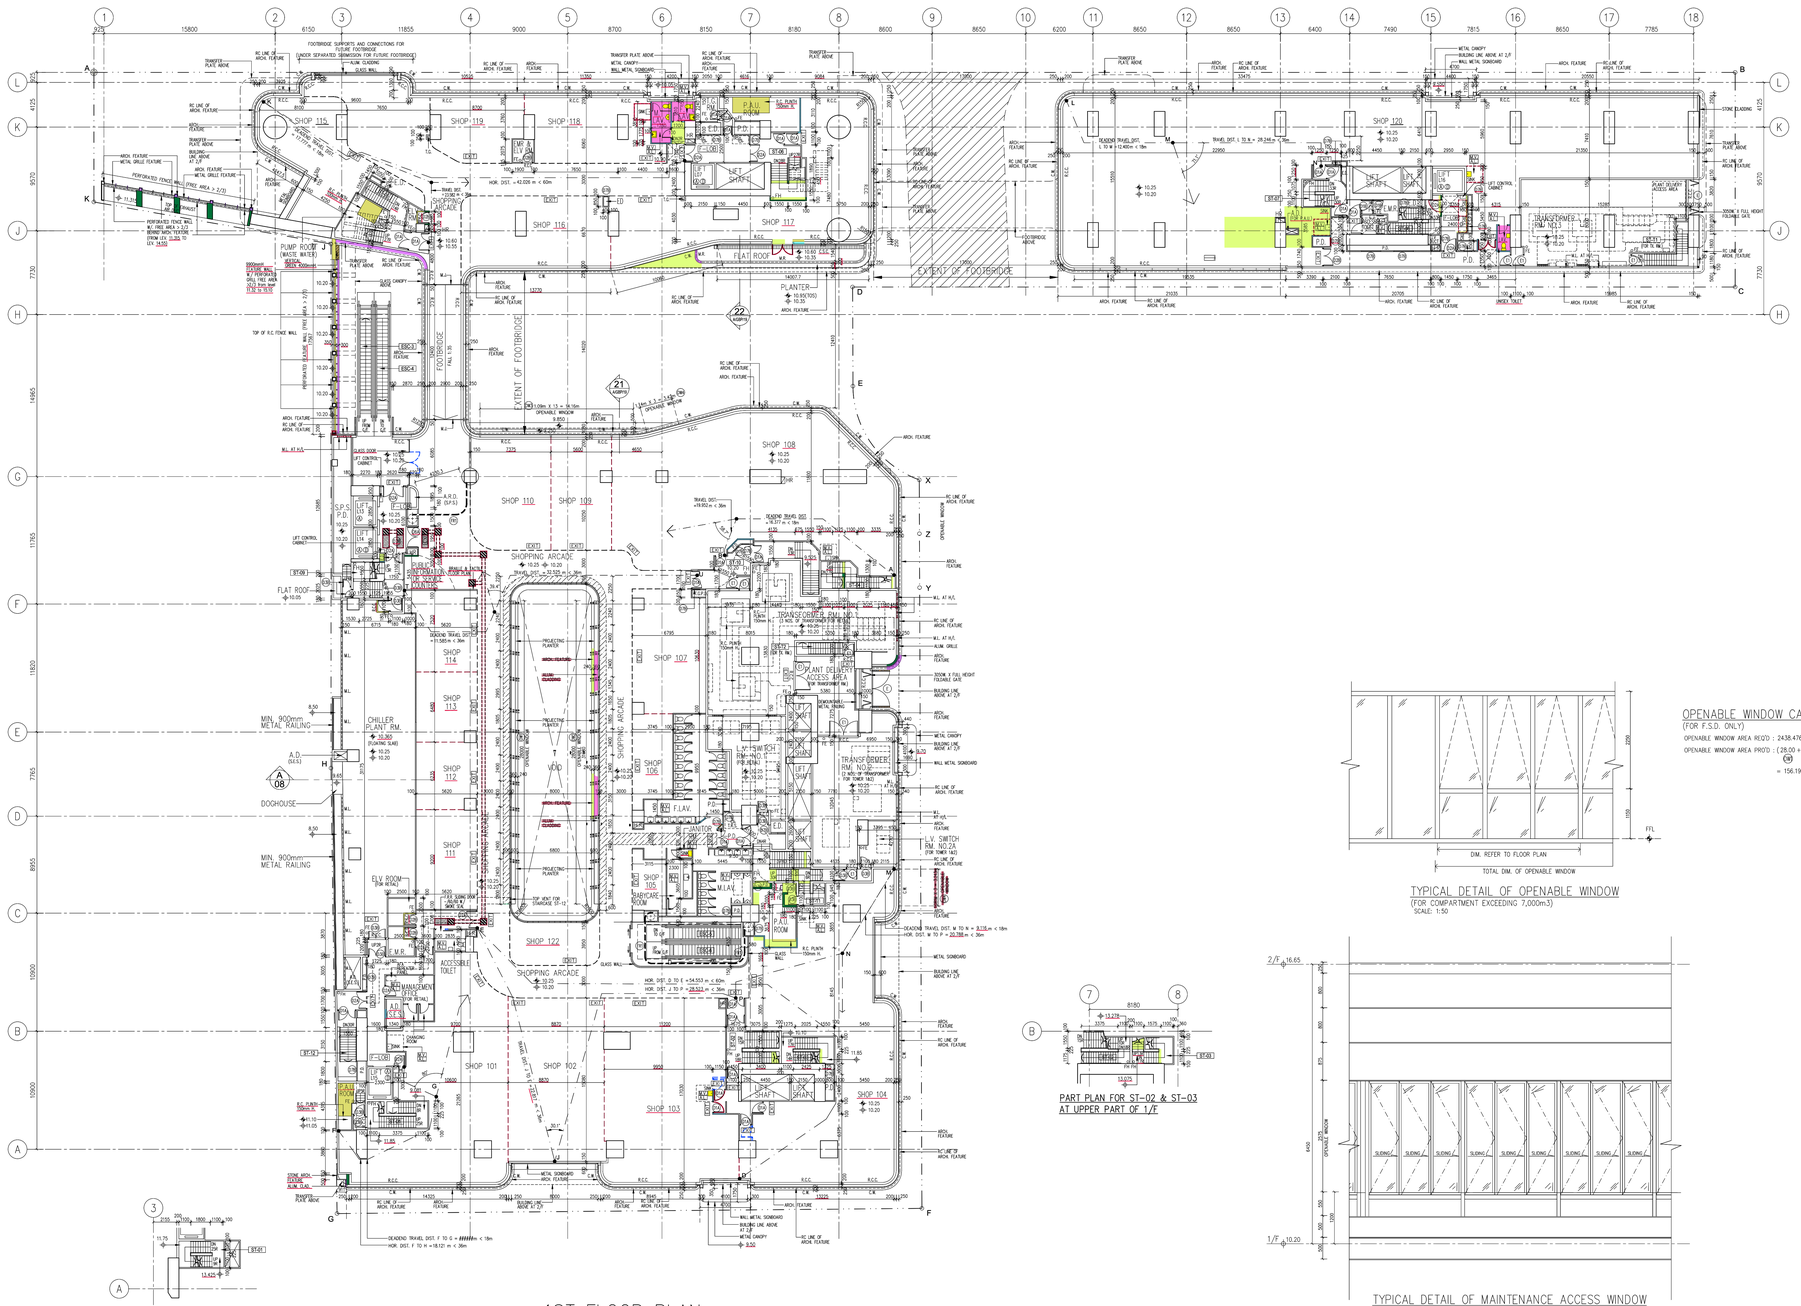
1
2
3
4
5
6
7
8
9
10
11
12
13
14
15
16
17
18
A
B
C
D
E
F
G
H
J
K
L
M
N
X
Y
Z
SHOP 115
SHOP 119
SHOP 118
SHOP 120
SHOP 116
SHOP 117
SHOP 108
SHOP 110
SHOP 109
SHOP 107
SHOP 106
SHOP 105
SHOP 114
SHOP 113
SHOP 112
SHOP 111
SHOP 122
SHOP 101
SHOP 102
SHOP 103
SHOP 104
SHOPPING ARCADE
EXTENT OF FOOTBRIDGE
FOOTBRIDGE SUPPORTS AND CONNECTIONS FOR FUTURE FOOTBRIDGE (UNDER SEPARATED SUBMISSION FOR FUTURE FOOTBRIDGE)
FLAT ROOF
PLANTER
PUMP ROOM (WASTE WATER)
CHILLER PLANT RM.
DOGHOUSE
MIN. 900mm METAL RAILING
ELV ROOM (FOR RETAIL)
MANAGEMENT OFFICE (FOR RETAIL)
ACCESSIBLE TOILET
S.P.S. P.D.
L.V. SWITCH RM. NO.1 (FOR RETAIL)
TRANSFORMER RM. NO.1 (FOR RETAIL)
L.V. SWITCH RM. NO.2A (FOR TOWER 1&2)
TRANSFORMER RM. NO.2 (FOR TOWER 1&2)
PLANT DELIVERY ACCESS AREA (FOR SHOPPING MALL)
LIFT SHAFT
LIFT OVR.
LIFT MACH.
M.V.A.C.
F.S.I.
F.S.D.
A.R.D.
P.D.
M.W.
M.V.F.
FLAV.
JANITOR
SHOPPING ARCADE
OPENABLE WINDOW
TRAVEL DIST. TO N = 28.248 m < 30m
TRAVEL DIST. = 42.026 m < 60m
TRAVEL DIST. TO M = 3.116 m < 18m
HOR. DIST. M TO P = 20.788 m < 35m
TRAVEL DIST. F TO G = 14.121 m < 18m
HOR. DIST. F TO H = 18.121 m < 35m
TRAVEL DIST. = 19.802 m < 30m
TRAVEL DIST. = 16.585 m < 30m
HOR. DIST. = 4.553 m < 60m
HOR. DIST. = 29.522 m < 35m
TRAVEL DIST. = 11.585 m < 30m
TRAVEL DIST. = 32.525 m < 60m
TRAVEL DIST. = 13.278 m < 18m
TRAVEL DIST. = 13.075 m < 18m
RC LINE OF ARCH. FEATURE
ARCH. FEATURE
TRANSFER PLATE ABOVE
METAL CANOPY
BUILDING LINE ABOVE AT 2/F
WALL METAL SIGNBOARD
STONE CLADDING
ALUM. CLADDING
GLASS WALL
METAL GRILLE FEATURE
PERFORATED FENCE WALL
TOP OF R.C. FENCE WALL
TOP OF R.C. PARAPET WALL
R.C. PLINTH
W.L. AT H.V.
ROOM X FULL HEIGHT FOLDING GATE
300MM X FULL HEIGHT FOLDING GATE
PROJECTING PLANTER
ARCH. FEATURE
METAL SIGNBOARD
BUILDING LINE ABOVE AT 3/F
TOP VENT FOR STAIRCASE ST-12
TOP VENT FOR STAIRCASE ST-13
FIRE ARCH. FEATURE
PLANT ROOM
M.W.
F.S.I.
F.S.D.
P.D.
LIFT CONTROL CABINET
GLASS DOOR
ACCESS LADDER
ST-01
ST-02
PART PLAN FOR ST-05
AT UPPER PART OF 2/F

PART PLAN FOR ST-06
AT LEVEL +17.424

PART PLAN FOR ST-06
AT UPPER PART OF 2/F

PART PLAN FOR ST-07
AT LEVEL +17.10

PART PLAN FOR ST-07
AT UPPER PART OF 2/F

PART PLAN FOR ST-08
AT UPPER PART OF 2/F

PART PLAN FOR ST-01
AT UPPER PART OF 2/F

PART PLAN FOR ST-04
AT UPPER PART OF 2/F

PART PLAN FOR ST-02 & ST-03
AT UPPER PART OF 2/F

PART PLAN FOR POOL DECK
AT LEVEL 15.20

PART SECTION A

2ND FLOOR PLAN

LEGEND

COVERED LANDSCAPED AREA

NOTE :

ROOM SHALL BE DESIGNATED AS "COMMON AREA" IN DEED OF MUTUAL COVENANT "DMC"

B.D. Ref :	80 2/4024/21
BIM Ref :	- --
F.S.D. Ref :	- --
D.L.O. Ref :	- --

Rev.	Description	Drawn	Checked	Approved	Date
-	1st Submission	WY	AW	AL	07/2022
A	2nd Submission	WY	AW	AL	11/2022
B	1st Amendment	TWM	AW	AL	04/2023
C	2nd Amendment	TWM	AW	AL	12/2023
D	3rd Amendment	TWM	AW	AL	04/2024
D	3rd Amendment (Re-submission)	TWM	AW	AL	05/2024
E	5th Amendment	TWM	AW	AL	12/2024
E	5th Amendment (Re-submission)	TWM	AW	AL	02/2025
F	8th Amendment	TWM	AW	AL	05/2025
G	9th Amendment	TWM	AW	AL	10/2025
G	9th Amendment (Re-submission)				
H	10th Amendment	TWM	AW	AL	12/2025
I	11th Amendment	TWM	AW	AL	02/2026

Type II works
(The works shown on these plans are Type II works (Building Amendment) in respect of which consent is applied for the purpose of Fast Track consent application under regulation 39 of the Building (Administration) Regulations.

RONALD LU & PARTNERS

呂元祥建築師事務所

Check all measurements on site. Do not scale off drawings.
This drawing is to be read in conjunction with the specification and any other relevant drawings issued in connection with this project.
This drawing remains the copyright property of the Architect and is not to be reproduced in whole or in part without permission of the Architect.

Project Title :
PROPOSED DEVELOPMENT
AT BAILEY STREET
& WING KWONG STREET
TO KWA WAN, KOWLOON

Drawing Title :
2ND FLOOR PLAN

Drawn By	TWM	Date	08/2025
Checked By	AW	Date	08/2025
Approved By	AL	Date	08/2025
Project No.	21163KL	Issue Date	08/2025

File Path :
J:\BA Proj Data\21163KL Bailey Street\Working\BASE\BIM\21163KL-F-Bailey Street1.rvt:Level 02_P1 2/F Drawing

Scale 1:200 By CAD

Drawing Number : A/GBP/08

Revision Number : I

Drawing Purpose

Buildings Department
Amended Plan

Digitally signed by LEUNG Kit Man Andy
APVA1/BD/83
16 March 2026

Received on
16 March 2026

Plan Approved
(Digitally Signed)
TSOI Lap-san, Lapson
Senior Building Surveyor
for BUILDING AUTHORITY
17 March 2026

Note: This plan has been processed on a curtailed check basis under the centralized processing system as promulgated in PNAP ADM-19. The duties of the authorized person, registered structural engineer and/or registered geotechnical engineer concerned as specified under section 4(3)(b) and the provision of section 14(2)(c) of the Buildings Ordinance are of particular relevance in this regard.

WING KWONG STREET

FACING STREET

TOWER 3

TOWER 5

TOWER 2

TOWER 1

ADJOINING BUILDING

ADJOINING LOT

MA TAU WAI ROAD

WAN ON STREET

BAILEY STREET

UNDER BUILDING (PLANNING) REG. 31
LEVEL OF MAIN ROOF PARAPET : 101.525
LEVEL OF WINDOW SILL AT 3/F : 23.05
REQUIRED LENGTH OF RECTANGULAR PLANE
= (101.525 - 23.05) / 6 = 13.079
RECTANGULAR HORIZONTAL PLANE AREA PROVIDED
= 13.100 x 2.300 = 30.130 > 21 m² (REQUIRED)

UNDER BUILDING (PLANNING) REG. 31
LEVEL OF MAIN ROOF PARAPET : 101.525
LEVEL OF WINDOW SILL AT 3/F : 23.05
REQUIRED LENGTH OF RECTANGULAR PLANE
= (101.525 - 23.05) / 3 = 26.158
RECTANGULAR HORIZONTAL PLANE AREA PROVIDED
= 26.200 x 2.300 =60.260 > 21 m² (REQUIRED)

UNDER BUILDING (PLANNING) REG. 31
LEVEL OF MAIN ROOF PARAPET : 101.525
LEVEL OF WINDOW SILL AT 3/F : 23.05
REQUIRED LENGTH OF RECTANGULAR PLANE
= (101.525 - 23.05) / 4 = 19.619
RECTANGULAR HORIZONTAL PLANE AREA PROVIDED
= 20.00 x 2.300 =46.000 > 21 m² (REQUIRED)

UNDER BUILDING (PLANNING) REG. 31
LEVEL OF FENCE WALL : 101.525
LEVEL OF WINDOW SILL AT 3/F : 23.05
REQUIRED LENGTH OF RECTANGULAR PLANE
= (101.525 - 23.05) / 6 = 9.809
RECTANGULAR HORIZONTAL PLANE AREA PROVIDED
= 9.850 x 2.300 = 22.655 > 21 m² (REQUIRED)

UNDER BUILDING (PLANNING) REG. 31
LEVEL OF MAIN ROOF PARAPET : 101.525
LEVEL OF WINDOW SILL AT 3/F : 23.05
REQUIRED LENGTH OF RECTANGULAR PLANE
= (101.525 - 23.05) / 6 = 13.079 < 15.000
RECTANGULAR HORIZONTAL PLANE AREA PROVIDED
= 13.100 x 2.300 = 30.130 > 21 m² (REQUIRED)

UNDER BUILDING (PLANNING) REG. 31
LEVEL OF MAIN ROOF PARAPET : 101.525
LEVEL OF WINDOW SILL AT 3/F : 23.05
REQUIRED LENGTH OF RECTANGULAR PLANE
= (101.525 - 23.05) / 7.6 = 13.079
RECTANGULAR HORIZONTAL PLANE AREA PROVIDED
= 13.500 x 2.300 = 31.050 > 21 m² (REQUIRED)

UNDER BUILDING (PLANNING) REG. 31
LEVEL OF MAIN ROOF PARAPET : 101.525
LEVEL OF WINDOW SILL AT 3/F : 23.05
REQUIRED LENGTH OF RECTANGULAR PLANE
= (101.525 - 23.05) / 3 = 26.158
RECTANGULAR HORIZONTAL PLANE AREA PROVIDED
= 26.200 x 2.300 =60.260 > 21 m² (REQUIRED)

CALCULATION OF PRESCRIBED WINDOW REFER TO DRAWING No. A/GBP/17

DIAGRAMMATIC SECTION FOR TOWER 5 FLAT M AT 3/F

TOWER 5 — TRANSFER PLATE — 100.00 R/F — 31.750 7/F — 28.50 6/F — 25.250 5/F — 22.00 3/F — BL — 3.250 x 23 STOREYS = 74.750 — 25.250 C/F — 22.00 3/F

3RD FLOOR PLAN

NOTE : 1. ALL FSI ON 3RD FLOOR OF TOWERS SHALL REFER TO TYPICAL FLOOR PLANS.

B.D. Ref :	BD 2/4024/21
BIM Ref :	- --
F.S.D. Ref :	- --
D.L.O. Ref :	- --

Rev.	Description	Drawn	Checked	Approved	Date
-	1st Submission	WY	AW	AL	07/2022
A	2nd Submission	WY	AW	AL	11/2022
B	1st Amendment	TWM	AW	AL	04/2023
C	2nd Amendment	TWM	AW	AL	12/2023
D	3rd Amendment	TWM	AW	AL	04/2024
D	3rd Amendment (Re-submission)	TWM	AW	AL	05/2024
E	5th Amendment	TWM	AW	AL	12/2024
E	5th Amendment (Re-submission)	TWM	AW	AL	02/2025
F	6th Amendment	TWM	AW	AL	02/2025
G	8th Amendment	TWM	AW	AL	05/2025
H	9th Amendment	TWM	AW	AL	08/2025
H	9th Amendment (Re-submission)	TWM	AW	AL	10/2025
I	10th Amendment	TWM	AW	AL	12/2025
J	11th Amendment	TWM	AW	AL	02/2026
K	13th Amendment	TWM	AW	AL	06/2026

Type II works
The works shown on these plans are Type II works (Building Amendment) in respect of which consent is applied for the purpose of Fast Track consent application under regulation 33 of the Building (Administration) Regulations.

RONALD LU & PARTNERS

呂元祥建築師事務所

Check all make-ups/dimensions on site. Do not scale off drawings.
This drawing is to be read in conjunction with the specification and any other drawings and written instructions issued.
This drawing remains the copyright property of the Architect and is not to be reproduced in whole or in part without permission of the Architect.

Project Title :
PROPOSED DEVELOPMENT
AT BAILEY STREET
& WING KWONG STREET
TO KWA WAN, KOWLOON

Drawing Title :
3RD FLOOR PLAN

Drawn By	TWM	Date	08/2025
Checked By	AW	Date	08/2025
Approved By	AL	Date	08/2025
Project No.	21163KL	Issue Date	08/2025

File Path :
I:\Bldg Proj_Dwg\2021\21KL Bailey Street & Wing Kwong Street\DWG\BD\BD\BD\3F 15 Hard Area\P1_3/F_3F.dwg

Scale 1:200 By CAD

Drawing Number : A/GBP/09
Revision Number : K

Drawing Purpose
Buildings Department
Amended Plan

Digitally signed by WONG Chi Kin Kenneth
APAU 19/55
08 July 2026

Received on
08 July 2026

Plan Approved
(Digitally Signed)
TSOI Lap-san, Lapson
Senior Building Surveyor
for BUILDING AUTHORITY
08 July 2026

Note: This plan has been processed on a curtailed check basis under the centralized processing system as promulgated in PNAP ADM-19. The duties of the authorized person, registered structural engineer and/or registered geotechnical engineer concerned as specified under section 4(3)(b) and the provision of section 14(2)(c) of the Buildings Ordinance are of particular relevance in this regard.

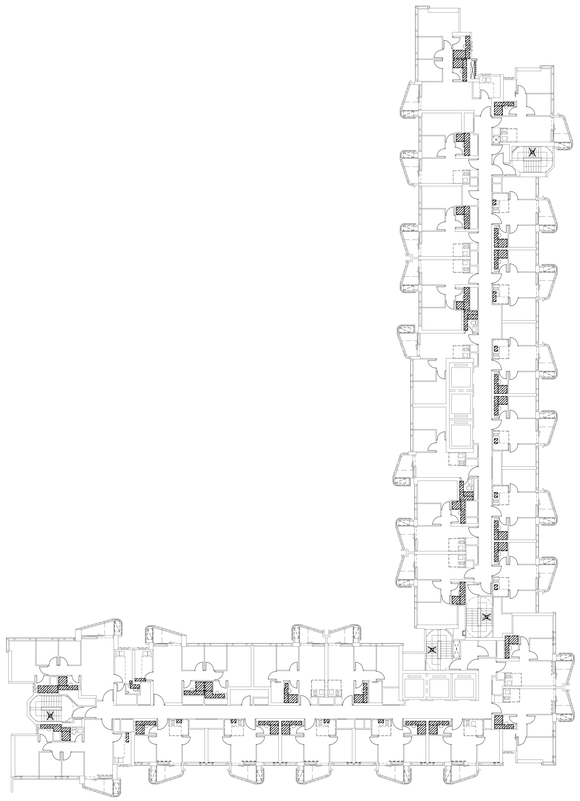

DIAGRAM OF SUNKEN SLAB EXTENT (5th TO 30th FLOOR)

SCALE 1:200

LEGEND:

SUNKEN SLAB

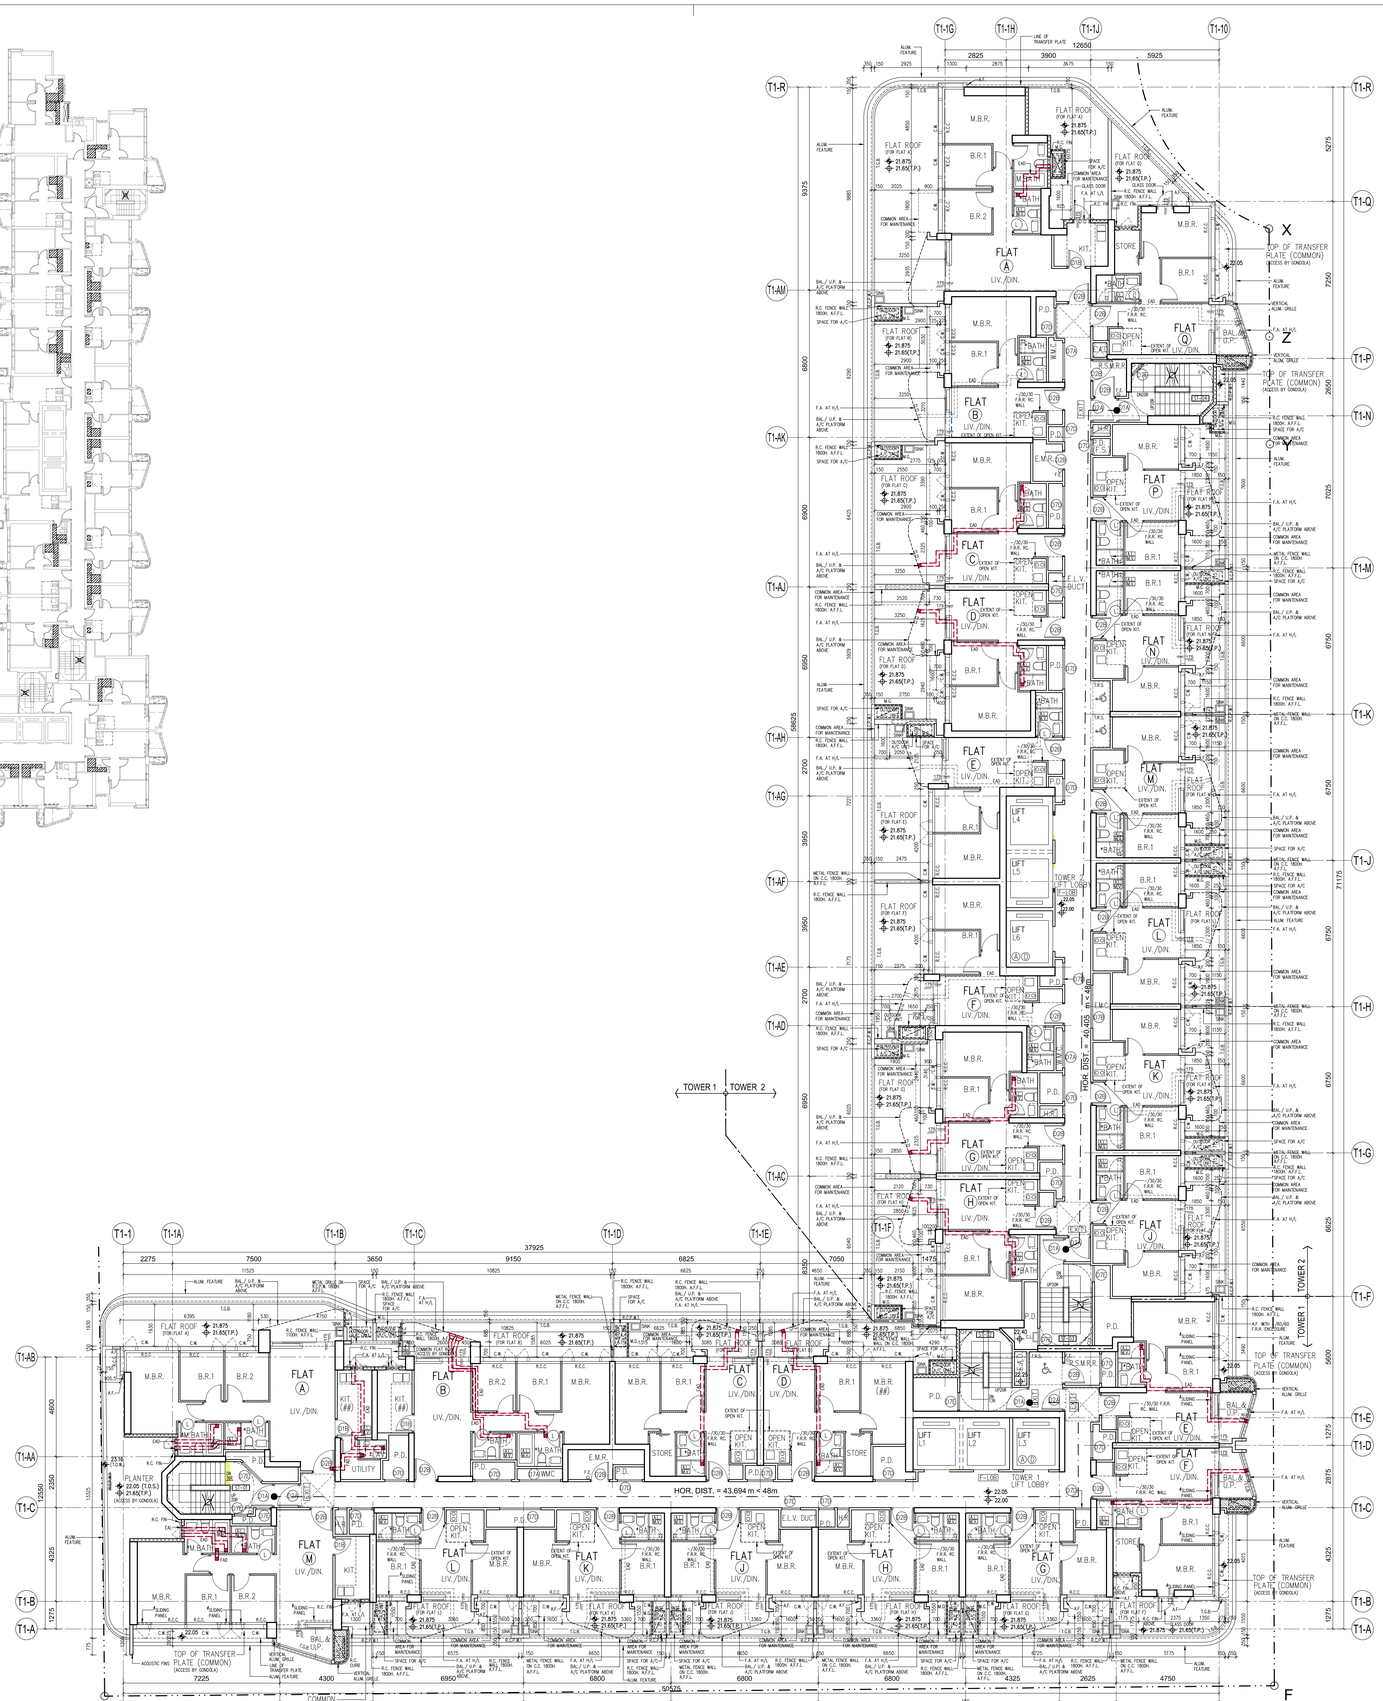

3RD FLOOR PLAN – TOWER 1 & TOWER 2

NOTE:

1. MECHANICAL VENTILATION AND ARTIFICIAL LIGHTING WILL BE PROVIDED AT THE BATHROOM/ LAVATORY MARKED WITH "*" FOR OMISSION OF NATURAL LIGHTING AND VENTILATION.
2. ALL DIMENSION ARE SAME AS 5/F – 30/F, EXCEPT OTHERWISE NOTED.
3. SLIDING PANEL TO BE PROVIDED AT WHICH MARKED WITH "ƒ" (REFER TO SLIDING PANEL SCHEDULE DWG. NO. A/GBP/11)
4. LIGHTING AND VENTILATION PROVISION TO ADOPT PERFORMANCE-BASED APPROACH FOR THE ROOM MARKED WITH (##) (REFER DWG. NO. A/GBP/10, A/GBP/10.1)
5. 5 ACH MECHANICAL VENTILATION SHALL BE PROVIDED TO KITCHENS USING UVA METHOD.

LEGEND:

NON-STRUCTURAL PREFABRICATE EXTERNAL WALL (THICKNESS MAX. 150mm)

COMMON AREA FOR MAINTENANCE

A/C PLATFORM

B.D. Ref : BD 2/4024/21

BIM Ref : - --

F.S.D. Ref : - --

D.L.O. Ref : - --

Rev.	Description	Drawn	Checked	Approved	Date
-	1st Submission	WY	AW	AL	07/2022
A	2nd Submission	WY	AW	AL	11/2022
B	1st Amendment	TWM	AW	AL	04/2023
C	2nd Amendment	TWM	AW	AL	12/2023
D	3rd Amendment	TWM	AW	AL	04/2024
D	3rd Amendment (Re-submission)	TWM	AW	AL	05/2024
E	5th Amendment	TWM	AW	AL	12/2024
E	5th Amendment (Re-submission)	TWM	AW	AL	02/2025
F	6th Amendment	TWM	AW	AL	02/2025
G	7th Amendment	TWM	AW	AL	05/2025
H	9th Amendment	TWM	AW	AL	08/2025
H	9th Amendment (Re-submission)	TWM	AW	AL	10/2025
I	10th Amendment	TWM	AW	AL	12/2025
J	11th Amendment	TWM	AW	AL	02/2026

Type II works

The works shown on these plans are Type II works (Building Amendment) in respect of which consent is applied for the purpose of Fast Track consent application under regulation 35 of the Building (Administration) Regulations.

RONALD LU & PARTNERS

呂元祥建築師事務所

Check all measurements on site. Do not scale off drawings.
This drawing is to be read in conjunction with the specification and any discrepancies are to be immediately reported to the Architect.
This drawing remains the copyright property of the Architect and is not to be reproduced in whole or part without permission of the Architect.

Project Title :

PROPOSED DEVELOPMENT AT BAILEY STREET & WING KWONG STREET TO KWA WAN, KOWLOON

Drawing Title :

3RD FLOOR PLAN FOR TOWER 1 & TOWER 2

Drawn By	TWM	Date	08/2025
Checked By	AW	Date	08/2025
Approved By	AL	Date	08/2025
Project No.	21163KL	Issue Date	08/2025

File Path : I:\Bim Proj\2021\21163KL\Bim Mod\01\Arch\Dwg\Dwg\DWG\SUBDEF\21163KL_3F.dwg

Scale 1:100 By CAD

Drawing Number : A/GBP/11

Revision Number : J

Drawing Purpose

Buildings Department
Amended Plan

Digitally signed by LEUNG Ka Man Andy
APVA (BOS)
18 March 2026

Received on 16 March 2026

Plan Approved

(Digitally Signed)
TSOI Lap-san, Lapson
Senior Building Surveyor
for BUILDING AUTHORITY
17 March 2026

Note: This plan has been processed on a curtailed check basis under the centralized processing system as promulgated in PNAP ADM-19. The duties of the authorized person, registered structural engineer and/or registered geotechnical engineer concerned as specified under section 4(3)(b) and the provision of section 14(2)(c) of the Buildings Ordinance are of particular relevance in this regard.

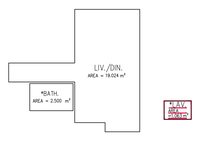

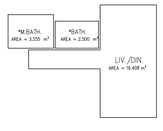

3/F – 30/F T1–FLAT A (LIV./DIN., BATH. & LAV.) ROOM AREA

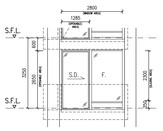

WINDOW AREA CALCULATION
FOR T1–FLAT A (LIV./DIN., BATH. & LAV.)
(FOR T1–FLAT B TO H, J TO N, P & Q (LIV./DIN. & BATH))

ROOM AREA = 19.024 s.m.

WINDOW AREA REQ'D = 19.024 / 10 = 1.902 s.m.
WINDOW AREA PROV'D = 2.800 x 2.300 x 0.70
= 4.508 s.m. > 1.902 s.m. (REQUIRED)

OPENABLE WINDOW AREA REQ'D = 19.024/16 x 2.500 / 10 = 1.063 / 10 = 1.545 s.m.
OPENABLE WINDOW AREA PROV'D = (1.285 x 2.650 x 0.70)
= 2.384 s.m. > 1.545 s.m. (REQUIRED)

3/F – 30/F T1–FLAT A (M.B.R. & M. BATH) ROOM AREA

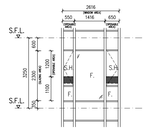

WINDOW AREA CALCULATION
FOR T1–FLAT A (M.B.R. & M. BATH)

ROOM AREA = 9.333 s.m.

WINDOW AREA REQ'D = 9.333 / 10 = 0.933 s.m.
WINDOW AREA PROV'D = 2.616 x 2.300 x 0.70
= 4.213 s.m. > 0.933 s.m. (REQUIRED)

OPENABLE WINDOW AREA REQ'D = 9.333 /16 x 3.255 /10 = 0.909 s.m.
OPENABLE WINDOW AREA PROV'D = (0.65 x 0.55) x 1.200 x 0.70
= 1.008 s.m. >0.909 s.m. (REQUIRED)

3/F – 30/F T1–FLAT A (B.R.1 & B.R.2) ROOM AREA

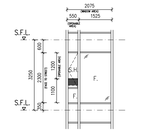

WINDOW AREA CALCULATION
FOR T1–FLAT A (B.R.1 & B.R.2)
(FOR T1–FLAT B TO H, J TO L (B.R.1 & B.R.2))

ROOM AREA = 4.400 s.m.

WINDOW AREA REQ'D = 4.400 / 10 = 0.440 s.m.
WINDOW AREA PROV'D = 2.075 x 2.300 x 0.70
= 3.343 s.m. > 0.440 s.m. (REQUIRED)

OPENABLE WINDOW AREA REQ'D = 4.400 /16 = 0.275 s.m.
OPENABLE WINDOW AREA PROV'D = 0.550 x 1.200 x 0.70
= 0.462 s.m. >0.275 s.m. (REQUIRED)

3/F – 30/F T1–FLAT M (M.B.R.) ROOM AREA

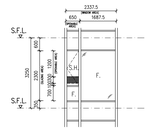

WINDOW AREA CALCULATION
FOR T1–FLAT M (M.B.R.)
(FOR T1–FLAT F (M.B.R.))

ROOM AREA = 8.879 s.m.

WINDOW AREA REQ'D = 8.879 / 10 = 0.888 s.m.
WINDOW AREA PROV'D = 2.3375 x 2.300 x 0.70
= 3.763 s.m. > 0.888 s.m. (REQUIRED)

OPENABLE WINDOW AREA REQ'D = 8.879 /16 = 0.555 s.m.
OPENABLE WINDOW AREA PROV'D = 0.650 x (1.200 x 0.10) x 0.80
= 0.478 s.m. >0.555 s.m. (REQUIRED)

3/F – 30/F T1–FLAT M (LIV./DIN., M.BATH & BATH.) ROOM AREA

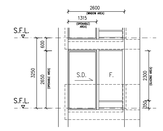

WINDOW AREA CALCULATION
FOR T1–FLAT M (LIV./DIN., M.BATH & BATH.)

ROOM AREA = 16.408 s.m.

WINDOW AREA REQ'D = 16.408 / 10 = 1.641 s.m.
WINDOW AREA PROV'D = 3.600 x 2.300 x 0.70
= 4.968 s.m. > 1.641 s.m. (REQUIRED)

OPENABLE WINDOW AREA REQ'D = 16.408/16 x 2.500 / 10 x 3.255 / 10 = 1.601 s.m.
OPENABLE WINDOW AREA PROV'D = (1.315 x 2.650 x 0.70)
= 2.439 s.m. >1.601 s.m. (REQUIRED)

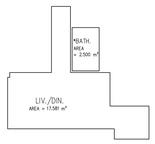

3/F – 30/F T2–FLAT A (LIV./DIN. & BATH.) ROOM AREA

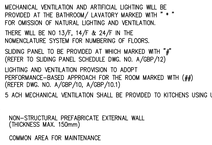

WINDOW AREA CALCULATION
FOR T2–FLAT A (LIV./DIN. & BATH.)
(FOR T2–FLAT B TO H, J TO N, P & Q (LIV./DIN. & BATH))

ROOM AREA = 17.581 s.m.

WINDOW AREA REQ'D = 17.581 / 10 = 1.758 s.m.
WINDOW AREA PROV'D = 2.2775 x 2.300 x 0.70
= 3.667 s.m. > 1.758 s.m. (REQUIRED)

OPENABLE WINDOW AREA REQ'D = 17.581/16 x 2.500 / 10 = 1.349 s.m.
OPENABLE WINDOW AREA PROV'D = [1.1025 x 2.650 x 0.70]
= 2.045 s.m. >1.349 s.m. (REQUIRED)

3/F – 30/F T2–FLAT A (M.B.R.) ROOM AREA

WINDOW AREA CALCULATION
FOR T2–FLAT A (M.B.R.)

ROOM AREA = 9.203 s.m.

WINDOW AREA REQ'D = 9.203 / 10 = 0.920 s.m.
WINDOW AREA PROV'D = 2.276 x 2.300 x 0.70
= 4.273 s.m. > 0.920 s.m. (REQUIRED)

OPENABLE WINDOW AREA REQ'D = 9.203 /16 = 0.575 s.m.
OPENABLE WINDOW AREA PROV'D = (0.645 x 0.55) x 1.200 x 0.70
= 1.008 s.m. >0.575 s.m. (REQUIRED)

3/F – 30/F T2–FLAT J (B.R.1) ROOM AREA

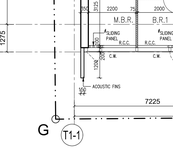

WINDOW AREA CALCULATION
FOR T2–FLAT J (B.R.1)
(FOR T2–FLAT B TO D, G, H, K TO N & P (B.R.1))

ROOM AREA = 4.950 s.m.

WINDOW AREA REQ'D = 4.950 / 10 = 0.495 s.m.
WINDOW AREA PROV'D = 1.450 x 2.300 x 0.70
= 2.334 s.m. > 0.495 s.m. (REQUIRED)

OPENABLE WINDOW AREA REQ'D = 4.950 /16 = 0.309 s.m.
OPENABLE WINDOW AREA PROV'D = 0.550 x 1.200 x 0.70
= 0.462 s.m. >0.309 s.m. (REQUIRED)

3/F – 30/F T2–FLAT A (B.R.2) ROOM AREA

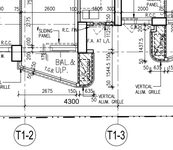

WINDOW AREA CALCULATION
FOR T2–FLAT A (B.R.2)
(FOR T2–FLAT A, E, F, J & Q (B.R.1))
(FOR T2–FLAT B TO H, K TO N, P & Q (M.B.R.))

ROOM AREA = 4.350 s.m.

WINDOW AREA REQ'D = 4.350 / 10 = 0.435 s.m.
WINDOW AREA PROV'D = 1.9375 x 2.300 x 0.70
= 3.118 s.m. > 0.435 s.m. (REQUIRED)

OPENABLE WINDOW AREA REQ'D = 4.350 /16 = 0.272 s.m.
OPENABLE WINDOW AREA PROV'D = 0.550 x 1.200 x 0.70
= 0.462 s.m. >0.272 s.m. (REQUIRED)

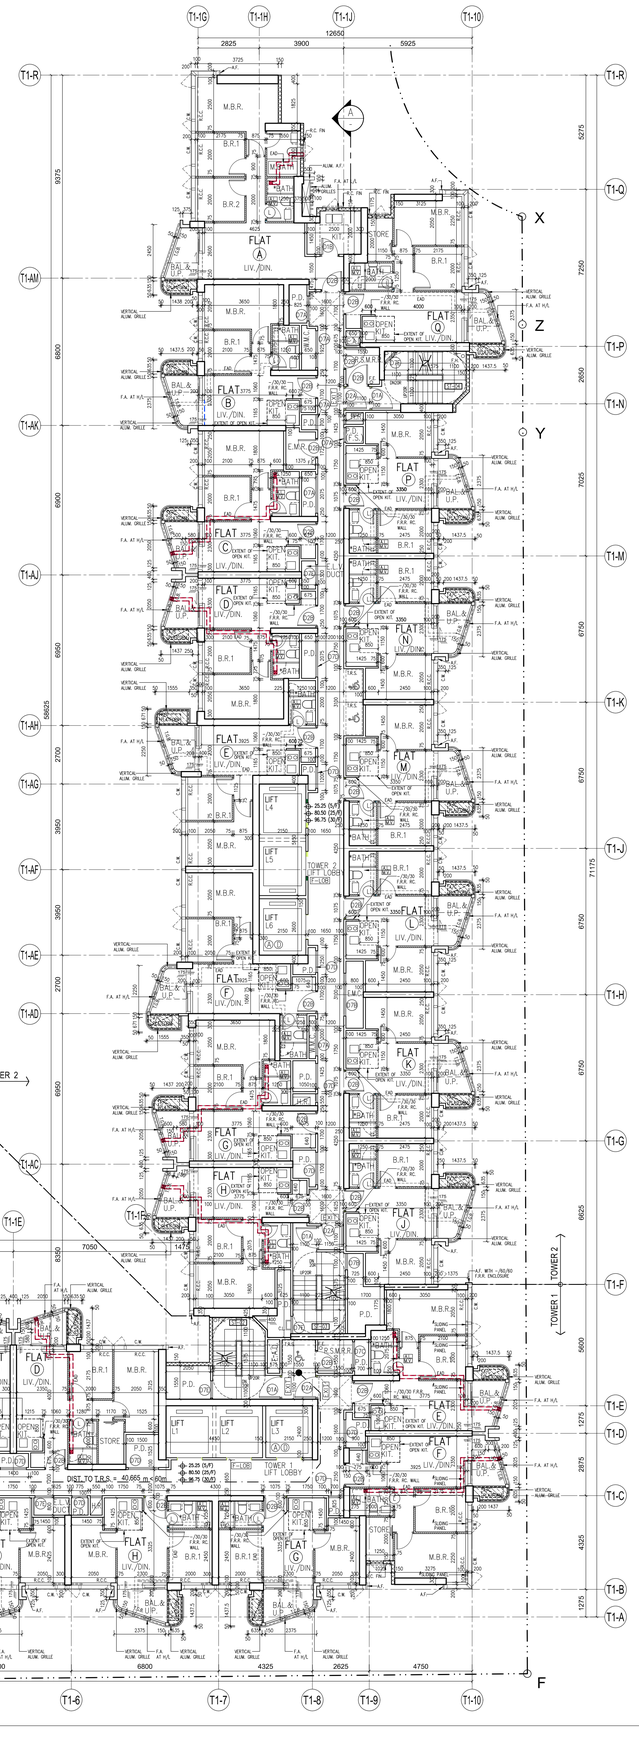

5TH TO 30TH FLOOR PLAN – TOWER 1 & TOWER 2 (23 STOREYS)

NOTE:
1. MECHANICAL VENTILATION AND ARTIFICIAL LIGHTING WILL BE PROVIDED AT THE BATHROOM/ LAVATORY MARKED WITH " * " FOR OMISSION OF NATURAL LIGHTING AND VENTILATION.
2. THERE WILL BE NO 13/F, 14/F & 24/F IN THE NOMENCLATURE SYSTEM FOR NUMBERING OF FLOORS.
3. SLIDING PANEL TO BE PROVIDED AT WHICH MARKED WITH "#" (REFER TO SLIDING PANEL SCHEDULE DWG. NO. A/GBP/12)
4. LIGHTING AND VENTILATION PROVISION TO ADOPT PERFORMANCE-BASED APPROACH FOR THE ROOM MARKED WITH (##) (REFER DWG. NO. A/GBP/10, A/GBP/10.1)
5. 5 ACH MECHANICAL VENTILATION SHALL BE PROVIDED TO KITCHENS USING UVA METHOD.

LEGEND:
- NON–STRUCTURAL PREFABRICATE EXTERNAL WALL (THICKNESS MAX. 150mm)
- COMMON AREA FOR MAINTENANCE
- A/C PLATFORM

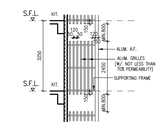

A TYPICAL DETAIL OF ALUM. GRILLES FOR SCREENING OF EXTERNAL PIPES AT T2

SLIDING PANEL SCHEDULE

TOWER 1		
FLAT	ROOM	FLOOR
E	LIV./DIN.#2	3/F – 5/F
	B.R.1#3	
	M.B.R.#2	3/F
F	LIV./DIN.#2	3/F – 5/F
	B.R.1#3	3/F – 6/F
	M.B.R.#2	3/F – 8/F
G	LIV./DIN.#2	5/F – 8/F
	M.B.R.#2	5/F – 9/F
	B.R.1#3	5/F – 8/F
H	LIV./DIN.#2	5/F – 8/F
	M.B.R.#2	5/F – 8/F
	B.R.1#3	
J	LIV./DIN.#2	5/F – 8/F
	M.B.R.#2	5/F – 8/F
	B.R.1#3	5/F – 9/F
K	LIV./DIN.#2	5/F – 9/F
	M.B.R.#2	5/F – 9/F
	B.R.1#3	5/F – 9/F
L	LIV./DIN.#2	5/F – 10/F
	B.R.1#3	3/F – 10/F
	M.B.R.#2	5/F – 10/F
M	LIV./DIN.#2	3/F – 12/F
	M.B.R.#2	3/F – 16/F
	B.R.1#3	
	B.R.2#3	3/F – 15/F

#2: ACOUSTIC DOOR
#3: ACOUSTIC WINDOW

B.D. Ref. :	80 2/4024/21				
BIM Ref. :	-	-			
F.S.D. Ref. :	-	-			
D.L.O. Ref. :	-	-			

Rev.	Description	Drawn	Checked	Approved	Date
-	1st Submission	WY	AW	AL	07/2022
A	2nd Submission	WY	AW	AL	11/2022
B	1st Amendment	TWM	AW	AL	04/2023
C	2nd Amendment	TWM	AW	AL	12/2023
D	3rd Amendment	TWM	AW	AL	04/2024
D	3rd Amendment (Re-submission)	TWM	AW	AL	05/2024
E	5th Amendment	TWM	AW	AL	12/2024
E	5th Amendment (Re-submission)	TWM	AW	AL	02/2025
F	8th Amendment	TWM	AW	AL	05/2025
G	9th Amendment	TWM	AW	AL	08/2025
G	9th Amendment (Re-submission)	TWM	AW	AL	10/2025
H	10th Amendment	TWM	AW	AL	12/2025
I	11th Amendment	TWM	AW	AL	02/2026

Type II works
The works shown on these plans are Type II works (Building Amendment) in respect of which consent is applied for the purpose of Fast Track consent application under regulation 33 of the Building (Administration) Regulations.

RONALD LU & PARTNERS

呂元祥建築師事務所

Check all measurements on site. Do not scale off drawings.
This drawing is to be read in conjunction with the specification and any discrepancies are to be immediately reported to the Architect.
The copyright of this drawing is reserved by architect of the Architect and is not to be reproduced in whole or in part without permission of the Architect.

Project Title :
PROPOSED DEVELOPMENT
AT BAILEY STREET
& WING KWONG STREET
TO KWA WAN, KOWLOON

Drawing Title :
5TH - 30TH FLOOR PLAN
FOR TOWER 1 & TOWER 2

Drawn By	TWM	Date	08/2025
Checked By	AW	Date	08/2025
Approved By	AL	Date	08/2025
Project No.	21163KL	Issue Date	08/2025

File Path :
J:\Bailey Office Data\2021\21163KL Bailey Street & Wing Kwong Street\DWG\BUILDING\BP 1\5-30 Amendment\ Mark Amend\5-30 FL DEP 1.0.dwg

Scale 1:100 By CAD

Drawing Number : A/GBP/12
Revision Number : I

Drawing Purpose
Buildings Department
Amended Plan

Digitally signed by LEUNG Kit Man Andy
APVI (BSR)
16 March 2026

Received on
16 March 2026

Plan Approved
(Digitally Signed)
TSOI Lap-san, Lapson
Senior Building Surveyor
for BUILDING AUTHORITY
17 March 2026

Note: This plan has been processed on a curtailed check basis under the centralized processing system as promulgated in PNAP ADM-15. The duties of the authorized person, registered structural engineer and/or registered geotechnical engineer concerned as specified under section 4(3)(b) and the provision of section 14(2)(c) of the Buildings Ordinance are of particular relevance in this regard.

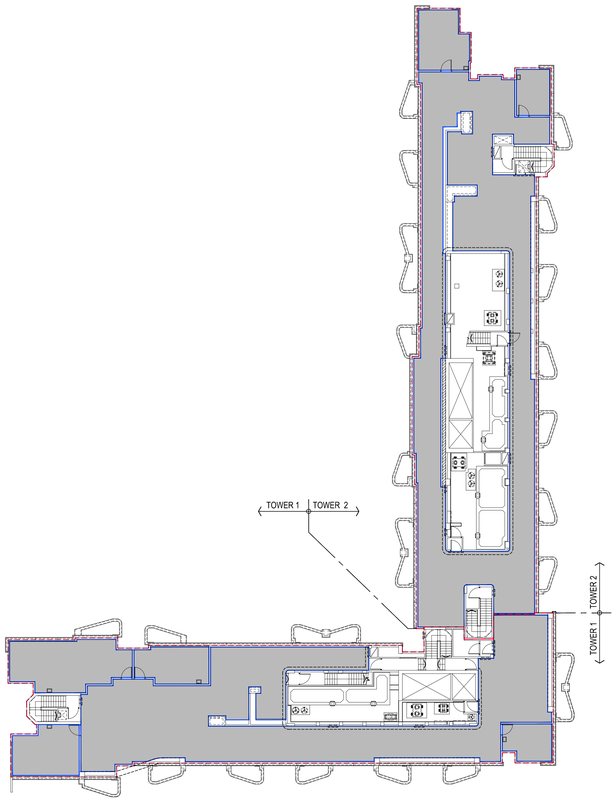

TOWER 1 & TOWER 2 ROOF FLOOR DIAGRAM

(UNDER PLANNING DEPARTMENT)
SCALE 1:200

	TOWER 1	TOWER 2
AREA OF ROOF	576.291 m^2	600.794 m^2
AREA OF ROOF W/O. ROOF TOP STRUCTURE	400.750 m^2 (69.540 % OF ROOF AREA)	340.058 m^2 (56.630 % OF ROOF AREA)

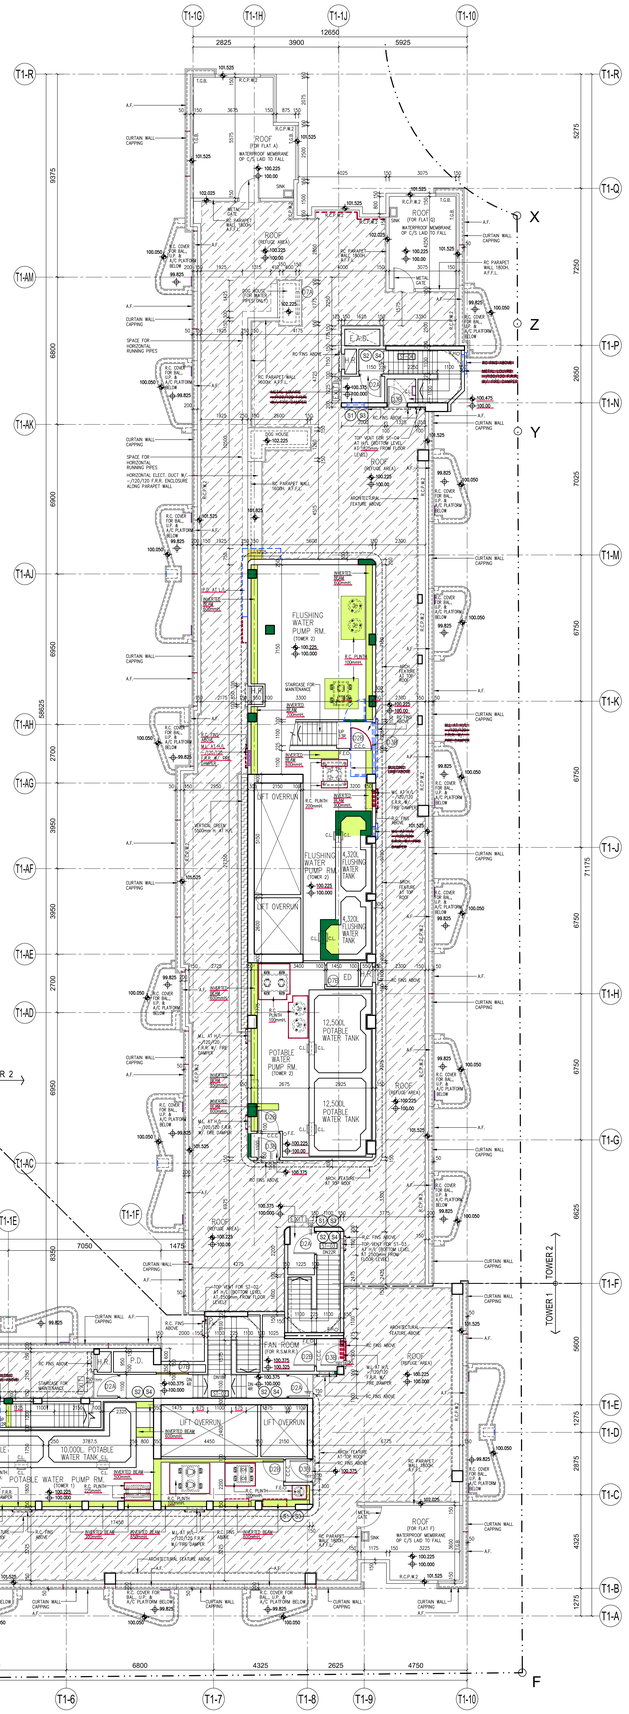
T1-1G
T1-1H
T1-1J
T1-1O
2825
3900
5925
12650
T1-1R
T1-1AM
T1-1AK
T1-1AJ
T1-1AH
T1-1AG
T1-1AF
T1-1AE
T1-1AD
T1-1AC
T1-1Q
T1-1P
T1-1N
T1-1M
T1-1K
T1-1J
T1-1H
T1-1G
T1-1F
T1-1E
T1-1D
T1-1C
T1-1B
T1-1A
X
Z
Y
ROOF (FOR FLAT A) WATERPROOF MEMBRANE OF C/S LAID TO FALL
ROOF (FOR FLAT C) WATERPROOF MEMBRANE OF C/S LAID TO FALL
ROOF (FOR FLAT D) WATERPROOF MEMBRANE OF C/S LAID TO FALL
ROOF (FOR FLAT E) WATERPROOF MEMBRANE OF C/S LAID TO FALL
ROOF (FOR FLAT F) WATERPROOF MEMBRANE OF C/S LAID TO FALL
ROOF (FOR FLAT G) WATERPROOF MEMBRANE OF C/S LAID TO FALL
ROOF (FOR FLAT H) WATERPROOF MEMBRANE OF C/S LAID TO FALL
ROOF (FOR FLAT I) WATERPROOF MEMBRANE OF C/S LAID TO FALL
ROOF (FOR FLAT J) WATERPROOF MEMBRANE OF C/S LAID TO FALL
ROOF (OTHER AREA)
FLUSHING WATER PUMP RM. (TOWER 2)
LIFT OVERRUN
4.320L FLUSHING WATER TANK
12.500L POTABLE WATER TANK
POTABLE WATER PUMP RM. (TOWER 2)
FAN ROOM (FOR ROOF)
E.&M.C.
STAIRCASE FOR MAINTENANCE
SPACE FOR HORIZONTAL RUNNING PIPES
SPACE FOR VERTICAL RUNNING PIPES
R.C. COVER FOR E.&M. C.P. & A/C PLATFORM BELOW
A/C PLATFORM BELOW
R.C. PARAPET WALL 900(H) A.F.F.L.
R.C. PARAPET WALL 750(H) A.F.F.L.
R.C.P.W.2
R.C.P.W.3
CURTAIN WALL CAPPING
A.F.
T.G.B.
R.C. FIN
R.C. PLINTH 150mm
R.C. PLINTH 200mm
R.C. PLINTH 300mm
R.C. PLINTH

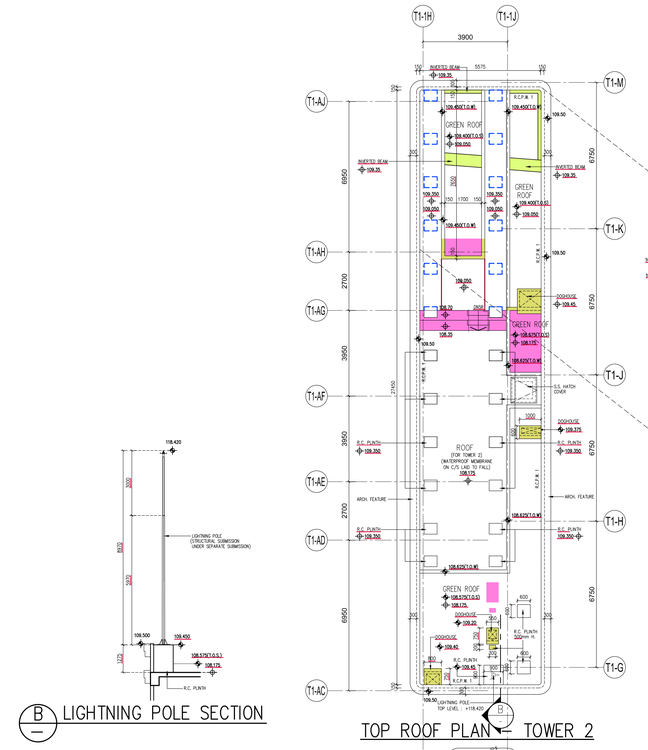

TOP ROOF PLAN – TOWER 2

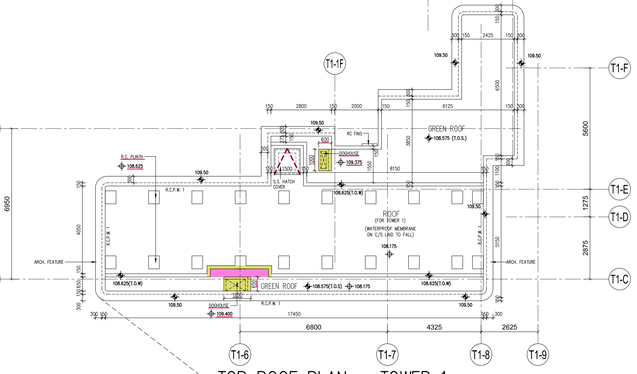

TOP ROOF PLAN – TOWER 1

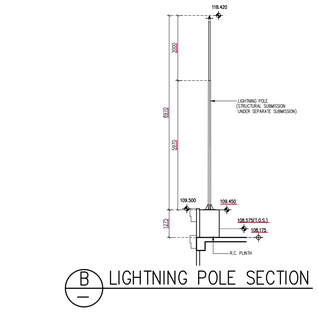

B LIGHTNING POLE SECTION

UPPER ROOF PLAN – TOWER 1 & TOWER 2

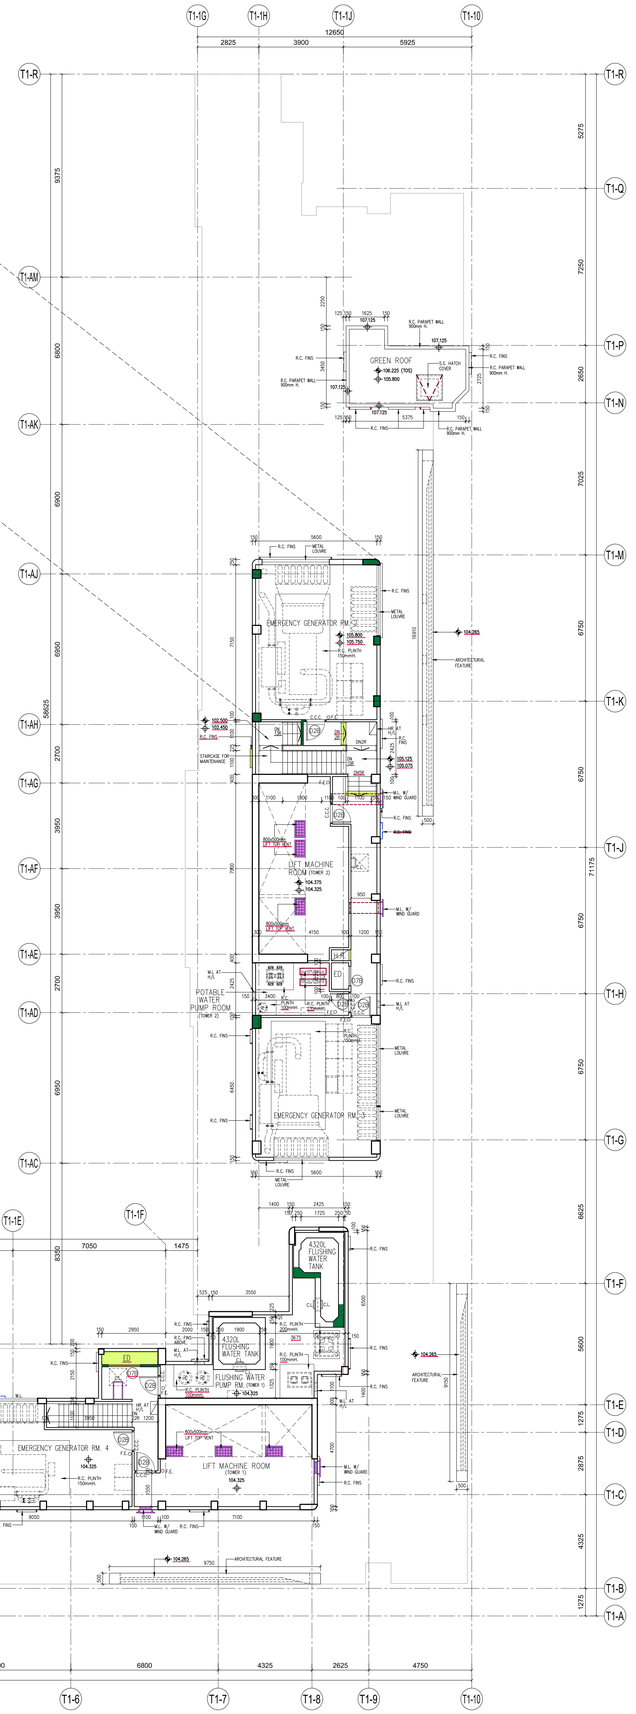

B.D. Ref :	BD 2/4024/21
BIM Ref :	- --
F.S.D. Ref :	- --
D.L.O. Ref :	- --

Rev.	Description	Drawn	Checked	Approved	Date
-	1st Submission	WY	AW	AL	07/2022
A	2nd Submission	WY	AW	AL	11/2022
B	1st Amendment	TWM	AW	AL	04/2023
C	2nd Amendment	TWM	AW	AL	12/2023
D	3rd Amendment	TWM	AW	AL	04/2024
D	3rd Amendment (Re-submission)	TWM	AW	AL	05/2024
E	5th Amendment	TWM	AW	AL	12/2024
E	5th Amendment (Re-submission)	TWM	AW	AL	02/2025
F	8th Amendment	TWM	AW	AL	05/2025
G	9th Amendment	TWM	AW	AL	10/2025
G	9th Amendment (Re-submission)	TWM	AW	AL	
H	10th Amendment	TWM	AW	AL	12/2025
I	11th Amendment	TWM	AW	AL	02/2026

Type III works
The works shown on these plans are Type III works (Building Amendment) in respect of which consent is applied for the purpose of Fast Track consent application under regulation 33 of the Building (Administration) Regulations.

RONALD LU & PARTNERS

呂元祥建築師事務所

Check all measurements on site. Do not scale off drawings.
This drawing is to be read in conjunction with the specification and any discrepancies are to be immediately reported to the Architect.
The copyright of this drawing is reserved by the Architect and is not to be reproduced in whole or in part without permission of the Architect.

Project Title :
PROPOSED DEVELOPMENT
AT BAILEY STREET
& WING KWONG STREET
TO KWA WAN, KOWLOON

Drawing Title :
UPPER ROOF FLOOR PLAN
FOR TOWER 1 & TOWER 2

Drawn By	TWM	Date	08/2025
Checked By	AW	Date	08/2025
Approved By	AL	Date	08/2025
Project No.	21163KL	Issue Date	08/2025

File Path :
...\Bldg. Dpty. Sec\2121DN_Sale Dev\Files\Kwa Dev\DWG\SUBDEP 1\Tnd Amendment\ Tnd Amend\P27A ZIP 1.0.dwg

Scale 1:100 By CAD

Drawing Number : A/GBP/14

Revision Number : I

Drawing Purpose

Buildings Department
Amended Plan

Digitally signed by LEUNG Kit Man Andy
APPLIABLE
16 March 2026

Received on
16 March 2026

Plan Approved
(Digitally Signed)
TSOI Lap-san, Lapson
Senior Building Surveyor
for BUILDING AUTHORITY
17 March 2026

Note: This plan has been processed on a curtailed check basis under the centralized processing system as promulgated in PNAP ADM-19. The duties of the authorized person, registered structural engineer and/or registered geotechnical engineer concerned as specified under section 4(3)(b) and the provision of section 14(2)(c) of the Buildings Ordinance are of particular relevance in this regard.

SLIDING PANEL SCHEDULE

TOWER 3		
FLAT	ROOM	FLOOR
D	LIV./DIN.#2	3/F – 30/F
	B.R.1#1#3	
	M.B.R.#3	
E	LIV./DIN.#2	3/F – 30/F
	B.R.1#1#3	
	M.B.R.#3	
F	LIV./DIN.#2	10/F – 30/F
	M.B.R.#3	
	B.R.1#3	11/F – 30/F
G	LIV./DIN.#2	15/F – 30/F
	M.B.R.#3	17/F – 26/F
	B.R.1#3	11/F – 30/F

#1 : WITH SOUND ABSORPTIVE MATERIAL
#2 : ACOUSTIC DOOR
#3 : ACOUSTIC WINDOW

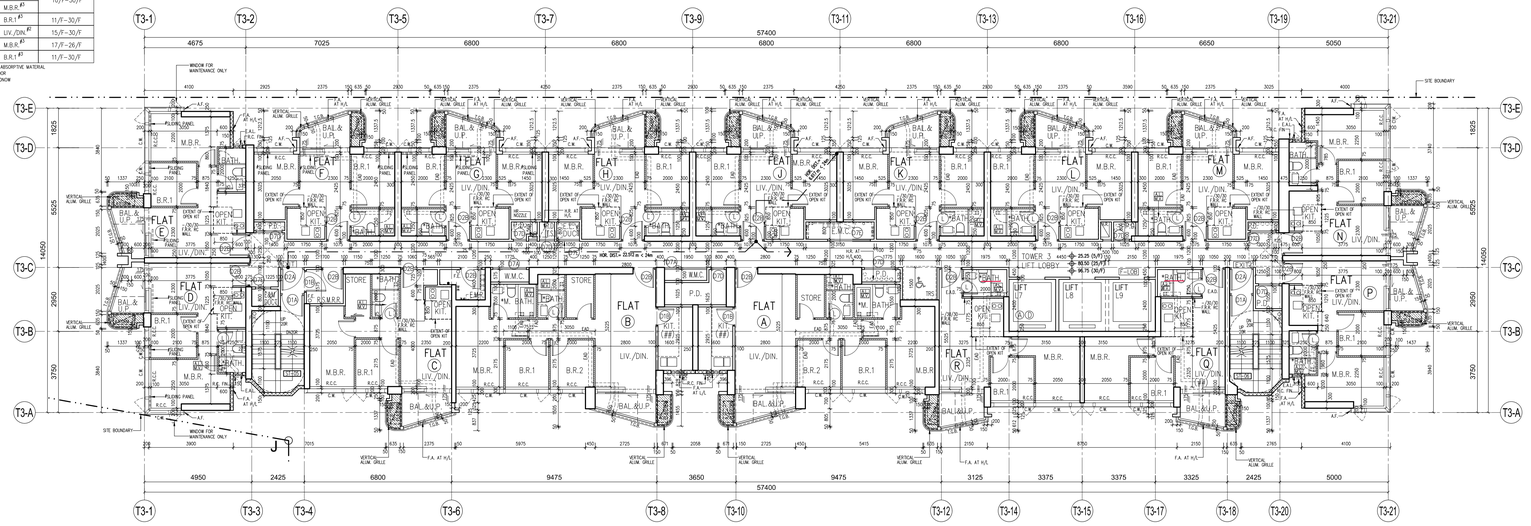

5TH TO 30TH FLOOR PLAN – TOWER 3 (23 STOREYS)

NOTE:
1. MECHANICAL VENTILATION AND ARTIFICIAL LIGHTING WILL BE PROVIDED AT THE BATHROOM/ LAVATORY MARKED WITH " • " FOR OMISSION OF NATURAL LIGHTING AND VENTILATION.
2. THERE WILL BE NO 13/F, 14/F & 24/F IN THE NOMENCLATURE SYSTEM FOR NUMBERING OF FLOORS.
3. SLIDING PANEL TO BE PROVIDED AT WHICH MARKED WITH "#" (REFER TO SLIDING PANEL SCHEDULE DWG. NO. A/GBP/19)
4. LIGHTING AND VENTILATION PROVISION TO ADOPT PERFORMANCE-BASED APPROACH FOR THE ROOM MARKED WITH (##) (REFER DWG. NO. A/GBP/10)
5. 5 ACH MECHANICAL VENTILATION SHALL BE PROVIDED TO KITCHENS USING UVA METHOD.

LEGEND:

A/C PLATFORM

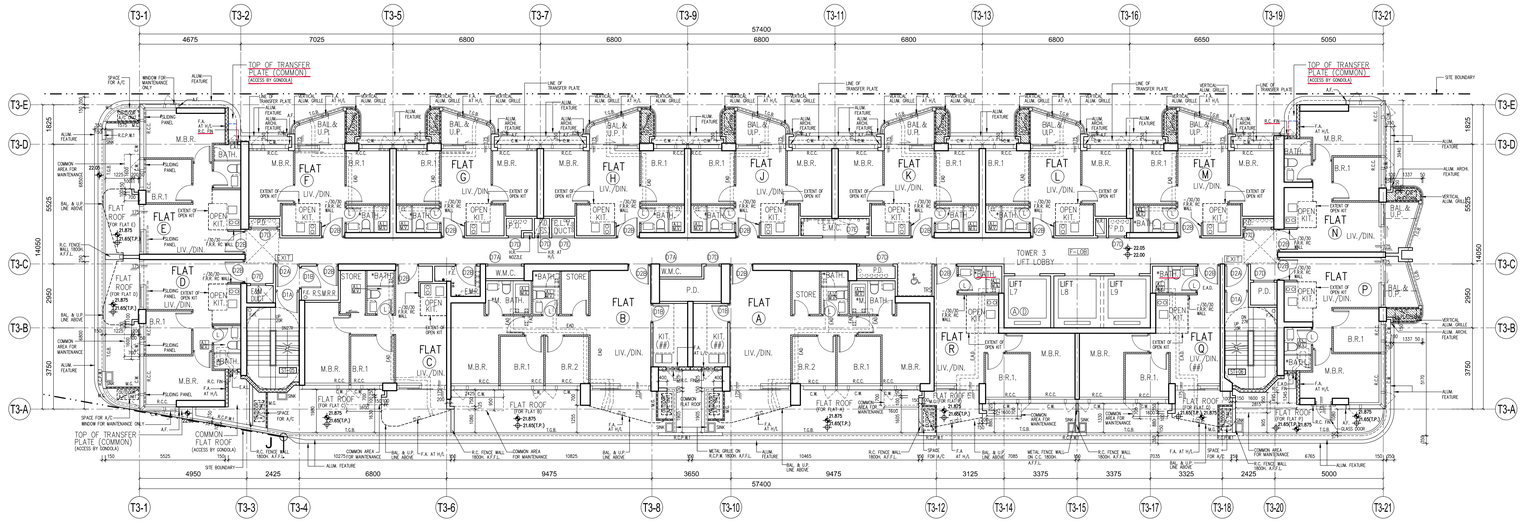

3RD FLOOR PLAN – TOWER 3

NOTE:
1. MECHANICAL VENTILATION AND ARTIFICIAL LIGHTING WILL BE PROVIDED AT THE BATHROOM/ LAVATORY MARKED WITH " • " FOR OMISSION OF NATURAL LIGHTING AND VENTILATION.
2. ALL DIMENSION ARE SAME AS 5/F – 30/F, EXCEPT OTHERWISE NOTED.
3. SLIDING PANEL TO BE PROVIDED AT WHICH MARKED WITH "#" (REFER TO SLIDING PANEL SCHEDULE DWG. NO. A/GBP/19)
4. LIGHTING AND VENTILATION PROVISION TO ADOPT PERFORMANCE-BASED APPROACH FOR THE ROOM MARKED WITH (##) (REFER DWG. NO. A/GBP/10)
5. 5 ACH MECHANICAL VENTILATION SHALL BE PROVIDED TO KITCHENS USING UVA METHOD.

LEGEND:

A/C PLATFORM

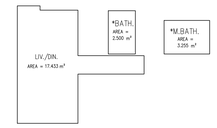

3/F – 30/F FLAT A (LIV./DIN. & BATH. & M.BATH.) ROOM AREA

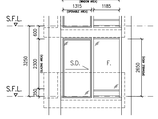

WINDOW AREA CALCULATION
FOR FLAT A (LIV./DIN. & BATH. & M.BATH.)
(FOR FLAT 6 TO 14, J TO N & P (LIV./DIN. & BATH. & M.BATH.))

ROOM AREA	= 17.433 s.m.	
WINDOW AREA REQ'D	= 17.433 / 10 = 1.743 s.m.	
WINDOW AREA PROV'D	= (2.600 x 2.300 x 0.70)	
	= 4.186 s.m. > 1.743 s.m.	(REQUIRED)
OPENABLE WINDOW AREA REQ'D	= 17.433 /16 x 2.500 /10 x 3.255 /10 =	1.665 s.m.
OPENABLE WINDOW AREA PROV'D	= (1.25 x 2.850 x 0.70)	
	= 2.439 s.m. > 1.665 s.m.	(REQUIRED)

3/F – 30/F FLAT A (M.B.R. & M. BATH.) ROOM AREA

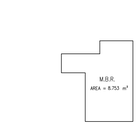

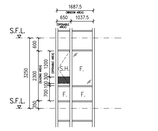

WINDOW AREA CALCULATION
FOR FLAT A (M.B.R. & M. BATH.)
(FOR FLAT B (M.B.R. & M. BATH.))

ROOM AREA	= 8.753 s.m.	
WINDOW AREA REQ'D	= 8.753 / 10 = 0.875 s.m.	
WINDOW AREA PROV'D	= (1.6875 x 2.300 x 0.70)	
	= 2.717 s.m. > 0.875 s.m.	(REQUIRED)
OPENABLE WINDOW AREA REQ'D	= 8.753 /16 = 0.547 s.m.	
OPENABLE WINDOW AREA PROV'D	= 0.600 x (1.200 x 0.50) x 0.8	
	= 0.576 s.m. > 0.547 s.m.	(REQUIRED)

3/F – 30/F FLAT F (B.R.1) ROOM AREA

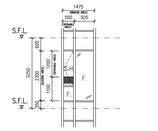

WINDOW AREA CALCULATION
FOR FLAT F (B.R.1)
(FOR FLAT A TO E, G, H, J TO N & P (B.R.1))
(FOR FLAT A TO H, J TO N & P (M.B.R. & M. BATH.))

ROOM AREA	= 4.900 s.m.	
WINDOW AREA REQ'D	= 4.900 / 10 = 0.490 s.m.	
WINDOW AREA PROV'D	= (1.475 x 2.300 x 0.70)	
	= 2.375 s.m. > 0.490 s.m.	(REQUIRED)
OPENABLE WINDOW AREA REQ'D	= 4.900 /16 = 0.306 s.m.	
OPENABLE WINDOW AREA PROV'D	= 0.550 x 1.200 x 0.70	
	= 0.462 s.m. > 0.306 s.m.	(REQUIRED)

3/F – 30/F FLAT A (B.R.2) ROOM AREA

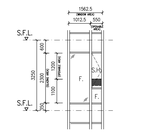

WINDOW AREA CALCULATION
FOR FLAT A (B.R.2)
(FOR FLAT B (B.R.2))

ROOM AREA	= 4.350 s.m.	
WINDOW AREA REQ'D	= 4.350 / 10 = 0.435 s.m.	
WINDOW AREA PROV'D	= (1.1625 x 2.300 x 0.70)	
	= 2.166 s.m. > 0.435 s.m.	(REQUIRED)
OPENABLE WINDOW AREA REQ'D	= 4.350 /16 = 0.272 s.m.	
OPENABLE WINDOW AREA PROV'D	= 0.550 x 1.200 x 0.70	
	= 0.462 s.m. > 0.272 s.m.	(REQUIRED)

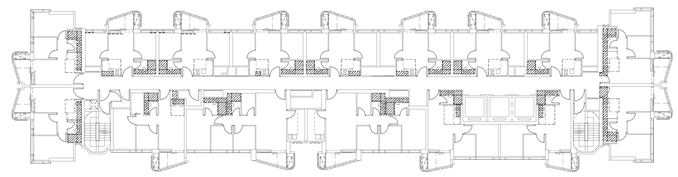

DIAGRAM OF SUNKEN SLAB EXTENT (5th TO 30th FLOOR)
SCALE 1:200

LEGEND:

SUNKEN SLAB

B.D. Ref : 80 2/4024/21

BIM Ref : - -

F.S.D. Ref : - -

D.L.O. Ref : - -

Rev.	Description	Drawn	Checked	Approved	Date
-	1st Submission	WY	AW	AL	07/2022
A	2nd Submission	WY	AW	AL	11/2022
B	1st Amendment	TWM	AW	AL	04/2023
C	2nd Amendment	TWM	AW	AL	12/2023
D	3rd Amendment	TWM	AW	AL	04/2024
D	3rd Amendment (Re-submission)	TWM	AW	AL	05/2024
E	5th Amendment	TWM	AW	AL	12/2024
E	5th Amendment (Re-submission)	TWM	AW	AL	02/2025
F	6th Amendment	TWM	AW	AL	02/2025
G	7th Amendment	TWM	AW	AL	05/2025
H	9th Amendment	TWM	AW	AL	08/2025
H	9th Amendment (Re-submission)	TWM	AW	AL	10/2025
I	10th Amendment	TWM	AW	AL	12/2025
J	11th Amendment	TWM	AW	AL	02/2026
K	13th Amendment	TWM	AW	AL	06/2026

Type II works
The works shown on these plans are Type II works (Building Amendment) in respect of which consent is applied for the purpose of Fast Track consent application under regulation 33 of the Building (Administration) Regulations.

RONALD LU & PARTNERS

呂元祥建築師事務所

Check all measurements on site. Do not scale off drawings. Contractor is responsible for checking all dimensions and any discrepancies are to be immediately reported to the Architect.
This drawing remains the copyright property of the Architect and is not to be reproduced in whole or in part without permission of the Architect.

Project Title :
PROPOSED DEVELOPMENT
AT BAILEY STREET
& WING KWONG STREET
TO KWA WAN, KOWLOON

Drawing Title :
3RD - 30TH FLOOR PLAN
FOR TOWER 3

Drawn By	TWM	Date	08/2025
Checked By	AW	Date	08/2025
Approved By	AL	Date	08/2025
Project No.	21163KL	Issue Date	08/2025

File Path :
I:\Bob BPs\ 2as\2021\21KL Bobs Sheet & Bing Kwong Sreet\DWG\RECS\BEDROP 15 nyo\Revit\P_L73_GBP_15.rvt

Scale 1:100 By CAD

Drawing Number : A/GBP/15 Revision Number : K

Drawing Purpose

Buildings Department
Amended Plan

Digitally signed by WONG Chi Kin Kenneth
APUN 19/66
08 July 2026

Received on
08 July 2026

Plan Approved
(Digitally Signed)
TSOI Lap-san, Lapson
Senior Building Surveyor
for BUILDING AUTHORITY
08 July 2026

Note: This plan has been processed on a curtailed check basis under the centralized processing system as promulgated in PNAP ADM-19. The duties of the authorized person, registered structural engineer and/or registered geotechnical engineer concerned as specified under section 4(3)(b) and the provision of section 14(2)(c) of the Buildings Ordinance are of particular relevance in this regard.

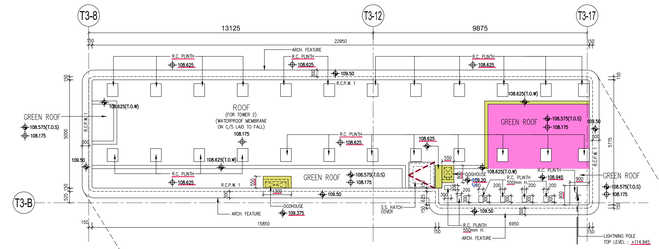

TOP ROOF PLAN – TOWER 3

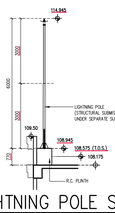

C LIGHTNING POLE SECTION

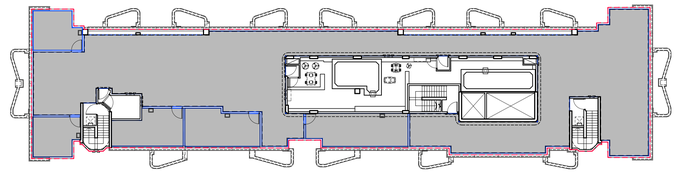

TOWER 3 ROOF FLOOR DIAGRAM

(UNDER PLANNING DEPARTMENT)

SCALE 1:200

AREA OF ROOF	=	652.004 m^2
AREA OF ROOF W/O. ROOF TOP STRUCTURE	=	451.783 m^2 (69.291 % OF ROOF AREA)

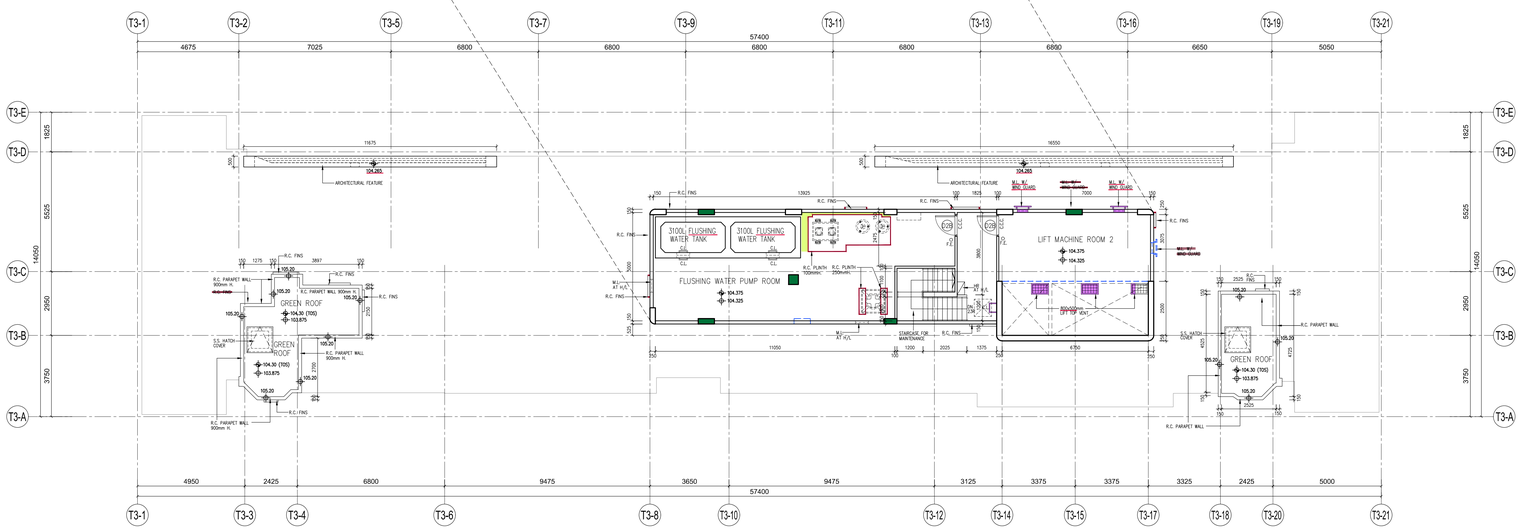

UPPER ROOF PLAN – TOWER 3

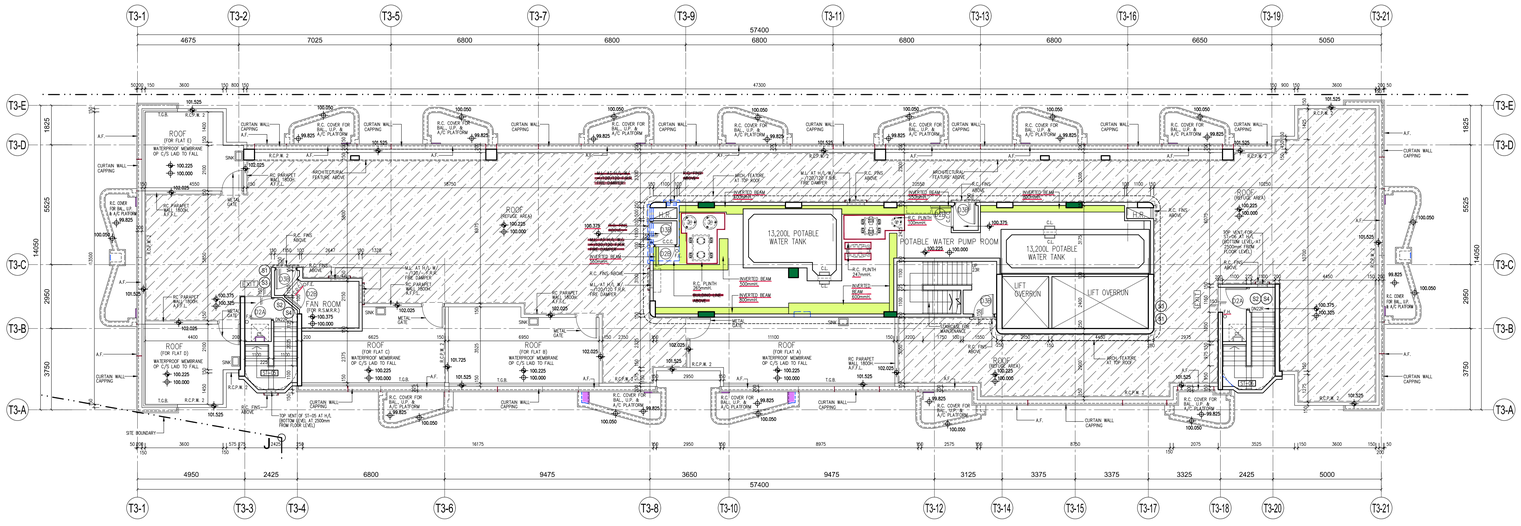

ROOF PLAN – TOWER 3

LEGEND:

- (R1) REFUGE FLOOR NOTICE
- (S1) STAIR NO. SIGN
- (S2) DIRECTIONAL SIGN TO EXIT STAIRCASE
- (S4) A SIGN INDICATING THE ENTRANCE TO THE REFUGE FLOOR
- NET REFUGE AREA = 340.816 m^2

THE PERCENTAGE OF THE NET REFUGE AREA

THE G.F.A. OF THE LARGEST FLOOR PLATE	=	663.064 m^2
PERCENTAGE OF REFUGE AREA PROVIDED	=	340.816 / 663.064 x 100%
	=	51.400 % > 50% (REQUIRED)

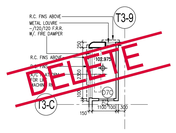

PART PLAN AT LEVEL 102.975

Rev.	Description	Drawn	Checked	Approved	Date
-	1st Submission	WY	AW	AL	07/2022
A	2nd Submission	WY	AW	AL	11/2022
B	1st Amendment	TWM	AW	AL	04/2023
C	2nd Amendment	TWM	AW	AL	12/2023
D	3rd Amendment	TWM	AW	AL	04/2024
D	3rd Amendment (Re-submission)	TWM	AW	AL	05/2024
E	5th Amendment	TWM	AW	AL	12/2024
E	5th Amendment (Re-submission)	TWM	AW	AL	02/2025
F	8th Amendment	TWM	AW	AL	05/2025
G	9th Amendment	TWM	AW	AL	08/2025
G	9th Amendment (Re-submission)	TWM	AW	AL	10/2025
H	10th Amendment	TWM	AW	AL	12/2025
I	11th Amendment	TWM	AW	AL	02/2026

B.D. Ref : 80 2/4024/21

BIM Ref : - --

F.S.D. Ref : - --

D.L.O. Ref : - --

Type II works
The works shown on these plans are Type II works (Building Amendment) in respect of which consent is applied for the purpose of Fast Track consent application under regulation 33 of the Building (Administration) Regulations.

RONALD LU & PARTNERS

呂元祥建築師事務所

Check all dimensions on site. Do not scale off drawings.
The drawings are to be read in conjunction with the specifications and any discrepancies are to be immediately reported to the Architect.
This drawing remains the copyright property of the Architect and is not to be reproduced in whole or in part without permission of the Architect.

Project Title :
PROPOSED DEVELOPMENT
AT BAILEY STREET
& WING KWONG STREET
TO KWA WAN, KOWLOON

Drawing Title :
ROOF FLOOR PLAN
FOR TOWER 3

Drawn By :	TWM	Date	08/2025
Checked By :	AW	Date	08/2025
Approved By :	AL	Date	08/2025
Project No.	21163KL	Issue Date	08/2025

File Path :
T:\Job Shu Jau\2021\21KL Bale Dev\Hyfrasy\Rev09\R0\20200331F.1\Hyfrasytest_test.revit\P27a.DP.f.log

Scale 1:100 By CAD

Drawing Number : A/GBP/16

Revision Number : I

Drawing Purpose

Buildings Department
Amended Plan

Digitally signed by LEUNG Ka Man, Andy
on
APUA 80/80
16 March 2026

Received on
16 March 2026

Plan Approved
(Digitally Signed)
TSOI Lap-san, Lapson
Senior Building Surveyor
for BUILDING AUTHORITY
17 March 2026

Note: This plan has been processed on a curtailed check basis under the centralized processing system as promulgated in PNAP ADM-19. The duties of the authorized person, registered structural engineer and/or registered geotechnical engineer concerned as specified under section 4(3)(b) and the provision of section 14(2)(c) of the Buildings Ordinance are of particular relevance in this regard.

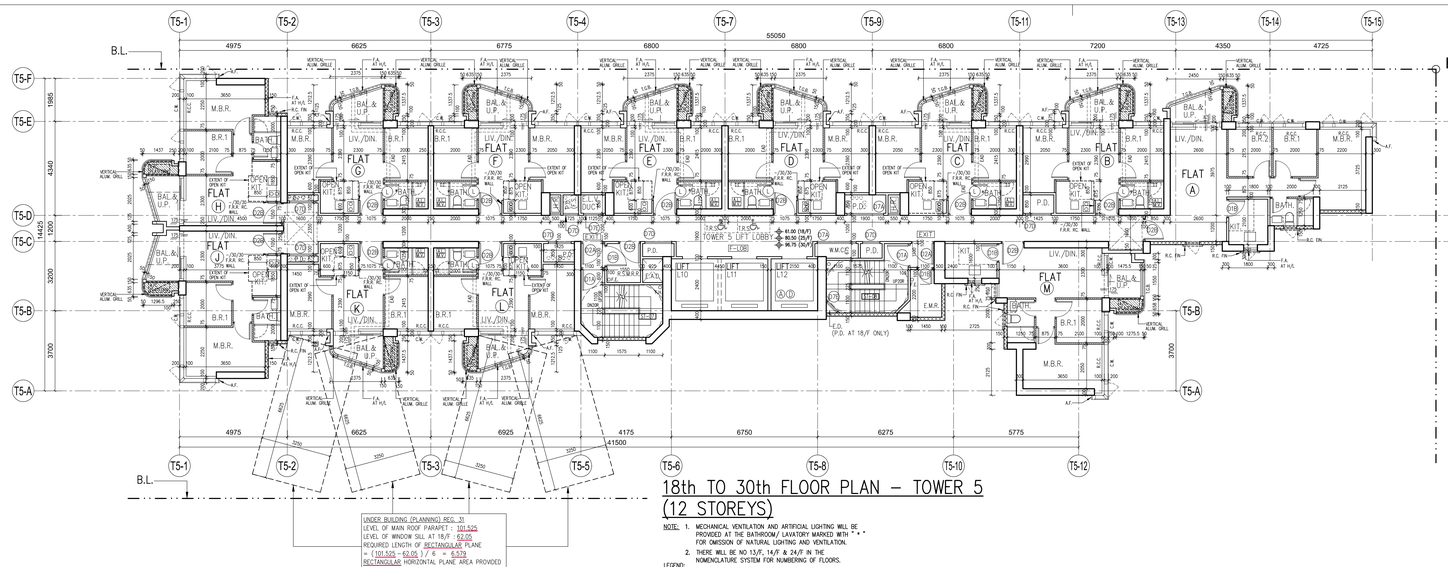

18th TO 30th FLOOR PLAN – TOWER 5 (12 STOREYS)

NOTE: 1. MECHANICAL VENTILATION AND ARTIFICIAL LIGHTING WILL BE PROVIDED AT THE BATHROOM/ LAVATORY MARKED WITH " * " FOR OMISSION OF NATURAL LIGHTING AND VENTILATION.
2. THERE WILL BE NO 13/F, 14/F & 24/F IN THE NOMENCLATURE SYSTEM FOR NUMBERING OF FLOORS.

LEGEND:
A/C PLATFORM

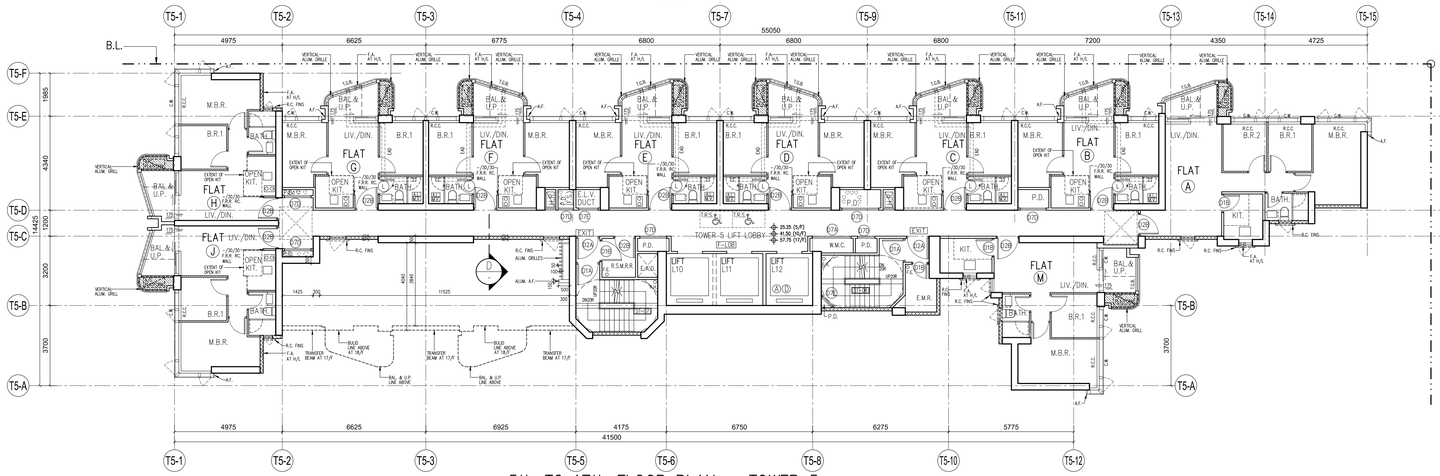

5th TO 17th FLOOR PLAN – TOWER 5 (11 STOREYS)

NOTE: 1. MECHANICAL VENTILATION AND ARTIFICIAL LIGHTING WILL BE PROVIDED AT THE BATHROOM/ LAVATORY MARKED WITH " * " FOR OMISSION OF NATURAL LIGHTING AND VENTILATION.
2. THERE WILL BE NO 13/F, 14/F & 24/F IN THE NOMENCLATURE SYSTEM FOR NUMBERING OF FLOORS.

LEGEND:
A/C PLATFORM

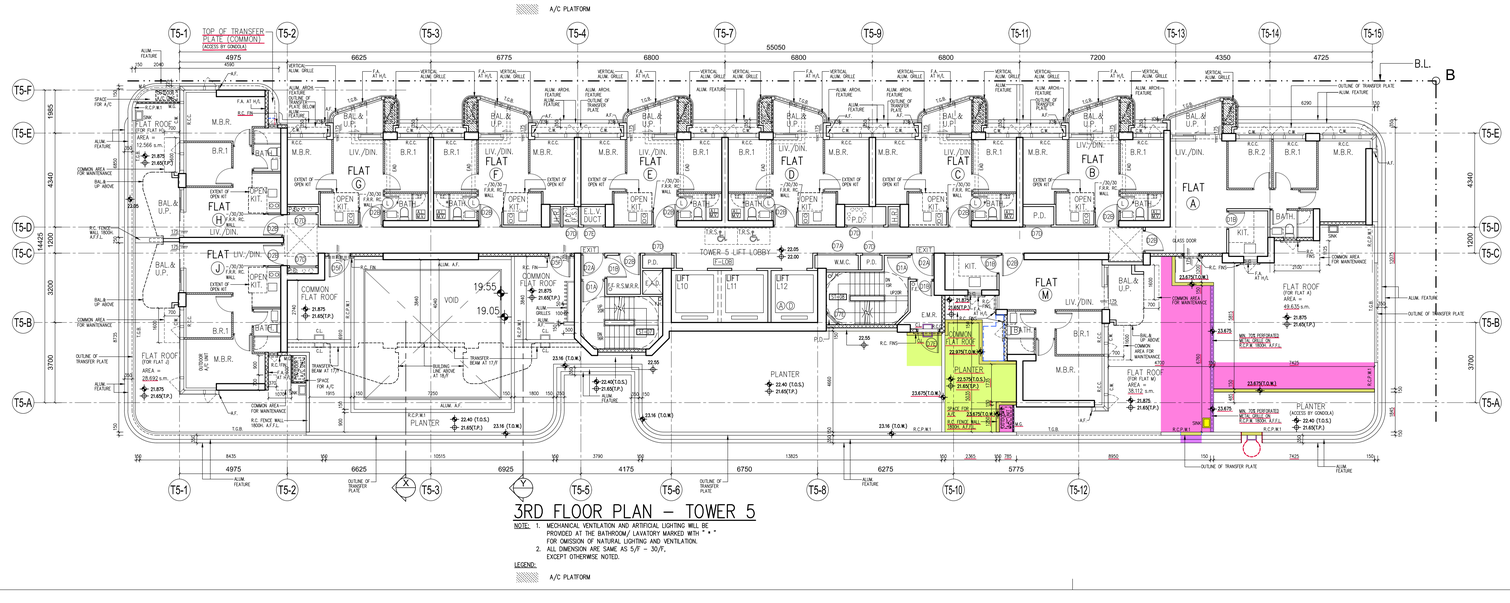

3RD FLOOR PLAN – TOWER 5

NOTE: 1. MECHANICAL VENTILATION AND ARTIFICIAL LIGHTING WILL BE PROVIDED AT THE BATHROOM/ LAVATORY MARKED WITH " * " FOR OMISSION OF NATURAL LIGHTING AND VENTILATION.
2. ALL DIMENSION ARE SAME AS 5/F – 30/F, EXCEPT OTHERWISE NOTED.

LEGEND:
A/C PLATFORM

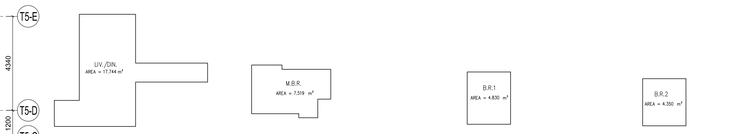

3/F – 30/F FLAT A (LIV./DIN.) ROOM AREA

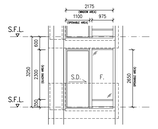

WINDOW AREA CALCULATION
FOR FLAT A (LIV./DIN.)
(FOR FLAT B TO H, J TO M (LIV./DIN.))

ROOM AREA = 17.744 s.m.

WINDOW AREA REQ'D: = 17.744 /10 = 1.774 s.m.
WINDOW AREA PROV'D: = (2.175 x 2.300 x 0.70)
= 3.502 s.m. > 1.774 s.m. (REQUIRED)

OPENABLE WINDOW AREA REQ'D: = 17.744 /76 = 1.109 s.m.
OPENABLE WINDOW AREA PROV'D: = 1.100 x 2.650 x 0.70
= 2.041 s.m. > 1.109 s.m. (REQUIRED)

3/F – 30/F FLAT H (M.B.R.) AREA

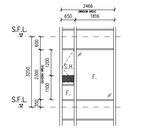

WINDOW AREA CALCULATION
FOR FLAT H (M.B.R.)
(FOR FLAT A TO G, J TO M (M.B.R.))

ROOM AREA = 7.519 s.m.

WINDOW AREA REQ'D: = 7.519 /10 = 0.752 s.m.
WINDOW AREA PROV'D: = 2.466 x 2.300 x 0.70
= 3.970 s.m. > 0.752 s.m. (REQUIRED)

OPENABLE WINDOW AREA REQ'D: = 7.519 /76 = 0.470 s.m.
OPENABLE WINDOW AREA PROV'D: = 0.65 x 1.200 x 0.70
= 0.546 s.m. >0.470 s.m. (REQUIRED)

3/F – 30/F FLAT B (B.R.1) ROOM AREA

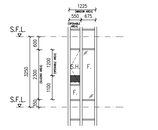

WINDOW AREA CALCULATION
FOR FLAT B (B.R.1)
(FOR FLAT A, C TO G, J TO M (B.R.1))

ROOM AREA = 4.830 s.m.

WINDOW AREA REQ'D: = 4.830 /10 = 0.483 s.m.
WINDOW AREA PROV'D: = (1.225 x 2.300 x 0.70)
= 1.972 s.m. > 0.483 s.m. (REQUIRED)

OPENABLE WINDOW AREA REQ'D: = 4.830 /76 = 0.392 s.m.
OPENABLE WINDOW AREA PROV'D: = (0.550 x 1.200 x 0.70)
= 0.462 s.m. >0.392 s.m. (REQUIRED)

3/F – 30/F FLAT A (B.R.2) ROOM AREA

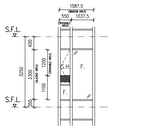

WINDOW AREA CALCULATION
FOR FLAT A (B.R.2)

ROOM AREA = 4.350 s.m.

WINDOW AREA REQ'D: = 4.350 /10 = 0.435 s.m.
WINDOW AREA PROV'D: = (1.5875 x 2.300 x 0.70)
= 2.556 s.m. > 0.435 s.m. (REQUIRED)

OPENABLE WINDOW AREA REQ'D: = 4.350 /76 = 0.272 s.m.
OPENABLE WINDOW AREA PROV'D: = (0.550 x 1.200 x 0.70)
= 0.462 s.m. >0.272 s.m. (REQUIRED)

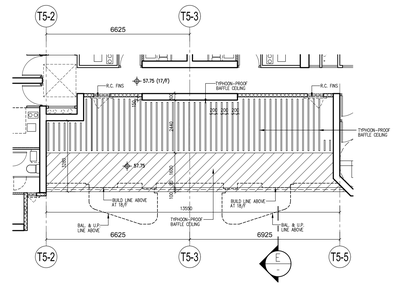

PART PLAN AT 17th FLOOR PLAN – TOWER 5

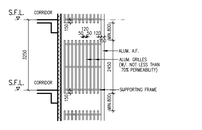

D TYPICAL DETAIL OF ALUM. GRILLES FOR SCREENING OF EXTERNAL PIPES AT T2

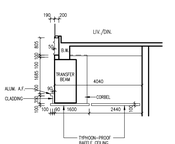

E TYPICAL DETAIL OF CLADDING & TYPHOON-PROOF BAFFLE CEILING
(STRUCTURAL SUBMISSION UNDER SEPARATE SUBMISSION)

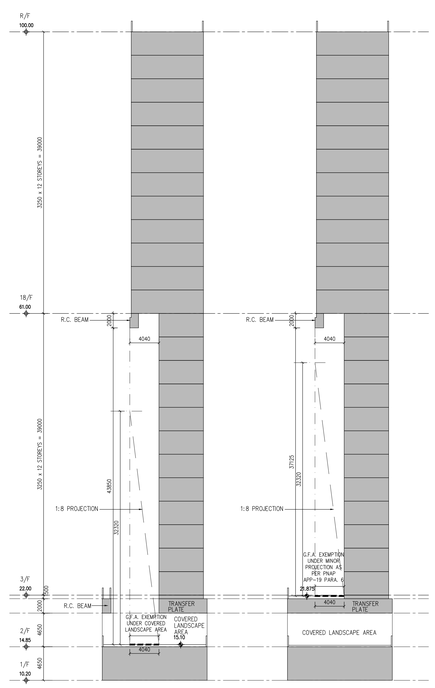

DIAGRAMMATIC SECTION X
SCALE 1:300

DIAGRAMMATIC SECTION Y
SCALE 1:300

B.D. Ref : 80 2/4024/21
BIM Ref : - -
F.S.D. Ref : - -
D.L.O. Ref : - -

Rev.	Description	Drawn	Checked	Approved	Date
-	1st Submission	WY	AW	AL	07/2022
A	2nd Submission	WY	AW	AL	11/2022
B	1st Amendment	TWM	AW	AL	04/2023
C	2nd Amendment	TWM	AW	AL	12/2023
D	3rd Amendment	TWM	AW	AL	04/2024
E	4th Amendment	TWM	AW	AL	08/2024
F	5th Amendment	TWM	AW	AL	12/2024
F	5th Amendment (Re-submission)	TWM	AW	AL	02/2025
G	6th Amendment	TWM	AW	AL	02/2025
H	7th Amendment	TWM	AW	AL	05/2025
I	8th Amendment	TWM	AW	AL	08/2025
J	9th Amendment	TWM	AW	AL	10/2025
J	9th Amendment (Re-submission)				
J	10th Amendment	TWM	AW	AL	12/2025
K	11th Amendment	TWM	AW	AL	02/2026
L	13th Amendment	TWM	AW	AL	06/2026

Type II works
The works shown on these plans are Type II works (Building Amendment) in respect of which consent is applied for the purpose of Fast Track consent application under regulation 33 of the Building (Administration) Regulations.

RONALD LU & PARTNERS

呂元祥建築師事務所

Check all measurements on site. Do not scale off drawings. Any discrepancies in the drawings shall be reported to the Architect and any discrepancies are to be immediately reported to the Architect.
This drawing remains the copyright property of the Architect and is not to be reproduced in whole or in part without permission of the Architect.

Project Title :
PROPOSED DEVELOPMENT AT BAILEY STREET & WING KWONG STREET TO KWA WAN, KOWLOON

Drawing Title :
3RD - 30TH FLOOR PLAN FOR TOWER 5

Drawn By	TWM	Date	08/2025
Checked By	AW	Date	08/2025
Approved By	AL	Date	08/2025
Project No.	21163KL	Issue Date	08/2025

File Path :
I:\Bailey & Wing Kwong Street\DWG\REGS\BEDOP 15 mp4\Hard\P_L73_SP 17.dwg

Scale 1:100 By CAD

Drawing Number : A/GBP/17

Revision Number : L

Drawing Purpose
Buildings Department
Amended Plan

Digitally signed by WONG Chi Kin Kenneth
APVA / 19/95
08 July 2026

Received on 08 July 2026

Plan Approved
(Digitally Signed)
TSOI Lap-san, Lapson
Senior Building Surveyor
for BUILDING AUTHORITY
08 July 2026

Note: This plan has been processed on a curtailed check basis under the centralized processing system as promulgated in PNAP ADM-19. The duties of the authorized person, registered structural engineer and/or registered geotechnical engineer concerned as specified under section 4(3)(b) and the provision of section 14(2)(c) of the Buildings Ordinance are of particular relevance in this regard.

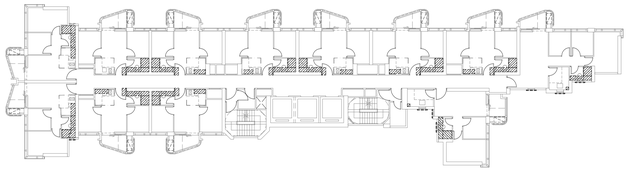

DIAGRAM OF SUNKEN SLAB EXTENT (18th TO 30th FLOOR)

SCALE 1:200

LEGEND:

SUNKEN SLAB

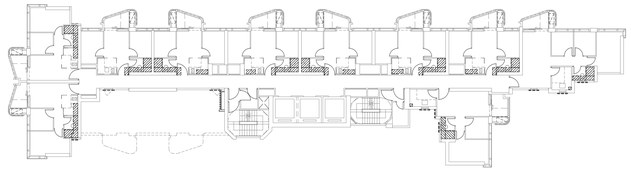

DIAGRAM OF SUNKEN SLAB EXTENT (5th TO 17th FLOOR)

SCALE 1:200

LEGEND:

SUNKEN SLAB

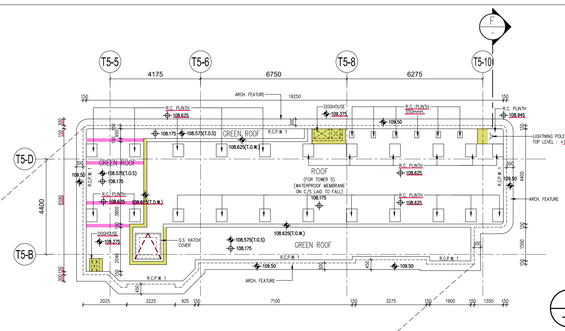

TOP ROOF PLAN – TOWER 5

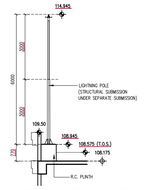

F LIGHTNING POLE SECTION

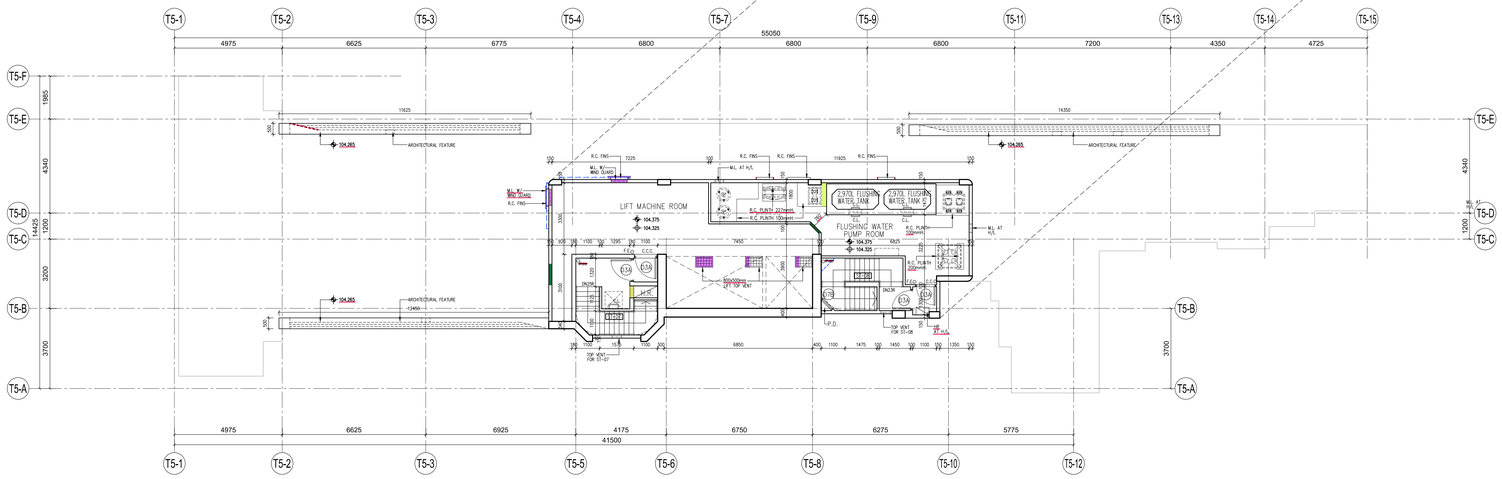

UPPER ROOF PLAN – TOWER 5

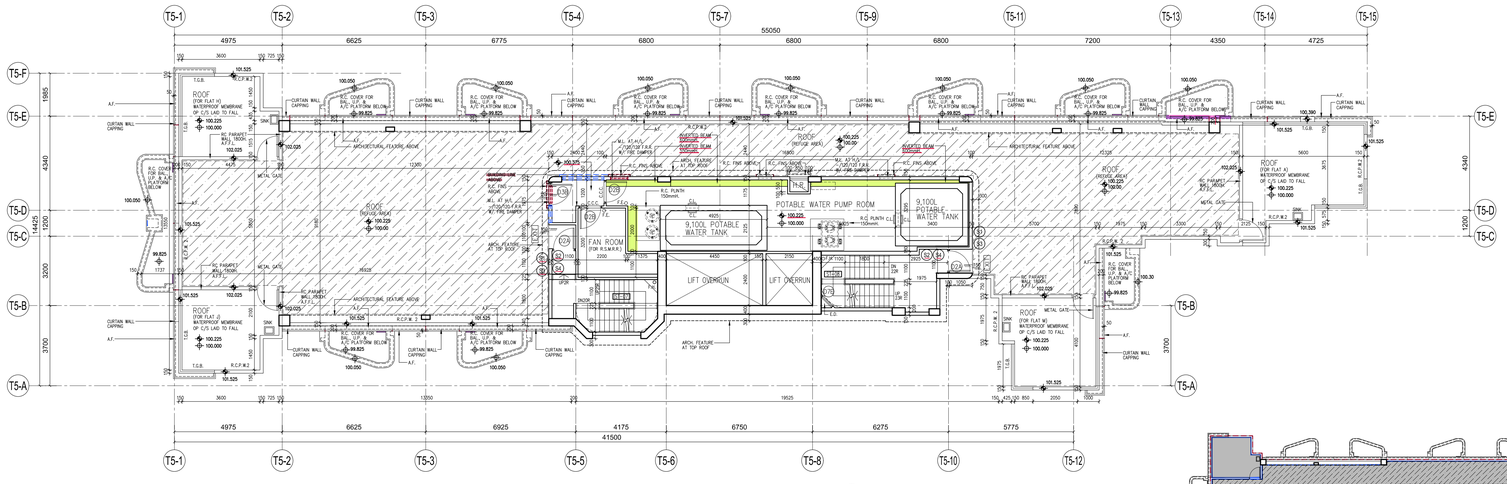

ROOF PLAN – TOWER 5

LEGEND:

- R1 REFUGE FLOOR NOTICE
- R2 STAIR NO. SIGN
- R3 DIRECTIONAL SIGN TO EXIT STAIRCASE
- R4 A SIGN INDICATING THE ENTRANCE TO THE REFUGE FLOOR

NET REFUGE AREA = 245.916 m^2

THE PERCENTAGE OF THE NET REFUGE AREA

THE G.A. OF THE LARGEST FLOOR PLATE = 490.398 m^2

PERCENTAGE OF REFUGE AREA PROVIDED = 245.916 / 490.398 x 100% = 50.146 % > 50% (REQUIRED)

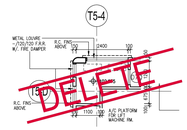

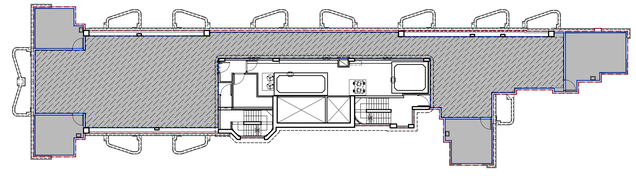

TOWER 5 ROOF FLOOR DIAGRAM

(UNDER PLANNING DEPARTMENT)

SCALE 1:200

AREA OF ROOF = 485.949 m^2

AREA OF ROOF W/O. ROOF TOP STRUCTURE = 323.718 m^2 (66.616 % OF ROOF AREA)

B.D. Ref : 80 2/4024/21

BIM Ref : - --

F.S.D. Ref : - --

D.L.O. Ref : - --

Rev.	Description	Drawn	Checked	Approved	Date
-	1st Submission	WY	AW	AL	07/2022
A	2nd Submission	WY	AW	AL	11/2022
B	1st Amendment	TWM	AW	AL	04/2023
C	2nd Amendment	TWM	AW	AL	12/2023
D	3rd Amendment	TWM	AW	AL	04/2024
D	3rd Amendment (Re-submission)	TWM	AW	AL	05/2024
E	5th Amendment	TWM	AW	AL	12/2024
E	5th Amendment (Re-submission)	TWM	AW	AL	02/2025
F	8th Amendment	TWM	AW	AL	05/2025
G	9th Amendment	TWM	AW	AL	08/2025
G	9th Amendment (Re-submission)	TWM	AW	AL	10/2025
H	10th Amendment	TWM	AW	AL	12/2025
I	11th Amendment	TWM	AW	AL	02/2026

Type III works

The works shown on these plans are Type II works (Building Amendment) in respect of which consent is applied for the purpose of Fast Track consent application under regulation 33 of the Building (Administration) Regulations.

RONALD LU & PARTNERS

呂元祥建築師事務所

Check all measurements on site. Do not scale off drawings.
This drawing is to be read in conjunction with the specification and any discrepancies are to be immediately reported to the Architect.
This drawing is copyright of the Architect and may not be reproduced and is not to be reproduced in whole or in part without permission of the Architect.

Project Title :

PROPOSED DEVELOPMENT AT BAILEY STREET & WING KWONG STREET TO KWA WAN, KOWLOON

Drawing Title :

ROOF FLOOR PLAN FOR TOWER 5

Drawn By	TWM	Date	08/2025
Checked By	AW	Date	08/2025
Approved By	AL	Date	08/2025
Project No.	21163KL	Issue Date	08/2025

File Path : I:\Bldg 2as\2021\21KL Bailey Street\Revit\Working Data\21KL-R2020.2022\21KL T-Tower 5 Amendment_Yang Kwong\21KL-T5_ROOF_R.rvt

Scale 1:100 By CAD

Drawing Number : A/GBP/18

Revision Number : I

Drawing Purpose

Buildings Department
Amended Plan

Digitally signed by LEUNG Ka Man Andy
APCAL 86169
16 March 2026

Received on 16 March 2026

Plan Approved

(Digitally Signed)
TSOI Lap-san, Lapson
Senior Building Surveyor
for BUILDING AUTHORITY
17 March 2026

Note: This plan has been processed on a curtailed check basis under the centralized processing system as promulgated in PNAP ADM-19. The duties of the authorized person, registered structural engineer and/or registered geotechnical engineer concerned as specified under section 4(3)(b) and the provision of section 14(2)(c) of the Buildings Ordinance are of particular relevance in this regard.

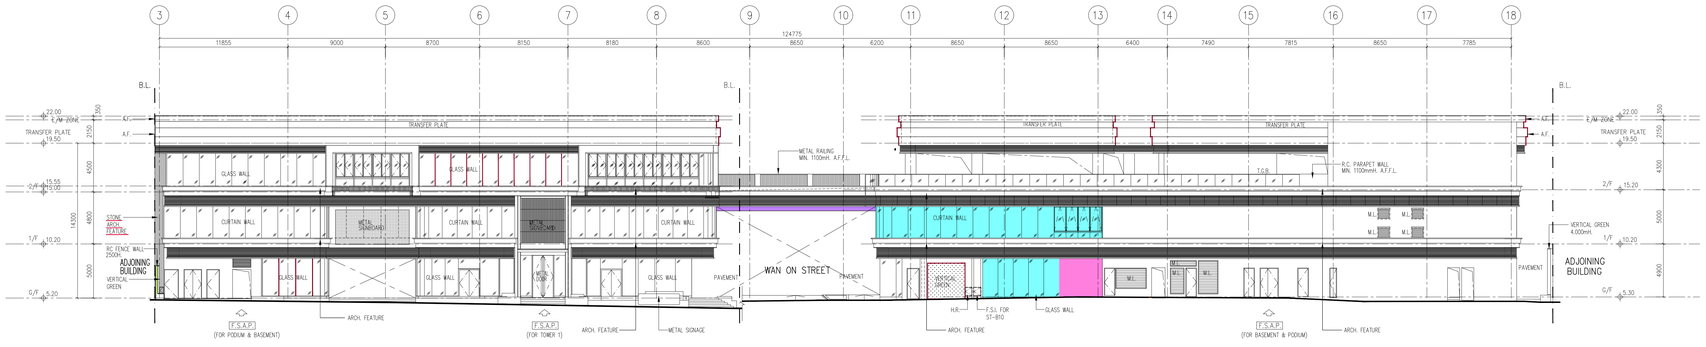

E1 ELEVATION (PODIUM)
SCALE :1:200

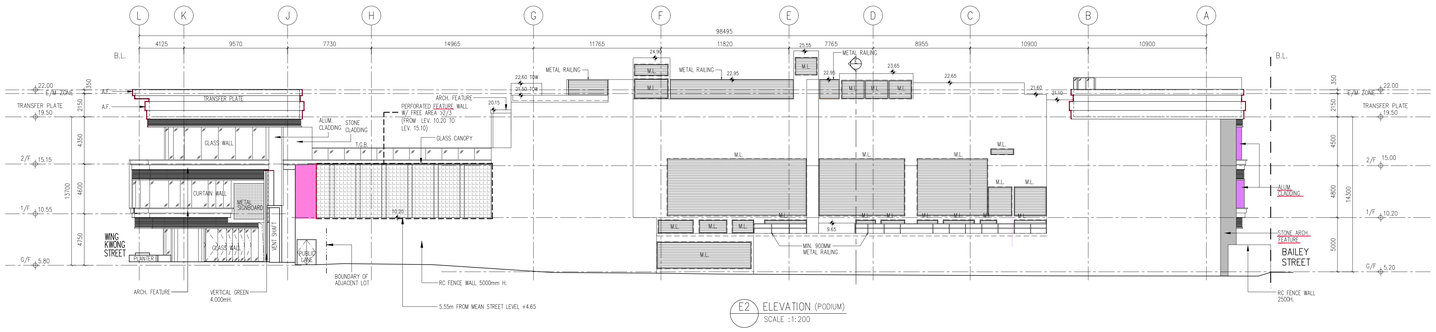

E2 ELEVATION (PODIUM)
SCALE :1:200

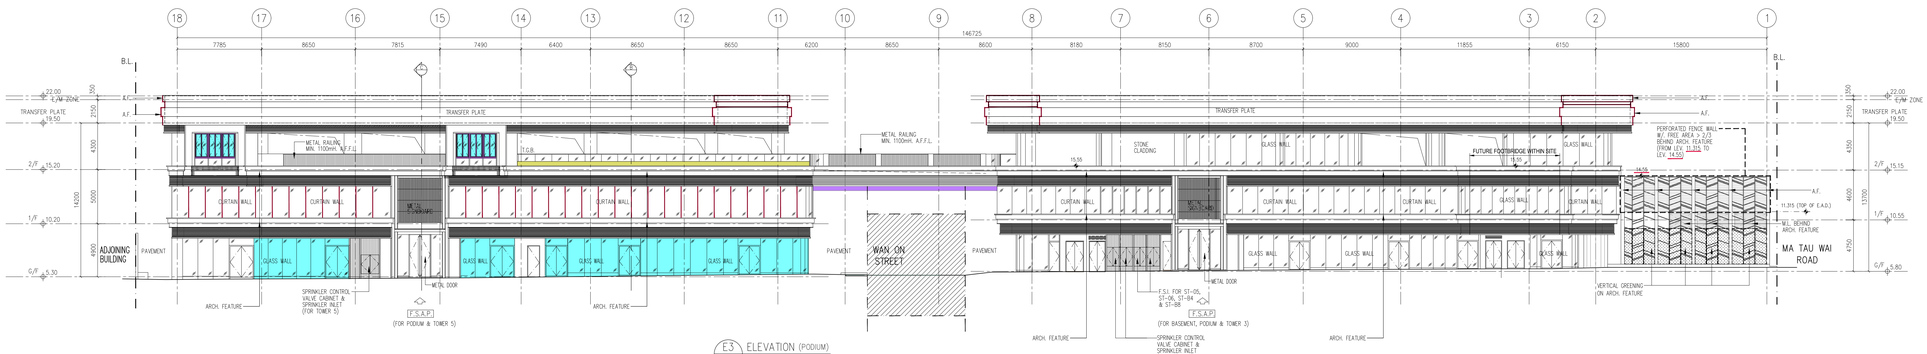

E3 ELEVATION (PODIUM)
SCALE :1:200

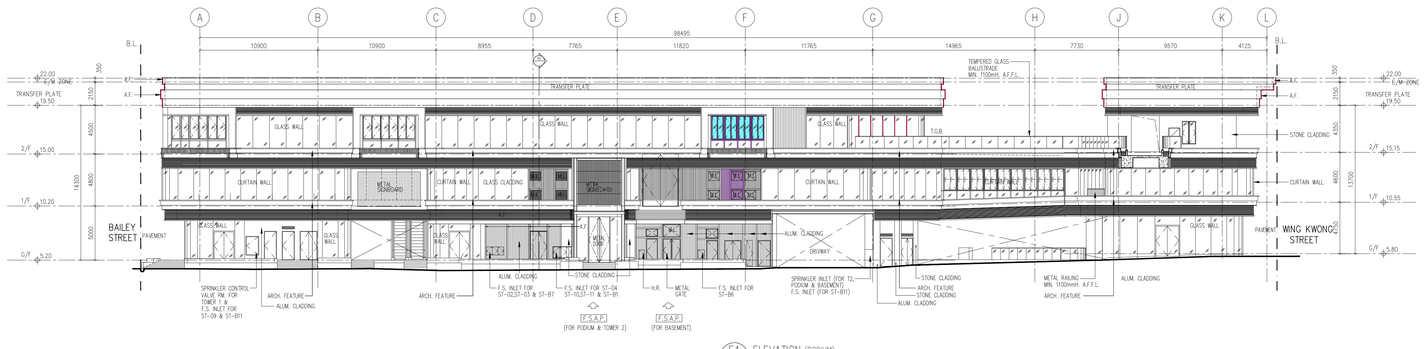

E4 ELEVATION (PODIUM)
SCALE :1:200

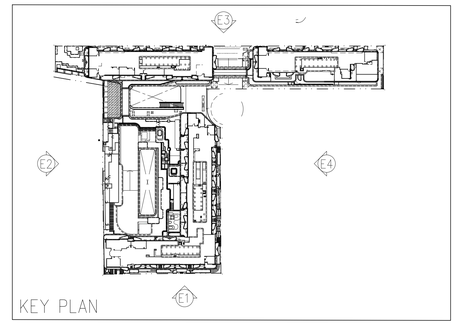

B.D. Ref : 80 2/4024/21

BIM Ref : - -

F.S.D. Ref : - -

D.L.O. Ref : - -

Rev.	Description	Drawn	Checked	Approved	Date
-	1st Submission	WY	AW	AL	07/2022
A	2nd Submission	WY	AW	AL	11/2022
B	1st Amendment	TWM	AW	AL	04/2023
C	2nd Amendment	TWM	AW	AL	12/2023
D	3rd Amendment	TWM	AW	AL	04/2024
D	3rd Amendment (Re-submission)	TWM	AW	AL	05/2024
E	5th Amendment	TWM	AW	AL	12/2024
E	5th Amendment (Re-submission)	TWM	AW	AL	02/2025
F	8th Amendment	LKM	AW	AL	05/2025
G	9th Amendment	LKM	AW	AL	08/2025
G	9th Amendment (Re-submission)	TWM	AW	AL	10/2025
H	10th Amendment	TWM	AW	AL	12/2025
I	11th Amendment	TWM	AW	AL	02/2026

Type II works
The works shown on these plans are Type II works (Building Amendment) in respect of which consent is applied for the purpose of Fast Track consent application under regulation 33 of the Building (Administration) Regulations.

RONALD LU & PARTNERS

呂元祥建築師事務所

Check all measurements on site. Do not scale off drawings. All discrepancies between drawings, specifications and any discrepancies are to be immediately reported to the Architect.
This drawing remains the copyright property of the Architect and is not to be reproduced in whole or in part without permission of the Architect.

Project Title :
PROPOSED DEVELOPMENT AT BAILEY STREET & WING KWONG STREET TO KWA WAN, KOWLOON

Drawing Title :
PODIUM ELEVATION 1, 2, 3 & 4

Drawn By	TWM	Date	08/2025
Checked By	AW	Date	08/2025
Approved By	AL	Date	08/2025
Project No.	21163KL	Issue Date	08/2025

File Path :
I:\Bob Sfty 2\a2021\21KL Bailey Street-Wing Kwong Street\DWG\SUBMISSION\I 11th\Elevation\E_Nett Area\SF275_SF 3.dwg

Scale 1:200 By CAD

Drawing Number : A/GBP/21 Revision Number : I

Drawing Purpose
Buildings Department
Amended Plan

Digitally signed by LEUNG Kit Man Andy
APUAL 86365
16 March 2026

Received on 16 March 2026

Plan Approved
(Digitally Signed)
TSOI Lap-san, Lapson
Senior Building Surveyor
for BUILDING AUTHORITY
17 March 2026

Note: This plan has been processed on a curtailed check basis under the centralized processing system as promulgated in PNAP ADM-19. The duties of the authorized person, registered structural engineer and/or registered geotechnical engineer concerned as specified under section 4(3)(b) and the provision of section 14(2)(c) of the Buildings Ordinance are of particular relevance in this regard.

TOWER 1

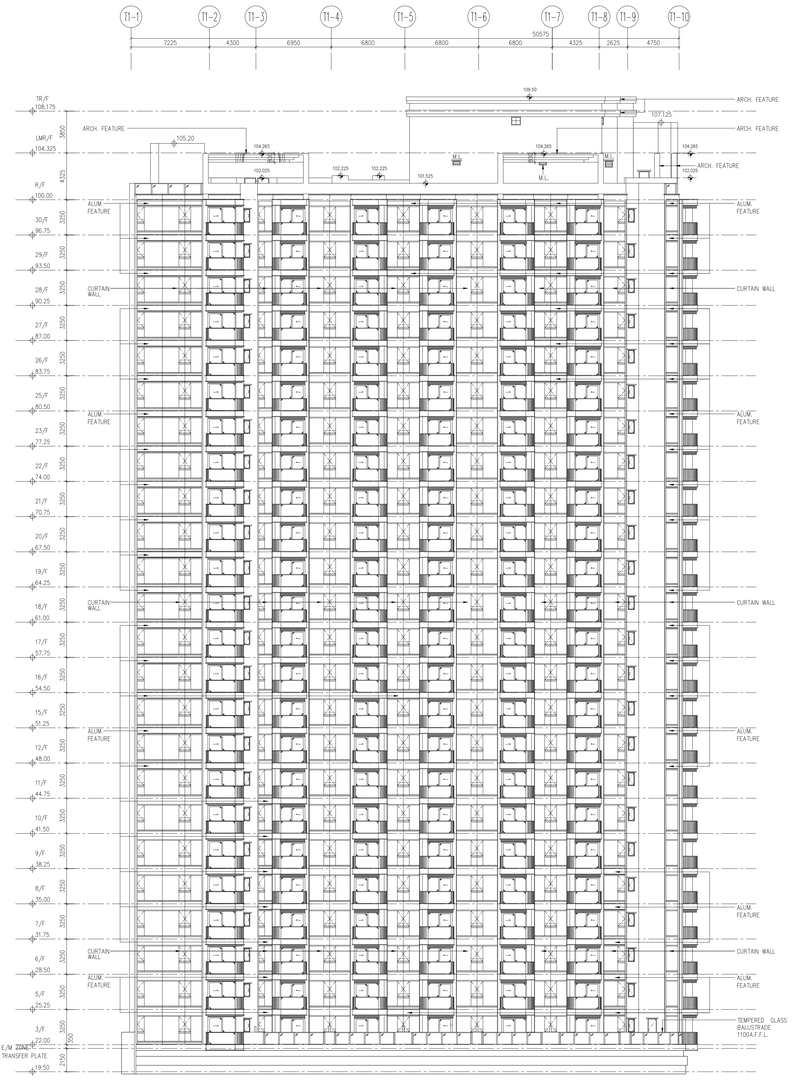
T1-1
T1-2
T1-3
T1-4
T1-5
T1-6
T1-7
T1-8
T1-9
T1-10
7225
4300
6950
6800
6800
6800
50575
4325
2625
4750
TR/F 108.175
LMR/F 104.325
R/F 100.00
30/F 96.75
29/F 93.50
28/F 90.25
27/F 87.00
26/F 83.75
25/F 80.50
23/F 77.25
22/F 74.00
21/F 70.75
20/F 67.50
19/F 64.25
18/F 61.00
17/F 57.75
16/F 54.50
15/F 51.25
12/F 48.00
11/F 44.75
10/F 41.50
9/F 38.25
8/F 35.00
7/F 31.75
6/F 28.50
5/F 25.25
3/F 22.00
E/M ZONE
TRANSFER PLATE
19.50
2650
4325
3250
2750
3250
2750
3250
2750

TOWER 1 & TOWER 2

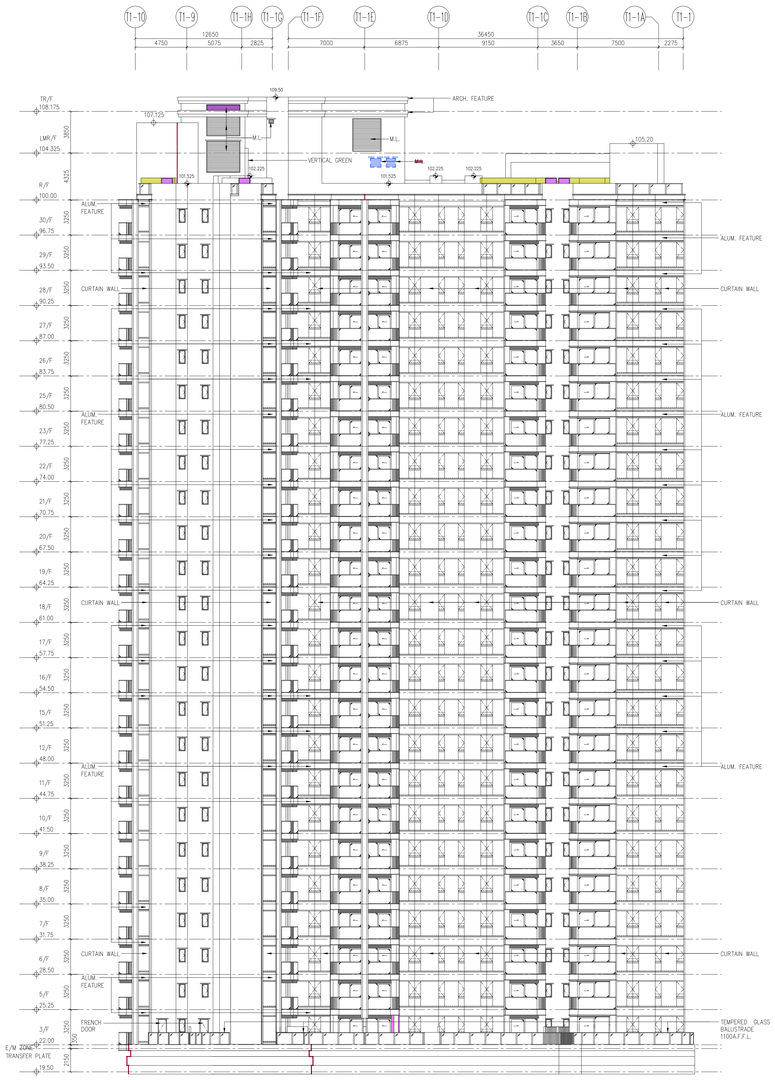

7 ELEVATION

TOWER 1 & TOWER 2

8 ELEVATION

B.D. Ref :	BD 2/4024/21				
BIM Ref :	-	-			
F.S.D. Ref :	-	-			
D.L.O. Ref :	-	-			

Rev.	Description	Drawn	Checked	Approved	Date
-	1st Submission	WY	AW	AL	07/2022
A	2nd Submission	WY	AW	AL	11/2022
B	1st Amendment	TWM	AW	AL	04/2023
C	2nd Amendment	TWM	AW	AL	12/2023
D	3rd Amendment	TWM	AW	AL	04/2024
D	3rd Amendment (Re-submission)	TWM	AW	AL	05/2024
E	5th Amendment	TWM	AW	AL	12/2024
E	5th Amendment (Re-submission)	TWM	AW	AL	02/2025
F	8th Amendment	LKM	AW	AL	05/2025
G	9th Amendment	LKM	AW	AL	08/2025
G	9th Amendment (Re-submission)	TWM	AW	AL	10/2025
H	10th Amendment	TWM	AW	AL	12/2025
I	11th Amendment	TWM	AW	AL	2/2026

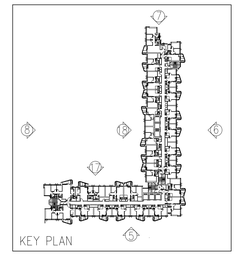

Type II works
The works shown on these plans are Type II works (Building Amendment) in respect of which consent is applied for the purpose of Fast Track consent application under regulation 33 of the Building (Administration) Regulations.

RONALD LU & PARTNERS

呂元祥建築師事務所

Check all measurements on site. Do not scale off drawings.
This drawing is to be read in conjunction with the specification and any discrepancies are to be immediately reported to the Architect.
This drawing remains the copyright property of the Architect and is not to be reproduced in whole or part without permission of the Architect.

Project Title :
PROPOSED DEVELOPMENT
AT BAILEY STREET
& WING KWONG STREET
TO KWA WAN, KOWLOON

Drawing Title :
ELEVATION 7 & 8
(TOWER 1)

Drawn By	TWM	Date	08/2025
Checked By	AW	Date	08/2025
Approved By	AL	Date	08/2025
Project No.	21163KL	Issue Date	08/2025

File Path :
I:\Bailey Proj 2\ac2021\21163KL Bailey Dev\1-0 Proj Aspects\2nd DW\ARCH\SD\SD\SDP 1-7 Rev\Elevation\E Elevation 7 & 8 (TOWER 1).DWG

Scale 1:200 By CAD

Drawing Number : A/GBP/26

Revision Number : I

Drawing Purpose

Buildings Department
Amended Plan

Digitally signed by LEUNG Kit Man Andy
APVA / BORS
16 March 2026

Received on
16 March 2026

Plan Approved
(Digitally Signed)
TSOI Lap-san, Lapson
Senior Building Surveyor
for BUILDING AUTHORITY
17 March 2026

Note: This plan has been processed on a curtailed check basis under the centralized processing system as promulgated in PNAP ADM-19. The duties of the authorized person, registered structural engineer and/or registered geotechnical engineer concerned as specified under section 4(3)(b) and the provision of section 14(2)(c) of the Buildings Ordinance are of particular relevance in this regard.

TOWER 1

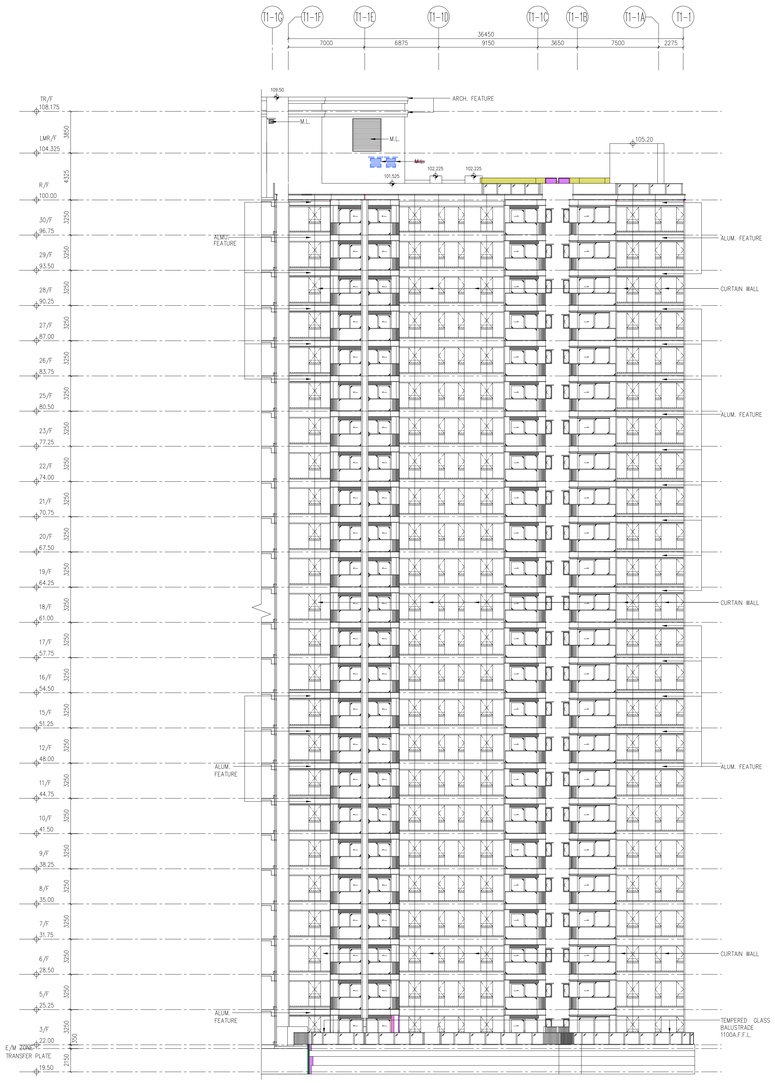

17 ELEVATION

TOWER 2

18 ELEVATION

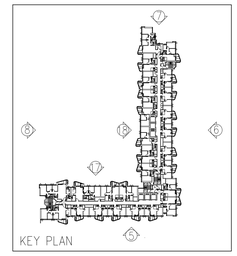

KEY PLAN

B.D. Ref : 80 2/4024/21

BIM Ref : - -

F.S.D. Ref : - -

D.L.O. Ref : - -

Rev.	Description	Drawn	Checked	Approved	Date
-	3rd Amendment	WAC	AW	AL	04/2024
A	5th Amendment	TWM	AW	AL	12/2024
A	5th Amendment (Re-submission)	TWM	AW	AL	02/2025
B	8th Amendment	LKM	AW	AL	05/2025
C	9th Amendment	LKM	AW	AL	08/2025
C	9th Amendment (Re-submission)	TWM	AW	AL	10/2025
D	10th Amendment	TWM	AW	AL	12/2025
E	11th Amendment	TWM	AW	AL	2/2026

Type II works
The works shown on these plans are Type II works (Building Amendment) in respect of which consent is applied for the purpose of Fast Track consent application under regulation 33 of the Building (Administration) Regulations.

RONALD LU & PARTNERS

呂元祥建築師事務所

Check all measurements on site. Do not scale off drawings.
Any discrepancies are to be read in conjunction with the Specification and any discrepancies are to be immediately reported to the Architect.
This drawing remains the copyright property of the Architect and is not to be reproduced in whole or in part without permission of the Architect.

Project Title :
PROPOSED DEVELOPMENT
AT BAILEY STREET
& WING KWONG STREET
TO KWA WAN, KOWLOON

Drawing Title :
ELEVATION 17 & 18
(TOWER 1 & TOWER 2)

Drawn By	TWM	Date	08/2025
Checked By	AW	Date	08/2025
Approved By	AL	Date	08/2025
Project No.	21163KL	Issue Date	08/2025

File Path : T:\Job 3Pro_Jobs\21163KL Bailey Street & Wing Kwong Street\DWG\BD\SUBMISSION\[21163KL Bailey Street & Wing Kwong Street_BP_E1.dwg

Scale	1:200	By	CAD
Drawing Number	A/GBP/26.1	Revision Number	E

Drawing Purpose
Buildings Department
Amended Plan

Digitally signed by LEUNG Ka Man Andy
APVA / BD/83
16 March 2026

Received on
16 March 2026

Plan Approved
(Digitally Signed)
TSOI Lap-san, Lapson
Senior Building Surveyor
for BUILDING AUTHORITY
17 March 2026

Note: This plan has been processed on a curtailed check basis under the centralized processing system as promulgated in PNAP ADM-19. The duties of the authorized person, registered structural engineer and/or registered geotechnical engineer concerned as specified under section 4(3)(b) and the provision of section 14(2)(c) of the Buildings Ordinance are of particular relevance in this regard.

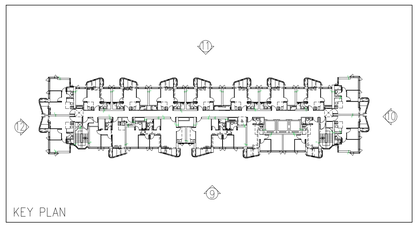

TOWER 3

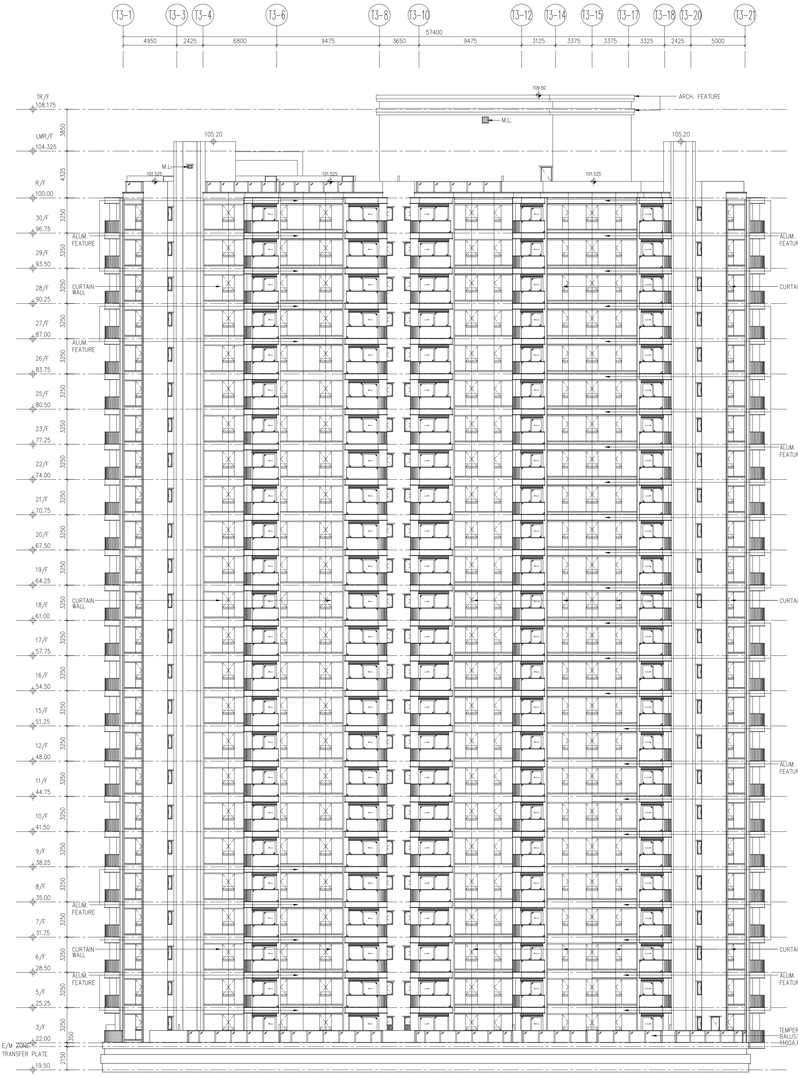

9 ELEVATION

TOWER 3

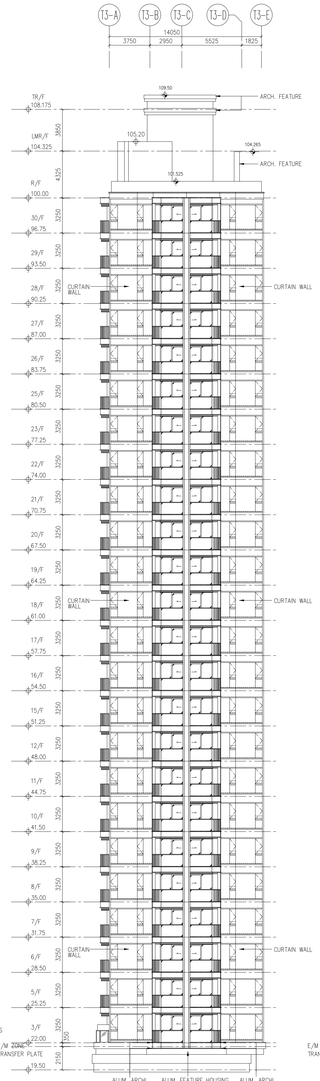

10 ELEVATION

TOWER 3

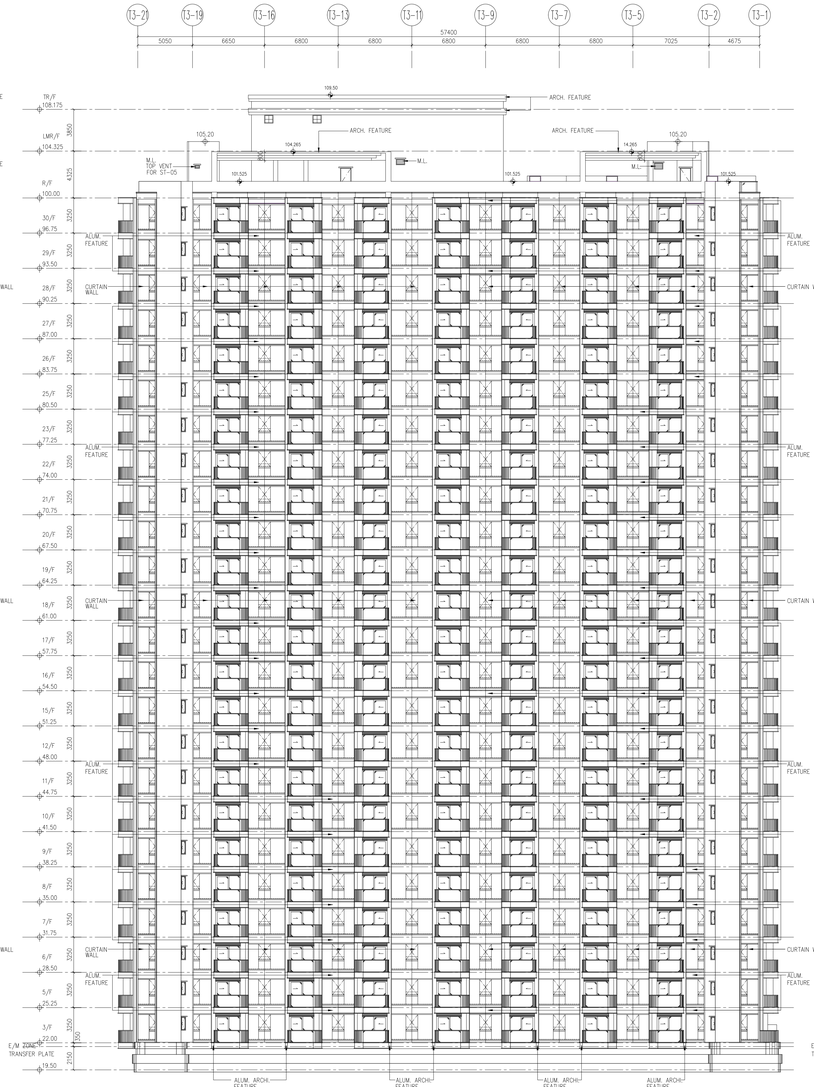

11 ELEVATION

TOWER 3

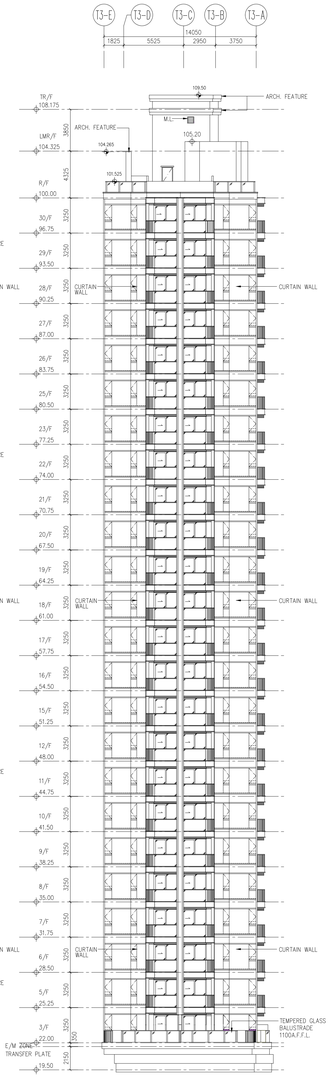

12 ELEVATION

B.D. Ref : 80 2/4024/21

BIM Ref : - -

F.S.D. Ref : - -

D.L.O. Ref : - -

Rev.	Description	Drawn	Checked	Approved	Date
-	1st Submission	WY	AW	AL	07/2022
A	2nd Submission	WY	AW	AL	11/2022
B	1st Amendment	TWM	AW	AL	04/2023
C	2nd Amendment	TWM	AW	AL	12/2023
D	3rd Amendment	TWM	AW	AL	04/2024
D	3rd Amendment (Re-submission)	TWM	AW	AL	05/2024
E	5th Amendment	TWM	AW	AL	12/2024
E	5th Amendment (Re-submission)	TWM	AW	AL	02/2025
F	8th Amendment	LKM	AW	AL	05/2025
G	9th Amendment	LKM	AW	AL	08/2025
G	9th Amendment (Re-submission)	TWM	AW	AL	10/2025
H	10th Amendment	TWM	AW	AL	12/2025
I	11th Amendment	TWM	AW	AL	02/2026
J	12th Amendment	TWM	AW	AL	05/2026

Type II works
The works shown on these plans are Type II works (Building Amendment) in respect of which consent is applied for the purpose of Fast Track consent application under regulation 33 of the Building (Administration) Regulations.

RONALD LU & PARTNERS

呂元祥建築師事務所

Check all dimensions on site. Do not scale off drawing. Use the dimensions as the read or written for construction and any discrepancies are to be immediately reported to the Architect.
This drawing remains the copyright property of the Architect and is not to be reproduced in whole or in part without permission of the Architect.

Project Title :
PROPOSED DEVELOPMENT
AT BAILEY STREET
& WING KWONG STREET
TO KWA WAN, KOWLOON

Drawing Title :
ELEVATION 9, 10, 11 & 12
(TOWER 2)

Drawn By	TWM	Date	08/2025
Checked By	AW	Date	08/2025
Approved By	AL	Date	08/2025
Project No.	21163KL	Issue Date	08/2025

File Path :
I:\Bailey, &Wing, Street\2021\21163KL Bailey Street & Wing Kwong Street\DWG\WORKING\BIM\21163KL_GBP_27.dwg

Scale 1:200 By CAD

Drawing Number : A/GBP/27

Revision Number : J

Drawing Purpose

Buildings Department
Amended Plan

Digitally signed by LEUNG Ka Man Andy
APVA | 80/85
27 May 2026

Received on
27 May 2026

Plan Approved
(Digitally Signed)
TSOI Lap-san, Lapson
Senior Building Surveyor
for BUILDING AUTHORITY
02 June 2026

Note: This plan has been processed on a curtailed check basis under the centralized processing system as promulgated in PNAP ADM-19. The duties of the authorized person, registered structural engineer and/or registered geotechnical engineer concerned as specified under section 4(3)(b) and the provision of section 14(2)(c) of the Buildings Ordinance are of particular relevance in this regard.

B.D. Ref. : 80 2/4024/21

BIM Ref. : - --

F.S.D. Ref. : - --

D.L.O. Ref. : - --

Rev.	Description	Drawn	Checked	Approved	Date
-	1st Submission	WY	AW	AL	07/2022
A	2nd Submission	WY	AW	AL	11/2022
B	1st Amendment	TWM	AW	AL	04/2023
C	2nd Amendment	TWM	AW	AL	12/2023
D	3rd Amendment	TWM	AW	AL	04/2024
D	3rd Amendment (Re-submission)	TWM	AW	AL	05/2024
E	5th Amendment	TWM	AW	AL	12/2024
E	5th Amendment (Re-submission)	TWM	AW	AL	02/2025
F	8th Amendment	LKM	AW	AL	05/2025
G	9th Amendment	LKM	AW	AL	08/2025
G	9th Amendment (Re-submission)	TWM	AW	AL	10/2025
H	10th Amendment	TWM	AW	AL	12/2025
I	11th Amendment	TWM	AW	AL	02/2026
J	12th Amendment	TWM	AW	AL	05/2026
K	13th Amendment	TWM	AW	AL	06/2026

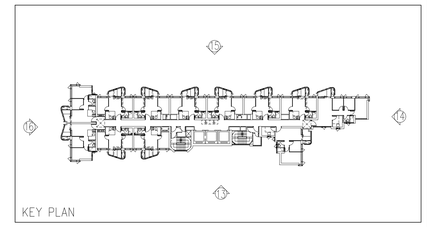

TOWER 5

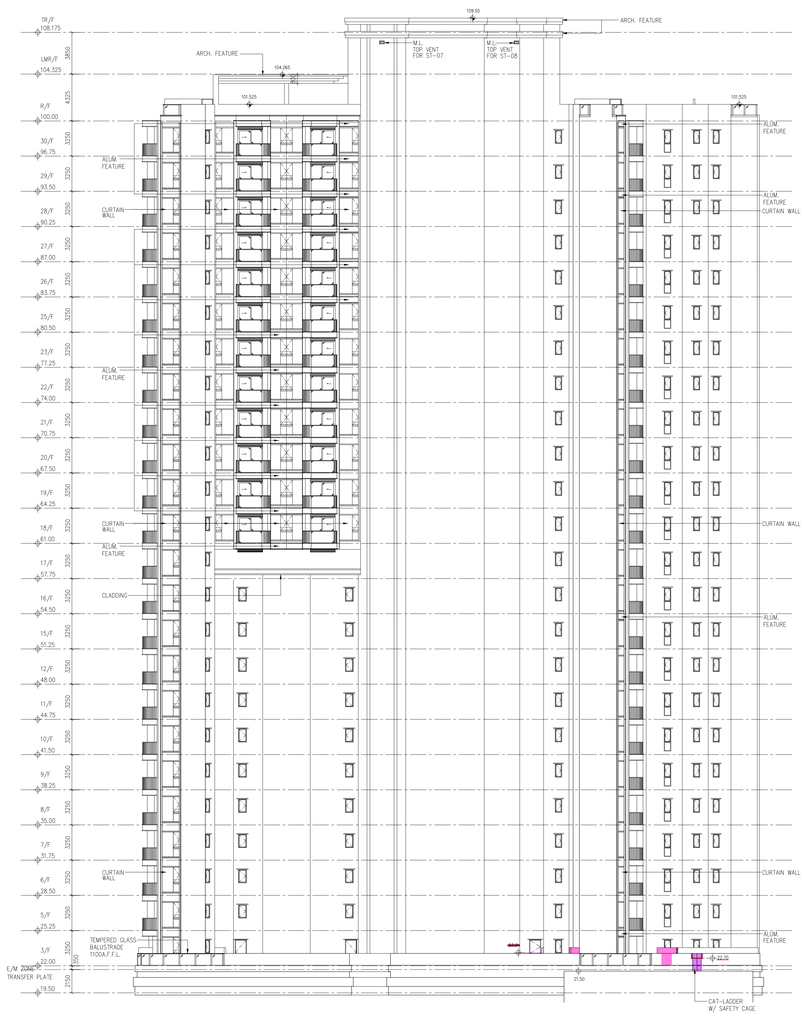

13 ELEVATION

TOWER 5

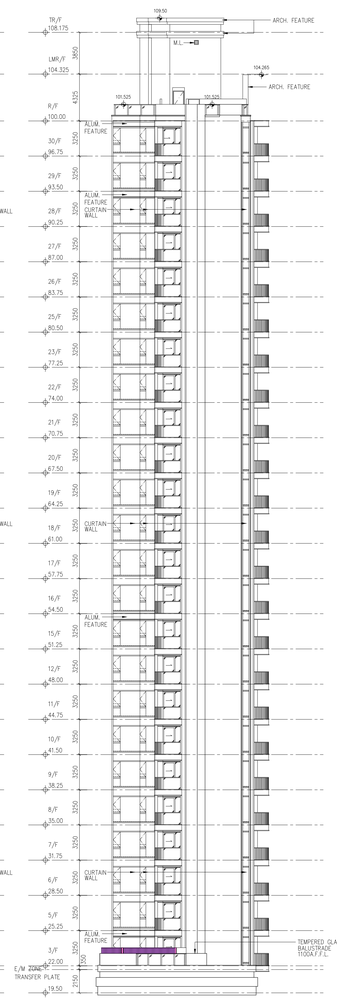

14 ELEVATION

TOWER 5

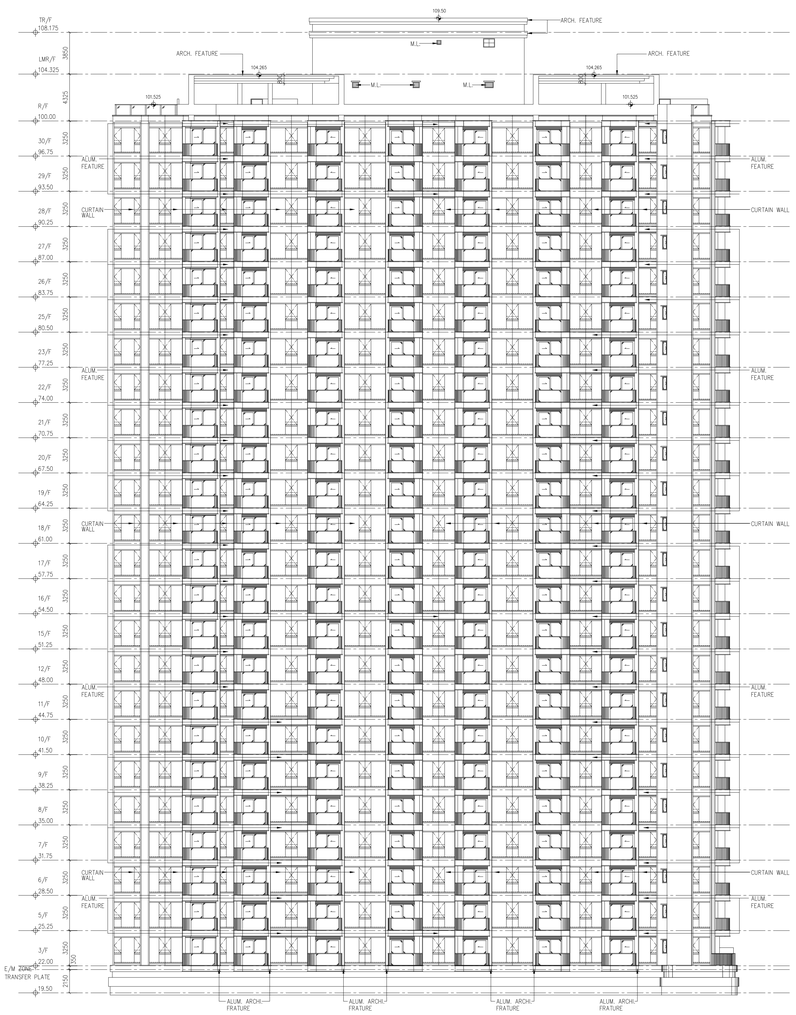

15 ELEVATION

TOWER 5

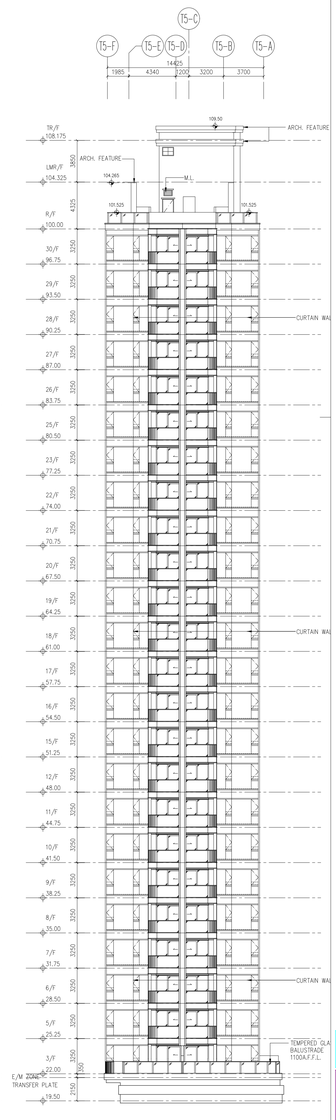

16 ELEVATION

Type II works

The works shown on these plans are Type II works (Building Amendment) in respect of which consent is applied for the purpose of Fast Track consent application under regulation 33 of the Building (Administration) Regulations.

RONALD LU & PARTNERS

呂元祥建築師事務所

Check all measurements on site. Do not scale off drawings.
Any discrepancies are to be read in conjunction with drawings and any discrepancies are to be immediately reported to the Architect.
This drawing remains the copyright property of the Architect and is not to be reproduced in whole or in part without permission of the Architect.

Project Title :
PROPOSED DEVELOPMENT
AT BAILEY STREET
& WING KWONG STREET
TO KWA WAN, KOWLOON

Drawing Title :
ELEVATION 13, 14, 15 & 16
(TOWER 3)

Drawn By	TWM	Date	08/2025
Checked By	AW	Date	08/2025
Approved By	AL	Date	08/2025
Project No.	21163KL	Issue Date	08/2025

File Path :
I:\Bailey &Wing Jobs\2021\KL Bailey Street & Wing Kwong Street\WORKING\BIM\DWF 作 mod level\PLOT A_DWF_BIM.dwg

Scale 1:200 By CAD

Drawing Number : A/GBP/28

Revision Number : K

Drawing Purpose

Buildings Department
Amended Plan

Digitally signed by WONG Chi Kin Kenneth
APAL/ 19/95
08 July 2026

Received on
08 July 2026

Plan Approved

(Digitally Signed)
TSOI Lap-sam, Lapson
Senior Building Surveyor
for BUILDING AUTHORITY
08 July 2026

Note: This plan has been processed on a curtailed check basis under the centralized processing system as promulgated in PNAP ADM-19. The duties of the authorized person, registered structural engineer and/or registered geotechnical engineer concerned as specified under section 4(3)(b) and the provision of section 14(2)(c) of the Buildings Ordinance are of particular relevance in this regard.