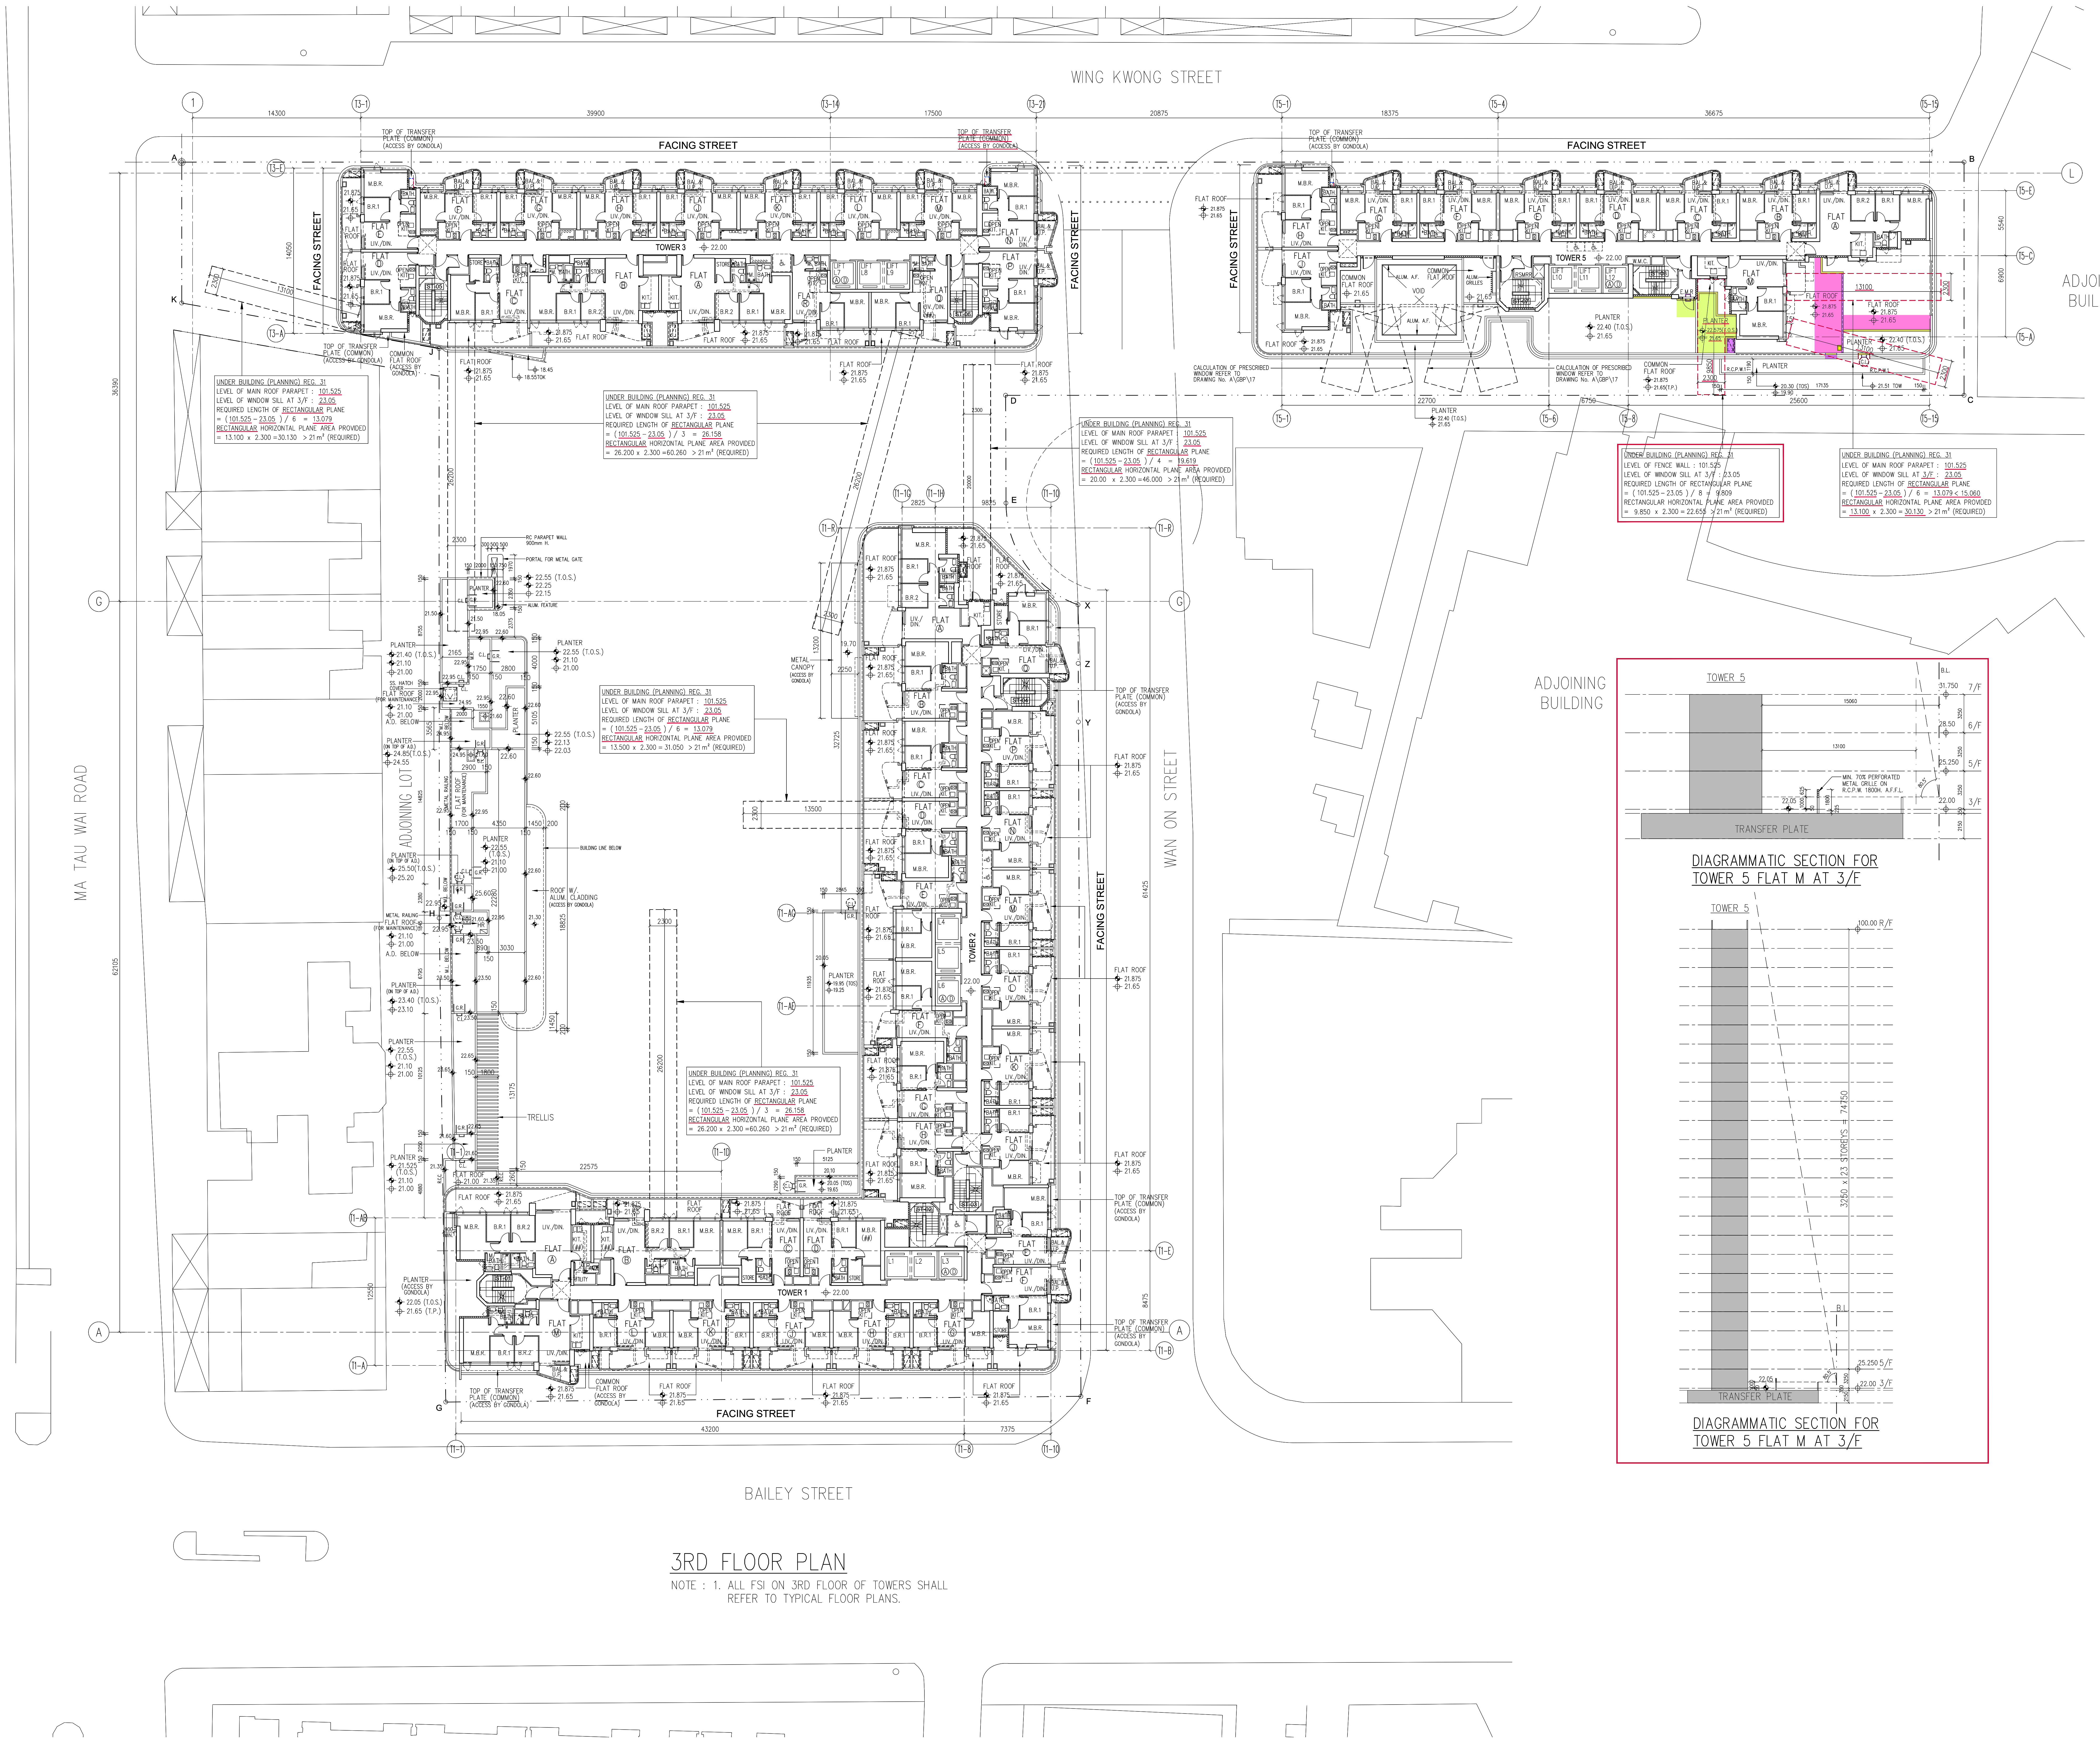
WING KWONG STREET
BAILEY STREET
MA TAU WAI ROAD
WAN ON STREET
FACING STREET
ADJOINING BUILDING
ADJOINING LOT
TOWER 1
TOWER 2
TOWER 3
TOWER 5
TRANSFER PLATE
TRELLIS
METAL CANOPY (ACCESS BY GONDOLA)
TOP OF TRANSFER PLATE (COMMON) (ACCESS BY GONDOLA)
COMMON FLAT ROOF (ACCESS BY GONDOLA)
CALCULATION OF PRESCRIBED WINDOW REFER TO DRAWING No. A\GBP\17
MIN. 70% PERFORATED METAL GRILLE ON R.C.P.W. 1800H. A.F.F.L.
7/F
6/F
5/F
3/F
R/F
32/F0 x 23 STOREYS = 74250

UNDER BUILDING (PLANNING) REG. 31
LEVEL OF MAIN ROOF PARAPET : 101.525
LEVEL OF WINDOW SILL AT 3/F : 23.05
REQUIRED LENGTH OF RECTANGULAR PLANE
= (101.525 – 23.05) / 6 = 13.079
RECTANGULAR HORIZONTAL PLANE AREA PROVIDED
= 13.100 x 2.300 =30.130 > 21 m² (REQUIRED)

UNDER BUILDING (PLANNING) REG. 31
LEVEL OF MAIN ROOF PARAPET : 101.525
LEVEL OF WINDOW SILL AT 3/F : 23.05
REQUIRED LENGTH OF RECTANGULAR PLANE
= (101.525 – 23.05) / 3 = 26.158
RECTANGULAR HORIZONTAL PLANE AREA PROVIDED
= 26.200 x 2.300 =60.260 > 21 m² (REQUIRED)

UNDER BUILDING (PLANNING) REG. 31
LEVEL OF MAIN ROOF PARAPET : 101.525
LEVEL OF WINDOW SILL AT 3/F : 23.05
REQUIRED LENGTH OF RECTANGULAR PLANE
= (101.525 – 23.05) / 4 = 19.619
RECTANGULAR HORIZONTAL PLANE AREA PROVIDED
= 20.00 x 2.300 =46.000 > 21 m² (REQUIRED)

UNDER BUILDING (PLANNING) REG. 31
LEVEL OF FENCE WALL : 101.525
LEVEL OF WINDOW SILL AT 3/F : 23.05
REQUIRED LENGTH OF RECTANGULAR PLANE
= (101.525 – 23.05) / 8 = 9.809
RECTANGULAR HORIZONTAL PLANE AREA PROVIDED
= 9.850 x 2.300 = 22.655 > 21 m² (REQUIRED)

UNDER BUILDING (PLANNING) REG. 31
LEVEL OF MAIN ROOF PARAPET : 101.525
LEVEL OF WINDOW SILL AT 3/F : 23.05
REQUIRED LENGTH OF RECTANGULAR PLANE
= (101.525 – 23.05) / 6 = 13.079 < 15.060
RECTANGULAR HORIZONTAL PLANE AREA PROVIDED
= 13.100 x 2.300 = 30.130 > 21 m² (REQUIRED)

UNDER BUILDING (PLANNING) REG. 31
LEVEL OF MAIN ROOF PARAPET : 101.525
LEVEL OF WINDOW SILL AT 3/F : 23.05
REQUIRED LENGTH OF RECTANGULAR PLANE
= (101.525 – 23.05) / 6 = 13.079
RECTANGULAR HORIZONTAL PLANE AREA PROVIDED
= 13.500 x 2.300 = 31.050 > 21 m² (REQUIRED)

UNDER BUILDING (PLANNING) REG. 31
LEVEL OF MAIN ROOF PARAPET : 101.525
LEVEL OF WINDOW SILL AT 3/F : 23.05
REQUIRED LENGTH OF RECTANGULAR PLANE
= (101.525 – 23.05) / 3 = 26.158
RECTANGULAR HORIZONTAL PLANE AREA PROVIDED
= 26.200 x 2.300 =60.260 > 21 m² (REQUIRED)

DIAGRAMMATIC SECTION FOR TOWER 5 FLAT M AT 3/F

DIAGRAMMATIC SECTION FOR TOWER 5 FLAT M AT 3/F

3RD FLOOR PLAN

NOTE : 1. ALL FSI ON 3RD FLOOR OF TOWERS SHALL
REFER TO TYPICAL FLOOR PLANS.

B.D. Ref : BD 2/4024/21
BIM Ref : - --
F.S.D. Ref : - --
D.L.O. Ref : - --

Rev.	Description	Drawn	Checked	Approved	Date
-	1st Submission	WY	AW	AL	07/2022
A	2nd Submission	WY	AW	AL	11/2022
B	1st Amendment	TWM	AW	AL	04/2023
C	2nd Amendment	TWM	AW	AL	12/2023
D	3rd Amendment	TWM	AW	AL	04/2024
D	3rd Amendment (Re-submission)	TWM	AW	AL	05/2024
E	5th Amendment	TWM	AW	AL	12/2024
E	5th Amendment (Re-submission)	TWM	AW	AL	02/2025
F	6th Amendment	TWM	AW	AL	02/2025
G	8th Amendment	TWM	AW	AL	05/2025
H	9th Amendment	TWM	AW	AL	08/2025
H	9th Amendment (Re-submission)	TWM	AW	AL	10/2025
I	10th Amendment	TWM	AW	AL	12/2025
J	11th Amendment	TWM	AW	AL	02/2026
K	13th Amendment	TWM	AW	AL	06/2026

Type II works
The works shown on these plans are Type II works (Building Amendment) in respect of which consent is applied for the purpose of Fast Track consent application under regulation 33 of the Building (Administration) Regulations.

RONALD LU
& PARTNERS
呂 元 祥 建 築 師 事 務 所

Check all measurements on site. Do not scale off drawings.
This drawing is to be read in conjunction with the specification and any discrepancies are to be immediately reported to the Architect.
This drawing remains the copyright property of the Architect and is not to be reproduced in whole or in part without permission of the Architect.

Project Title :
PROPOSED DEVELOPMENT
AT BAILEY STREET
& WING KWONG STREET
TO KWA WAN, KOWLOON

Drawing Title :
3RD FLOOR PLAN

Drawn By	TWM	Date	08/2025
Checked By	AW	Date	08/2025
Approved By	AL	Date	08/2025
Project No.	21163KL	Issue Date	08/2025

File Path :
U:\Studio_B\Proj_Data\2021\21163KL_Bailey Street & Wing Kwong Street\DRAWING\SUB\BD\GBP_15_Hand Amend\PLOT\A_GBP_09.dwg

Scale 1:200 By CAD

Drawing Number : A/GBP/09
Revision Number : K

Drawing Purpose
Buildings Department
Amended Plan

Digitally signed by
WONG Chi Kin Kenneth
AP(A) 19/95
08 July 2026

Received on
08 July 2026

Plan Approved
(Digitally Signed)
TSOI Lap-san, Lapson
Senior Building Surveyor
for BUILDING AUTHORITY
08 July 2026

Note: This plan has been processed on a curtailed check basis under the centralized processing system as promulgated in PNAP ADM-19. The duties of the authorized person, registered structural engineer and/or registered geotechnical engineer concerned as specified under section 4(3)(b) and the provision of section 14(2)(c) of the Buildings Ordinance are of particular relevance in this regard.