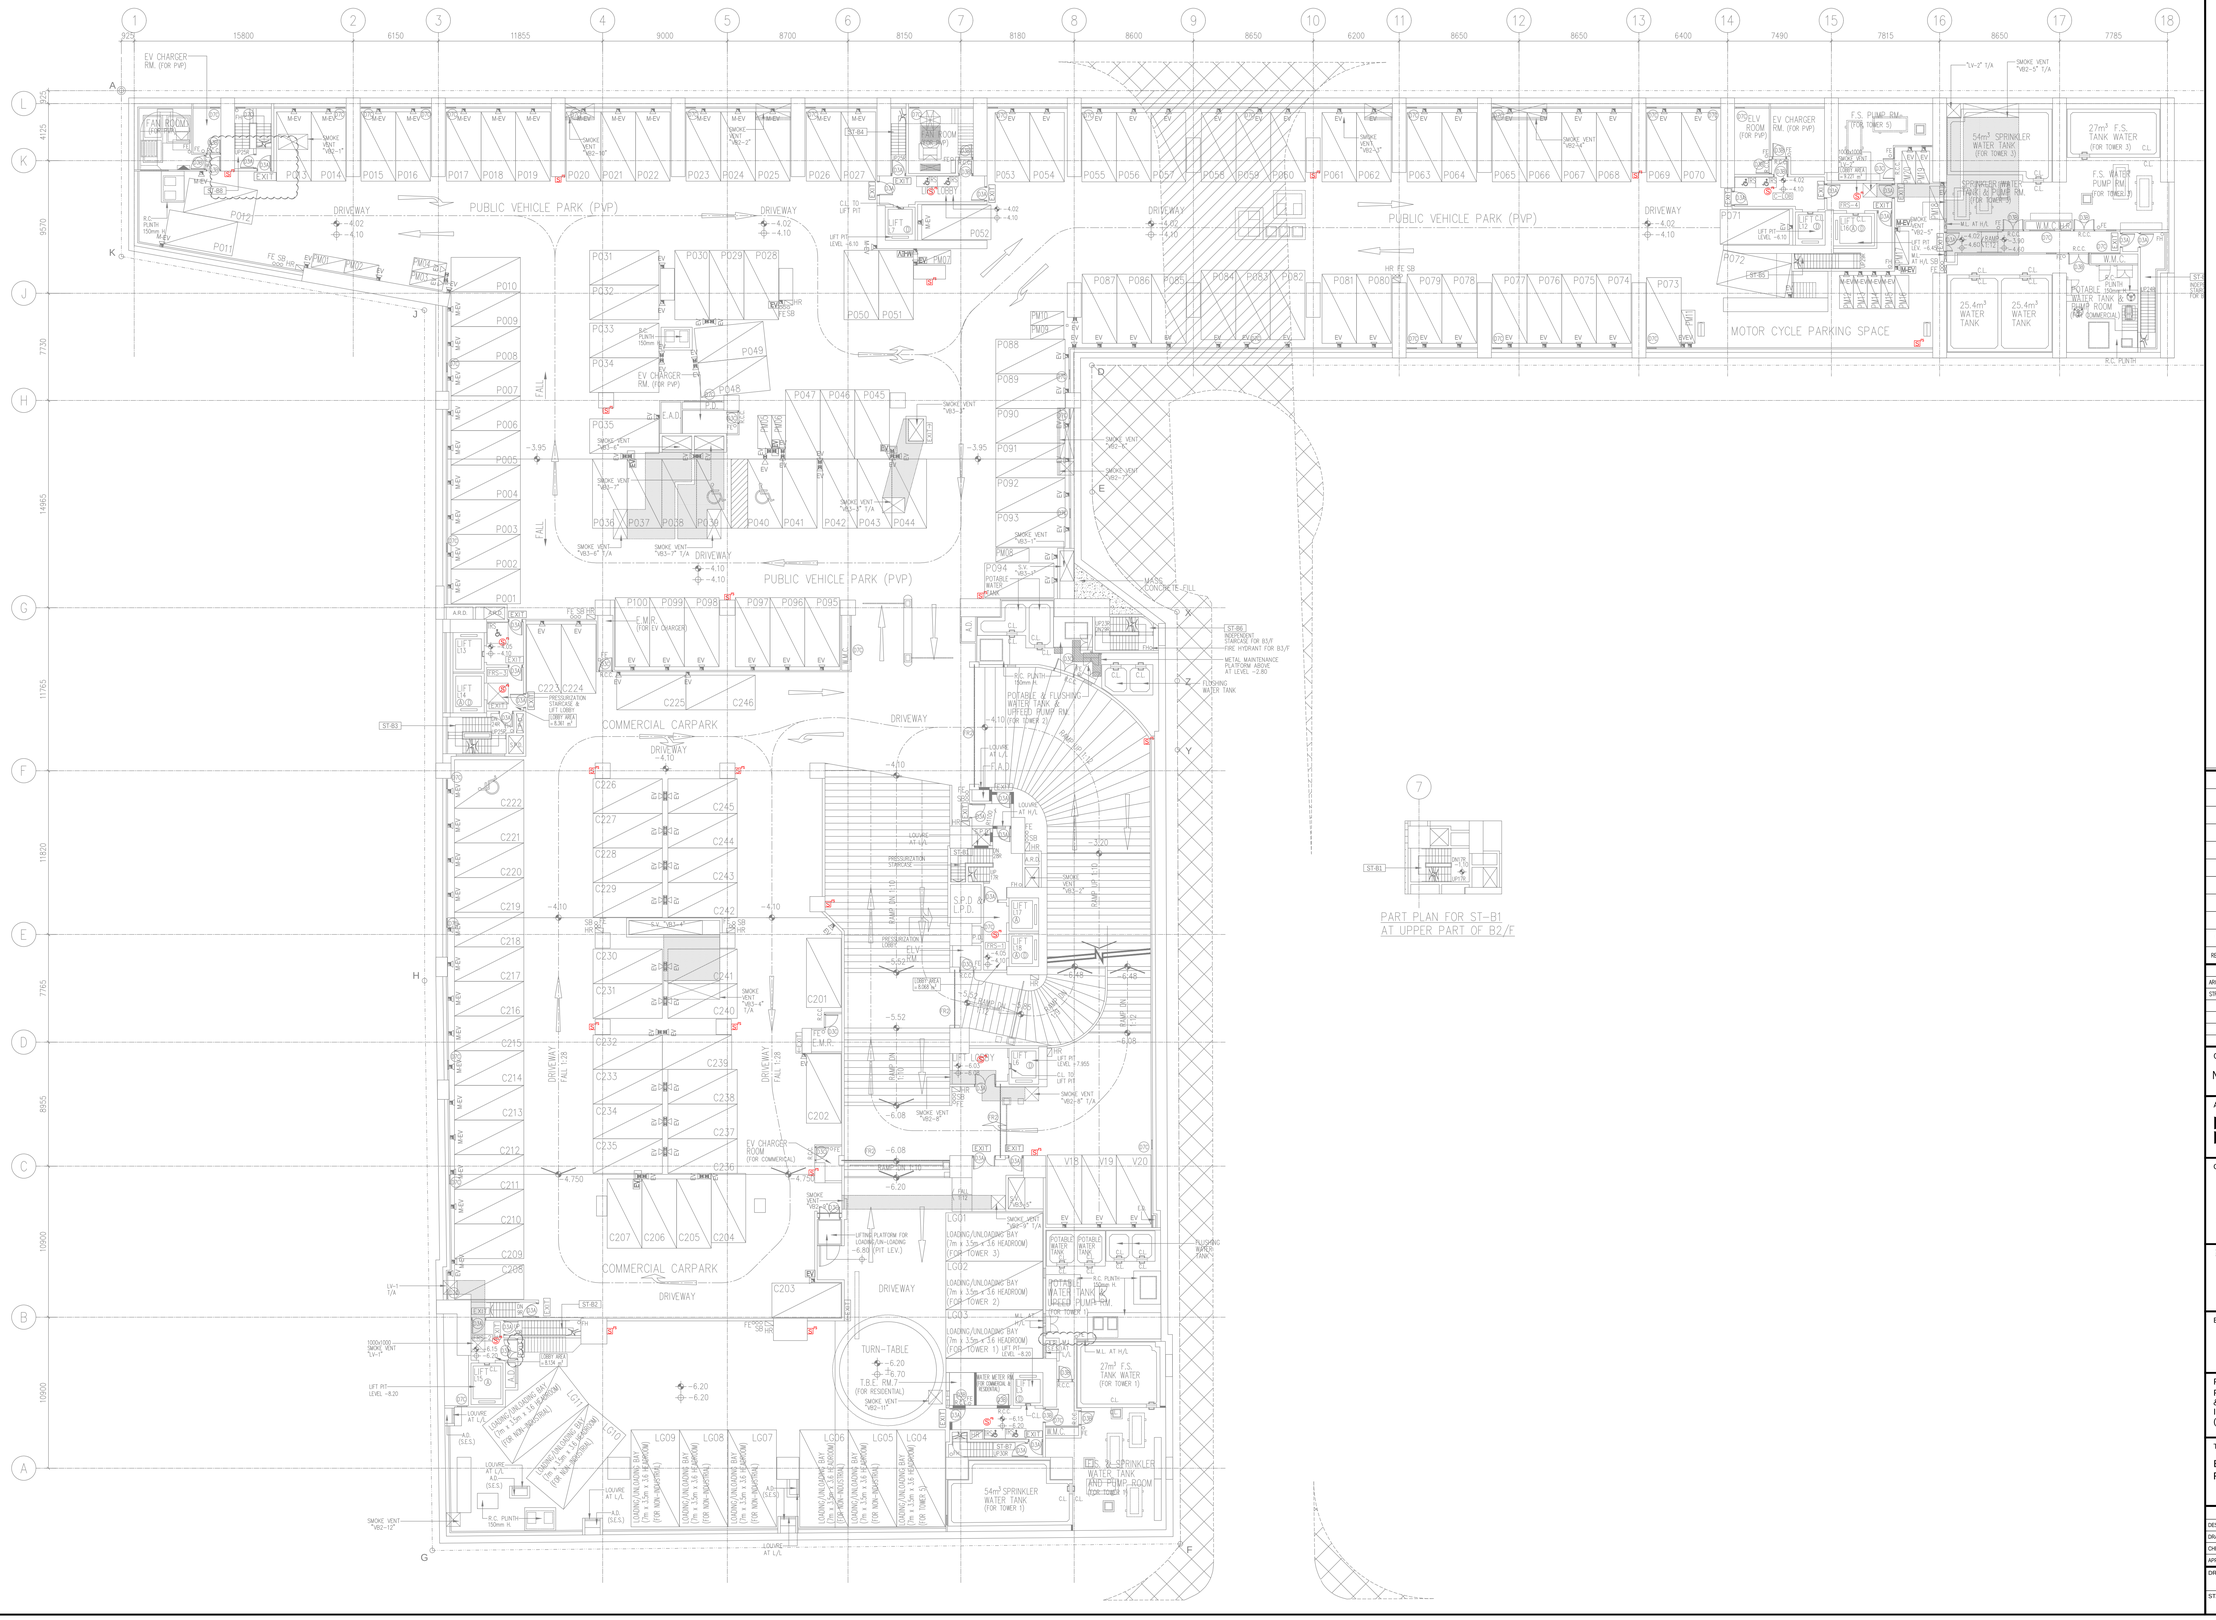


LEGEND:

- WALL MOUNTED SPEAKER FOR FS
- CEILING MOUNT SPEAKER FOR FS
- WALL MOUNTED SPEAKER FOR FS & BGM
- CEILING MOUNT SPEAKER FOR FS & BGM

REV.	DESCRIPTION	BY	DATE
0	1ST SUBMISSION	AC	10/2024

	DRAWING REFERENCE	REV.	DATE
ARCHITECTURAL	A/GBP/10 (11th AMENDMENT)		02/2026
STRUCTURAL			

CLIENT

NATION STAR DEVELOPMENT LIMITED

ARCHITECT

RONALD LU & PARTNERS

Ronald Lu & Partners (Hong Kong) Ltd.
呂元祥建築師事務所(香港)有限公司
33rd Floor, Wu Chung House,
213 Queen's Road East,
Wanchai, Hong Kong

CONSULTANT

wsp

7/F, One Kowloon
1 Wang Yuen Street
Kowloon Bay, Hong Kong

MAIN CONTRACTOR

中國海外房屋工程有限公司
CHINA OVERSEAS BUILDING CONSTRUCTION LIMITED

E & M CONTRACTOR

U-Tech Engineering Company Limited
Member of Tongda Group
6/F, TOC, 157 KAS WAN ROAD, KOWLOON, HONG KONG.
TEL : (852) 2765 – 5666 ; FAX : (852) 2392 – 7422

PROJECT

PROPOSED DEVELOPMENT AT BAILEY STREET & WING KWONG STREET, TO KWA WAN, KLN.
INLAND LOT NO. 11279
(URA PROJECT KC-009)

TITLE

ELV LAYOUT FOR BASEMENT 2 FLOOR PLAN

	NAME	INITIAL	DATE
DESIGNED BY	RONALD WONG		02/10/2024
DRAWN BY	AAREN CHU		02/10/2024
CHECKED BY	SAM KWOK		02/10/2024
APPROVED BY	WILSON YUEN		02/10/2024

DRAWING NO.	D/EE/503	DATE 02/10/2024	REV. 0
STATUS		SCALE 1:150 @ A0	
		DO NOT SCALE THE DRAWING.	