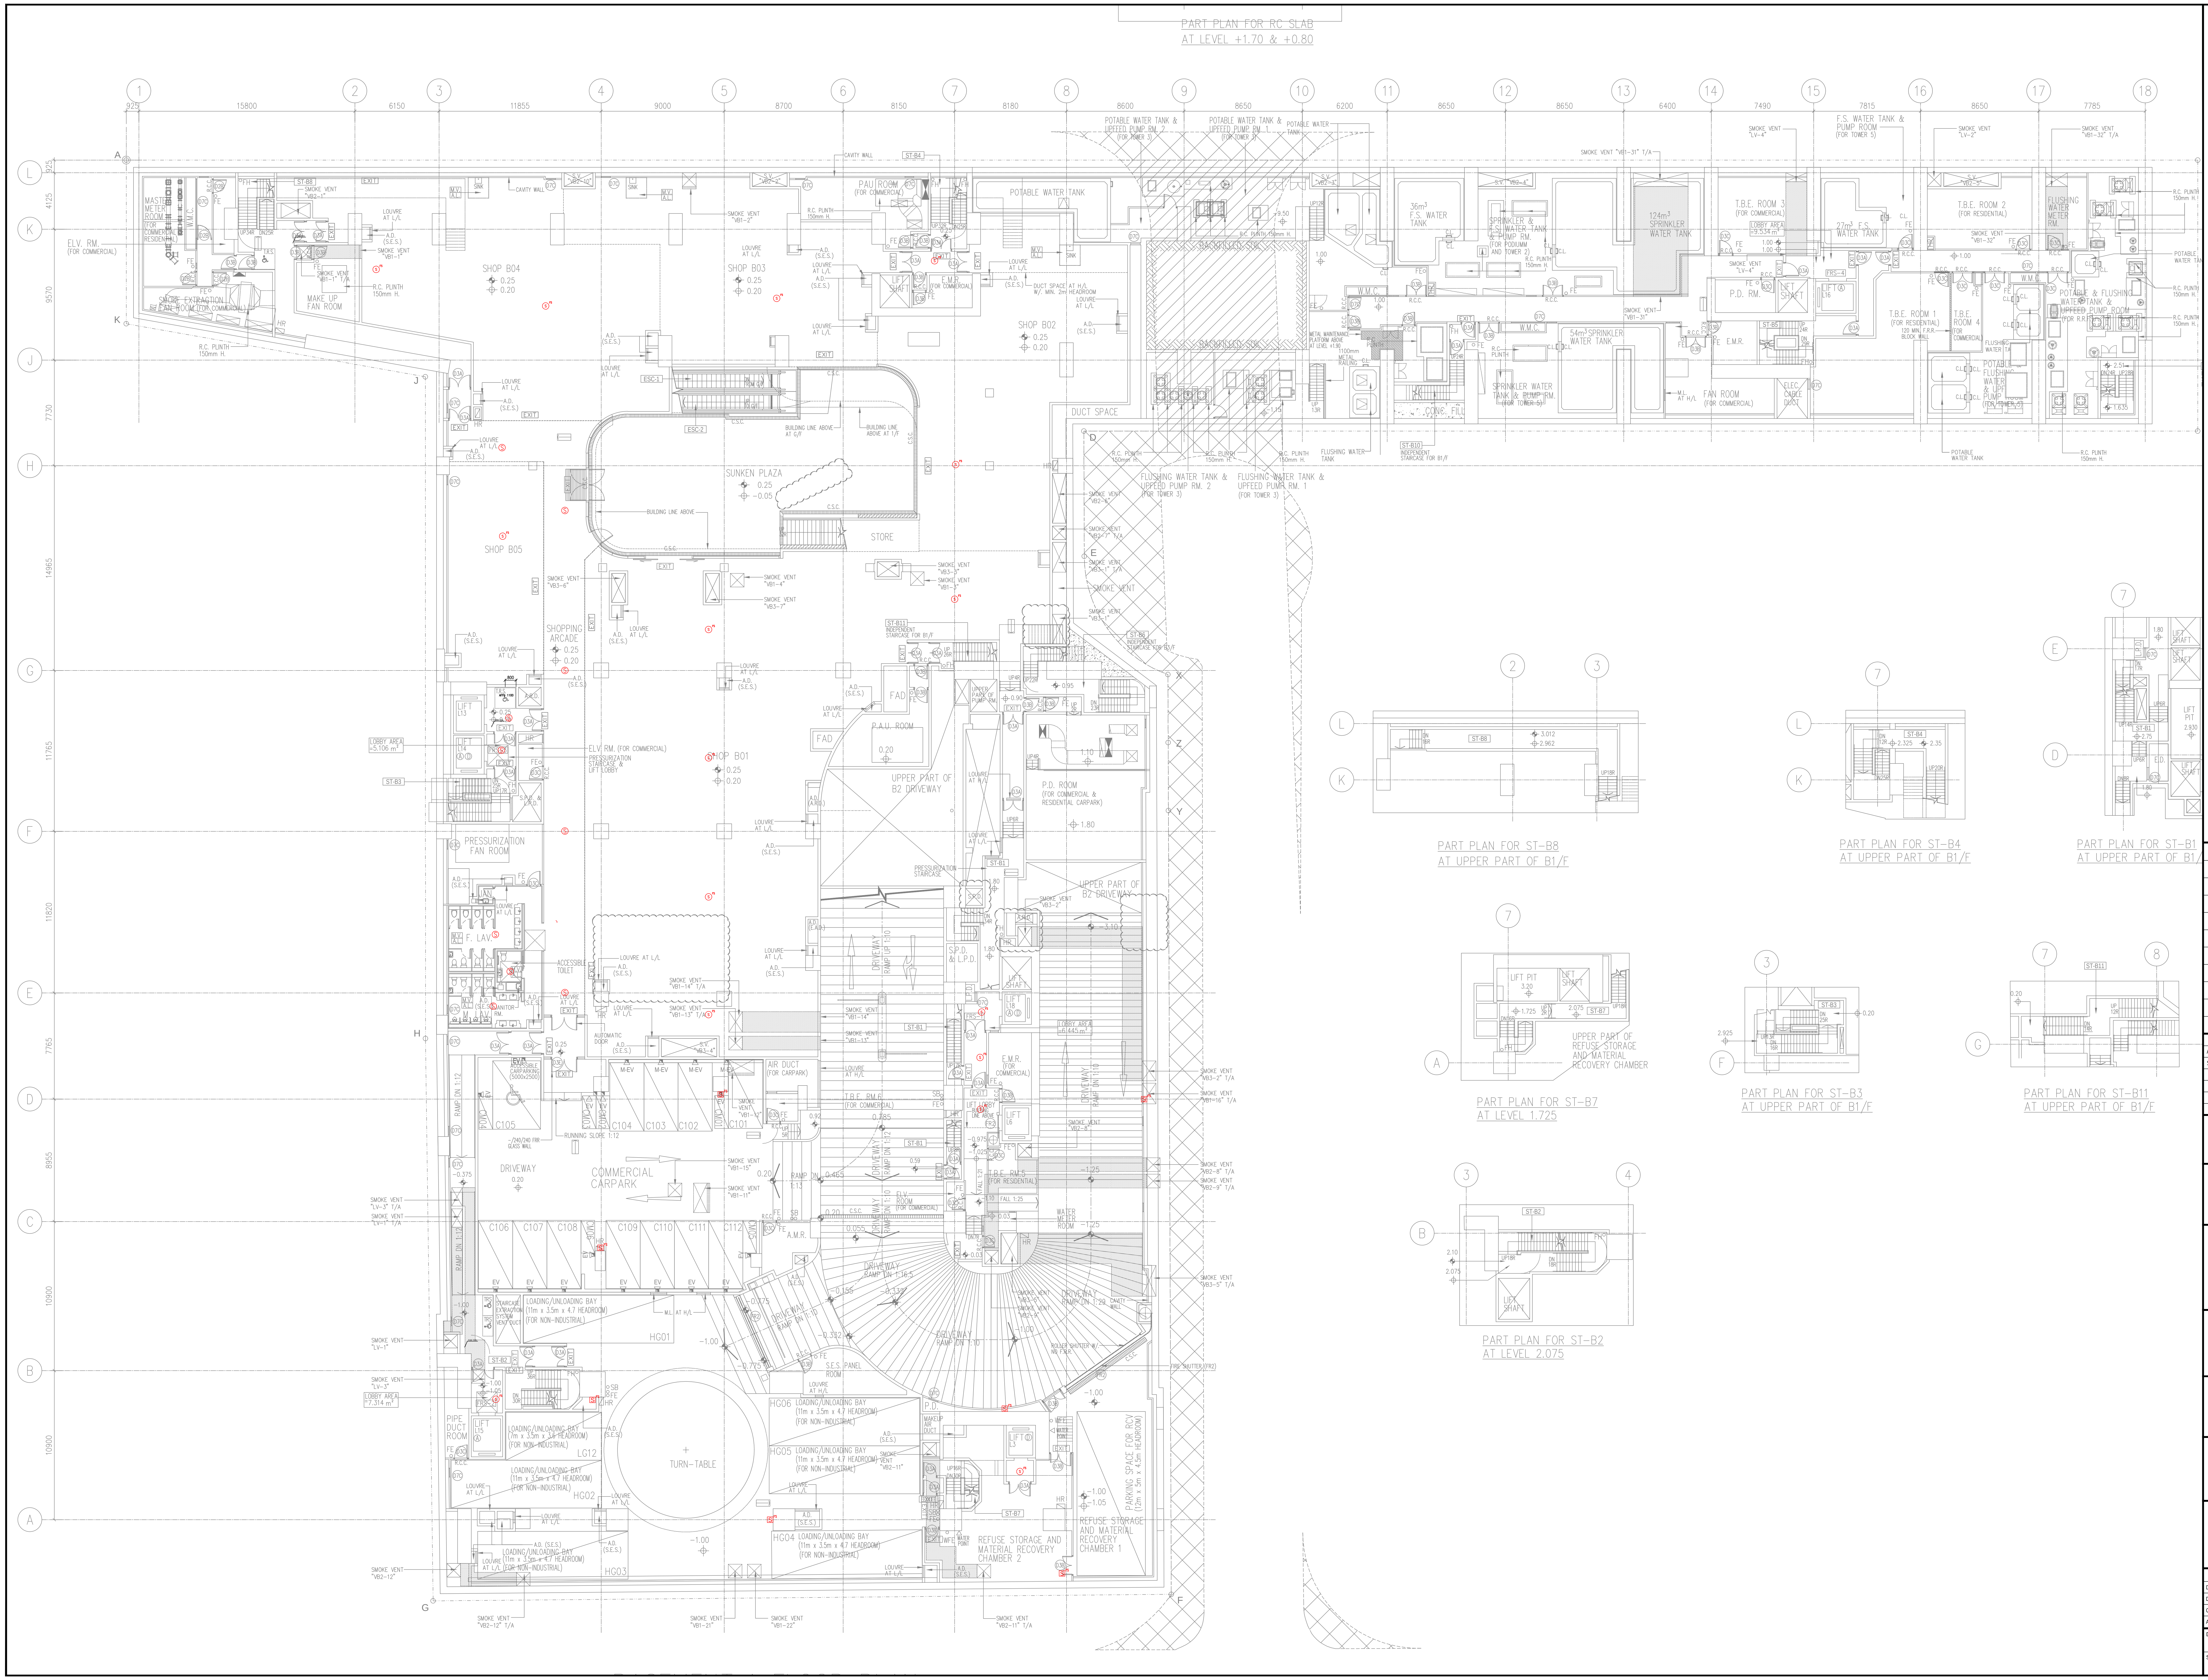
PART PLAN FOR RC SLAB AT LEVEL +1.70 & +0.80
1
2
3
4
5
6
7
8
9
10
11
12
13
14
15
16
17
18
L
K
J
H
G
F
E
D
C
B
A
ELV. RM. (FOR COMMERCIAL)
MAKE UP FAN ROOM
SHOP B04
SHOP B03
SHOP B02
PAU ROOM (FOR COMMERCIAL)
POTABLE WATER TANK
DUCT SPACE
SUNKEN PLAZA
STORE
SHOP B05
SHOPPING ARCADE
SHOP B01
ELV. RM. (FOR COMMERCIAL)
PRESSURIZATION FAN ROOM
P.A.U. ROOM
UPPER PART OF B2 DRIVEWAY
P.D. ROOM (FOR COMMERCIAL & RESIDENTIAL CARPARK)
UPPER PART OF B2 DRIVEWAY
COMMERCIAL CARPARK
DRIVEWAY
T.B.E. RM. (FOR COMMERCIAL)
T.B.E. RM. 5 (FOR RESIDENTIAL)
E.M.R. (FOR COMMERCIAL)
TURN-TABLE
REFUSE STORAGE AND MATERIAL RECOVERY CHAMBER 2
REFUSE STORAGE AND MATERIAL RECOVERY CHAMBER 1
36m³ F.S. WATER TANK
124m³ SPRINKLER WATER TANK
T.B.E. ROOM 3 (FOR COMMERCIAL)
T.B.E. ROOM 2 (FOR RESIDENTIAL)
T.B.E. ROOM 1 (FOR RESIDENTIAL)
54m³ SPRINKLER WATER TANK
SPRINKLER WATER TANK & PUMP RM.
FAN ROOM (FOR COMMERCIAL)
P.D. RM.
FLUSHING WATER TANK & UPFEED PUMP RM. 2
FLUSHING WATER TANK & UPFEED PUMP RM. 1
PART PLAN FOR ST-B8 AT UPPER PART OF B1/F
PART PLAN FOR ST-B4 AT UPPER PART OF B1/F
PART PLAN FOR ST-B1 AT UPPER PART OF B1/F
PART PLAN FOR ST-B7 AT LEVEL 1.725
PART PLAN FOR ST-B3 AT UPPER PART OF B1/F
PART PLAN FOR ST-B11 AT UPPER PART OF B1/F
PART PLAN FOR ST-B2 AT LEVEL 2.075

LEGEND:

S^FS (square)	WALL MOUNTED SPEAKER FOR FS
S^FS (circle)	CEILING MOUNT SPEAKER FOR FS
S (square)	WALL MOUNTED SPEAKER FOR FS & BGM
S (circle)	CEILING MOUNT SPEAKER FOR FS & BGM

REV.	DESCRIPTION	BY	DATE
0	1ST SUBMISSION	AC	10/2024

	DRAWING REFERENCE	REV.	DATE
ARCHITECTURAL	A/GBP/05 (11th AMENDMENT)		02/2026
STRUCTURAL			

CLIENT
NATION STAR DEVELOPMENT LIMITED

ARCHITECT
RONALD LU & PARTNERS
Ronald Lu & Partners (Hong Kong) Ltd.
呂元祥建築師事務所(香港)有限公司
33rd Floor, Wu Chung House,
213 Queen's Road East,
Wanchai, Hong Kong

CONSULTANT
wsp
7/F, One Kowloon
1 Wang Yuen Street
Kowloon Bay, Hong Kong

MAIN CONTRACTOR
中國海外房屋工程有限公司
CHINA OVERSEAS BUILDING CONSTRUCTION LIMITED

E & M CONTRACTOR
U-Tech Engineering Company Limited
Member of Towngas Group
6/F, 100 TO KWA WAN ROAD, KOWLOON, HONG KONG
TEL : (852) 2765 – 5666 ; FAX : (852) 2392 – 7422

PROJECT
PROPOSED DEVELOPMENT AT BAILEY STREET
& WING KWONG STREET, TO KWA WAN, KLN.
INLAND LOT NO. 11279
(URA PROJECT KC-009)

TITLE
ELV LAYOUT FOR BASEMENT 1
FLOOR PLAN

	NAME	INITIAL	DATE
DESIGNED BY	RONALD WONG		02/10/2024
DRAWN BY	AAREN CHU		02/10/2024
CHECKED BY	SAM KWOK		02/10/2024
APPROVED BY	WILSON YUEN		02/10/2024

DRAWING NO. D/EE/503
DATE 02/10/2024
REV. 0
STATUS
SCALE 1:150 @ A0
DO NOT SCALE THE DRAWING