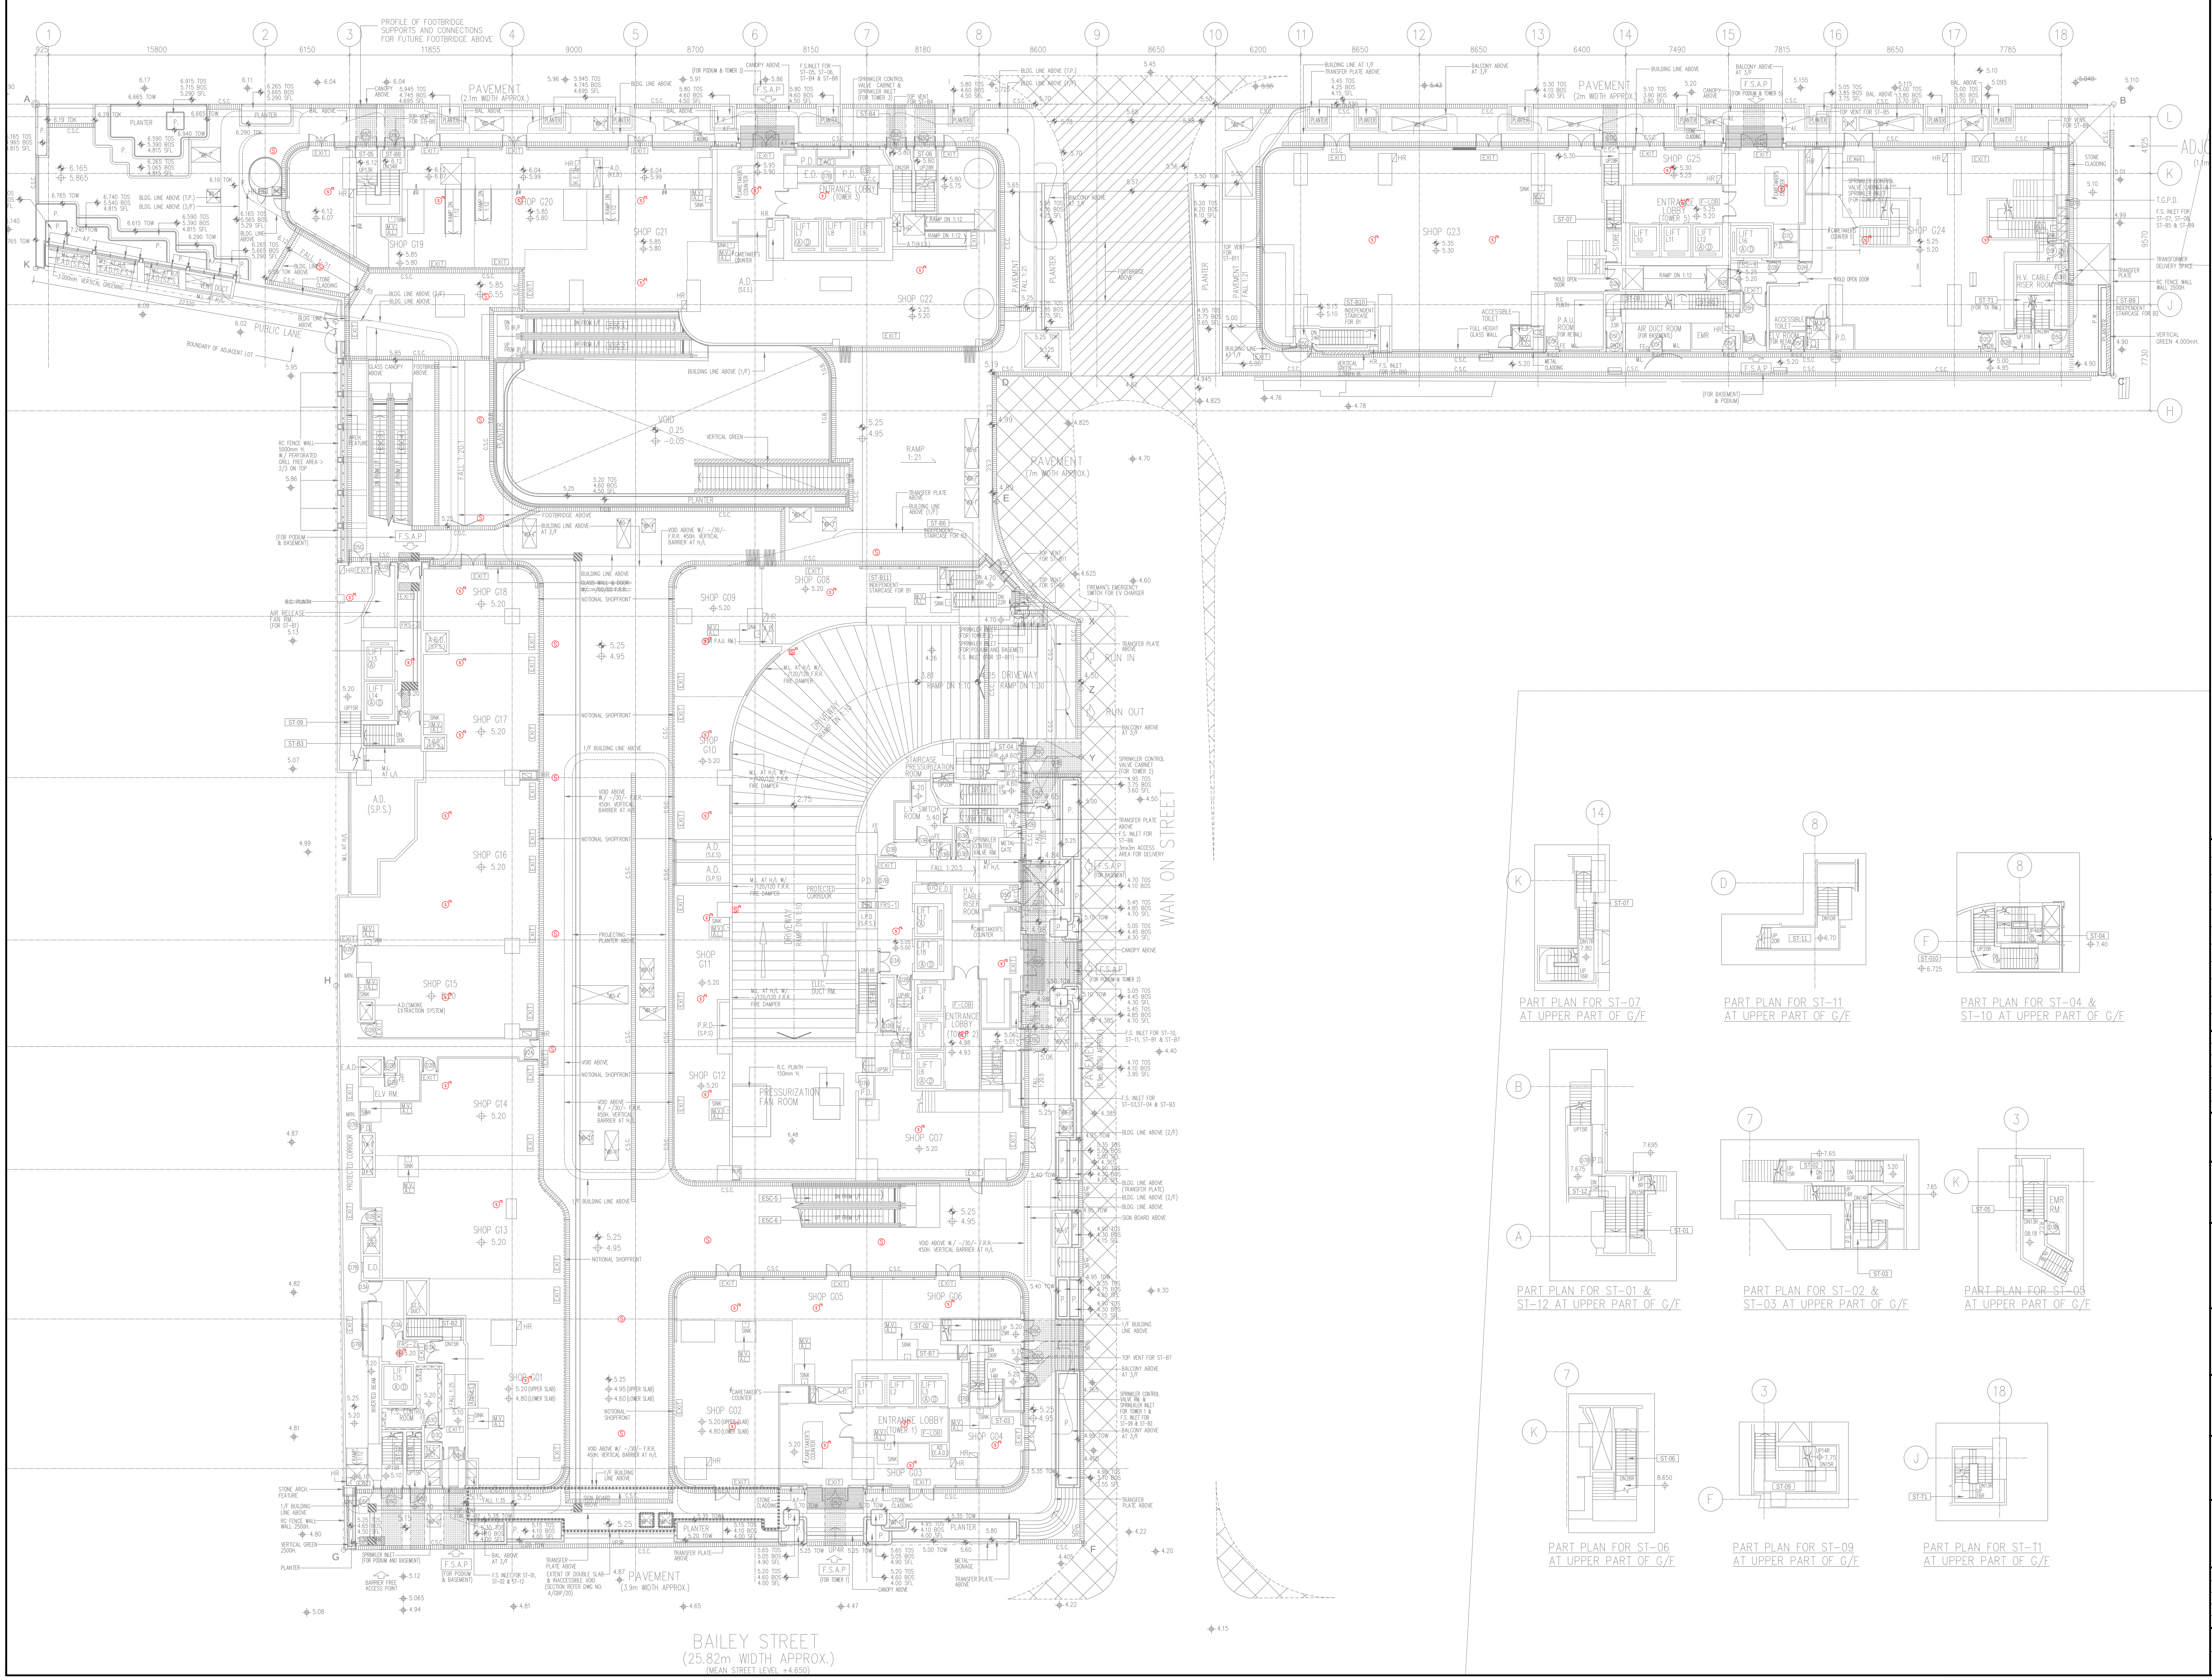

PART PLAN FOR ST-07 AT UPPER PART OF G/F

PART PLAN FOR ST-11 AT UPPER PART OF G/F

PART PLAN FOR ST-04 & ST-10 AT UPPER PART OF G/F

PART PLAN FOR ST-01 & ST-12 AT UPPER PART OF G/F

PART PLAN FOR ST-02 & ST-03 AT UPPER PART OF G/F

PART PLAN FOR ST-05 AT UPPER PART OF G/F

PART PLAN FOR ST-06 AT UPPER PART OF G/F

PART PLAN FOR ST-09 AT UPPER PART OF G/F

PART PLAN FOR ST-T1 AT UPPER PART OF G/F

LEGEND:

S^FS (square)	WALL MOUNTED SPEAKER FOR FS
S^FS (circle)	CEILING MOUNT SPEAKER FOR FS
S (square)	WALL MOUNTED SPEAKER FOR FS & BGM
S (circle)	CEILING MOUNT SPEAKER FOR FS & BGM

REV.	DESCRIPTION	BY	DATE
0	1ST SUBMISSION	AC	10/2024

	DRAWING REFERENCE	REV.	DATE
ARCHITECTURAL	A/GBP/6 (11th AMENDMENT)	D	02/2026
STRUCTURAL			

CLIENT

NATION STAR DEVELOPMENT LIMITED

ARCHITECT

RONALD LU & PARTNERS

Ronald Lu & Partners (Hong Kong) Ltd.
呂元祥建築師事務所(香港)有限公司
33rd Floor, Wu Chung House,
213 Queen's Road East,
Wanchai, Hong Kong

CONSULTANT

wsp

7/F, One Kowloon
1 Wang Yuen Street
Kowloon Bay, Hong Kong

MAIN CONTRACTOR

中國海外房屋工程有限公司
CHINA OVERSEAS BUILDING CONSTRUCTION LIMITED

E & M CONTRACTOR

U-Tech Engineering Company Limited
Member of Towngas Group
6/F, 100 TO KWA WAN ROAD, KOWLOON, HONG KONG
TEL : (852) 2765 – 5666 ; FAX : (852) 2392 – 7422

PROJECT
PROPOSED DEVELOPMENT AT BAILEY STREET
& WING KWONG STREET, TO KWA WAN, KLN.
INLAND LOT NO. 11279
(URA PROJECT KC-009)

TITLE

ELV LAYOUT FOR GROUND FLOOR PLAN

	NAME	INITIAL	DATE
DESIGNED BY	RONALD WONG		02/10/2024
DRAWN BY	AAREN CHU		02/10/2024
CHECKED BY	SAM KWOK		02/10/2024
APPROVED BY	WILSON YUEN		02/10/2024

DRAWING NO.	DATE	REV.
UT/KC009/EL/805	02/10/2024	0

STATUS	SCALE 1:150 @ A0
	DO NOT SCALE THE DRAWING