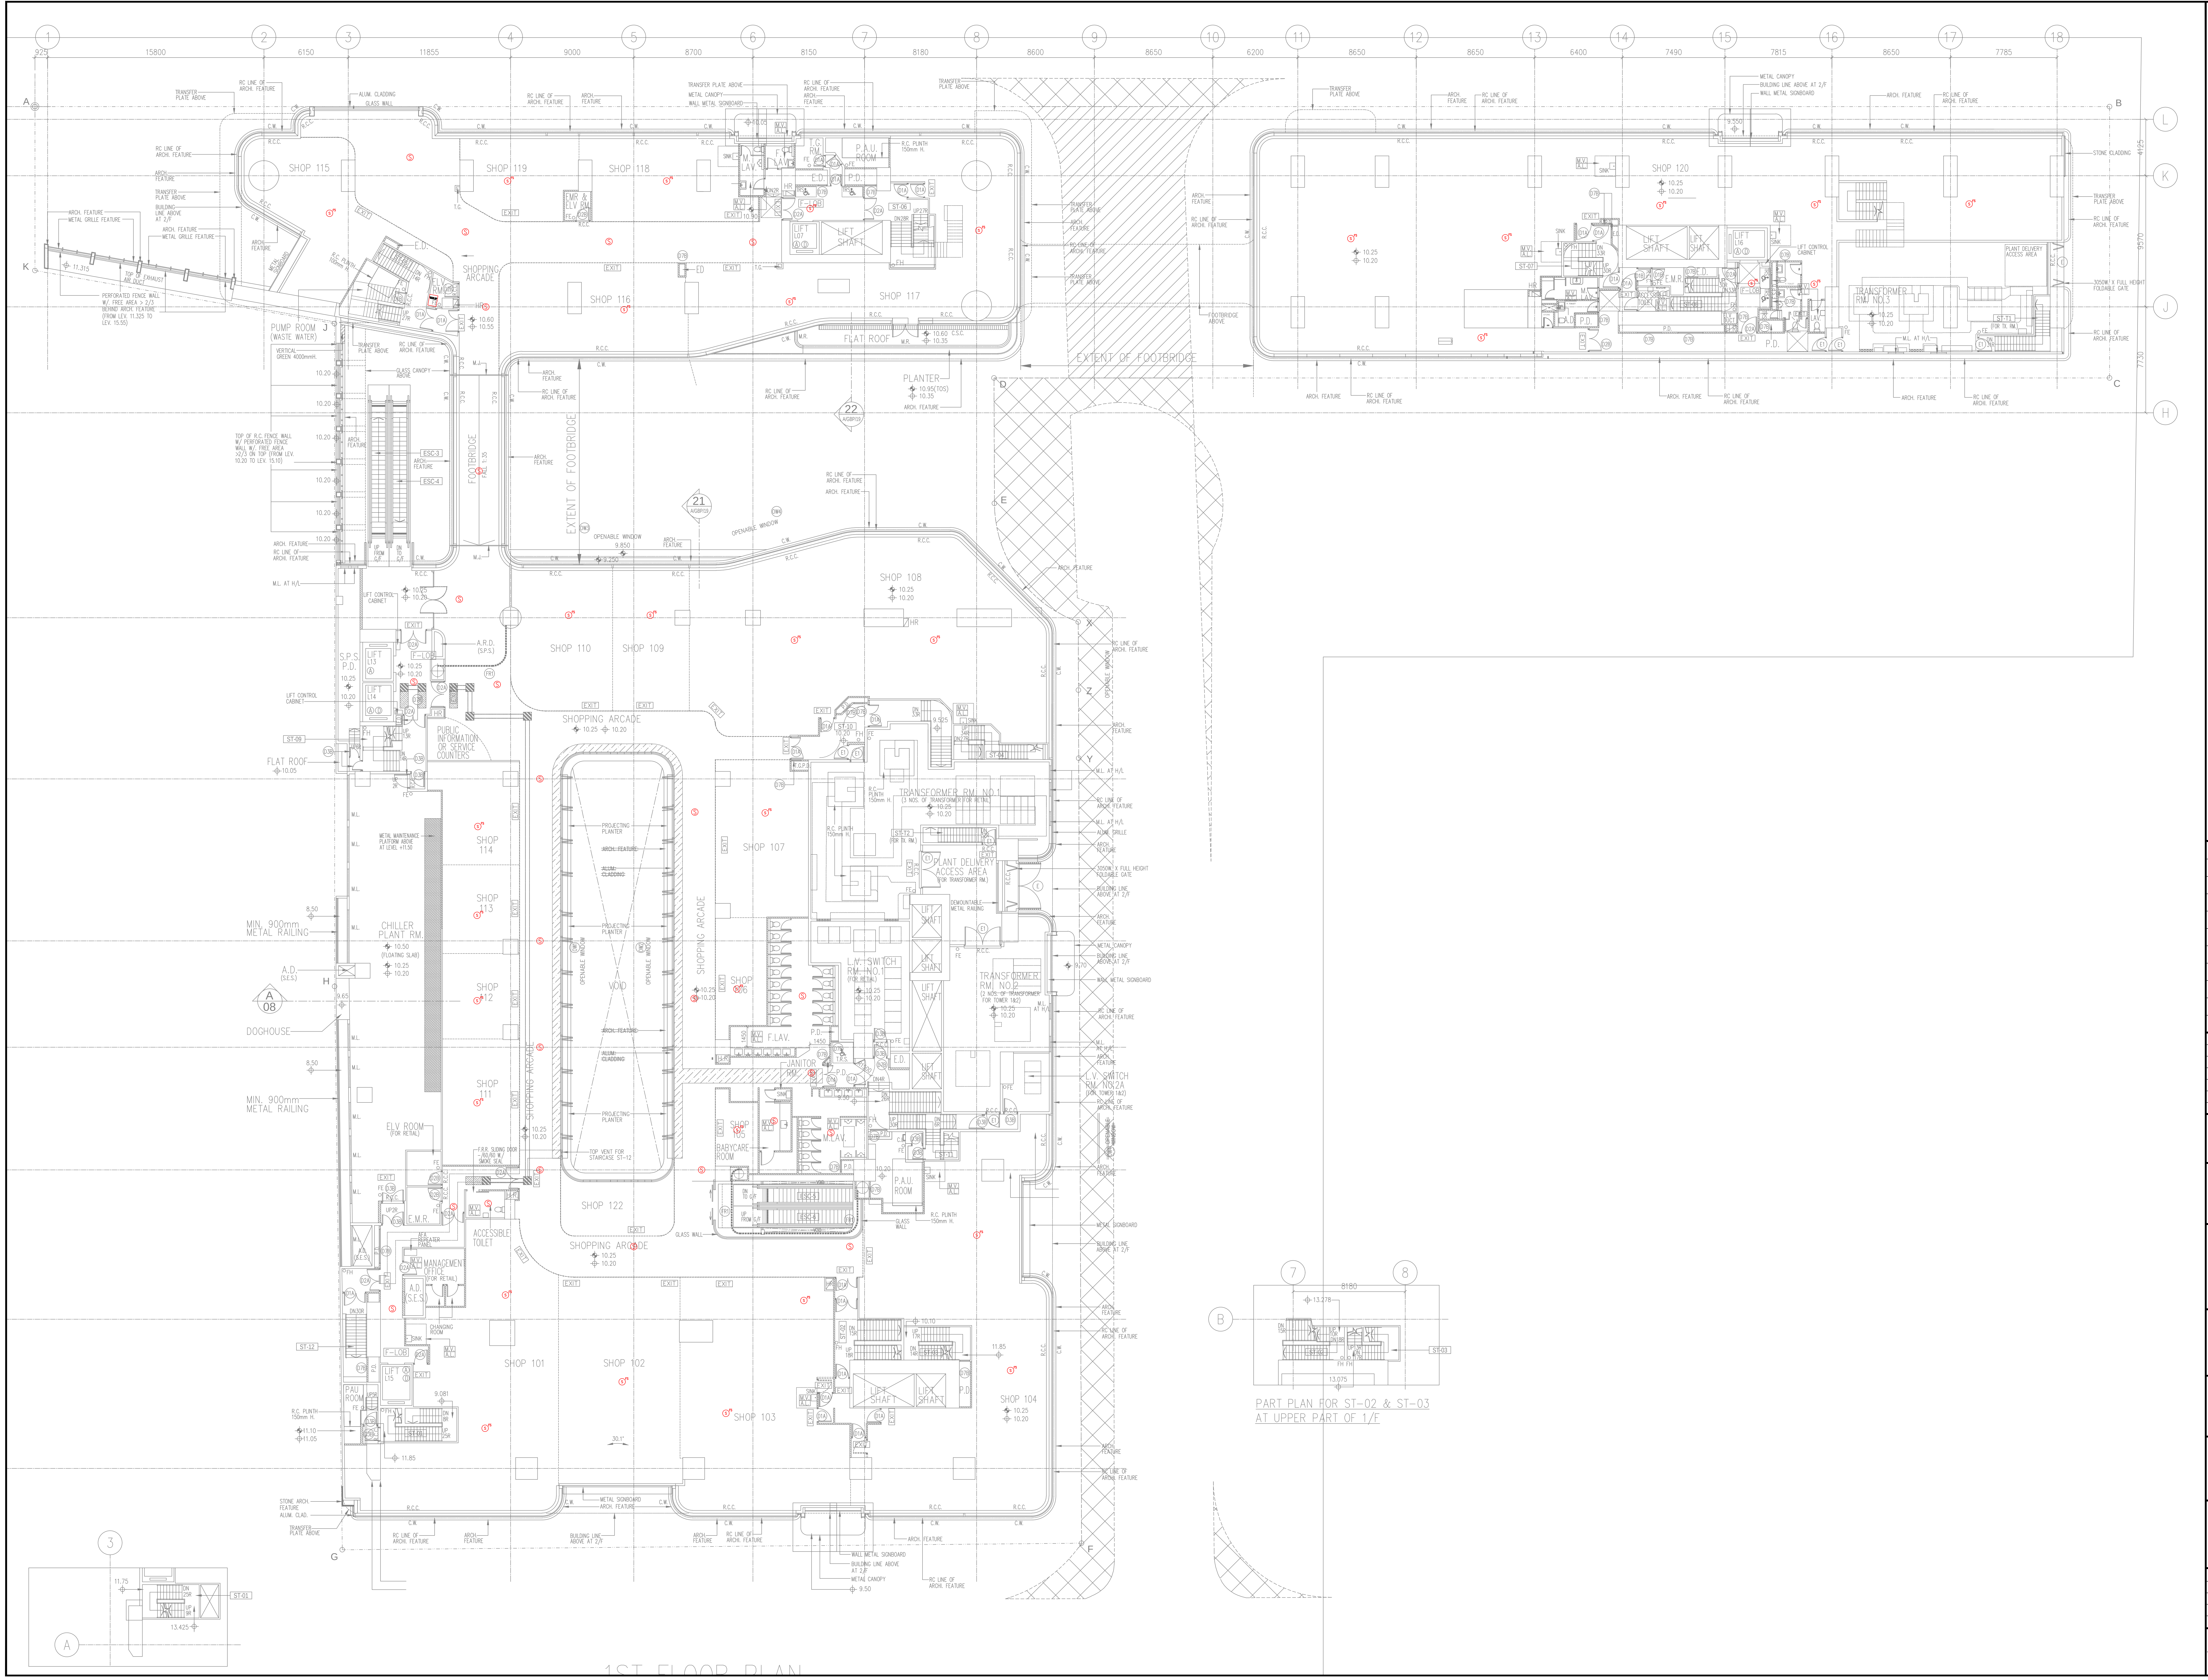

LEGEND:

S^FS (square)	WALL MOUNTED SPEAKER FOR FS
S^FS (circle)	CEILING MOUNT SPEAKER FOR FS
S (square)	WALL MOUNTED SPEAKER FOR FS & BGM
S (circle)	CEILING MOUNT SPEAKER FOR FS & BGM

REV.	DESCRIPTION	BY	DATE
0	1ST SUBMISSION	AC	10/2024

	DRAWING REFERENCE	REV.	DATE
ARCHITECTURAL	A/GBP/7 (11th AMENDMENT)		02/2026
STRUCTURAL			

CLIENT

NATION STAR DEVELOPMENT LIMITED

ARCHITECT

RONALD LU & PARTNERS

Ronald Lu & Partners (Hong Kong) Ltd.
呂元祥建築師事務所(香港)有限公司
33rd Floor, Wu Chung House,
213 Queen's Road East,
Wanchai, Hong Kong

CONSULTANT

wsp

7/F, One Kowloon
1 Wang Yuen Street
Kowloon Bay, Hong Kong

MAIN CONTRACTOR

中國海外房屋工程有限公司
CHINA OVERSEAS BUILDING CONSTRUCTION LIMITED

E & M CONTRACTOR

U-Tech Engineering Company Limited
Member of Towngas Group
6/F, 100 TO KWA WAN ROAD, KOWLOON, HONG KONG
TEL : (852) 2765 – 5666 ; FAX : (852) 2392 – 7422

PROJECT
PROPOSED DEVELOPMENT AT BAILEY STREET
& WING KWONG STREET, TO KWA WAN, KLN.
INLAND LOT NO. 11279
(URA PROJECT KC-009)

TITLE

ELV LAYOUT FOR FIRST FLOOR PLAN

	NAME	INITIAL	DATE
DESIGNED BY	RONALD WONG		02/10/2024
DRAWN BY	AAREN CHU		02/10/2024
CHECKED BY	SAM KWOK		02/10/2024
APPROVED BY	WILSON YUEN		02/10/2024

DRAWING NO. UT/KC009/EL/805
DATE 02/10/2024
REV. 0
STATUS
SCALE 1:150 @ A0
DO NOT SCALE THE DRAWING