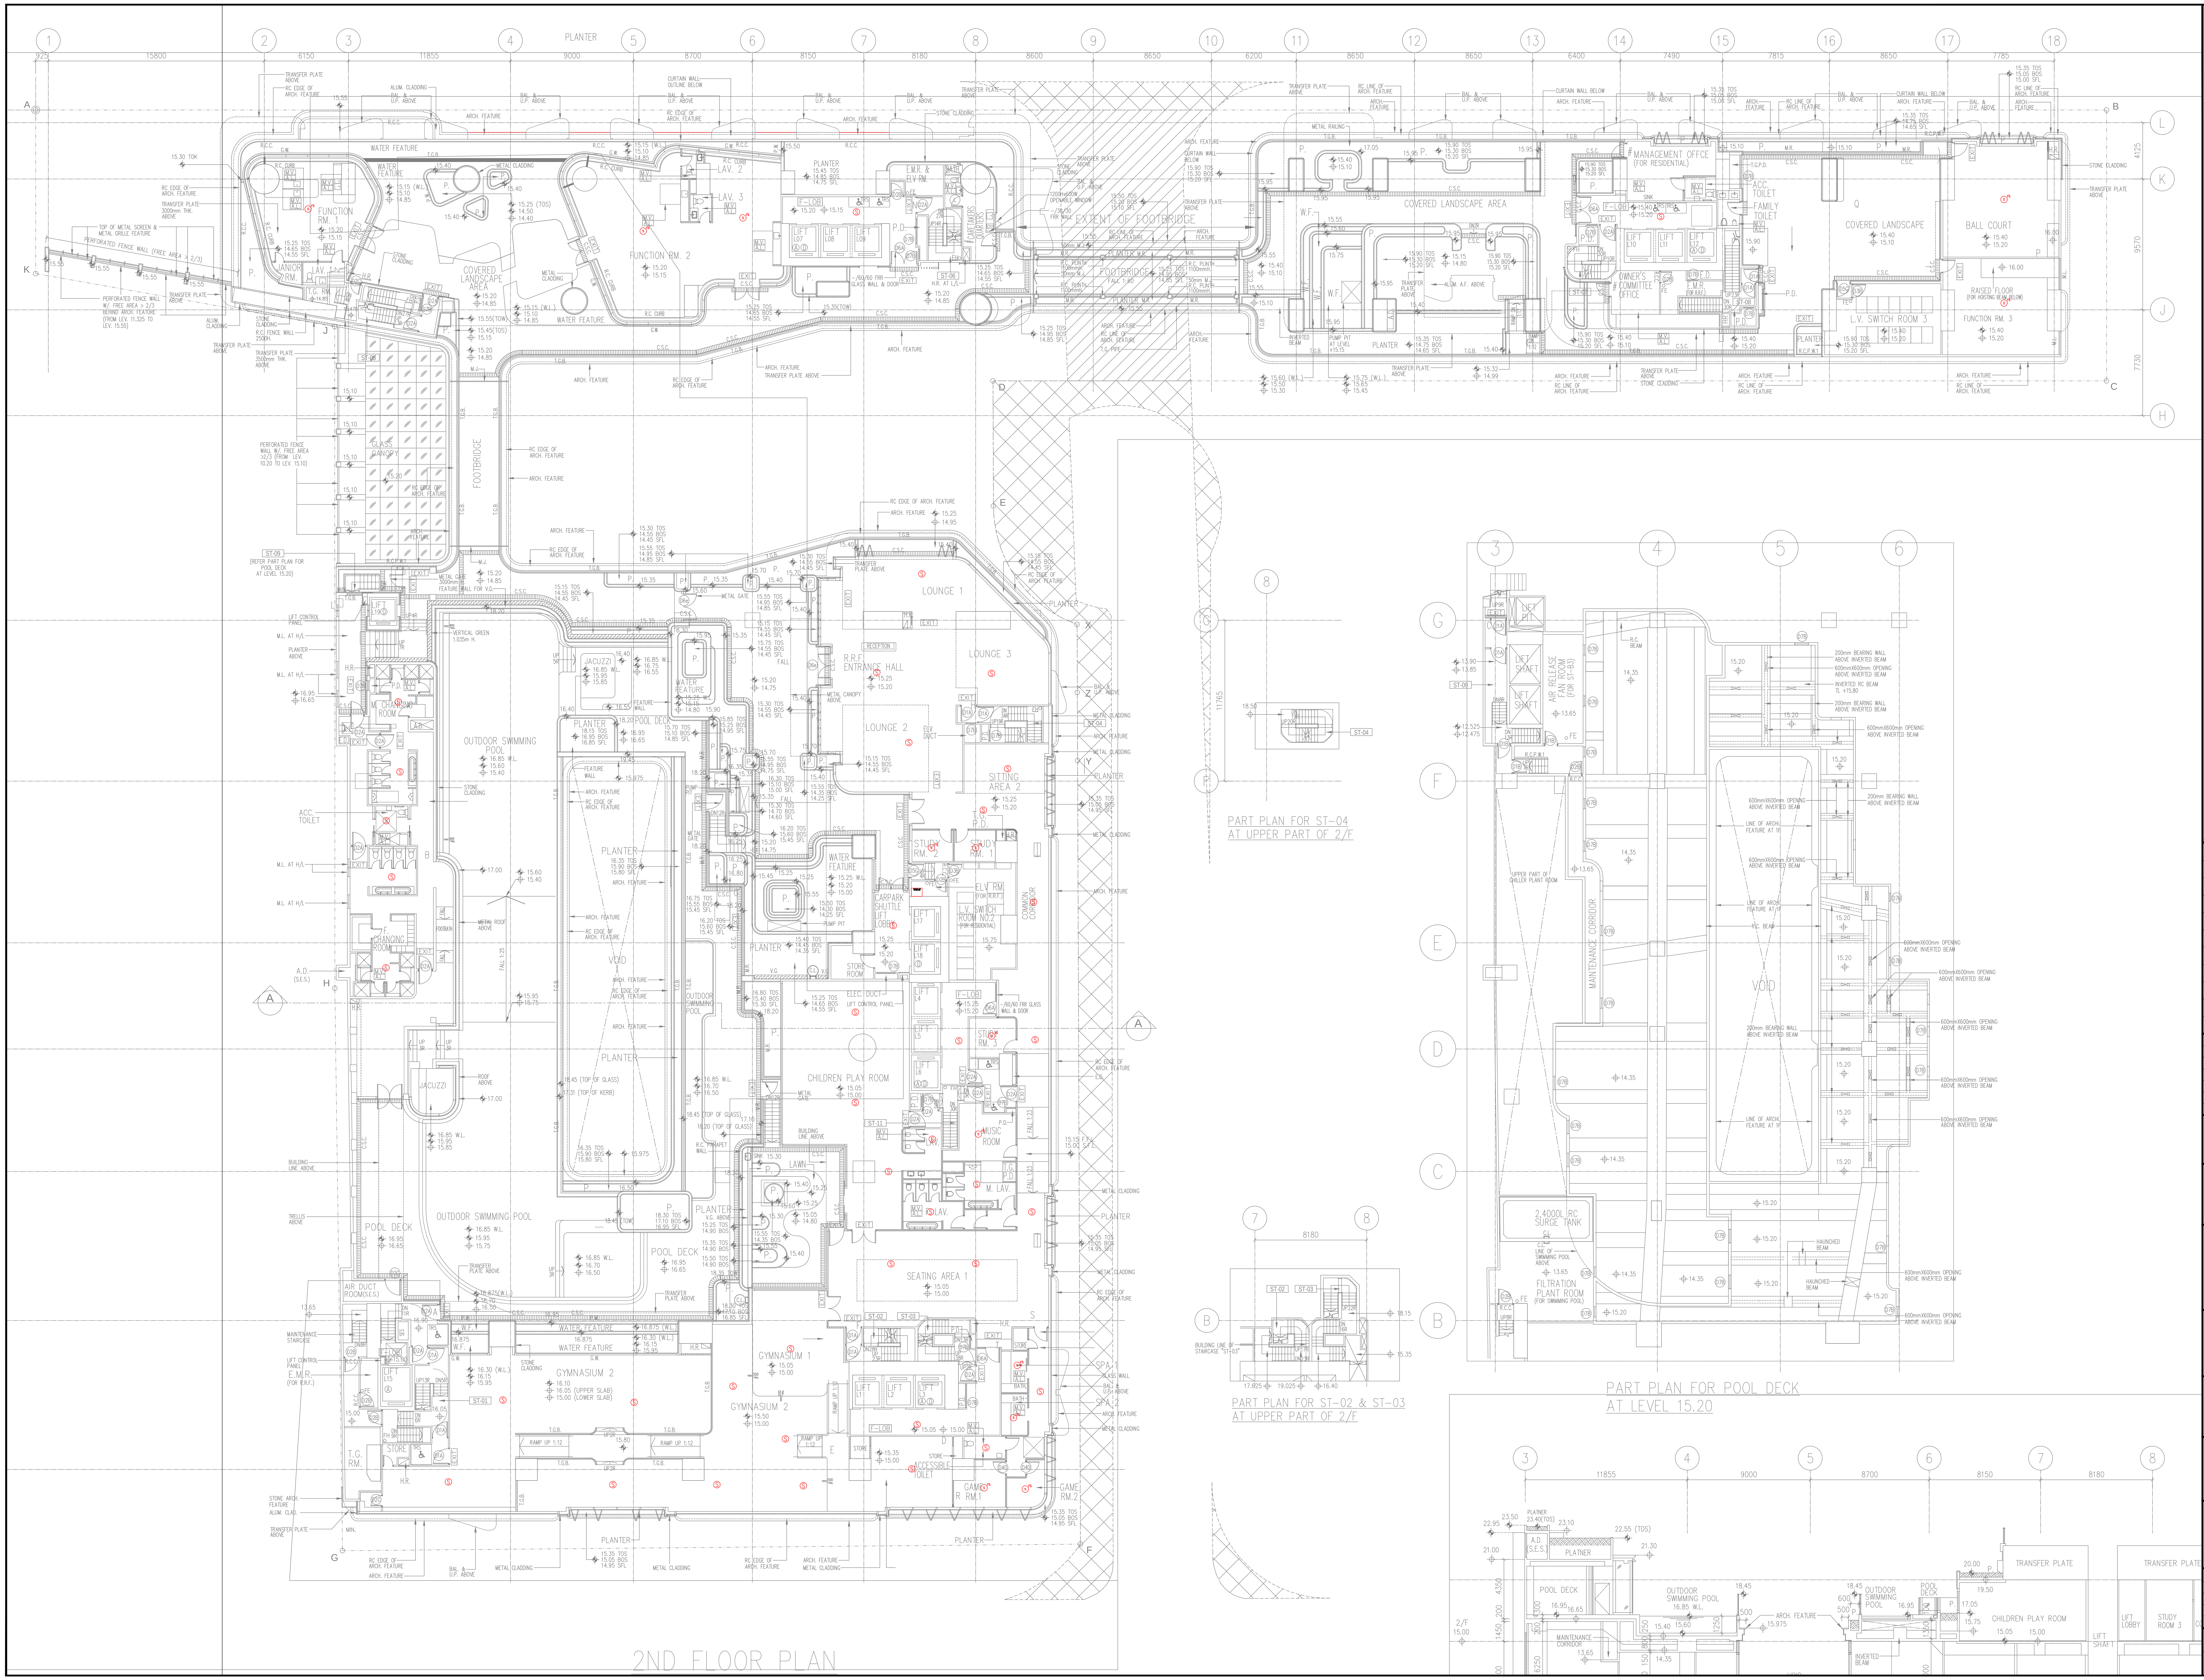
PLANTER
WATER FEATURE
FUNCTION RM.
FUNCTION RM. 2
FUNCTION RM. 3
COVERED LANDSCAPE AREA
COVERED LANDSCAPE
LAV. 2
LAV. 3
EXTENT OF FOOTBRIDGE
FOOTBRIDGE
MANAGEMENT OFFICE (FOR RESIDENTIAL)
ACC. TOILET
FAMILY TOILET
OWNER'S COMMITTEE OFFICE
BALL COURT
L.V. SWITCH ROOM 3
LOUNGE 1
LOUNGE 2
LOUNGE 3
R.R.F. ENTRANCE HALL
SITTING AREA 2
OUTDOOR SWIMMING POOL
JACUZZI
POOL DECK
VOID
CHILDREN PLAY ROOM
MUSIC ROOM
SEATING AREA 1
GYMNASIUM 1
GYMNASIUM 2
ACCESSIBLE TOILET
GAME RM. 1
GAME RM. 2
CHANGING ROOM
AIR DUCT ROOM (S.E.)
T.G. RM.
LAWN
CARPARK SHUTTLE LIFT LOBBY
L.V. SWITCH ROOM NO.2
COMMON CORRIDOR
ELV RM.
STORE ROOM
2ND FLOOR PLAN
PART PLAN FOR ST-04 AT UPPER PART OF 2/F
PART PLAN FOR ST-02 & ST-03 AT UPPER PART OF 2/F
PART PLAN FOR POOL DECK AT LEVEL 15.20
2,400L(R.C) SURGE TANK
FILTRATION PLANT ROOM (FOR SWIMMING POOL)
MAINTENANCE CORRIDOR
AIR RELEASE FAN ROOM (FOR ST-03)
OUTDOOR SWIMMING POOL
CHILDREN PLAY ROOM
TRANSFER PLATE
STUDY ROOM 3
LIFT LOBBY
LIFT SHAFT

LEGEND:

$\boxed{S}^{FS}$	WALL MOUNTED SPEAKER FOR FS
Ⓢ FS	CEILING MOUNT SPEAKER FOR FS
$\boxed{S}$	WALL MOUNTED SPEAKER FOR FS & BGM
Ⓢ	CEILING MOUNT SPEAKER FOR FS & BGM

REV.	DESCRIPTION	BY	DATE
0	1ST SUBMISSION	AC	10/2024

	DRAWING REFERENCE	REV.	DATE
ARCHITECTURAL	A/GBP/8 (11th AMENDMENT)		02/2026
STRUCTURAL			

CLIENT

NATION STAR DEVELOPMENT LIMITED

ARCHITECT

RONALD LU & PARTNERS

Ronald Lu & Partners (Hong Kong) Ltd.
呂元祥建築師事務所(香港)有限公司
33rd Floor, Wu Chung House,
213 Queen's Road East,
Wanchai, Hong Kong

CONSULTANT

wsp

7/F, One Kowloon
1 Wang Yuen Street
Kowloon Bay, Hong Kong

MAIN CONTRACTOR

中國海外房屋工程有限公司
CHINA OVERSEAS BUILDING CONSTRUCTION LIMITED

E & M CONTRACTOR

U-Tech Engineering Company Limited
Member of Towngas Group
6/F, 100 TO KWA WAN ROAD, KOWLOON, HONG KONG
TEL : (852) 2765 – 5666 ; FAX : (852) 2392 – 7422

PROJECT
PROPOSED DEVELOPMENT AT BAILEY STREET
& WING KWONG STREET, TO KWA WAN, KLN.
INLAND LOT NO. 11279
(URA PROJECT KC-009)

TITLE

ELV LAYOUT FOR SECOND FLOOR PLAN

	NAME	INITIAL	DATE
DESIGNED BY	RONALD WONG		02/10/2024
DRAWN BY	AAREN CHU		02/10/2024
CHECKED BY	SAM KWOK		02/10/2024
APPROVED BY	WILSON YUEN		02/10/2024

DRAWING NO. UT/KC009/EL/805
DATE 02/10/2024
REV. 0
STATUS
SCALE 1:150 @ A0
DO NOT SCALE THE DRAWING