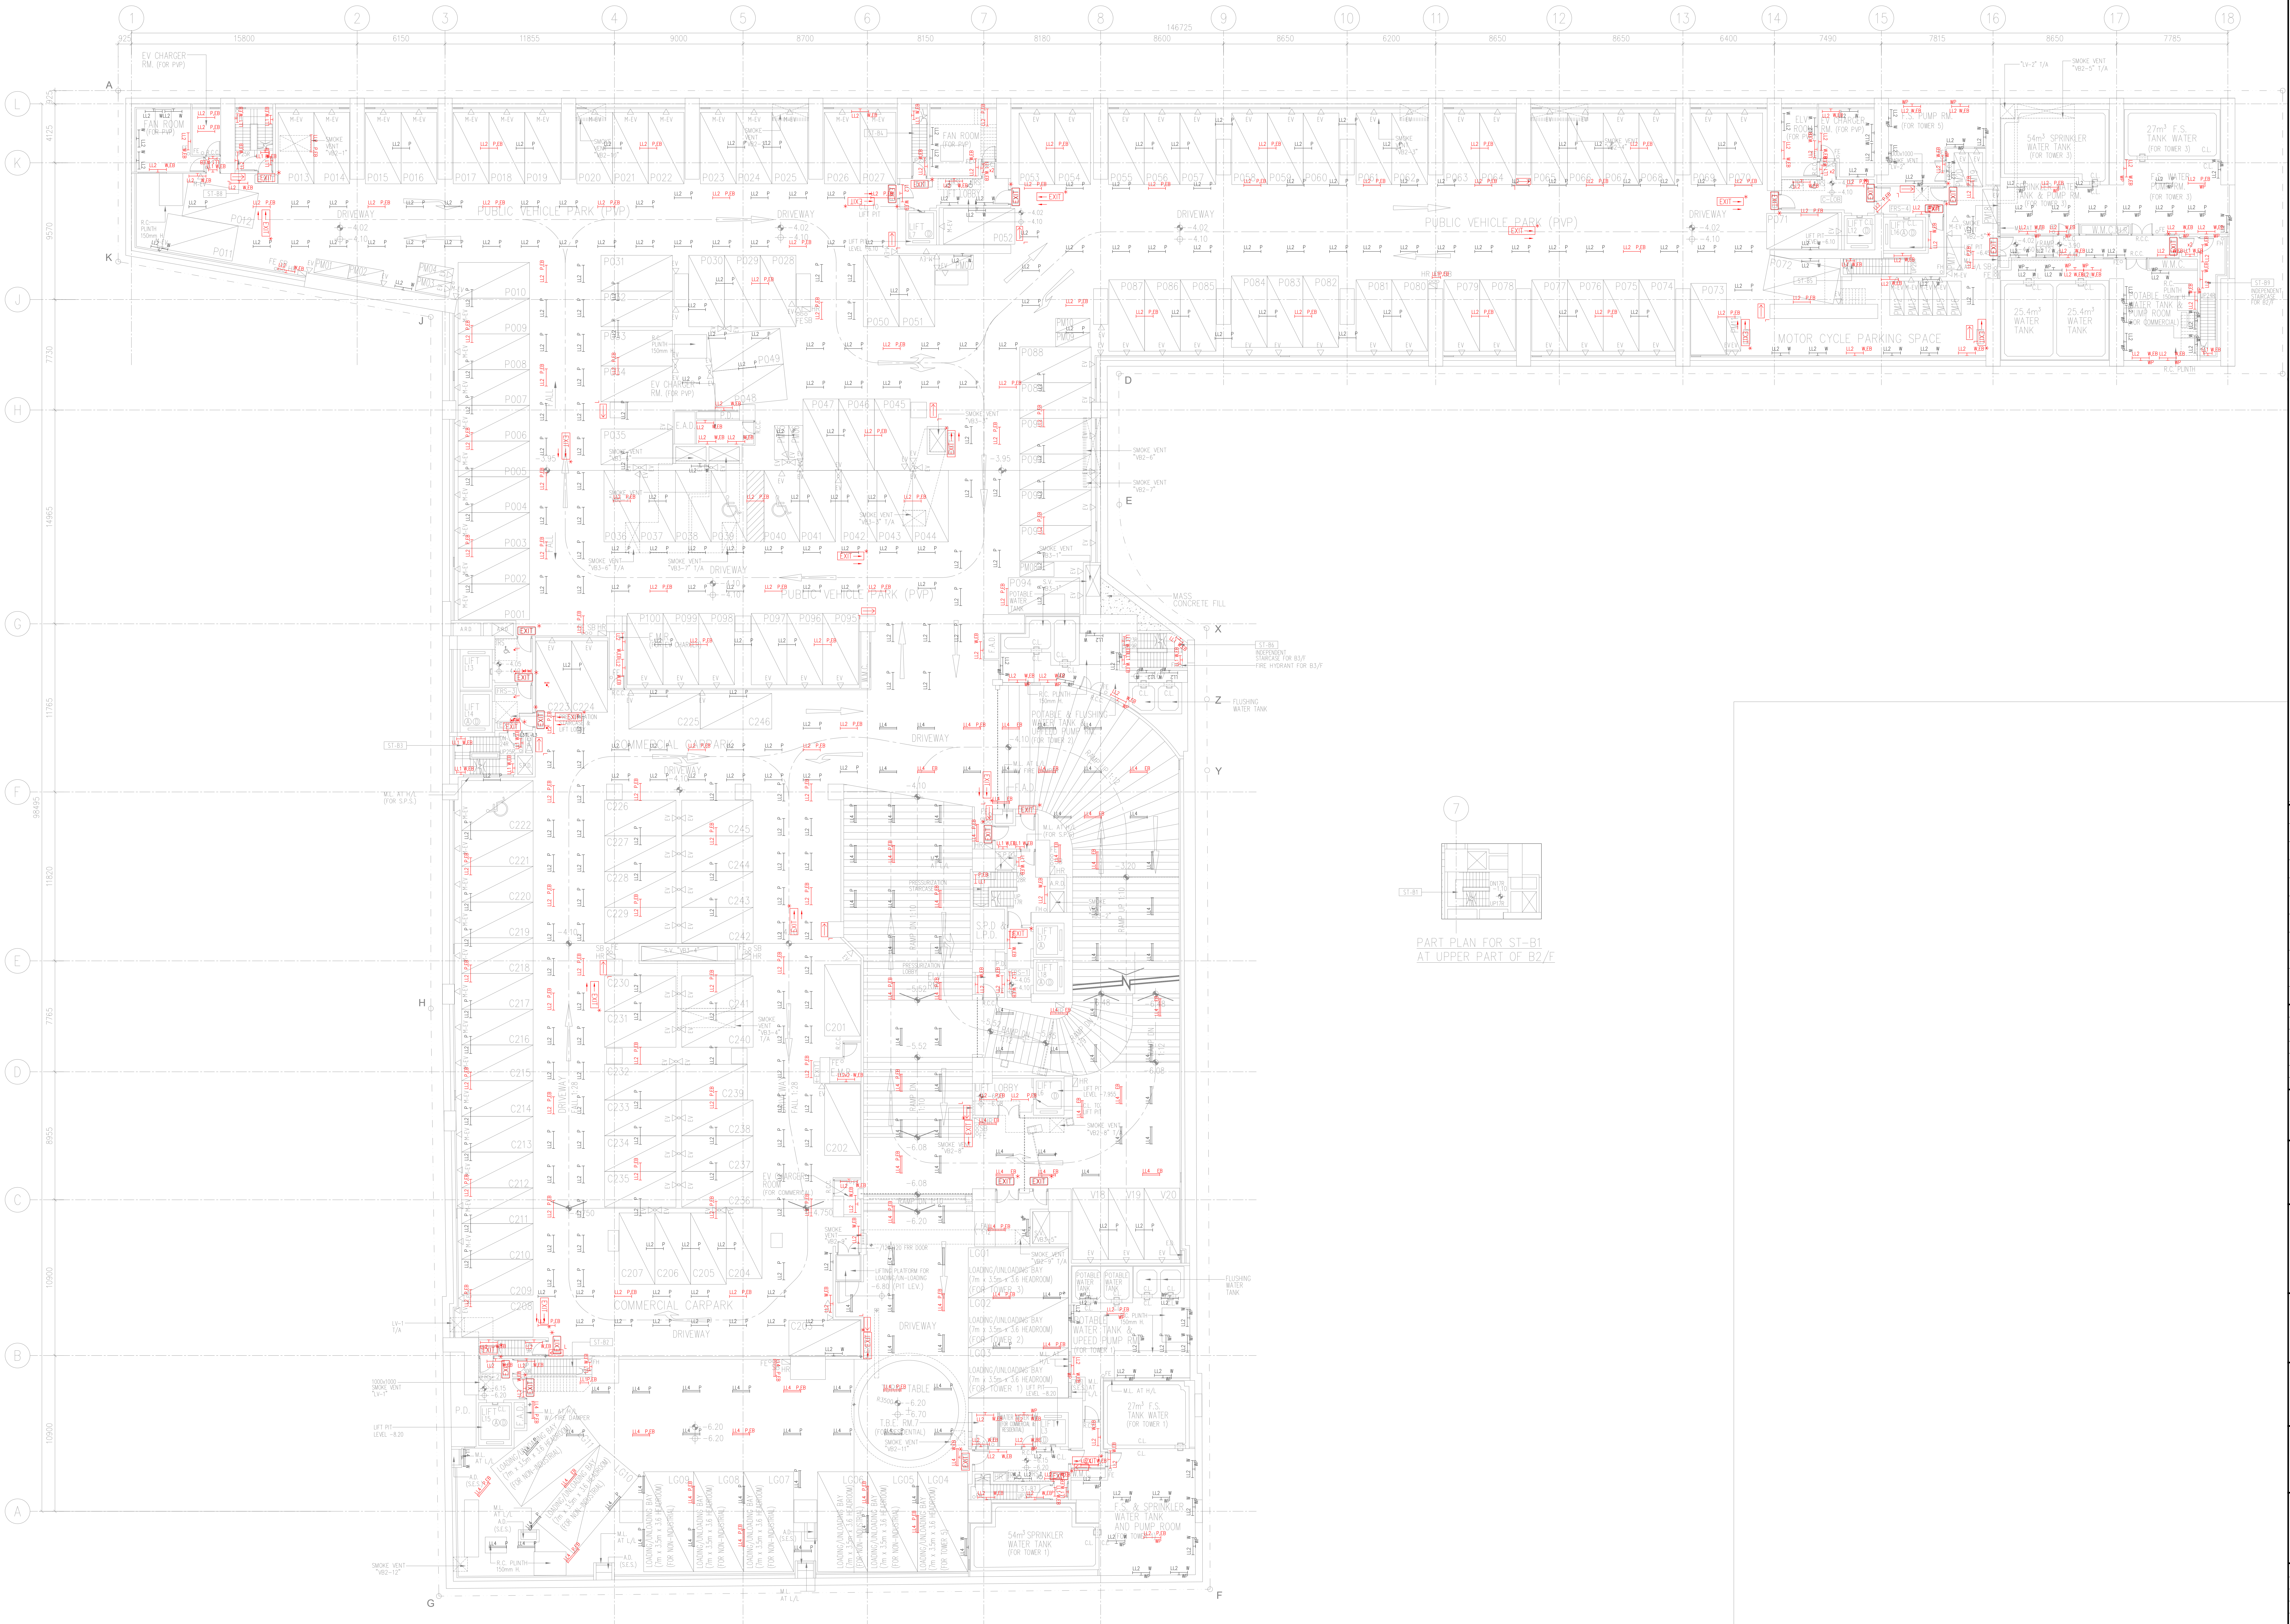
PUBLIC VEHICLE PARK (PVP)
DRIVEWAY
COMMERCIAL CARPARK
MOTOR CYCLE PARKING SPACE
EV CHARGER RM. (FOR PVP)
FAN ROOM
54m³ SPRINKLER WATER TANK (FOR TOWER 3)
27m³ F.S. TANK WATER (FOR TOWER 3)
25.4m³ WATER TANK
POTABLE WATER TANK
LOADING/UNLOADING BAY
TURNTABLE
54m³ SPRINKLER WATER TANK (FOR TOWER 1)
27m³ F.S. TANK WATER (FOR TOWER 1)
F.S. & SPRINKLER WATER TANK AND PUMP ROOM
MASS CONCRETE FILL
FLUSHING WATER TANK
ST-B9 INDEPENDENT STAIRCASE FOR B2/F
ST-B1

PART PLAN FOR ST-B1
AT UPPER PART OF B2/F

LEGEND :

LL1 P	600mm SINGLE BATTEN T5 LED FITTING, BUILT-IN LED DRIVER, PENDANT TYPE
LL1P,EB LL1 W,EB	600mm SINGLE BATTEN T5 LED FITTING, BUILT-IN LED DRIVER, PENDANT / WALL MOUNTED TYPE WITH ESSENTIAL POWER
LL2 P LL2 W	1200mm SINGLE BATTEN T5 LED FITTING, BUILT-IN LED DRIVER, PENDANT / WALL MOUNTED TYPE
LL2 P,EB LL2 W,EB	1200mm SINGLE BATTEN T5 LED FITTING, BUILT-IN LED DRIVER, PENDANT / WALL MOUNTED TYPE WITH ESSENTIAL POWER
LL4 P LL4 W	1200mm TWIN BATTEN T5 LED FITTING, BUILT-IN LED DRIVER, PENDANT TYPE
LL4 P,EB LL4 W,EB	1200mm TWIN BATTEN T5 LED FITTING, BUILT-IN LED DRIVER, PENDANT TYPE WITH ESSENTIAL POWER
⇦ L / ⇨ L	LOW LEVEL PHOTOLUMINESCENT DIRECTIONAL PLATE
EXIT *	HIGH LEVEL EXIT SIGN (FOR AUDIO/VISUAL ADVISORY SYSTEM)
EXIT→ * / ←EXIT * / ↑EXIT *	HIGH LEVEL DIRECTIONAL SIGN (FOR AUDIO/VISUAL ADVISORY SYSTEM)
EXIT→ * / ←EXIT *	HIGH LEVEL DIRECTIONAL SIGN, DOUBLE FACED TYPE (FOR AUDIO/VISUAL ADVISORY SYSTEM)
●	10A 1-WAY SINGLE POLE LIGHTING SWITCH AT 1350mm A.F.F.L. UNLESS OTHERWISE SPECIFIED
◉	10A 1-WAY SINGLE POLE WEATHERPROOF LIGHTING SWITCH AT 1350mm A.F.F.L. UNLESS OTHERWISE SPECIFIED
	MOTION SENSOR

ABBREVIATIONS :

E	ESSENTIAL POWER FROM EMERGENCY GENERATOR TO BE PROVIDED
B	BATTERY KIT FOR 2-HOURS
WP	WATERPROOF TYPE, IP65 UNLESS OTHERWISE SPECIFY
P	PENDANT TYPE, 2600 AFFL OR COORDINATION ON SITE
W	WALL MOUNTED TYPE, 2350 AFFL OR COORDINATION ON SITE

REV.	DESCRIPTION	BY	DATE
0	1ST SUBMISSION	AC	10/2024

	DRAWING REFERENCE	REV.	DATE
ARCHITECTURAL	A/GBP/10 (3nd AMENDMENT)	D	05/2024
STRUCTURAL			

CLIENT
NATION STAR DEVELOPMENT LIMITED

ARCHITECT
RONALD LU & PARTNERS
Ronald Lu & Partners (Hong Kong) Ltd.
呂元祥建築師事務所(香港)有限公司
33rd Floor, Wu Chung House,
213 Queen's Road East,
Wanchai, Hong Kong

CONSULTANT
wsp
7/F, One Kowloon
1 Wang Yuen Street
Kowloon Bay, Hong Kong

MAIN CONTRACTOR
中國海外房屋工程有限公司
CHINA OVERSEAS BUILDING CONSTRUCTION LIMITED

E & M CONTRACTOR
卓裕工程有限公司
U-Tech Engineering Company Limited
Member of Towngas Group
6/F, 100 TO KWA WAN ROAD, KOWLOON, HONG KONG
TEL : (852) 2765 – 5666 ; FAX : (852) 2392 – 7422

PROJECT
PROPOSED DEVELOPMENT AT BAILEY STREET
& WING KWONG STREET, TO KWA WAN, KLN.
INLAND LOT NO. 11279
(URA PROJECT KC-009)

TITLE
LIGHTING LAYOUT FOR BASEMENT 2 FLOOR PLAN

	NAME	INITIAL	DATE
DESIGNED BY	RONALD WONG		02/10/2024
DRAWN BY	AAREN CHU		02/10/2024
CHECKED BY	SAM KWOK		02/10/2024
APPROVED BY	WILSON YUEN		02/10/2024

DRAWING NO. D/EE/202	**DATE** 31/10/2026	REV. 0
STATUS	SCALE 1:100 @ A0	
	DO NOT SCALE THE DRAWING	