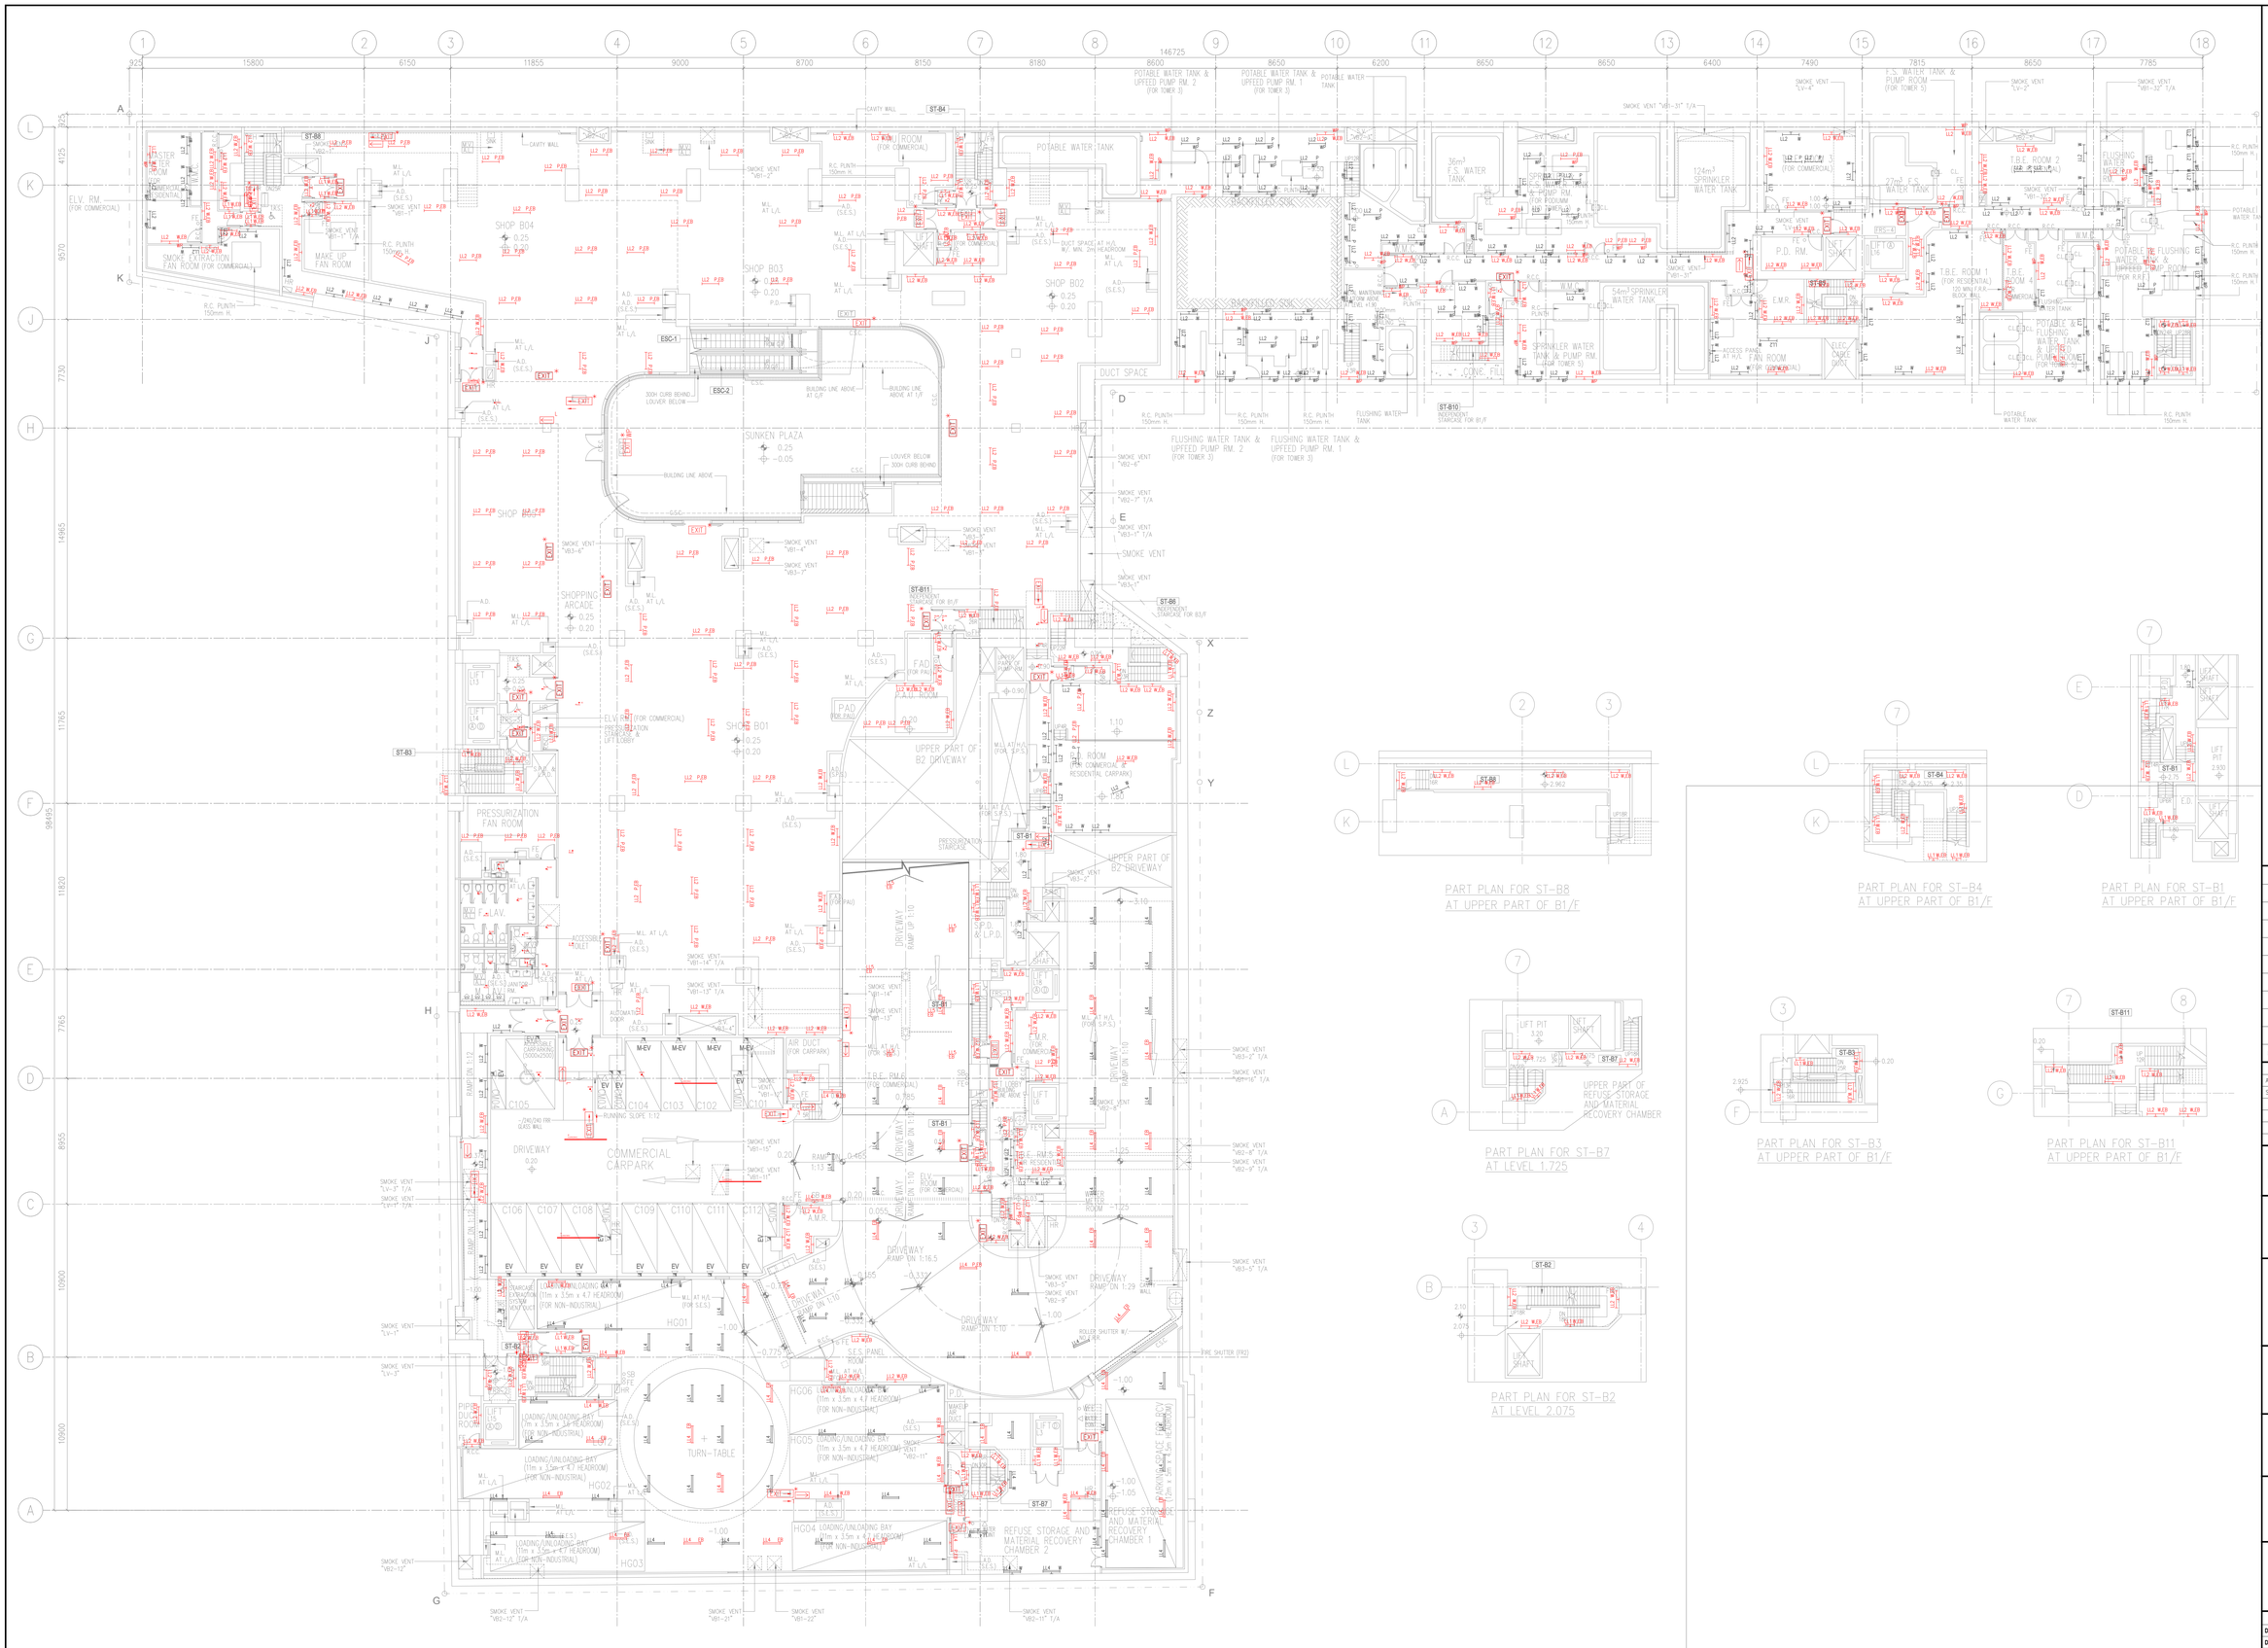


BASEMENT 1 FLOOR PLAN

LEGEND :

L1 P / L1 W	600mm SINGLE BATTEN T5 LED FITTING, BUILT-IN LED DRIVER, PENDANT / WALL MOUNTED TYPE
L2 P / L2 W	1200mm SINGLE BATTEN T5 LED FITTING, BUILT-IN LED DRIVER, PENDANT / WALL MOUNTED TYPE
L3 P / L3 W	600mm DOUBLE BATTEN T5 LED FITTING, BUILT-IN LED DRIVER, PENDANT / WALL MOUNTED TYPE WITH DIFFUSER
L4 P / L4 W	1200mm DOUBLE BATTEN T5 LED FITTING, BUILT-IN LED DRIVER, PENDANT / WALL MOUNTED TYPE WITH DIFFUSER
L5 P / L5 W	1200mm TRIPLE BATTEN T5 LED FITTING, BUILT-IN LED DRIVER, PENDANT / WALL MOUNTED TYPE
L6 P / L6 W	1200mm TRIPLE BATTEN T5 LED FITTING, BUILT-IN LED DRIVER, PENDANT / WALL MOUNTED TYPE WITH DIFFUSER
	LOW LEVEL PHOTOLUMINESCENT DIRECTIONAL PLATE
EXIT	HIGH LEVEL EXIT SIGN (FOR AUDIO/VISUAL ADVISORY SYSTEM)
EXIT	HIGH LEVEL DIRECTIONAL SIGN (FOR AUDIO/VISUAL ADVISORY SYSTEM)
EXIT	HIGH LEVEL DIRECTIONAL SIGN, DOUBLE FACED TYPE (FOR AUDIO/VISUAL ADVISORY SYSTEM)
	10A 1-WAY SINGLE POLE LIGHTING SWITCH AT 1350mm A.F.L. UNLESS OTHERWISE SPECIFIED
	10A 1-WAY SINGLE POLE WEATHERPROOF LIGHTING SWITCH AT 1350mm A.F.L. UNLESS OTHERWISE SPECIFIED
	MOTION SENSOR

ABBREVIATIONS :

- E ESSENTIAL POWER FROM EMERGENCY GENERATOR TO BE PROVIDED
- B BATTERY KIT FOR 2-HOURS
- WP WATERPROOF TYPE, IP65 UNLESS OTHERWISE SPECIFY
- P PENDANT TYPE, 2600 AFFL OR COORDINATION ON SITE
- W WALL MOUNTED TYPE, 2350 AFFL OR COORDINATION ON SITE

PART PLAN FOR ST-B8 AT UPPER PART OF B1/F

PART PLAN FOR ST-B4 AT UPPER PART OF B1/F

PART PLAN FOR ST-B1 AT UPPER PART OF B1/F

PART PLAN FOR ST-B7 AT LEVEL 7.725

PART PLAN FOR ST-B3 AT UPPER PART OF B1/F

PART PLAN FOR ST-B11 AT UPPER PART OF B1/F

PART PLAN FOR ST-B2 AT LEVEL 2.075

REV.	DESCRIPTION	BY	DATE
0	1ST SUBMISSION	AC	11/2024

	DRAWING REFERENCE	REV.	DATE
ARCHITECTURAL	A/GBP/110 (2nd AMENDMENT)	D	05/2024
STRUCTURAL			

CLIENT

NATION STAR DEVELOPMENT LIMITED

ARCHITECT

RONALD LU & PARTNERS

Ronald Lu & Partners (Hong Kong) Ltd.
呂元祥建築師事務所(香港)有限公司
33rd Floor, Wu Chung House,
213 Queen's Road East,
Wanchai, Hong Kong

CONSULTANT

wsp

7/F, One Kowloon
1 Wang Yuen Street
Kowloon Bay, Hong Kong

MAIN CONTRACTOR

中國海外房屋工程有限公司
CHINA OVERSEAS BUILDING CONSTRUCTION LIMITED

E & M CONTRACTOR

卓 裕 工 程 有 限 公 司
U-Tech Engineering Company Limited
Member of Sawgrass Group
6/F., TAK YIP WAN ROAD, KOWLOON, HONG KONG.
TEL : (852) 2765 ~ 5666 : FAX : (852) 2392 ~ 7422

PROJECT

PROPOSED DEVELOPMENT AT BAILEY STREET & WING KWONG STREET, TO KWA WAN, KLN.
INLAND LOT NO. 11279
(URA PROJECT KC-009)

TITLE

LIGHTING LAYOUT FOR BASEMENT 1 FLOOR PLAN

	NAME	INITIAL	DATE
DESIGNED BY	RONALD WONG		01/11/2024
DRAWN BY	AAREN CHU		01/11/2024
CHECKED BY	SAM KWOK		01/11/2024
APPROVED BY	WILSON YUEN		01/11/2024

DRAWING NO.	D/EE/203	DATE	31/10/2026
		REV.	0
STATUS		SCALE	1:150 @ A0
			DO NOT SCALE THE DRAWING