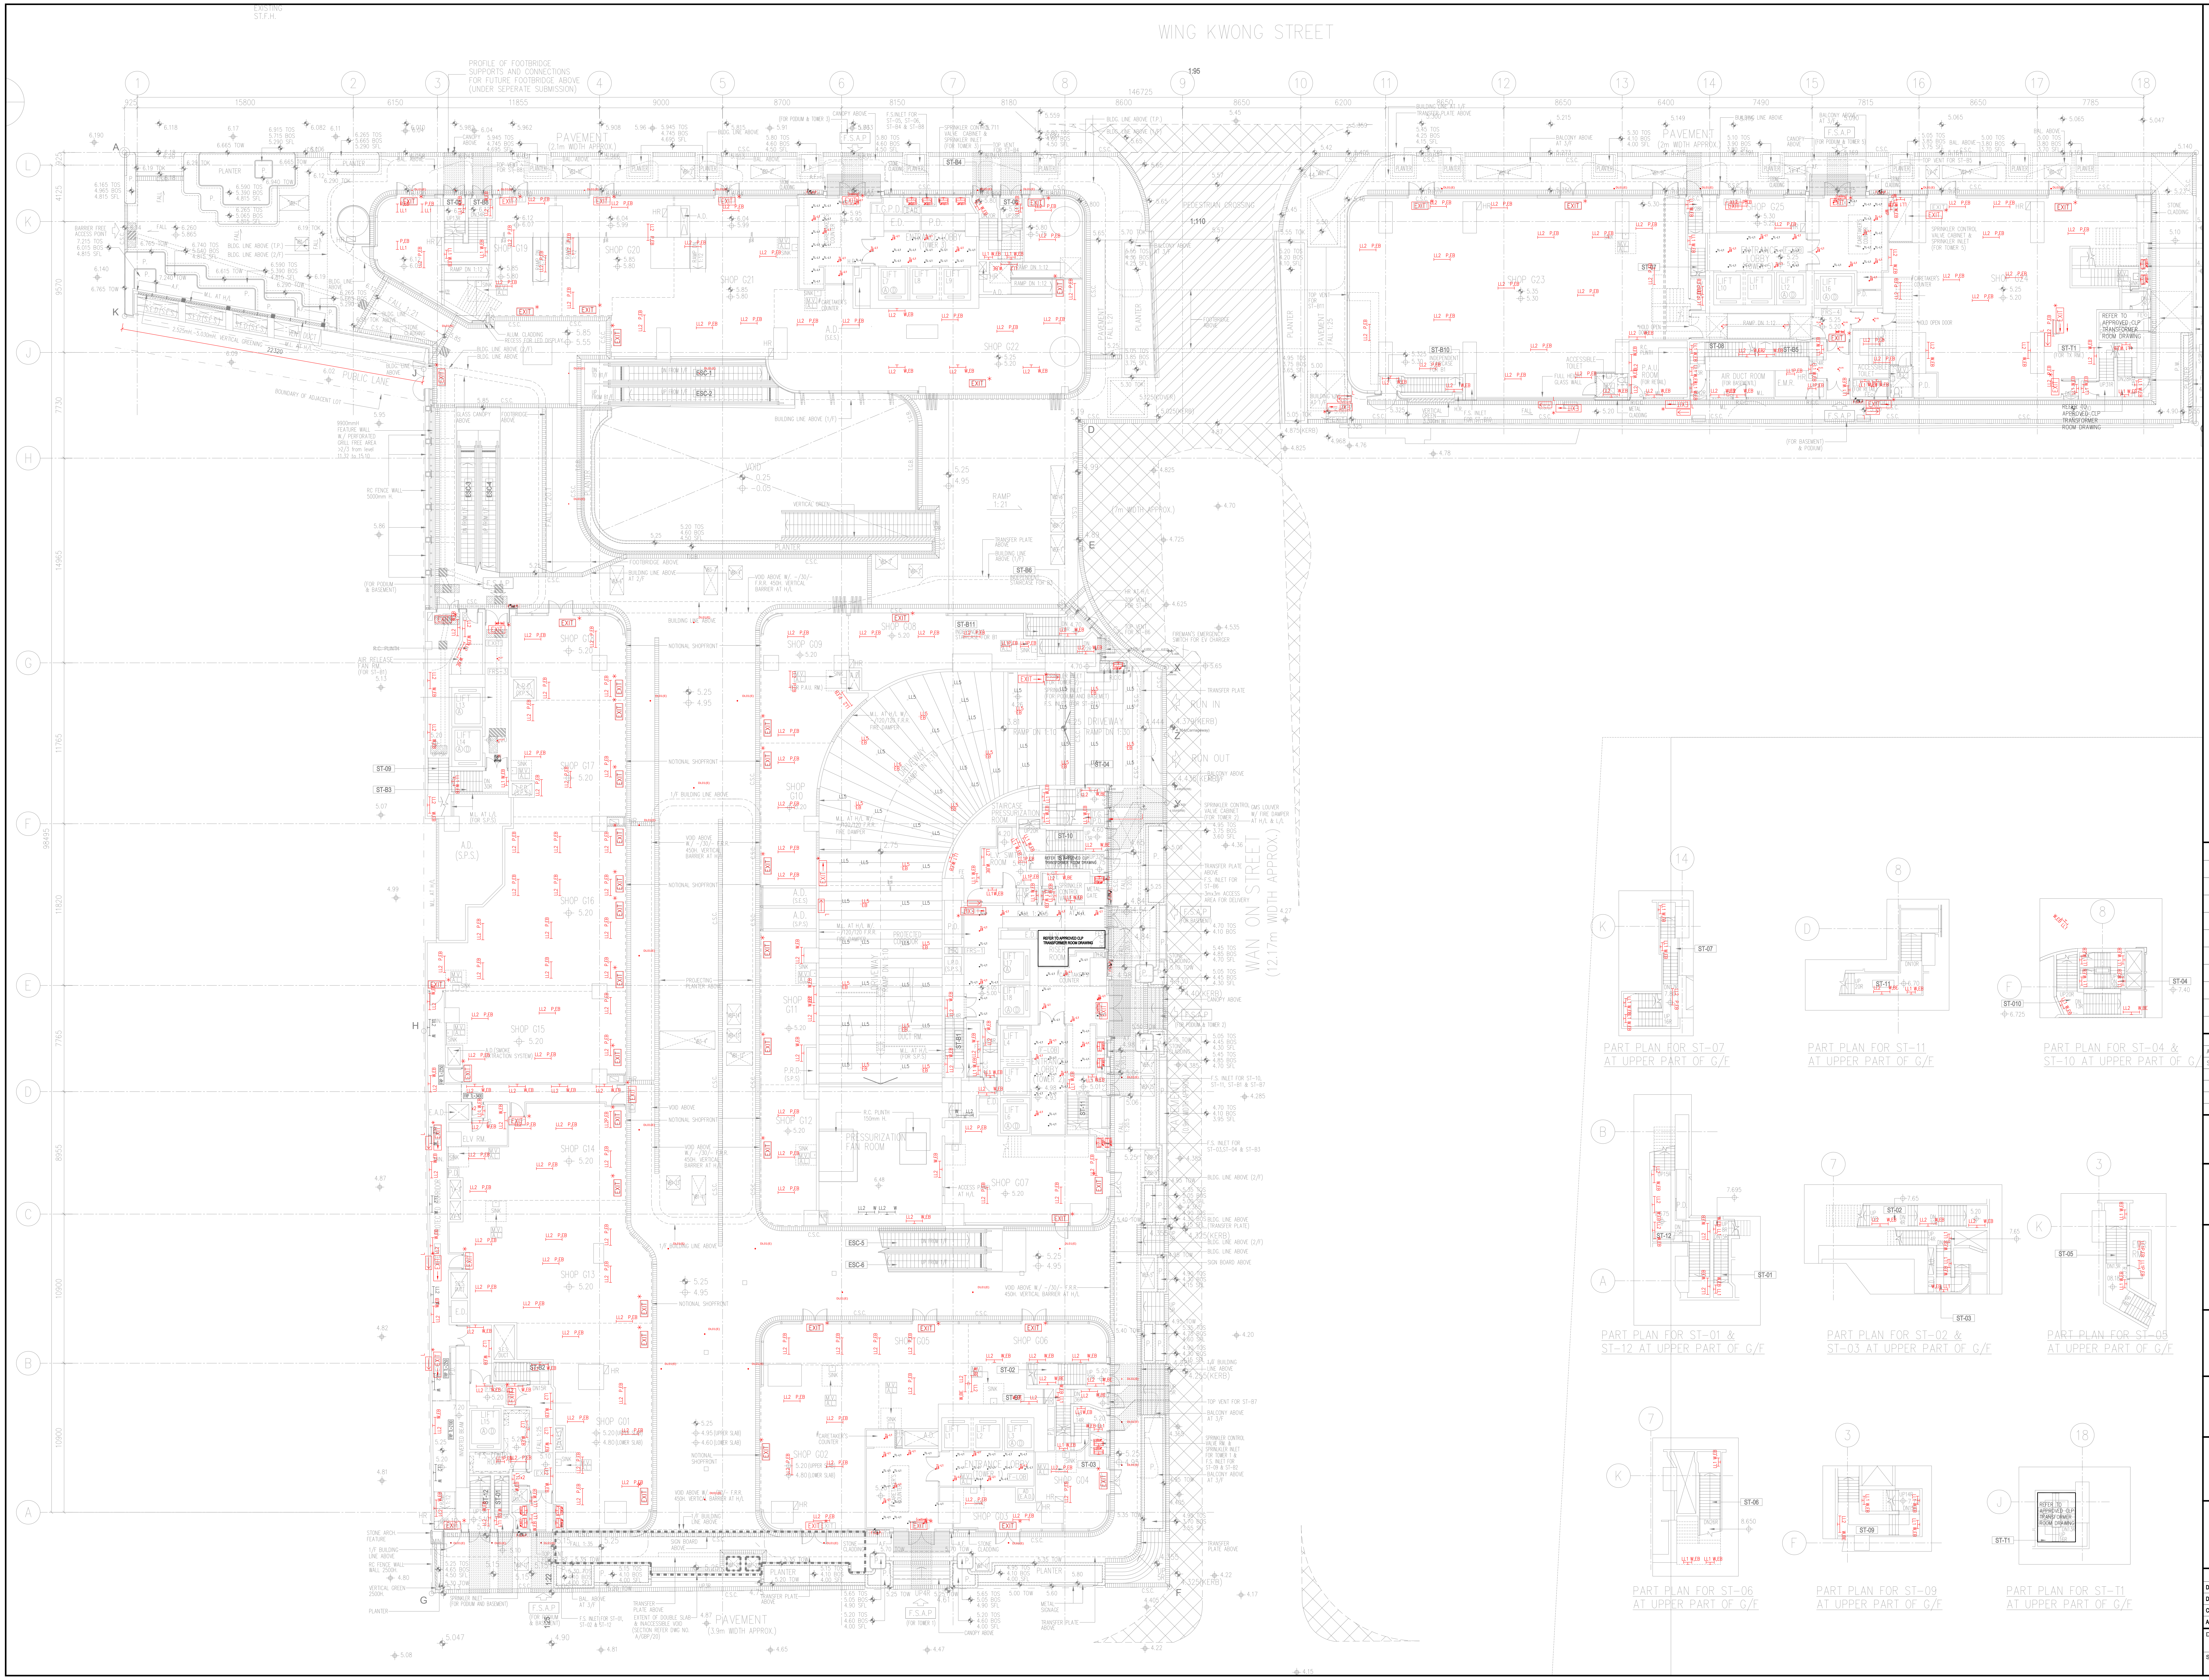
WING KWONG STREET
WAN ON STREET (12.17m WIDTH APPROX.)
PUBLIC LANE
PAVEMENT
PEDESTRIAN CROSSING
SHOP G01
SHOP G02
SHOP G05
SHOP G06
SHOP G07
SHOP G09
SHOP G13
SHOP G14
SHOP G15
SHOP G16
SHOP G17
SHOP G18
SHOP G20
SHOP G21
SHOP G22
SHOP G23
SHOP G24
SHOP G25
PART PLAN FOR ST-07 AT UPPER PART OF G/F
PART PLAN FOR ST-11 AT UPPER PART OF G/F
PART PLAN FOR ST-04 & ST-10 AT UPPER PART OF G/F
PART PLAN FOR ST-01 & ST-12 AT UPPER PART OF G/F
PART PLAN FOR ST-02 & ST-03 AT UPPER PART OF G/F
PART PLAN FOR ST-05 AT UPPER PART OF G/F
PART PLAN FOR ST-06 AT UPPER PART OF G/F
PART PLAN FOR ST-09 AT UPPER PART OF G/F
PART PLAN FOR ST-T1 AT UPPER PART OF G/F

LEGEND :

LL1 P	600mm SINGLE BATTEN T5 LED FITTING, BUILT-IN LED DRIVER, PENDANT TYPE
LL1P,EB LL1 W,EB	600mm SINGLE BATTEN T5 LED FITTING, BUILT-IN LED DRIVER, PENDANT / WALL MOUNTED TYPE WITH ESSENTIAL POWER
LL2 P LL2 W	1200mm SINGLE BATTEN T5 LED FITTING, BUILT-IN LED DRIVER, PENDANT / WALL MOUNTED TYPE
LL2 P,EB LL2 W,EB	1200mm SINGLE BATTEN T5 LED FITTING, BUILT-IN LED DRIVER, PENDANT / WALL MOUNTED TYPE WITH ESSENTIAL POWER
LL4 P LL4 W	1200mm TWIN BATTEN T5 LED FITTING, BUILT-IN LED DRIVER, PENDANT TYPE
LL4 P,EB LL4 W,EB	1200mm TWIN BATTEN T5 LED FITTING, BUILT-IN LED DRIVER, PENDANT TYPE WITH ESSENTIAL POWER
⇐ L / ⇒ L	LOW LEVEL PHOTOLUMINESCENT DIRECTIONAL PLATE
EXIT *	HIGH LEVEL EXIT SIGN (FOR AUDIO/VISUAL ADVISORY SYSTEM)
EXIT→ * / ←EXIT * / ↑EXIT *	HIGH LEVEL DIRECTIONAL SIGN (FOR AUDIO/VISUAL ADVISORY SYSTEM)
EXIT→ * / ←EXIT *	HIGH LEVEL DIRECTIONAL SIGN, DOUBLE FACED TYPE (FOR AUDIO/VISUAL ADVISORY SYSTEM)
	10A 1-WAY SINGLE POLE LIGHTING SWITCH AT 1350mm A.F.F.L. UNLESS OTHERWISE SPECIFIED
	10A 1-WAY SINGLE POLE WEATHERPROOF LIGHTING SWITCH AT 1350mm A.F.F.L. UNLESS OTHERWISE SPECIFIED
OS	MOTION SENSOR

ABBREVIATIONS :

E	ESSENTIAL POWER FROM EMERGENCY GENERATOR TO BE PROVIDED
B	BATTERY KIT FOR 2-HOURS
WP	WATERPROOF TYPE, IP65 UNLESS OTHERWISE SPECIFY
P	PENDANT TYPE, 2600 AFFL OR COORDINATION ON SITE
W	WALL MOUNTED TYPE, 2350 AFFL OR COORDINATION ON SITE

REV.	DESCRIPTION	BY	DATE
0	1ST SUBMISSION	AC	11/2024

	DRAWING REFERENCE	REV.	DATE
ARCHITECTURAL	A/GBP/10 (3nd AMENDMENT)	D	05/2024
STRUCTURAL			

CLIENT

NATION STAR DEVELOPMENT LIMITED

ARCHITECT

RONALD LU & PARTNERS

Ronald Lu & Partners (Hong Kong) Ltd.
呂元祥建築師事務所(香港)有限公司
33rd Floor, Wu Chung House,
213 Queen's Road East,
Wanchai, Hong Kong

CONSULTANT

wsp

7/F, One Kowloon
1 Wang Yuen Street
Kowloon Bay, Hong Kong

MAIN CONTRACTOR

中國海外房屋工程有限公司
CHINA OVERSEAS BUILDING CONSTRUCTION LIMITED

E & M CONTRACTOR

卓 裕 工 程 有 限 公 司
U-Tech Engineering Company Limited
Member of Towngas Group
6/F, 100 TO KWA WAN ROAD, KOWLOON, HONG KONG
TEL : (852) 2765 - 5666 ; FAX : (852) 2392 - 7422

PROJECT
PROPOSED DEVELOPMENT AT BAILEY STREET
& WING KWONG STREET, TO KWA WAN, KLN.
INLAND LOT NO. 11279
(URA PROJECT KC-009)

TITLE

LIGHTING LAYOUT FOR G/F PLAN

	NAME	INITIAL	DATE
DESIGNED BY	RONALD WONG		01/11/2024
DRAWN BY	AAREN CHU		01/11/2024
CHECKED BY	SAM KWOK		01/11/2024
APPROVED BY	WILSON YUEN		01/11/2024

DRAWING NO. D/EE/204
DATE 31/10/2026
REV. 0
STATUS
SCALE 1:150 @ A0
DO NOT SCALE THE DRAWING