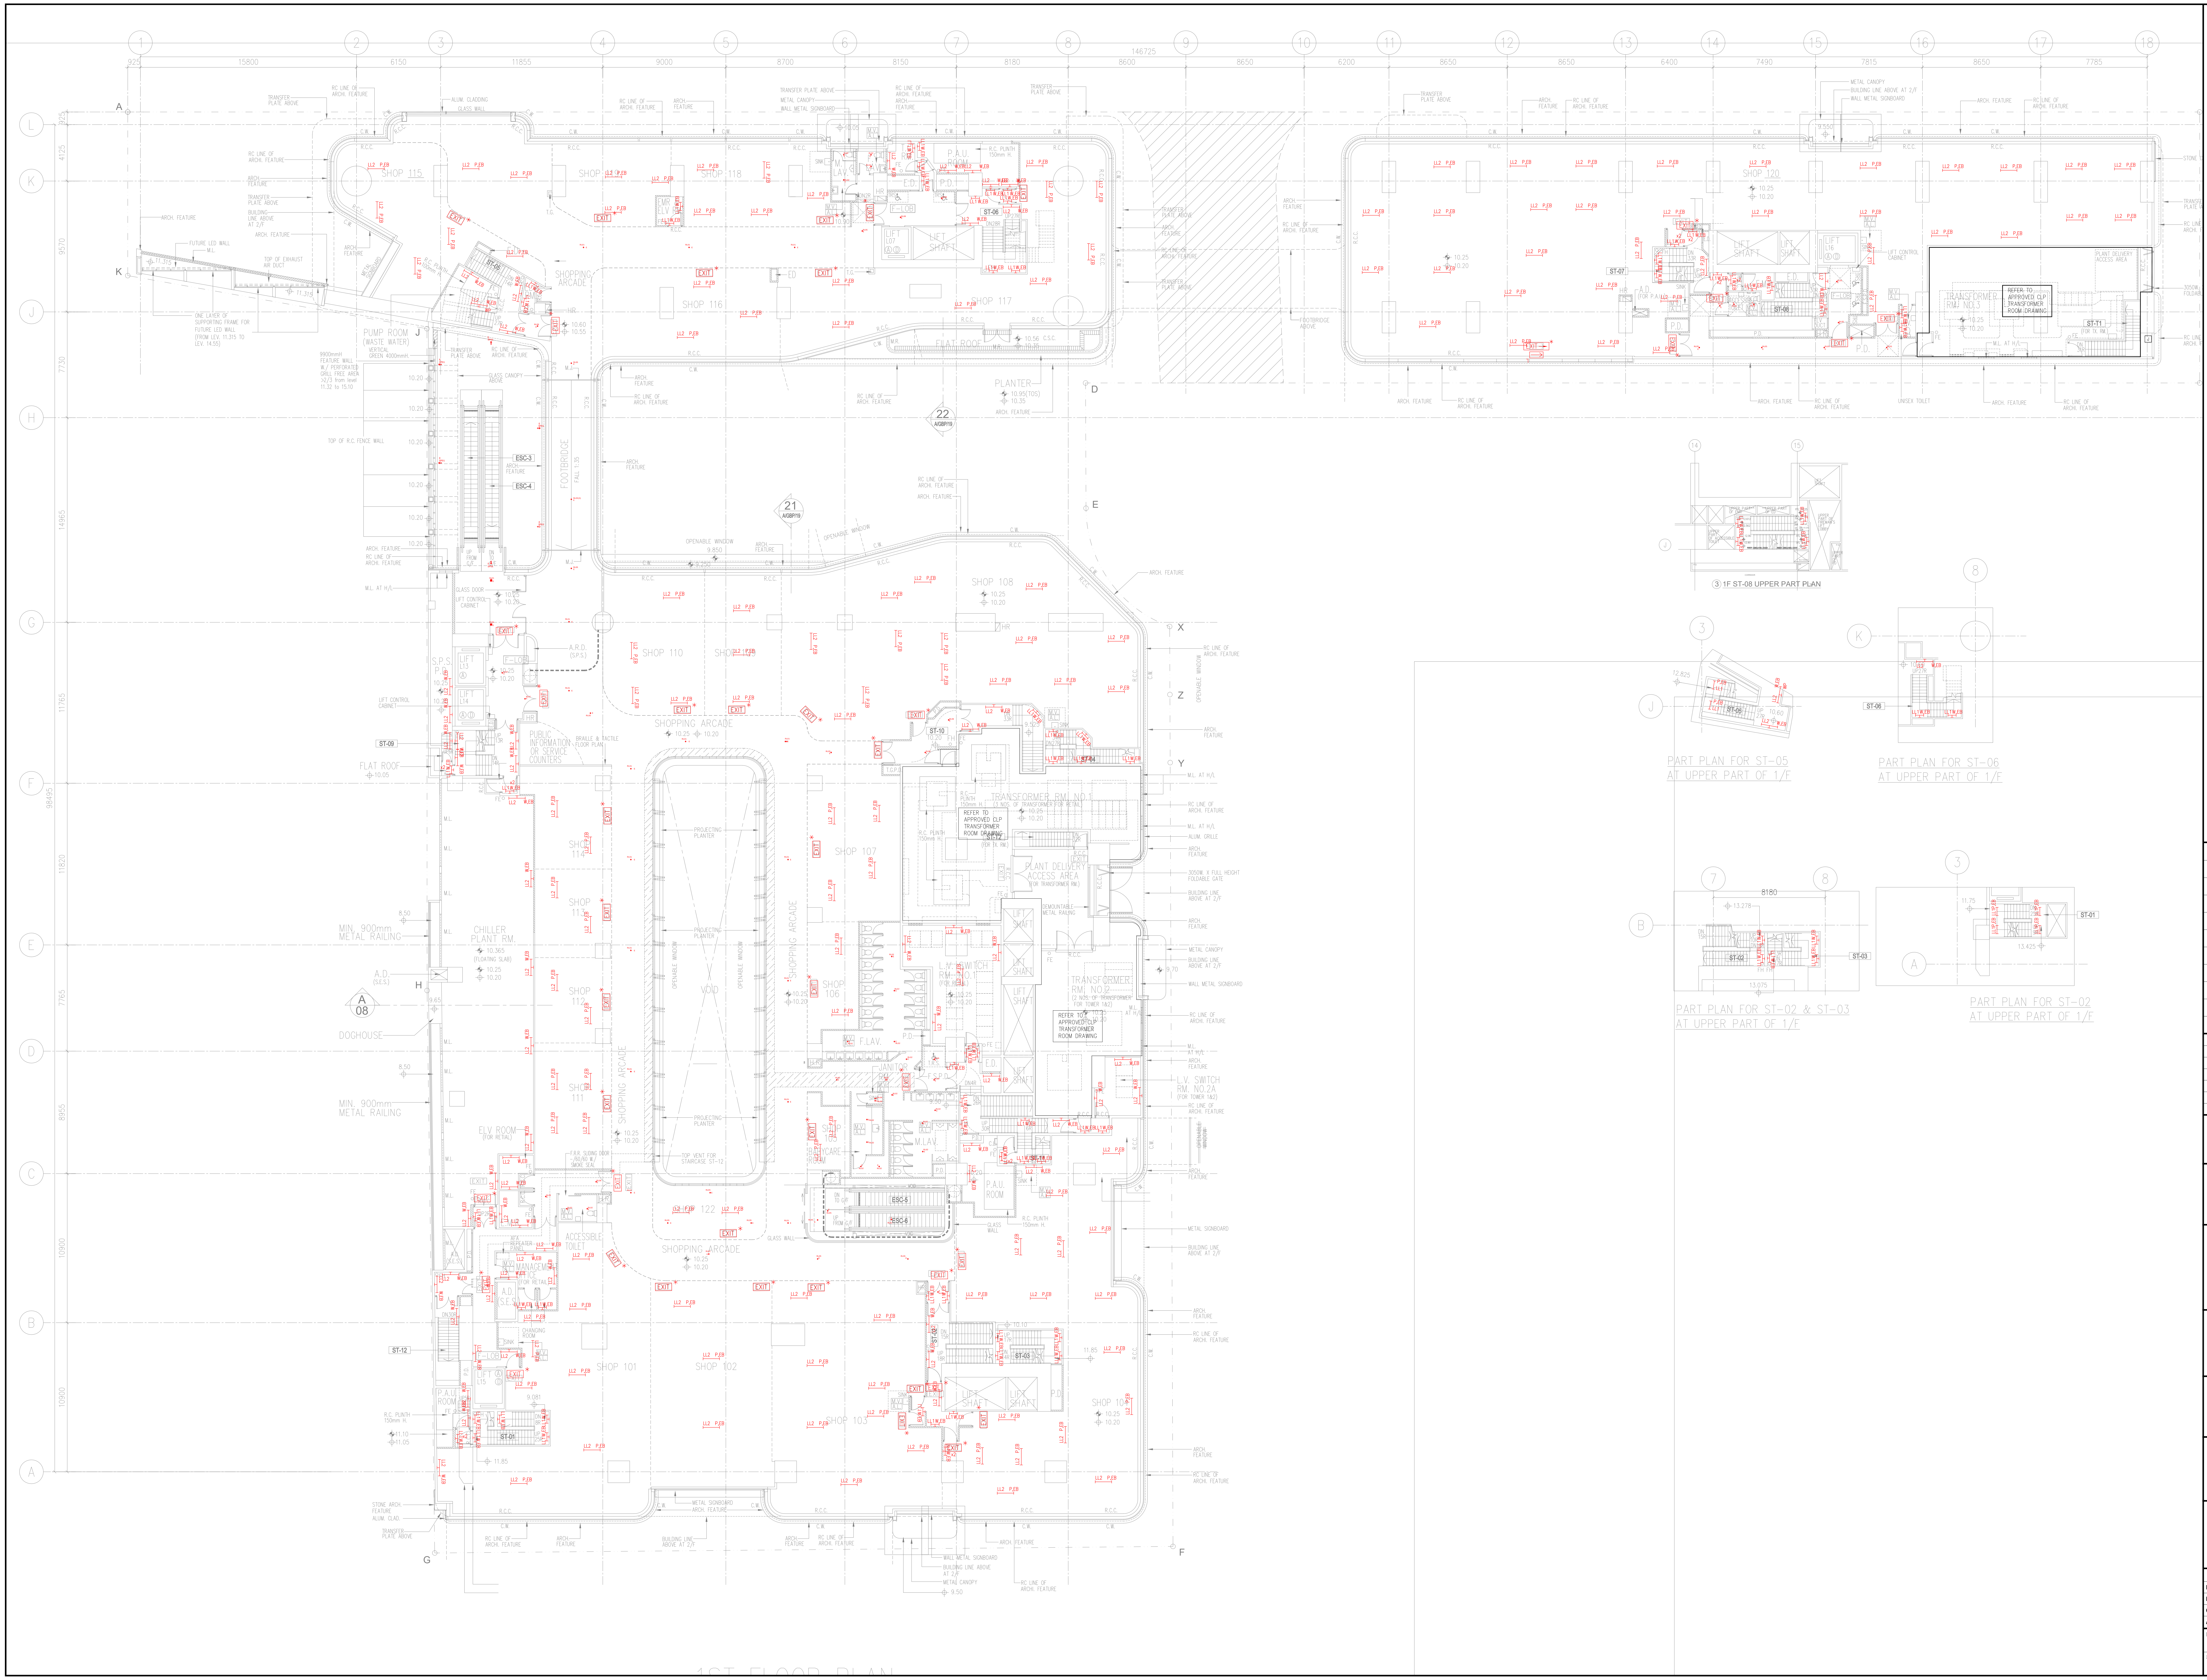

## LEGEND :

| | |
|---|---|
| | 600mm SINGLE BATTEN T5 LED FITTING, BUILT-IN LED DRIVER, PENDANT TYPE |
| LL1P,EB LL1W,EB | 600mm SINGLE BATTEN T5 LED FITTING, BUILT-IN LED DRIVER, PENDANT / WALL MOUNTED TYPE WITH ESSENTIAL POWER |
| LL2 P | 1200mm SINGLE BATTEN T5 LED FITTING, BUILT-IN LED DRIVER, PENDANT / WALL MOUNTED TYPE |
| LL2 P,EB LL2 W,EB | 1200mm SINGLE BATTEN T5 LED FITTING, BUILT-IN LED DRIVER, PENDANT / WALL MOUNTED TYPE WITH ESSENTIAL POWER |
| LL4 P | 1200mm TWIN BATTEN T5 LED FITTING, BUILT-IN LED DRIVER, PENDANT TYPE |
| LL4 P,EB | 1200mm TWIN BATTEN T5 LED FITTING, BUILT-IN LED DRIVER, PENDANT TYPE WITH ESSENTIAL POWER |
| ← L / → L | LOW LEVEL PHOTOLUMINESCENT DIRECTIONAL PLATE |
| EXIT * | HIGH LEVEL EXIT SIGN (FOR AUDIO/VISUAL ADVISORY SYSTEM) |
| EXIT→ * / ←EXIT * / ↑ EXIT * | HIGH LEVEL DIRECTIONAL SIGN (FOR AUDIO/VISUAL ADVISORY SYSTEM) |
| EXIT→ * / ←EXIT * | HIGH LEVEL DIRECTIONAL SIGN, DOUBLE FACED TYPE (FOR AUDIO/VISUAL ADVISORY SYSTEM) |
| | 10A 1-WAY SINGLE POLE LIGHTING SWITCH AT 1350mm A.F.F.L. UNLESS OTHERWISE SPECIFIED |
| | 10A 1-WAY SINGLE POLE WEATHERPROOF LIGHTING SWITCH AT 1350mm A.F.F.L. UNLESS OTHERWISE SPECIFIED |
| | MOTION SENSOR |

## ABBREVIATIONS :

| | |
|---|---|
| E | ESSENTIAL POWER FROM EMERGENCY GENERATOR TO BE PROVIDED |
| B | BATTERY KIT FOR 2-HOURS |
| WP | WATERPROOF TYPE, IP65 UNLESS OTHERWISE SPECIFY |
| P | PENDANT TYPE, 2600 AFFL OR COORDINATION ON SITE |
| W | WALL MOUNTED TYPE, 2350 AFFL OR COORDINATION ON SITE |

| REV. | DESCRIPTION | BY | DATE |
|---|---|---|---|
| 0 | 1ST SUBMISSION | AC | 12/2024 |

| | DRAWING REFERENCE | REV. | DATE |
|---|---|---|---|
| ARCHITECTURAL | A/GBP/10 (3nd AMENDMENT) | D | 05/2024 |
| STRUCTURAL | | | |

CLIENT

**NATION STAR DEVELOPMENT LIMITED**

ARCHITECT

RONALD LU & PARTNERS

Ronald Lu & Partners (Hong Kong) Ltd.
呂元祥建築師事務所(香港)有限公司
33rd Floor, Wu Chung House,
213 Queen's Road East,
Wanchai, Hong Kong

CONSULTANT

wsp

7/F, One Kowloon
1 Wang Yuen Street
Kowloon Bay, Hong Kong

**MAIN CONTRACTOR**

中國海外房屋工程有限公司
CHINA OVERSEAS BUILDING CONSTRUCTION LIMITED

E & M CONTRACTOR

卓 裕 工 程 有 限 公 司
U-Tech Engineering Company Limited
Member of Towngas Group
6/F, 100 TO KWA WAN ROAD, KOWLOON, HONG KONG
TEL : (852) 2765 - 5666 ; FAX : (852) 2392 - 7422

PROJECT
PROPOSED DEVELOPMENT AT BAILEY STREET
& WING KWONG STREET, TO KWA WAN, KLN.
INLAND LOT NO. 11279
(URA PROJECT KC-009)

TITLE

LIGHTING LAYOUT FOR 1/F PLAN

| | NAME | INITIAL | DATE |
|---|---|---|---|
| **DESIGNED BY** | RONALD WONG | | 5/12/2024 |
| **DRAWN BY** | AAREN CHU | | 5/12/2024 |
| **CHECKED BY** | SAM KWOK | | 5/12/2024 |
| **APPROVED BY** | WILSON YUEN | | 5/12/2024 |

| | | |
|---|---|---|
| DRAWING NO. D/EE/205 | DATE 31/10/2026 | REV. 0 |
| STATUS | SCALE 1:150 @ A0 | |
| | DO NOT SCALE THE DRAWING | |