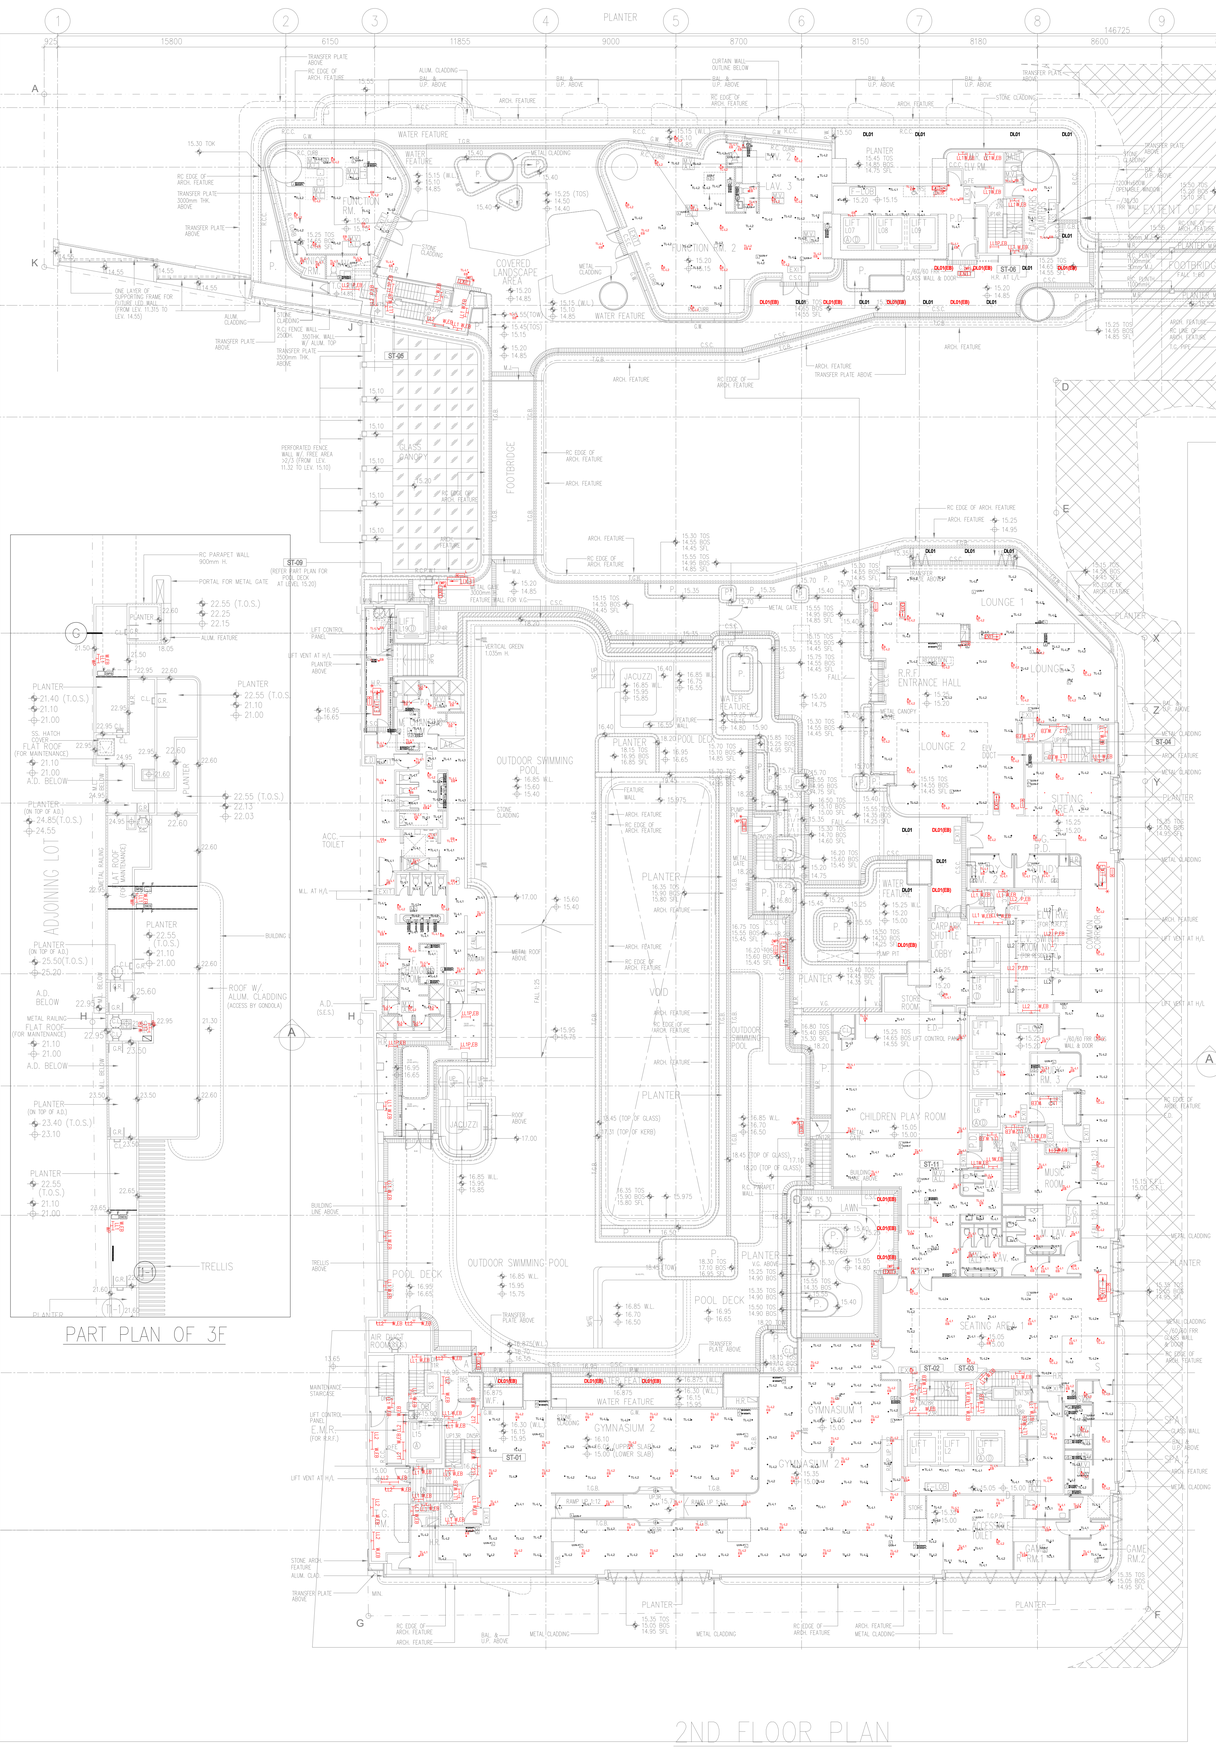


LEGEND :

	600mm SMALL BATTEN T5 LED FITTING, BUILT-IN LED DIMER, PROGRAMMABLE TYPE
	600mm SMALL BATTEN T5 LED FITTING, BUILT-IN LED DIMER, 3 HOURS BATTERY PACK WITH STANDBY MODE & T5 HOURS BATTERY
	1200mm SMALL BATTEN T5 LED FITTING, BUILT-IN LED DIMER, PROGRAMMABLE TYPE
	1200mm SMALL BATTEN T5 LED FITTING, BUILT-IN LED DIMER, 3 HOURS BATTERY PACK WITH STANDBY MODE & T5 HOURS BATTERY
	1200mm TBS BATTEN T5 LED FITTING, BUILT-IN LED DIMER, PROGRAMMABLE TYPE
	1200mm TBS BATTEN T5 LED FITTING, BUILT-IN LED DIMER, 3 HOURS BATTERY PACK WITH STANDBY MODE
	LOW LEVEL PHOTOLUMINESCENT DIRECTIONAL PLATE
	HIGH LEVEL EXIT SIGN (FOR AUDIO/VISUAL ADVISORY SYSTEM)
	HIGH LEVEL DIRECTIONAL SIGN (FOR AUDIO/VISUAL ADVISORY SYSTEM)
	HIGH LEVEL DIRECTIONAL SIGN, DOUBLE FACED TYPE (FOR AUDIO/VISUAL ADVISORY SYSTEM)
	32A 1.5 WAY SINGLE POLE LOUDING SWITCH AT 1500mm A.F.L. UNLESS OTHERWISE SPECIFIED
	32A 1.5 WAY SINGLE POLE LOUDING SWITCH AT 1500mm A.F.L. UNLESS OTHERWISE SPECIFIED WITH MOTION SENSOR
P.W.D.	600mm SMALL BATTEN T5 LED FITTING, BUILT-IN LED DIMER, PROGRAMMABLE TYPE, 3 HOURS BATTERY BACK UP
P.W.D.	1200mm SMALL BATTEN T5 LED FITTING, BUILT-IN LED DIMER, PROGRAMMABLE TYPE, 3 HOURS BATTERY BACK UP
	RECESSED DOWN LIGHT CH-L1 (DETAIL REFERS TO RWA DESIGN DRAWING)
	RECESSED DOWN LIGHT CH-L2 (DETAIL REFERS TO RWA DESIGN DRAWING)
	LED LIGHT STRIP CH-L3 (DETAIL REFERS TO RWA DESIGN DRAWING)

ABBREVIATIONS :

E	ESSENTIAL POWER FROM EMERGENCY GENERATOR TO BE PROVIDED
B	BATTERY KIT FOR 3-HOURS
WP	WATERPROOF TYPE, IP65 UNLESS OTHERWISE SPECIFY
P	PENDANT TYPE, 2600 AFL OR COORDINATION ON SITE
W	WALL MOUNTED TYPE, 2350 AFL OR COORDINATION ON SITE

REV.	DESCRIPTION	BY	DATE
1	2ND SUBMISSION	AC	8/2025
0	1ST SUBMISSION	AC	12/2024

	DRAWING REFERENCE	REV.	DATE
ARCHITECTURAL	A/GBP/08 (8th AMENDMENT)	F	06/2025
STRUCTURAL			

CLIENT

NATION STAR DEVELOPMENT LIMITED

ARCHITECT

RONALD LU & PARTNERS

Ronald Lu & Partners (Hong Kong) Ltd.
香化祥建築師事務所(香港)有限公司
33rd Floor, Wu Chung House,
213 Queen's Road East,
Wanchai, Hong Kong

CONSULTANT

wsp

7/F, One Kowloon
1 Wang Yuen Street
Kowloon Bay, Hong Kong

MAIN CONTRACTOR

中國海外寶厦工程有限公司
CHINA OVERSEAS BUILDING CONSTRUCTION LIMITED

E & M CONTRACTOR

卓格工程有限公司
U-Tech Engineering Company Limited
Member of Teamjet Group
6/F, TOO TO KWAI WAN ROAD, KOWLOON, HONG KONG
TEL : (852) 2765 - 5668 ; FAX : (852) 2392 - 7422

PROJECT

PROPOSED DEVELOPMENT AT BAILEY STREET & WING KWONG STREET, TO KWA WAN, KLN.
INLAND LOT NO. 11279
(URA PROJECT KC-009)

TITLE

LIGHTING LAYOUT FOR 2/F PLAN

	NAME	INITIAL	DATE
DESIGNED BY	RONALD WONG		13/8/2025
DRAWN BY	AAREN CHU		13/8/2025
CHECKED BY	SAM KWOK		13/8/2025
APPROVED BY	WILSON YUEN		13/8/2025

DRAWING NO. D/EE/206

DATE 31/10/2026

REV. 1

STATUS

SCALE 1:150 @ A0

DO NOT SCALE THE DRAWING