
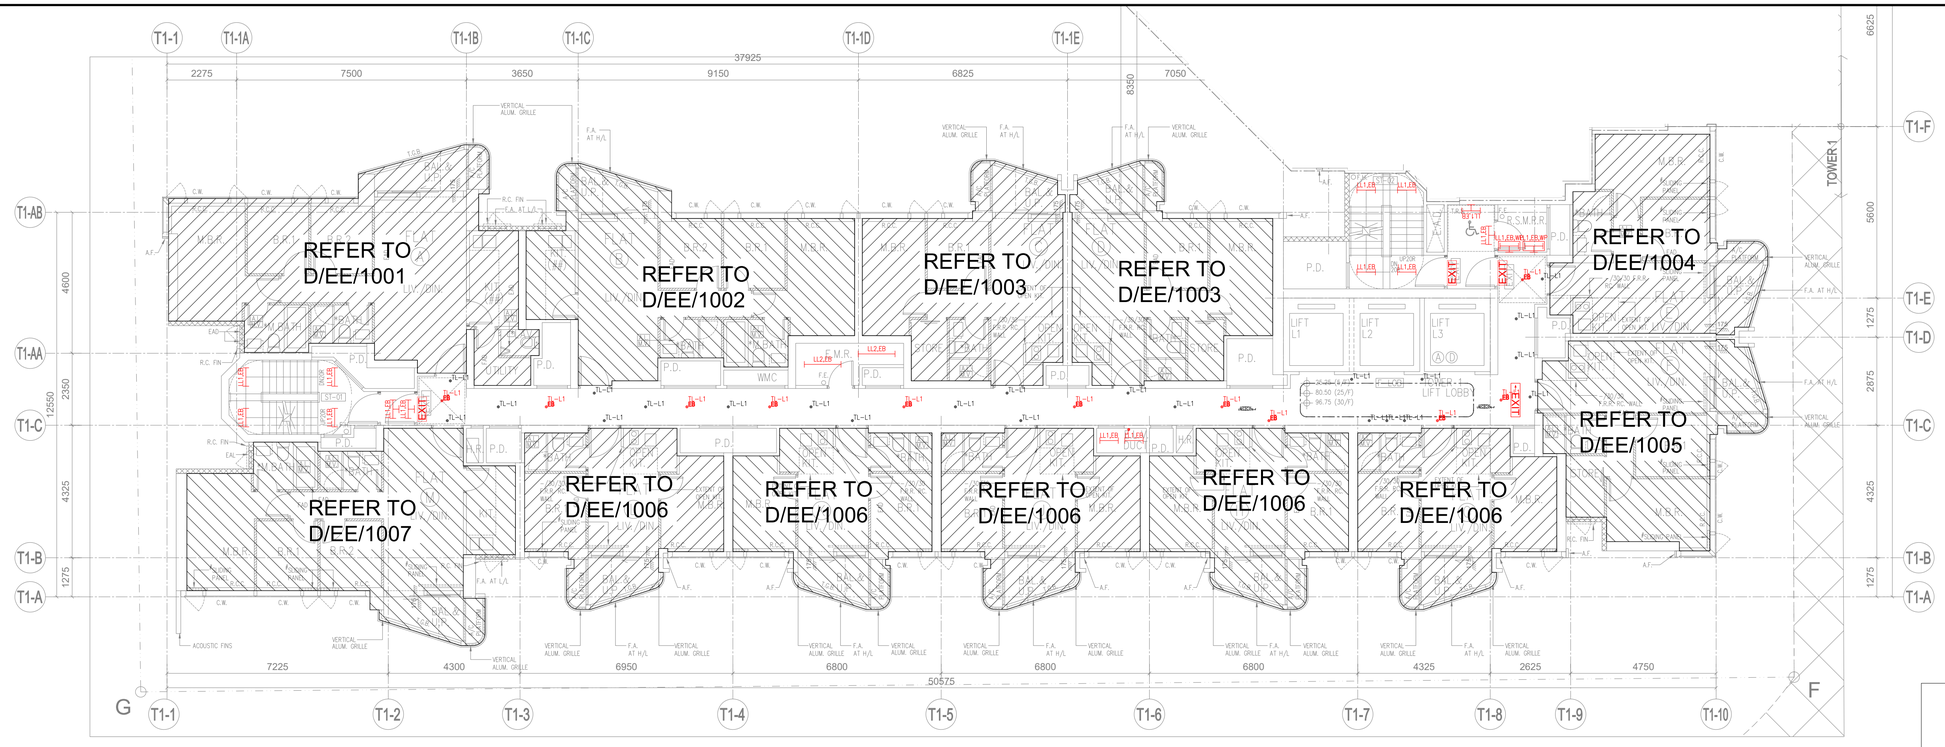


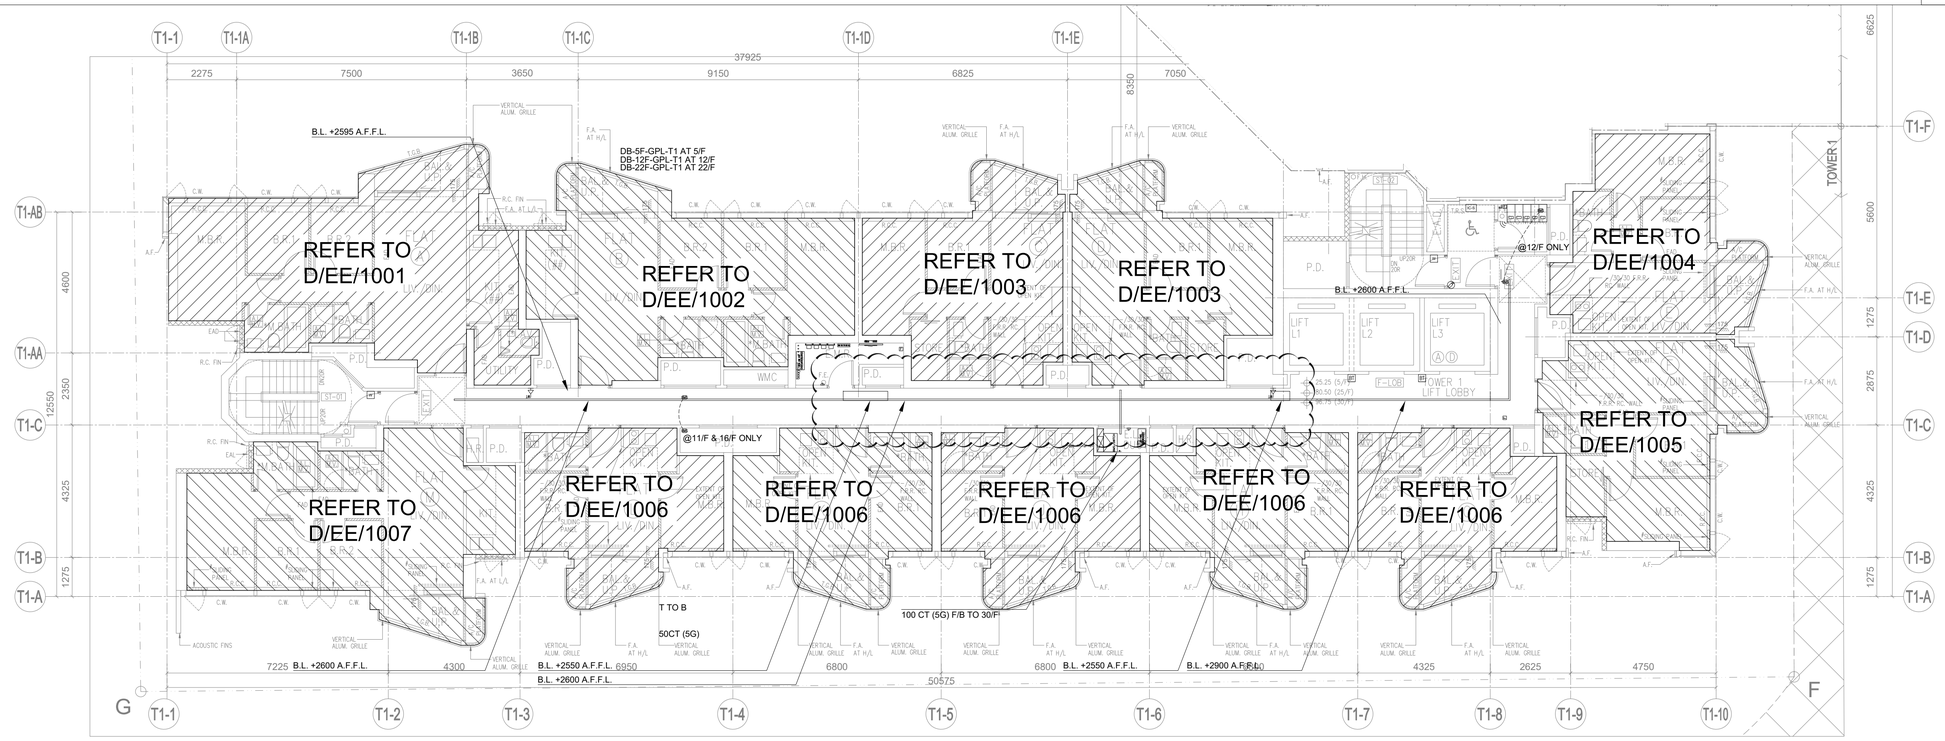

	"X"	"Y"
22/F TO 30/F	23F	22F
12/F TO 21/F	15F	12F
3/F TO 11/F	6F	5F

LTG

PWR & ELV

REV.	DESCRIPTION	BY	DATE
1	2nd SUBMISSION	WC	12/2025
0	1ST SUBMISSION	AC	0

	DRAWING REFERENCE	REV.	DATE
ARCHITECTURAL	A/GBP/12 (9th AMENDMENT)	E	11/2025
STRUCTURAL			

CLIENT
NATION STAR DEVELOPMENT LIMITED

ARCHITECT
RONALD LU & PARTNERS
Ronald Lu & Partners (Hong Kong) Ltd.
呂元祥建築師事務所(香港)有限公司
33rd Floor, Wu Chung House,
213 Queen's Road East,
Wanchai, Hong Kong

CONSULTANT
wsp
7/F, One Kowloon
1 Wang Yuen Street
Kowloon Bay, Hong Kong

MAIN CONTRACTOR
中国海外房屋工程有限公司
CHINA OVERSEAS BUILDING CONSTRUCTION LIMITED

E & M CONTRACTOR
卓裕工程有限公司
U-Tech Engineering Company Limited
Member of Townqas Group
6/F., 100 TO KWA WAN ROAD, KOWLOON, HONG KONG
TEL : (852) 2765 - 5666 ; FAX : (852) 2392 - 7422

PROJECT
PROPOSED DEVELOPMENT AT BAILEY STREET & WING KWONG STREET, TO KWA WAN, KLN.
INLAND LOT NO. 11279
(URA PROJECT KC-009)

TITLE
ENLARGED ELECTRICAL LAYOUT
FOR 3/F TO 30/F PLAN OF TOWER 1

	NAME	INITIAL	DATE
DESIGNED BY	RONALD WONG		12/12/2025
DRAWN BY	AAREN CHU		12/12/2025
CHECKED BY	SAM KWOK		12/12/2025
APPROVED BY	WILSON YUEN		12/12/2025

DRAWING NO.	DATE (DD/MM/YY)	REV.
UT/KC009/EL/602	28/10/2026	1
STATUS	SCALE 1:100 @ A1	
	DO NOT SCALE THE DRAWING	