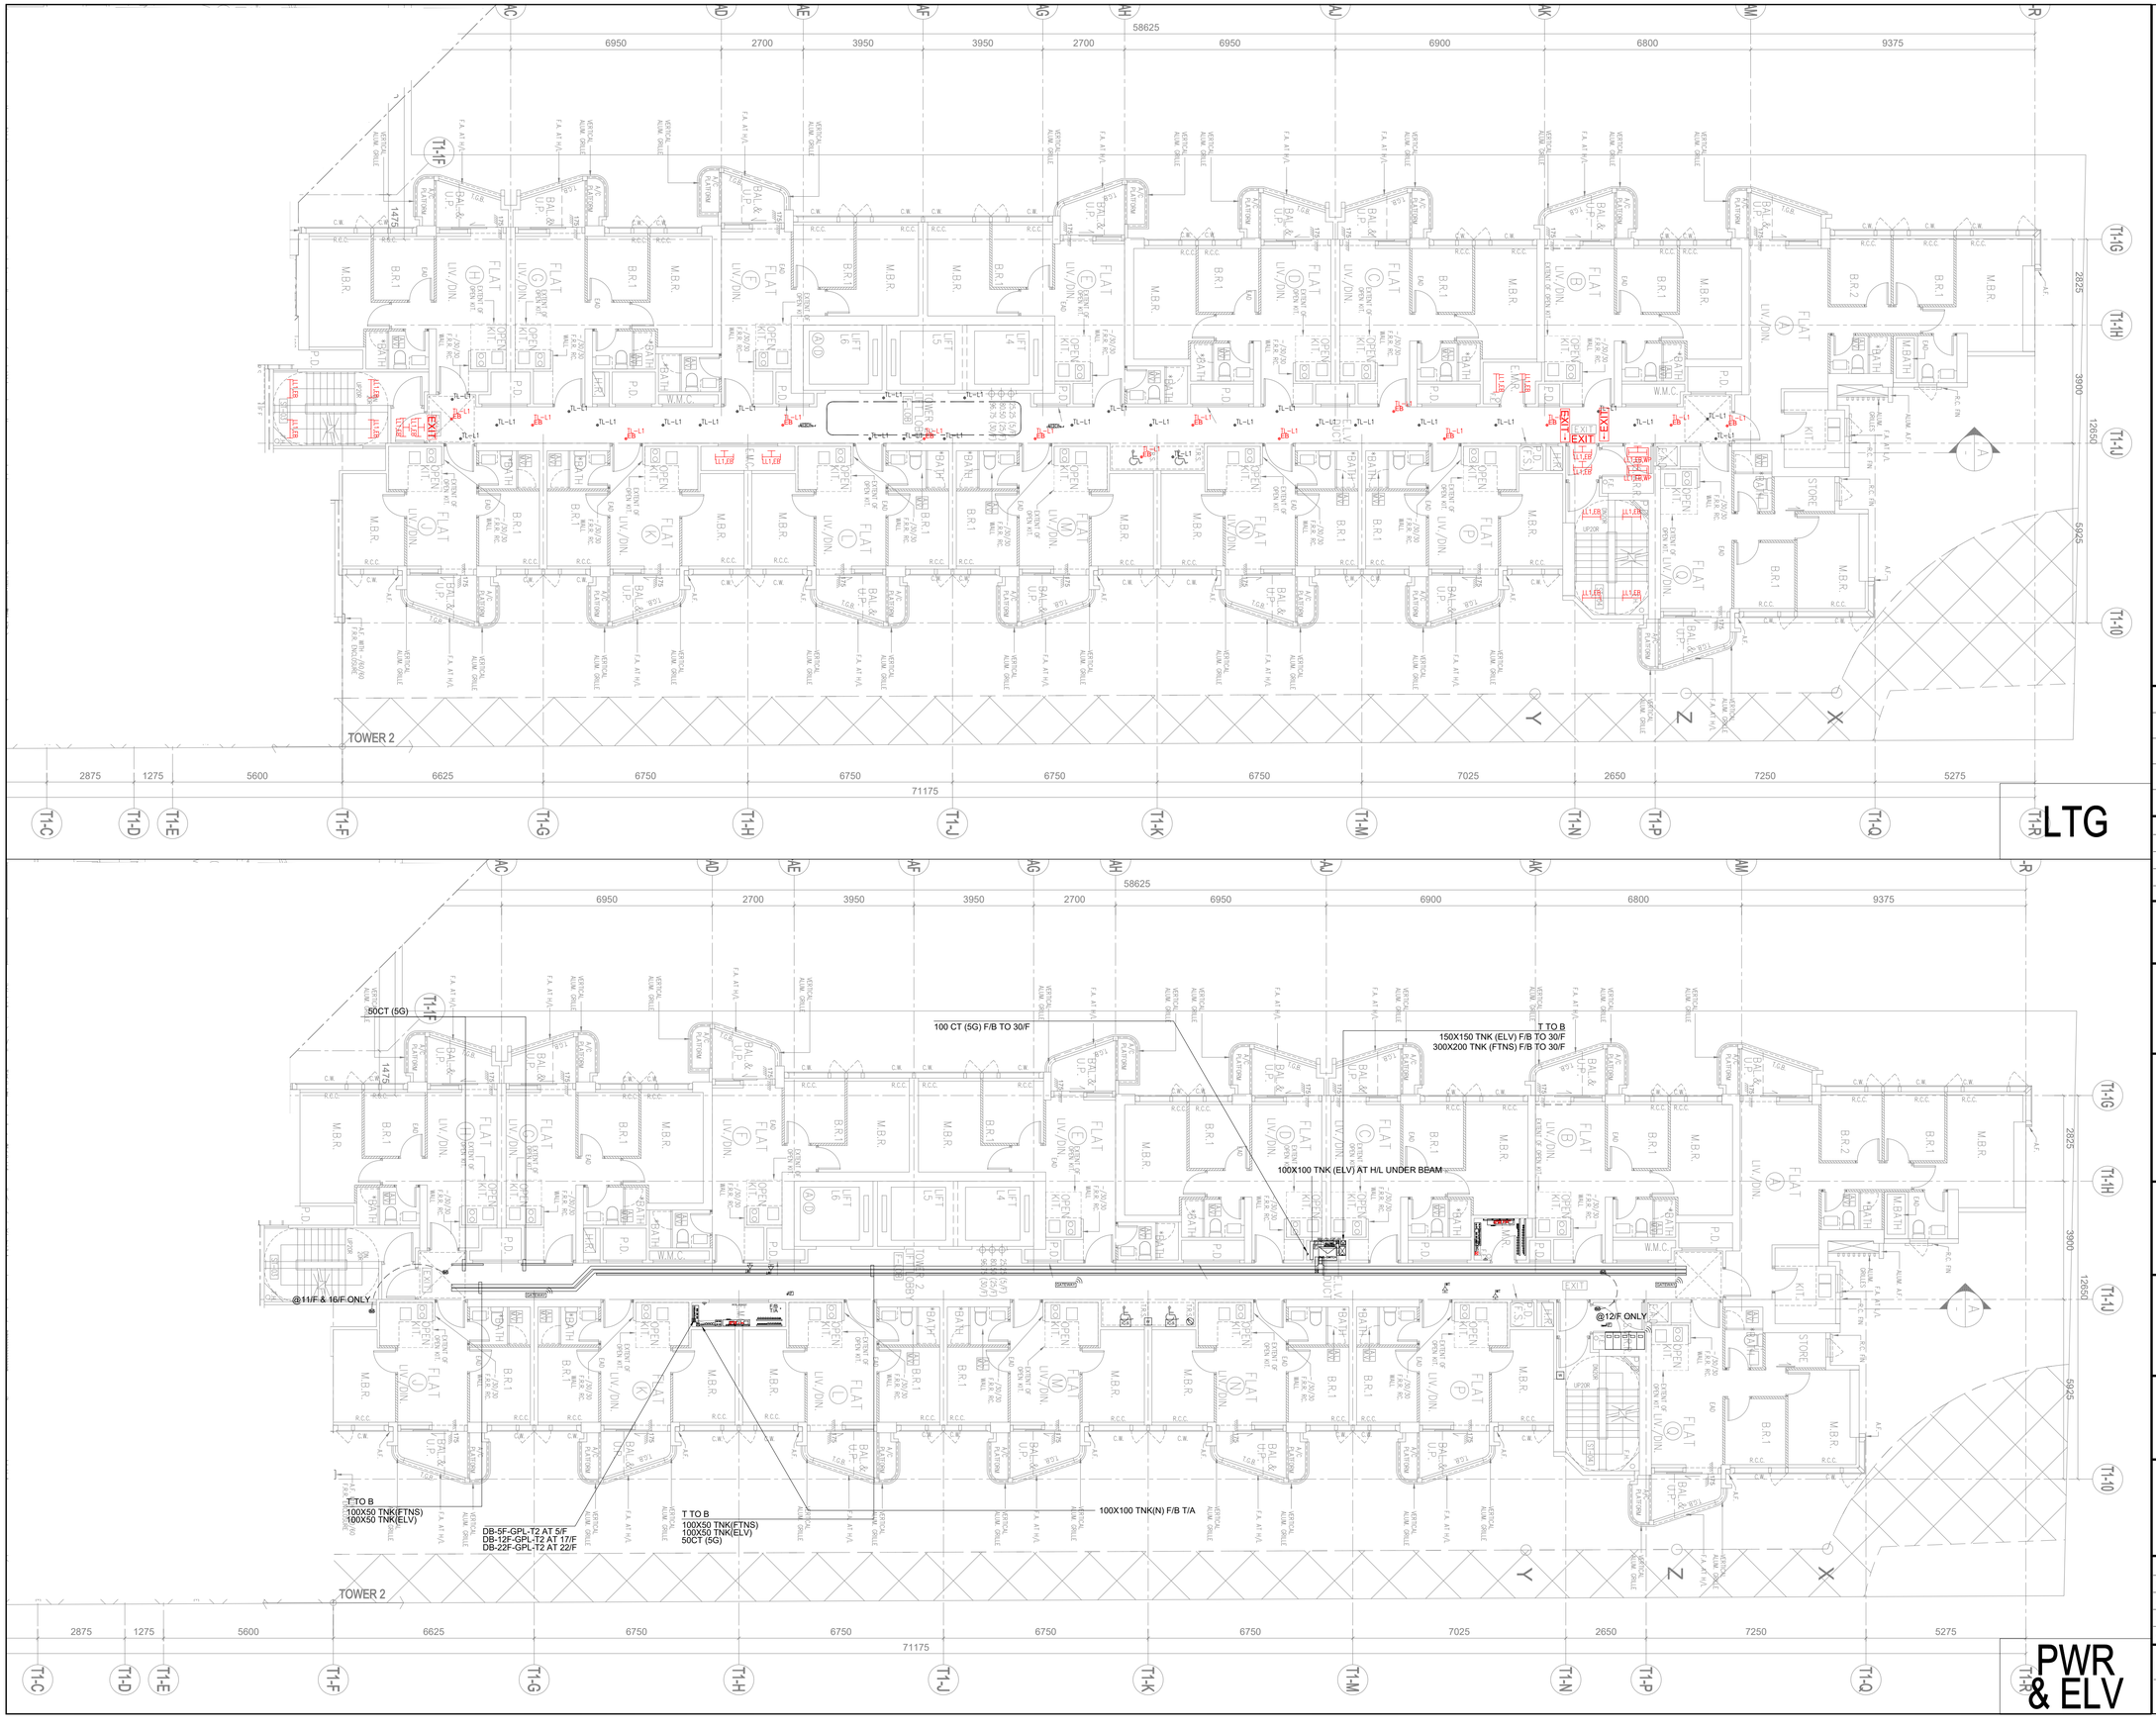


	"X"	"Y"
22/F TO 30/F	23F	22F
12/F TO 21/F	15F	12F
3/F TO 11/F	6F	5F

REV.	DESCRIPTION	BY	DATE
1	2nd SUBMISSION	WC	12/2025
0	1ST SUBMISSION	AC	12/2024

	DRAWING REFERENCE	REV.	DATE
ARCHITECTURAL	A/GBP/12 (9th AMENDMENT)	E	12/2025
STRUCTURAL			

CLIENT

NATION STAR DEVELOPMENT LIMITED

ARCHITECT

RONALD LU & PARTNERS

Ronald Lu & Partners (Hong Kong) Ltd.
呂元祥建築師事務所(香港)有限公司
33rd Floor, Wu Chung House,
213 Queen's Road East,
Wanchai, Hong Kong

CONSULTANT

wsp

7/F, One Kowloon
1 Wang Yuen Street
Kowloon Bay, Hong Kong

MAIN CONTRACTOR

中國海外房屋工程有限公司
CHINA OVERSEAS BUILDING CONSTRUCTION LIMITED

E & M CONTRACTOR

卓裕工程有限公司
U-Tech Engineering Company Limited
Member of Townpage Group
6/F, 100 TO KWA WAN ROAD, KOWLOON, HONG KONG
TEL : (852) 2765 - 5666 ; FAX : (852) 2392 - 7422

PROJECT

PROPOSED DEVELOPMENT AT BAILEY STREET & WING KWONG STREET, TO KWA WAN, KLN. INLAND LOT NO. 11279 (URA PROJECT KC-009)

TITLE

ENLARGED ELECTRICAL LAYOUT FOR 3/F TO 30/F PLAN OF TOWER 2

	NAME	INITIAL	DATE
DESIGNED BY	RONALD WONG		12/12/2025
DRAWN BY	AAREN CHU		12/12/2025
CHECKED BY	SAM KWOK		12/12/2025
APPROVED BY	WILSON YUEN		12/12/2025

DRAWING NO.
UT/KC009/EL/606

DATE (DD/MM/YY)
28/10/2026

REV.
1

STATUS

SCALE 1:100 @ A1

DO NOT SCALE THE DRAWING