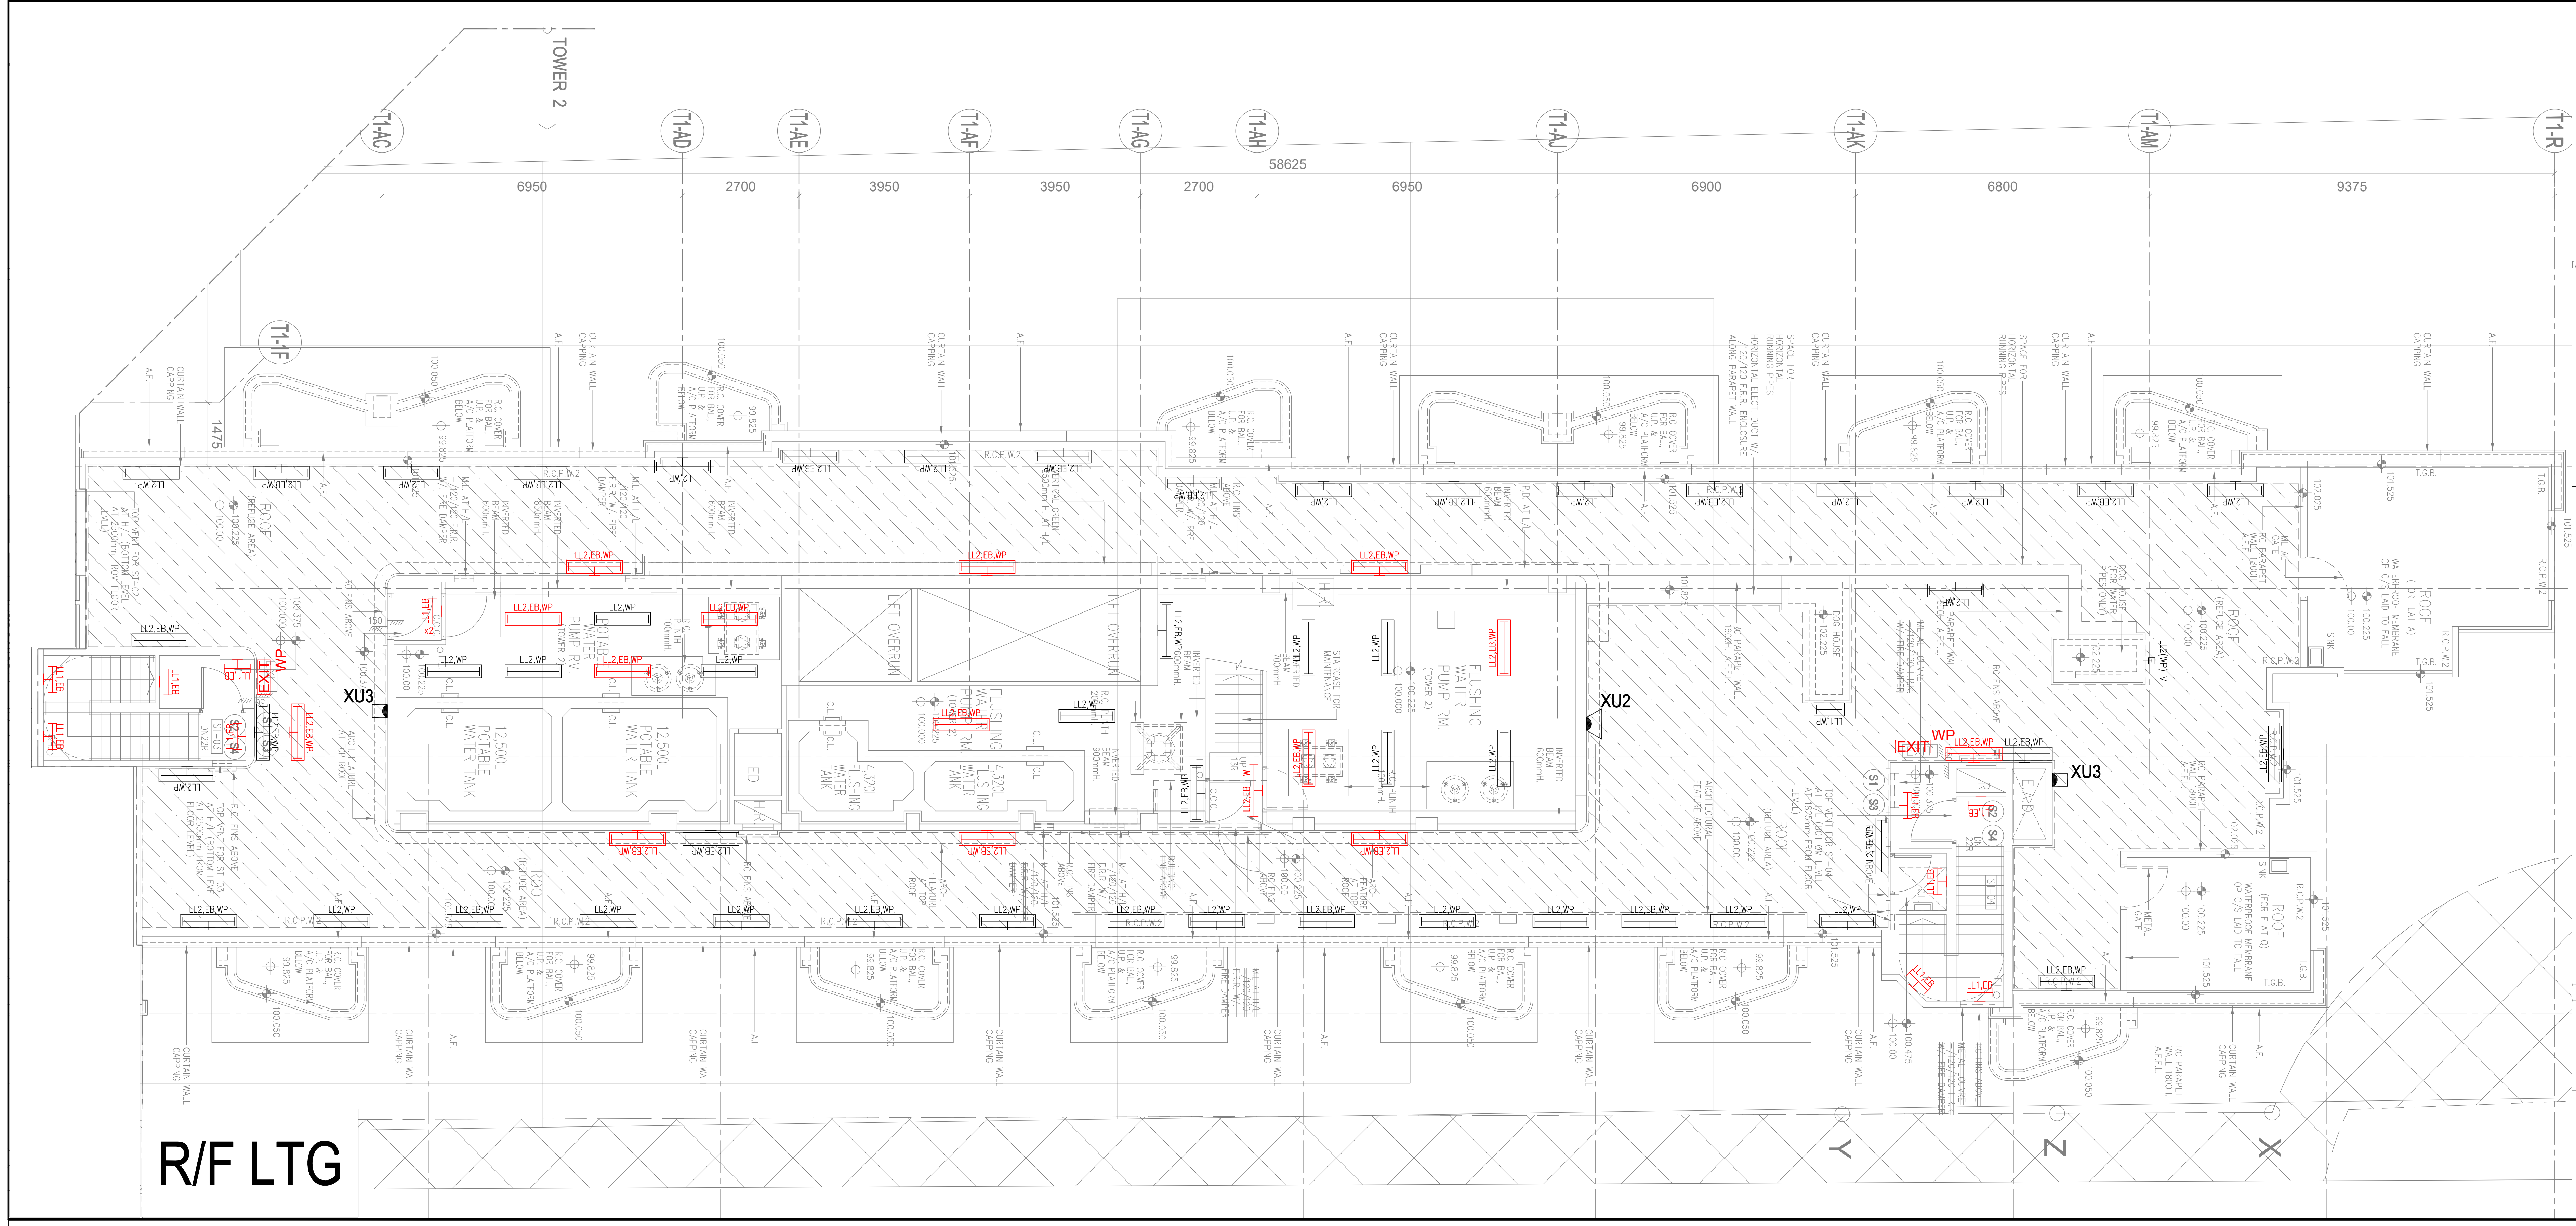

R/F LTG

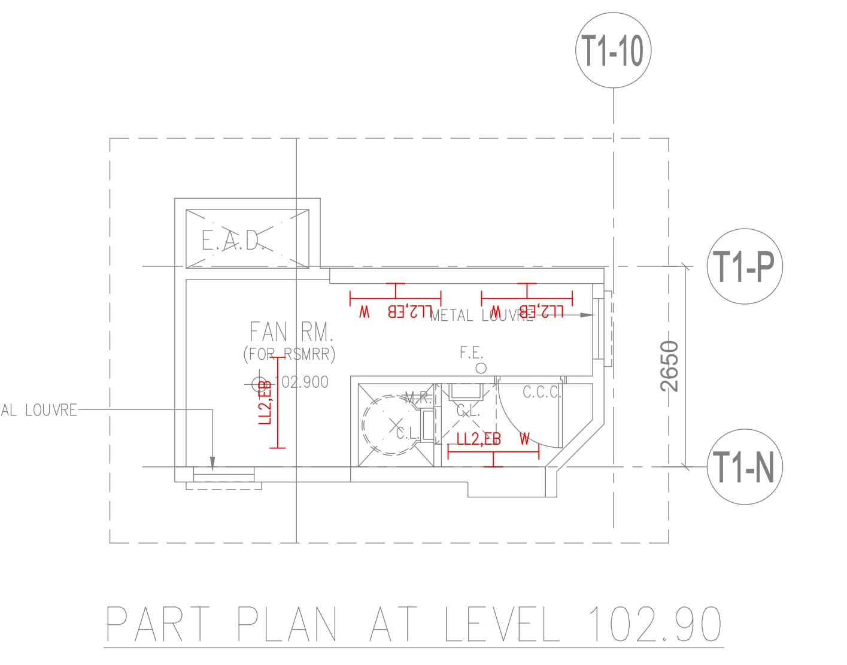

PART PLAN AT LEVEL 102.90

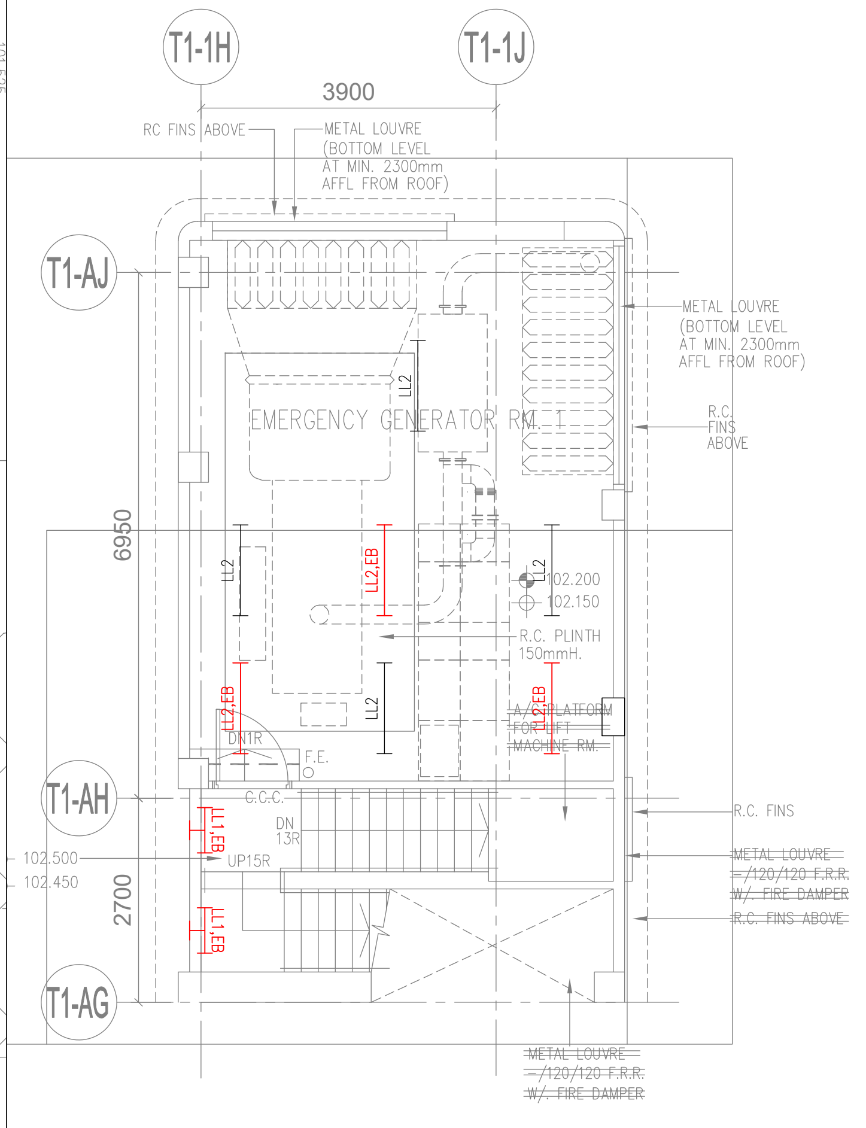

PART PLAN AT LEVEL 102.150

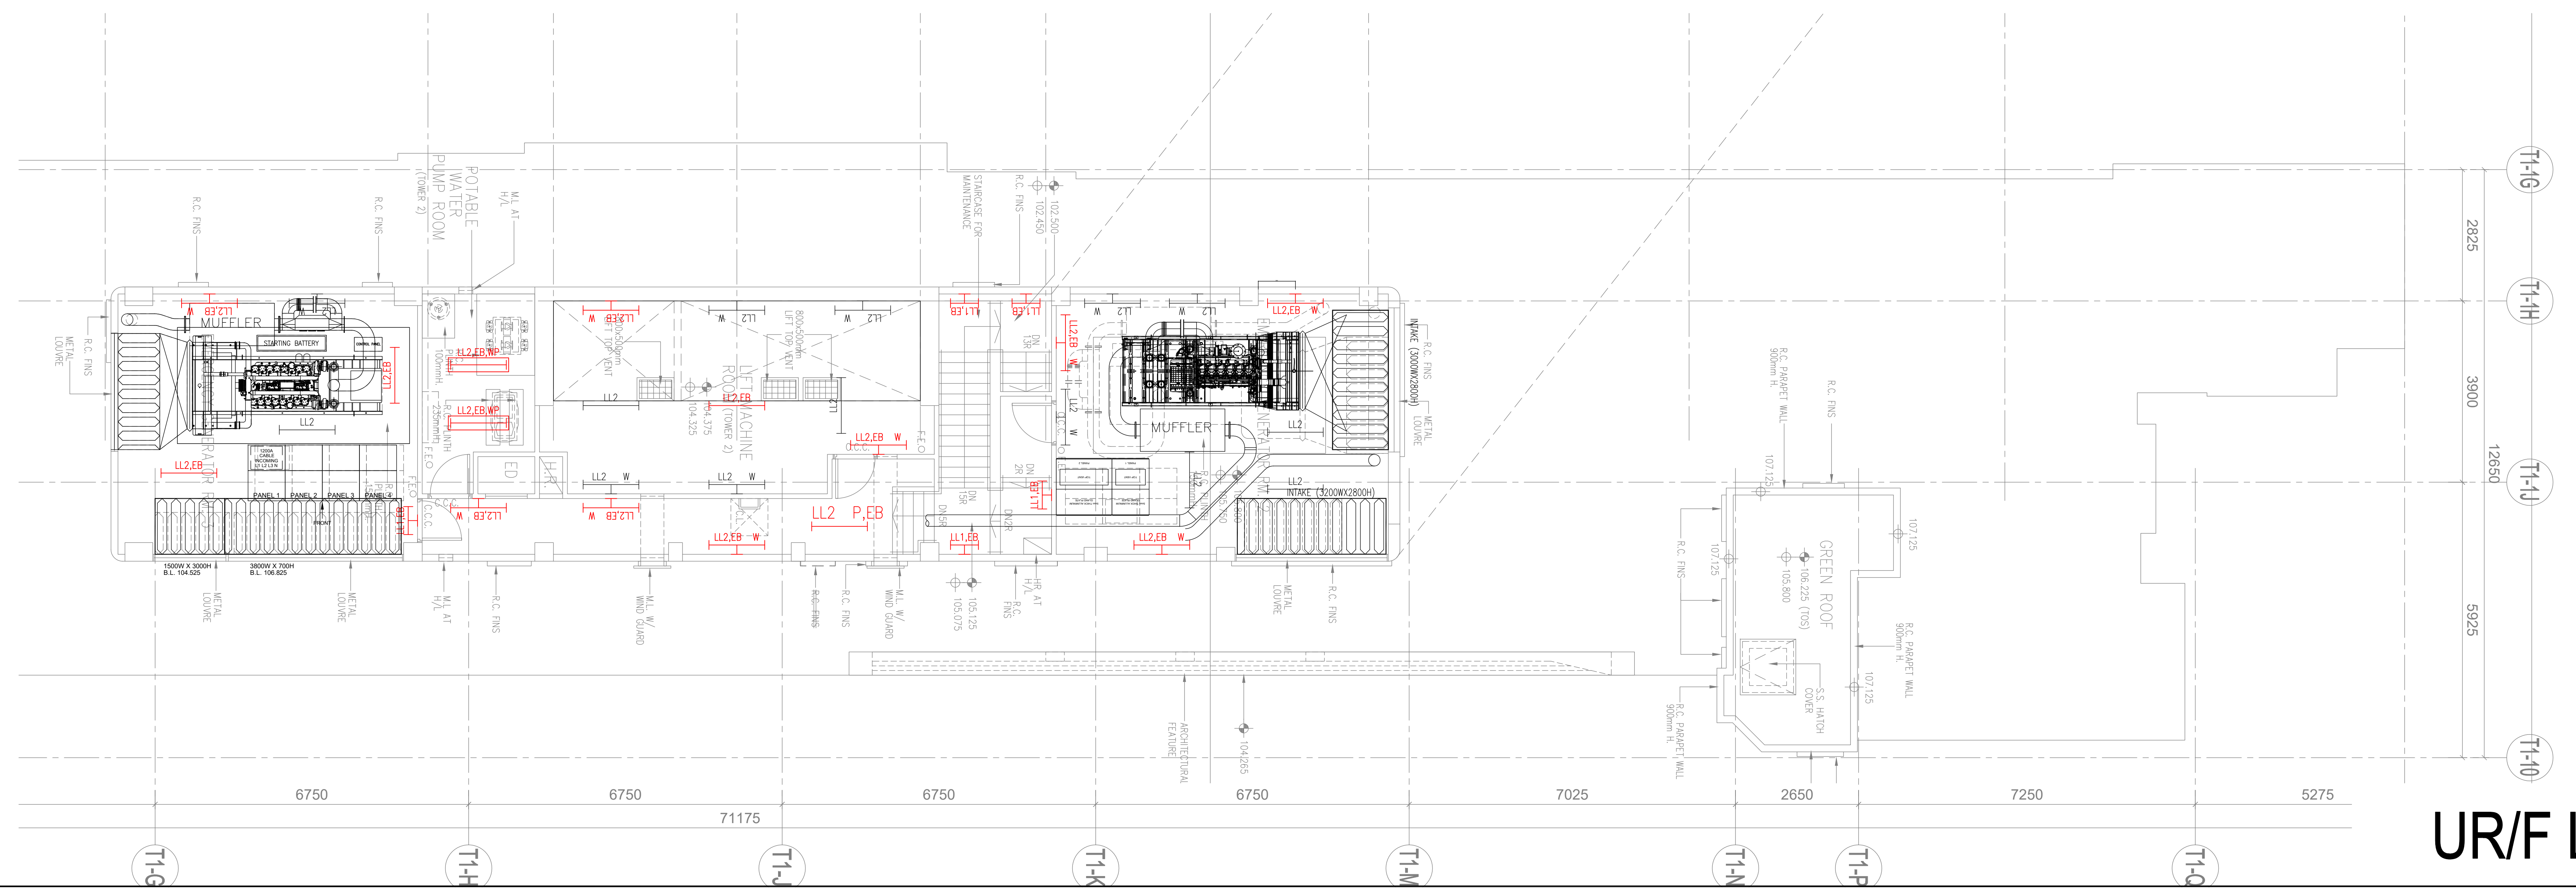

UR/F LTG

REV.	DESCRIPTION	BY	DATE
0	1ST SUBMISSION	AC	12/2024

	DRAWING REFERENCE	REV.	DATE
ARCHITECTURAL	A/GBP/12 (5TH AMENDMENT)	E	12/2024
STRUCTURAL			

CLIENT

NATION STAR DEVELOPMENT LIMITED

ARCHITECT

RONALD LU & PARTNERS

Ronald Lu & Partners (Hong Kong) Ltd.
呂元祥建築師事務所(香港)有限公司
33rd Floor, Wu Chung House,
213 Queen's Road East,
Wanchai, Hong Kong

CONSULTANT

wsp

7/F, One Kowloon
1 Wang Yuen Street
Kowloon Bay, Hong Kong

MAIN CONTRACTOR

中國海外房屋工程有限公司
CHINA OVERSEAS BUILDING CONSTRUCTION LIMITED

E & M CONTRACTOR

卓裕工程有限公司
U-Tech Engineering Company Limited
Member of Towngas Group
6/F, 100 TO KWA WAN ROAD, KOWLOON, HONG KONG
TEL : (852) 2765 – 5666 ; FAX : (852) 2392 – 7422

PROJECT

PROPOSED DEVELOPMENT AT BAILEY STREET
& WING KWONG STREET, TO KWA WAN, KLN.
INLAND LOT NO. 11279
(URA PROJECT KC-009)

TITLE

ELECTRICAL LIGHTING LAYOUT FOR
R/F & UR/F PLAN OF TOWER 2

	NAME	INITIAL	DATE
DESIGNED BY	RONALD WONG		30/12/2024
DRAWN BY	AAREN CHU		30/12/2024
CHECKED BY	SAM KWOK		30/12/2024
APPROVED BY	WILSON YUEN		30/12/2024

DRAWING NO.	DATE (DD/MM/YY)	REV.
UT/KC009/EL/607	31/10/2026	0
STATUS	SCALE 1:100 @ A1	
	DO NOT SCALE THE DRAWING	