
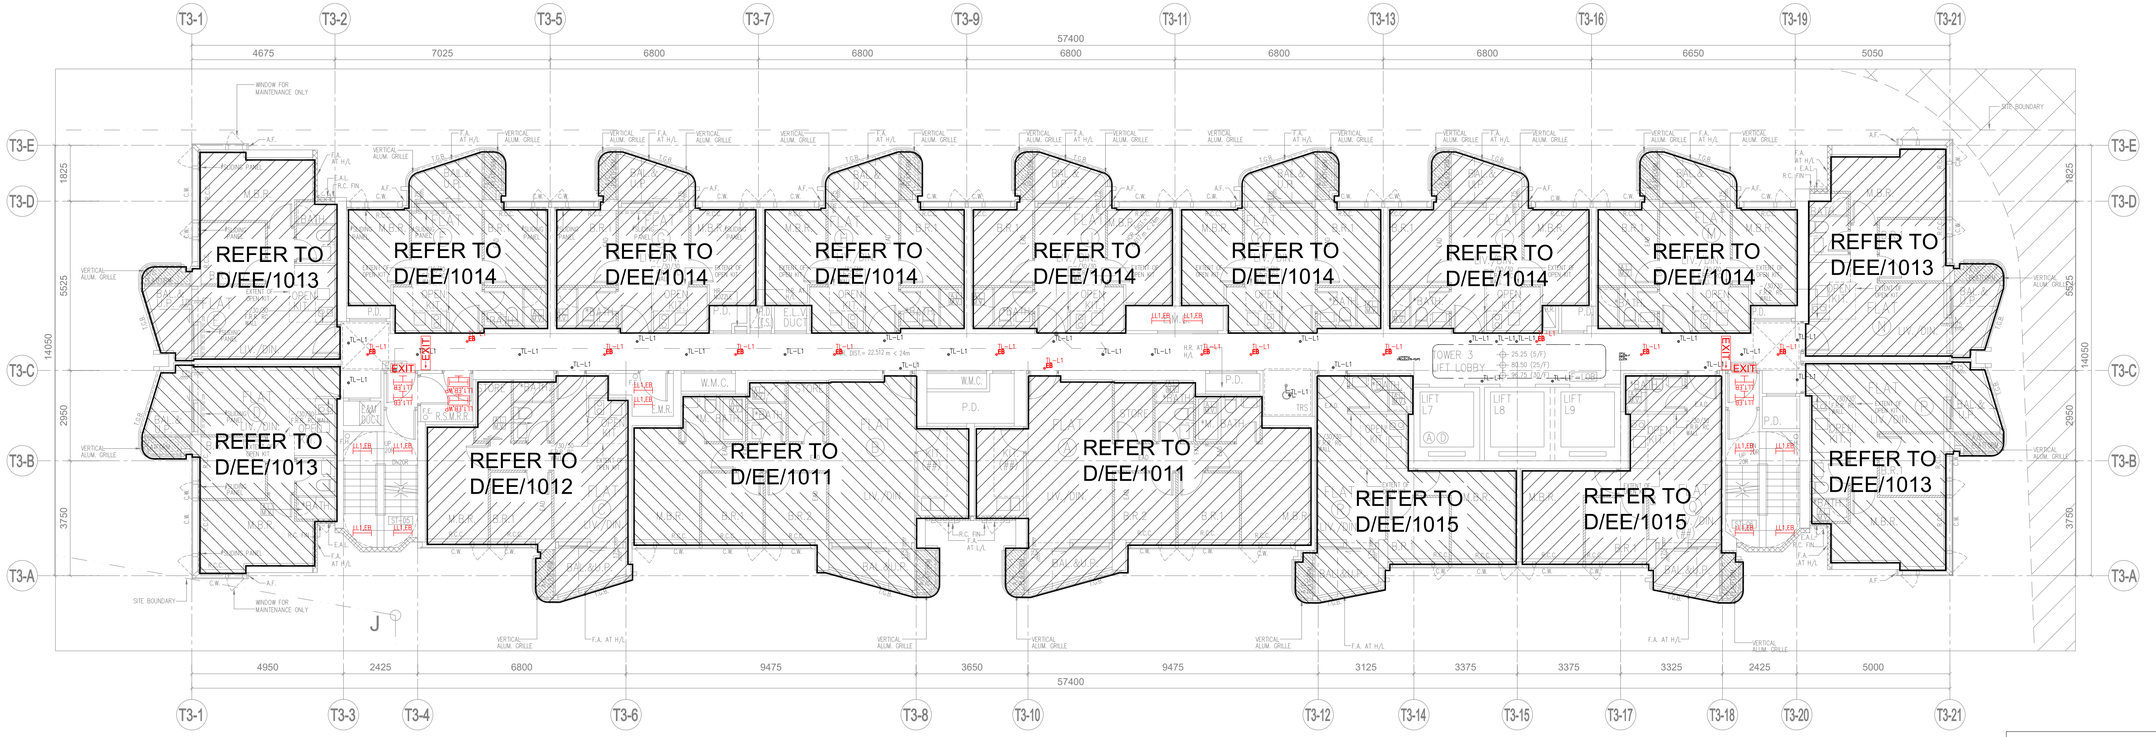


5TH TO 30TH FLOOR PLAN – TOWER 3
(23 STOREYS)

LTG

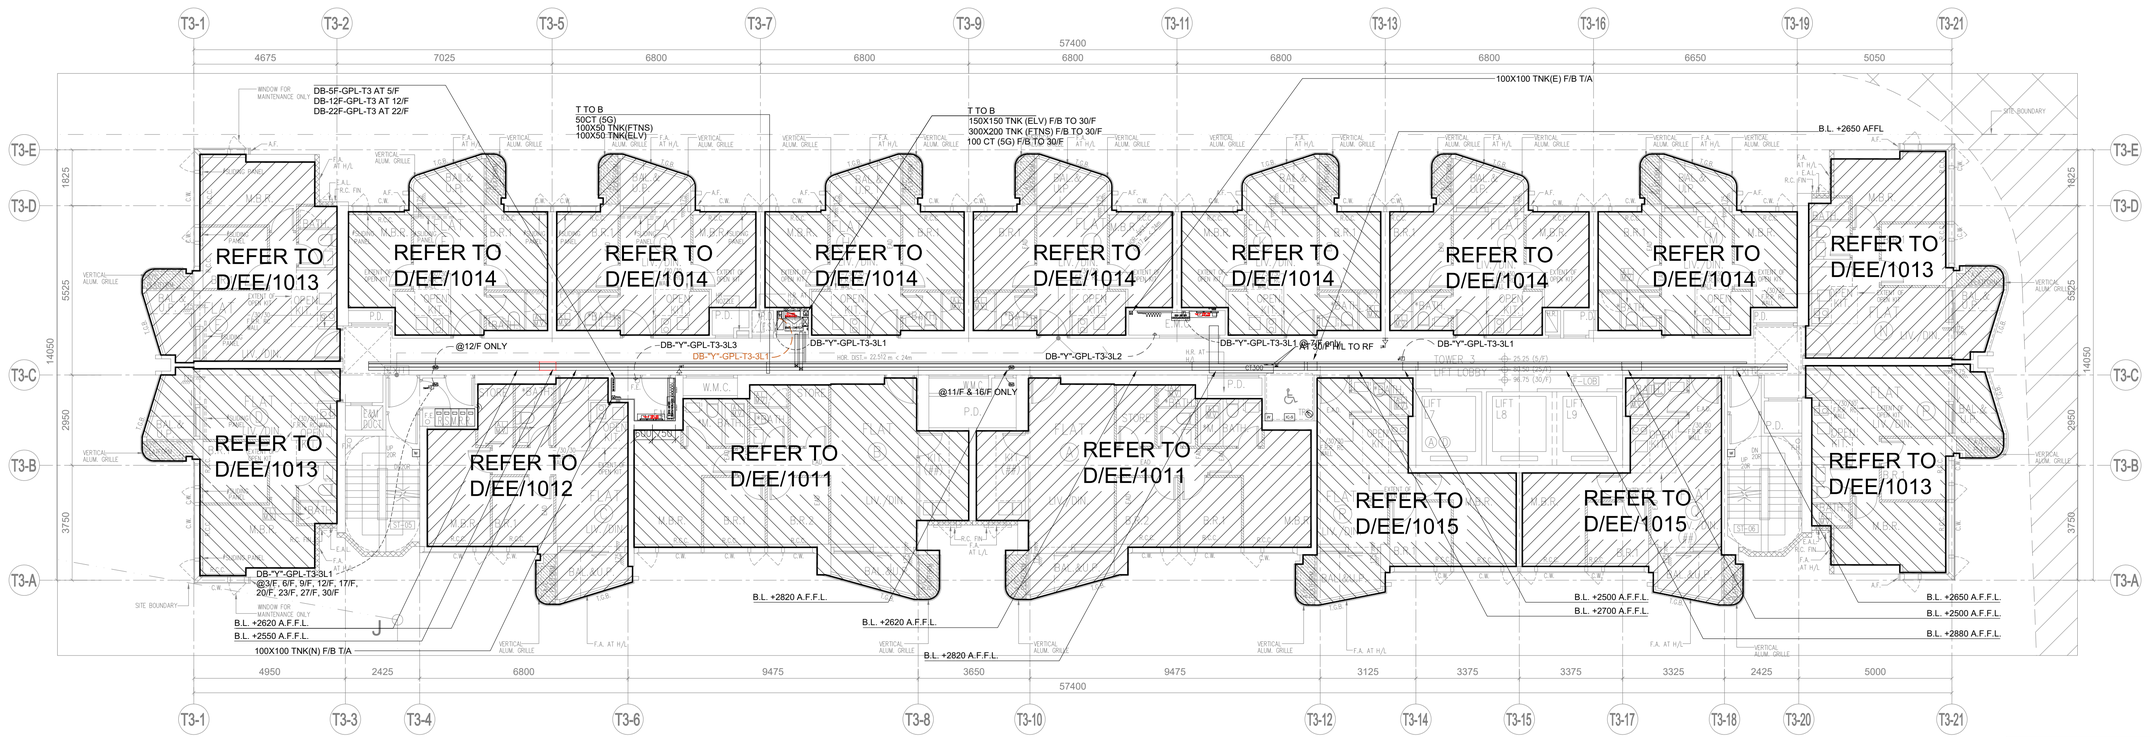

5TH TO 30TH FLOOR PLAN – TOWER 3
(23 STOREYS)

PWR & ELV

	"X"	"Y"
22/F TO 30/F	22F	22F
12/F TO 21/F	12F	12F
3/F TO 11/F	5F	5F

REV.	DESCRIPTION	BY	DATE
1	2nd SUBMISSION	WC	12/2025
0	1ST SUBMISSION	AC	01/2025

	DRAWING REFERENCE	REV.	DATE
ARCHITECTURAL	A/GBP/15 (9th AMENDMENT)	E	11/2025
STRUCTURAL			

CLIENT
NATION STAR DEVELOPMENT LIMITED

ARCHITECT
RONALD LU & PARTNERS
Ronald Lu & Partners (Hong Kong) Ltd.
呂元祥建築師事務所(香港)有限公司
33rd Floor, Wu Chung House,
213 Queen's Road East,
Wanchai, Hong Kong

CONSULTANT
wsp
7/F, One Kowloon
1 Wang Yuen Street
Kowloon Bay, Hong Kong

MAIN CONTRACTOR
中國海外房屋工程有限公司
CHINA OVERSEAS BUILDING CONSTRUCTION LIMITED

E & M CONTRACTOR
卓裕工程有限公司
U-Tech Engineering Company Limited
Member of Townpark Group
6/F., 100 TO KWA WAN ROAD, KOWLOON, HONG KONG.
TEL : (852) 2765 – 5666 ; FAX : (852) 2392 – 7422

PROJECT
PROPOSED DEVELOPMENT AT BAILEY STREET & WING KWONG STREET, TO KWA WAN, KLN.
INLAND LOT NO. 11279
(URA PROJECT KC-009)

TITLE
ENLARGED ELECTRICAL LAYOUT
FOR 3/F TO 30/F PLAN OF TOWER 3

	NAME	INITIAL	DATE
DESIGNED BY	RONALD WONG		12/12/2025
DRAWN BY	AAREN CHU		12/12/2025
CHECKED BY	SAM KWOK		12/12/2025
APPROVED BY	WILSON YUEN		12/12/2025

DRAWING NO.	DATE (DD/MM/YY)	REV.
UT/KC009/EL/610	28/10/2026	1
STATUS	SCALE 1:100 @ A1	
	DO NOT SCALE THE DRAWING	