
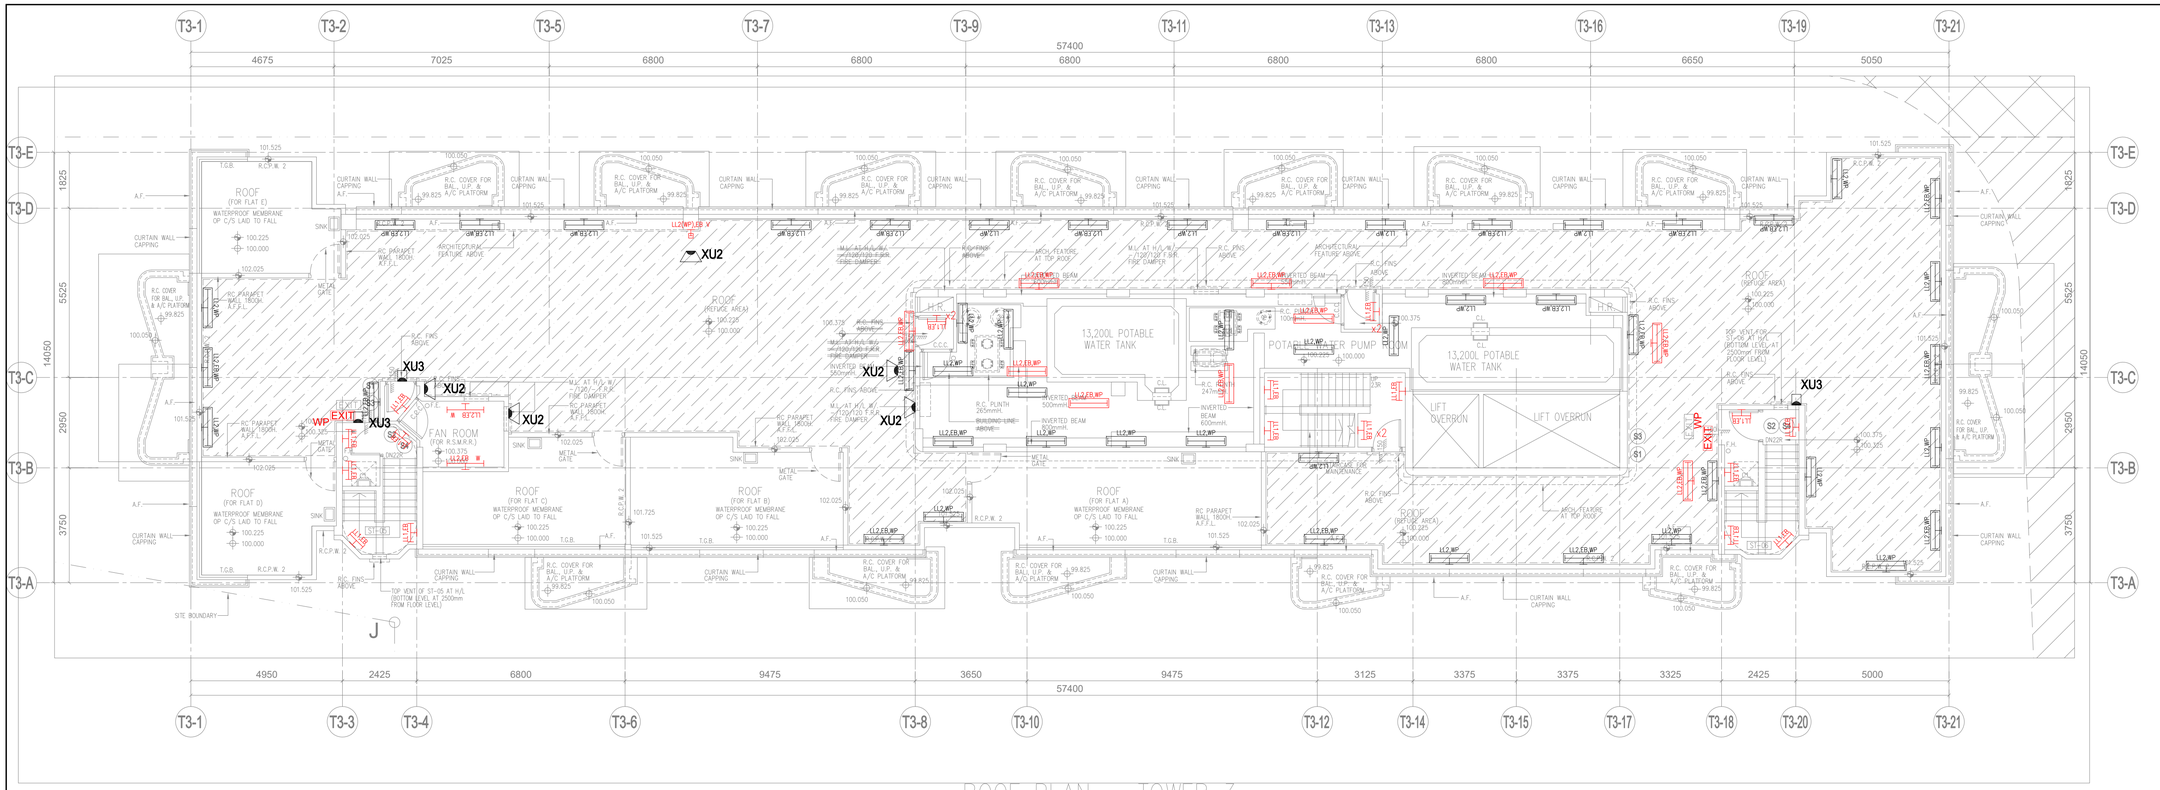


ROOF PLAN – TOWER 3

LEGEND:

(S1) REFUGE FLOOR NOTICE

(S2) STAIR NO. SIGN

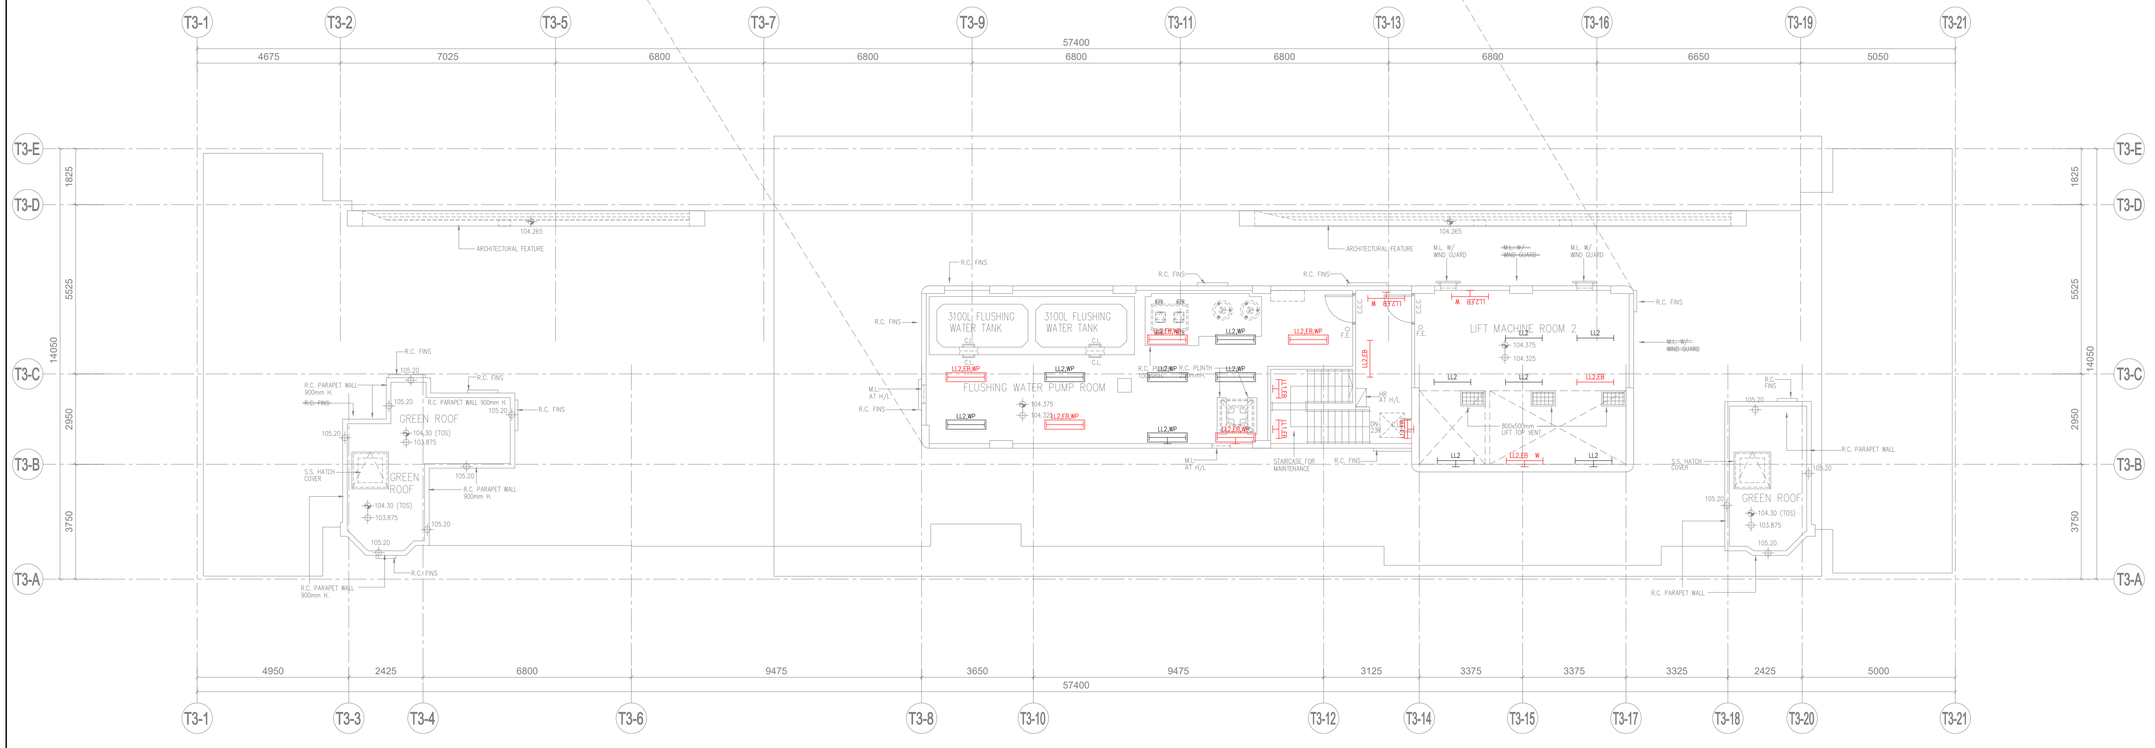

UPPER ROOF PLAN – TOWER 3

LEGEND :

L1.1/B, L1.1/B	600mm SINGLE BATTEN T5 LED FITTING, BUILT-IN LED DRIVER, CEILING / WALL MOUNTED TYPE WITH ESSENTIAL POWER
L1.1/BWP, L1.1/BWP	600mm SINGLE BATTEN T5 LED FITTING, BUILT-IN LED DRIVER, WATERPROOF TYPE, CEILING / WALL MOUNTED TYPE WITH ESSENTIAL POWER
L1.2, L1.2	1200mm SINGLE BATTEN T5 LED FITTING, BUILT-IN LED DRIVER, CEILING / WALL MOUNTED TYPE
L1.2/B, L1.2/B	1200mm SINGLE BATTEN T5 LED FITTING, BUILT-IN LED DRIVER, WATERPROOF TYPE, CEILING / WALL MOUNTED TYPE WITH ESSENTIAL POWER
L1.2/BWP, L1.2/BWP	1200mm SINGLE BATTEN T5 LED FITTING, BUILT-IN LED DRIVER, WATERPROOF TYPE, CEILING / WALL MOUNTED TYPE
L1.2/BWP, L1.2/BWP	1200mm SINGLE BATTEN T5 LED FITTING, BUILT-IN LED DRIVER, WATERPROOF TYPE, CEILING / WALL MOUNTED TYPE WITH ESSENTIAL POWER
EXIT	HIGH LEVEL EXIT SIGN
EXIT / EXIT	HIGH LEVEL DIRECTIONAL SIGN
	10A 1-WAY SINGLE POLE LIGHTING SWITCH AT 1350mm A.F.F.L. UNLESS OTHERWISE SPECIFIED
	10A 1-WAY SINGLE POLE WEATHERPROOF LIGHTING SWITCH AT 1350mm A.F.F.L. UNLESS OTHERWISE SPECIFIED

ABBREVIATIONS :

E	ESSENTIAL POWER FROM EMERGENCY GENERATOR TO BE PROVIDED
B	BATTERY KIT FOR 2-HOURS
WP	WATERPROOF TYPE, IP65 UNLESS OTHERWISE SPECIFY
P	PENDANT TYPE, 2600 AFFL OR COORDINATION ON SITE
W	WALL MOUNTED TYPE, 2350 AFFL OR COORDINATION ON SITE

	"X"	"Y"
22/F TO 30/F	27F	26F
12/F TO 21/F	18F	17F
3/F TO 11/F	8F	7F

REV.	DESCRIPTION	BY	DATE
0	1ST SUBMISSION	AC	6/2025

	DRAWING REFERENCE	REV.	DATE
ARCHITECTURAL	A/GBP/16 (8th AMENDMENT)	F	5/2025
STRUCTURAL			

CLIENT

NATION STAR DEVELOPMENT LIMITED

ARCHITECT

RONALD LU & PARTNERS

Ronald Lu & Partners (Hong Kong) Ltd.
呂元祥建築師事務所(香港)有限公司
33rd Floor, Wu Chung House,
213 Queen's Road East,
Wanchai, Hong Kong

CONSULTANT

wsp

7/F, One Kowloon
1 Wang Yuen Street
Kowloon Bay, Hong Kong

MAIN CONTRACTOR

中國海外房屋工程有限公司
CHINA OVERSEAS BUILDING CONSTRUCTION LIMITED

E & M CONTRACTOR

卓裕工程有限公司
U-Tech Engineering Company Limited
Member of Townpoint Group
6/F, 100 TO KWA WAN ROAD, KOWLOON, HONG KONG
TEL : (852) 2765 – 5666 ; FAX : (852) 2392 – 7422

PROJECT

PROPOSED DEVELOPMENT AT BAILEY STREET & WING KWONG STREET, TO KWA WAN, KLN.
INLAND LOT NO. 11279
(URA PROJECT KC-009)

TITLE

ELECTRICAL LIGHTING LAYOUT FOR R/F TO UR/F PLAN OF TOWER 3

	NAME	INITIAL	DATE
DESIGNED BY	RONALD WONG		18/6/2025
DRAWN BY	AAREN CHU		18/6/2025
CHECKED BY	SAM KWOK		18/6/2025
APPROVED BY	WILSON YUEN		18/6/2025

DRAWING NO.	DATE (DD/MM/YY)	REV.
D/EE/611	31/10/2026	0
STATUS	SCALE 1:100 @ A1	
	DO NOT SCALE THE DRAWING	