
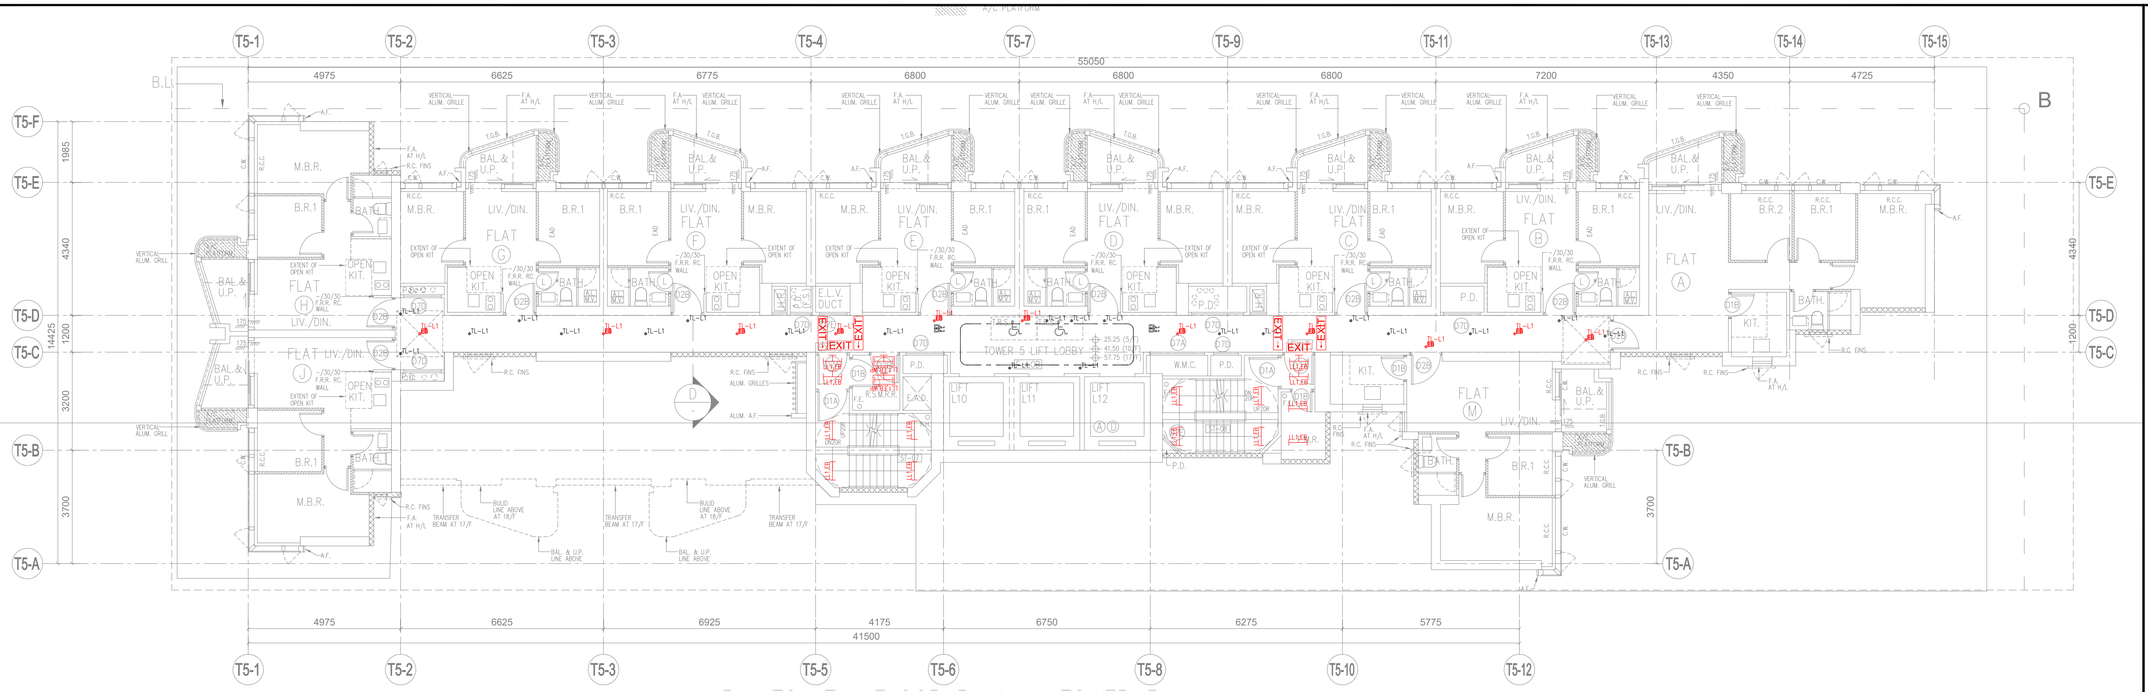


3/F TO 17/F

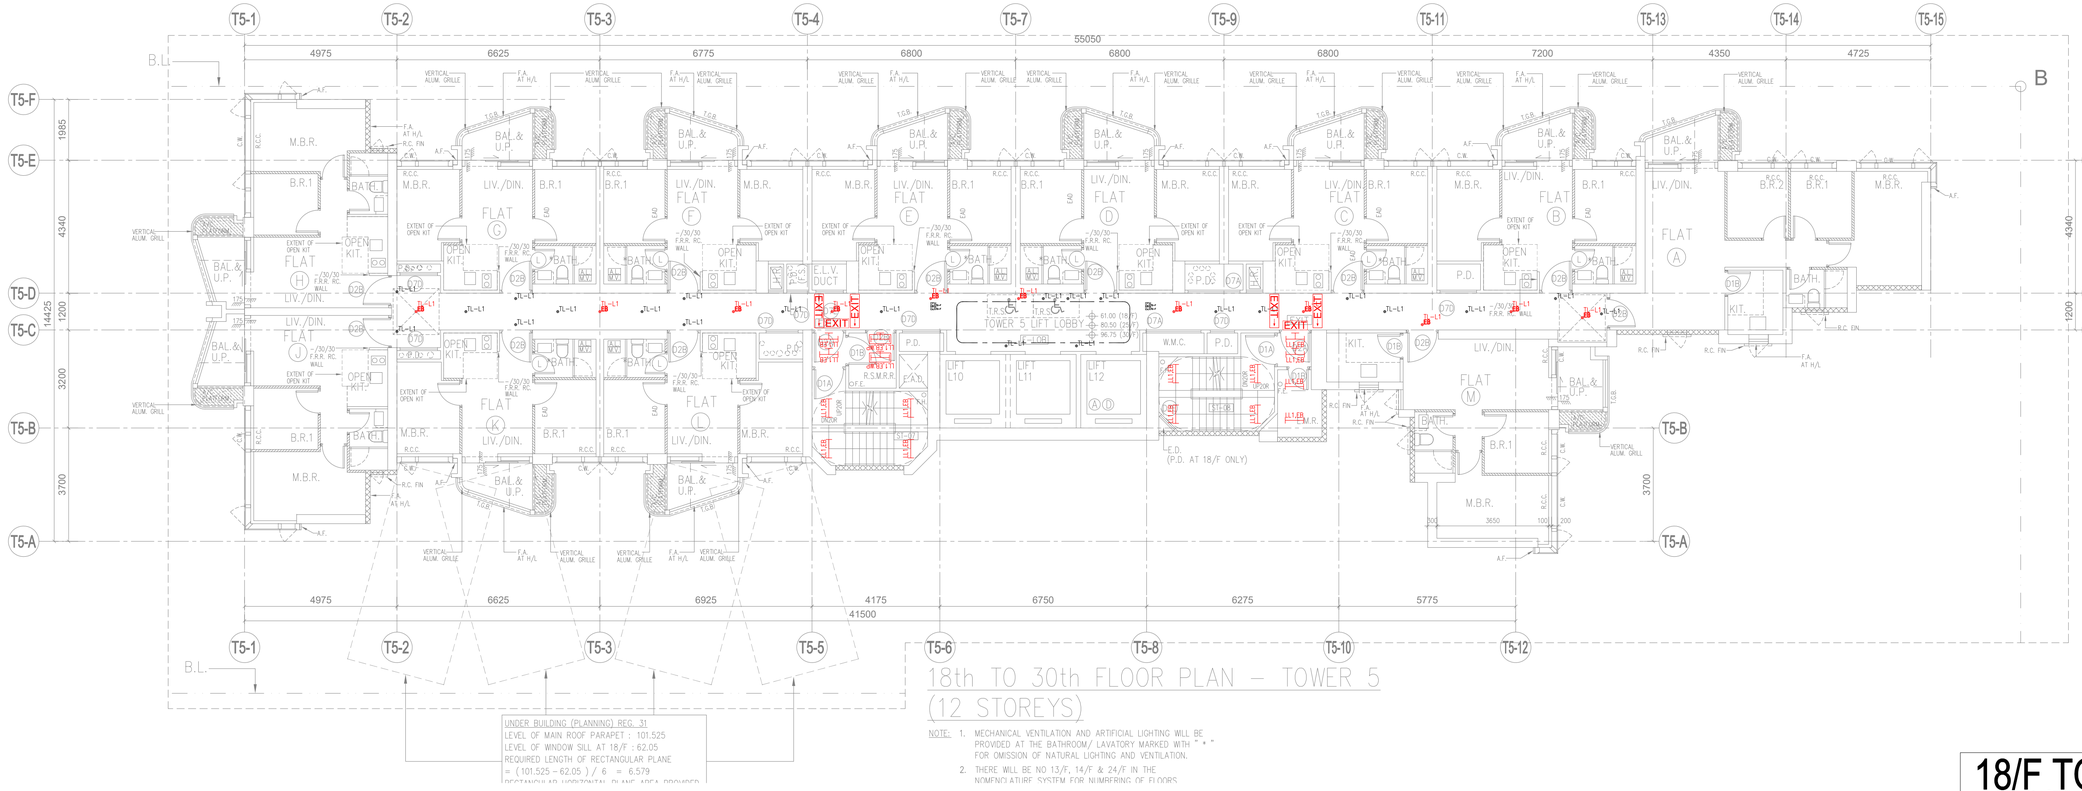

18/F TO 30/F

UNDER BUILDING (PLANNING) REG. 31
LEVEL OF MAIN ROOF PARAPET : 101.525
LEVEL OF WINDOW SILL AT 18/F : 62.05
REQUIRED LENGTH OF RECTANGULAR PLANE
= (101.525 – 62.05) / 6 = 6.579

18th TO 30th FLOOR PLAN – TOWER 5
(12 STOREYS)

NOTE:
1. MECHANICAL VENTILATION AND ARTIFICIAL LIGHTING WILL BE PROVIDED AT THE BATHROOM/ LAVATORY MARKED WITH " • " FOR OMISSION OF NATURAL LIGHTING AND VENTILATION.
2. THERE WILL BE NO 13/F, 14/F & 24/F IN THE NOMENCLATURE SYSTEM FOR NUMBERING OF FLOORS

	"X"	"Y"
22/F TO 30/F	23F	22F
12/F TO 21/F	15F	12F
3/F TO 11/F	6F	5F

REV.	DESCRIPTION	BY	DATE
1	2nd SUBMISSION	WC	12/2025
0	1ST SUBMISSION	AC	01/2025

	DRAWING REFERENCE	REV.	DATE
ARCHITECTURAL	A/GBP/17 (9th AMENDMENT)	F	12/2025
STRUCTURAL			

CLIENT
NATION STAR DEVELOPMENT LIMITED

ARCHITECT
RONALD LU & PARTNERS
Ronald Lu & Partners (Hong Kong) Ltd.
呂元祥建築師事務所(香港)有限公司
33rd Floor, Wu Chung House,
213 Queen's Road East,
Wanchai, Hong Kong

CONSULTANT
wsp
7/F, One Kowloon
1 Wang Yuen Street
Kowloon Bay, Hong Kong

MAIN CONTRACTOR
中國海外房屋工程有限公司
CHINA OVERSEAS BUILDING CONSTRUCTION LIMITED

E & M CONTRACTOR
卓 裕 工 程 有 限 公 司
U-Tech Engineering Company Limited
Member of Towngas Group
6/F., 100 TO KWA WAN ROAD, KOWLOON, HONG KONG
TEL : (852) 2765 – 5666 ; FAX : (852) 2392 – 7422

PROJECT
PROPOSED DEVELOPMENT AT BAILEY STREET & WING KWONG STREET, TO KWA WAN, KLN.
INLAND LOT NO. 11279
(URA PROJECT KC-009)

TITLE
ELECTRICAL LIGHTING LAYOUT FOR 3/F TO 30/F PLAN OF TOWER 5

	NAME	INITIAL	DATE
DESIGNED BY	RONALD WONG		12/12/2025
DRAWN BY	AAREN CHU		12/12/2025
CHECKED BY	SAM KWOK		12/12/2025
APPROVED BY	WILSON YUEN		12/12/2025

DRAWING NO. UT/KC009/EL/614
DATE (DD/MM/YY) 28/10/2026
REV. 1
STATUS
SCALE 1:100 @ A1
DO NOT SCALE THE DRAWING