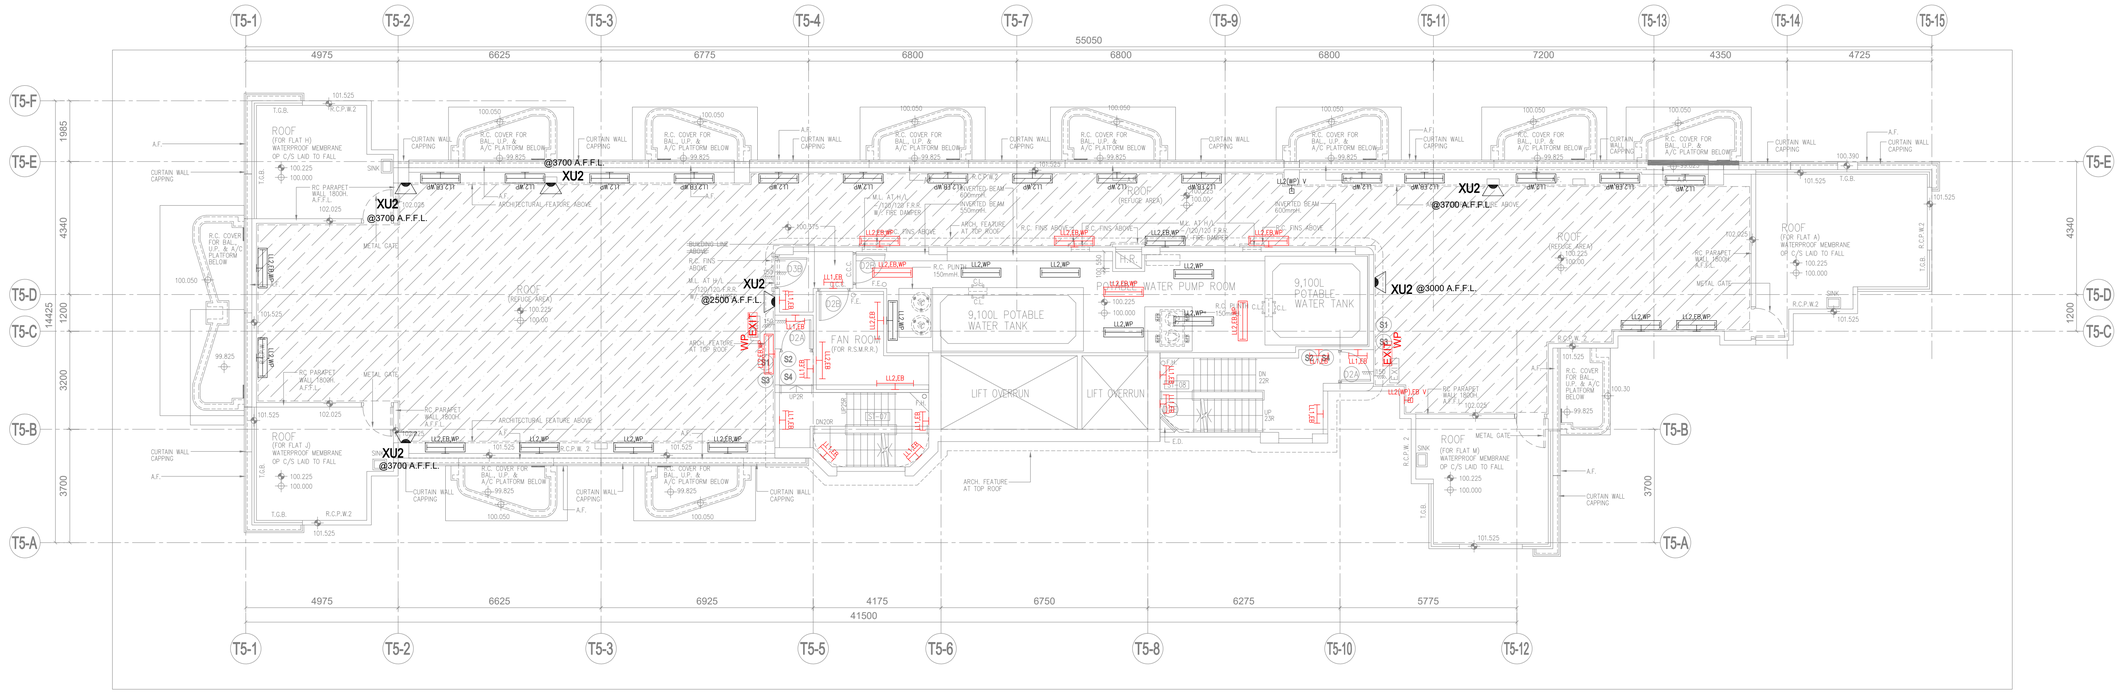



ROOF PLAN – TOWER 5

LEGEND:

(S1) REFUGE FLOOR NOTICE

(S2) STAIR NO. SIGN

(S3) DIRECTIONAL SIGN TO EXIT STAIRCASE

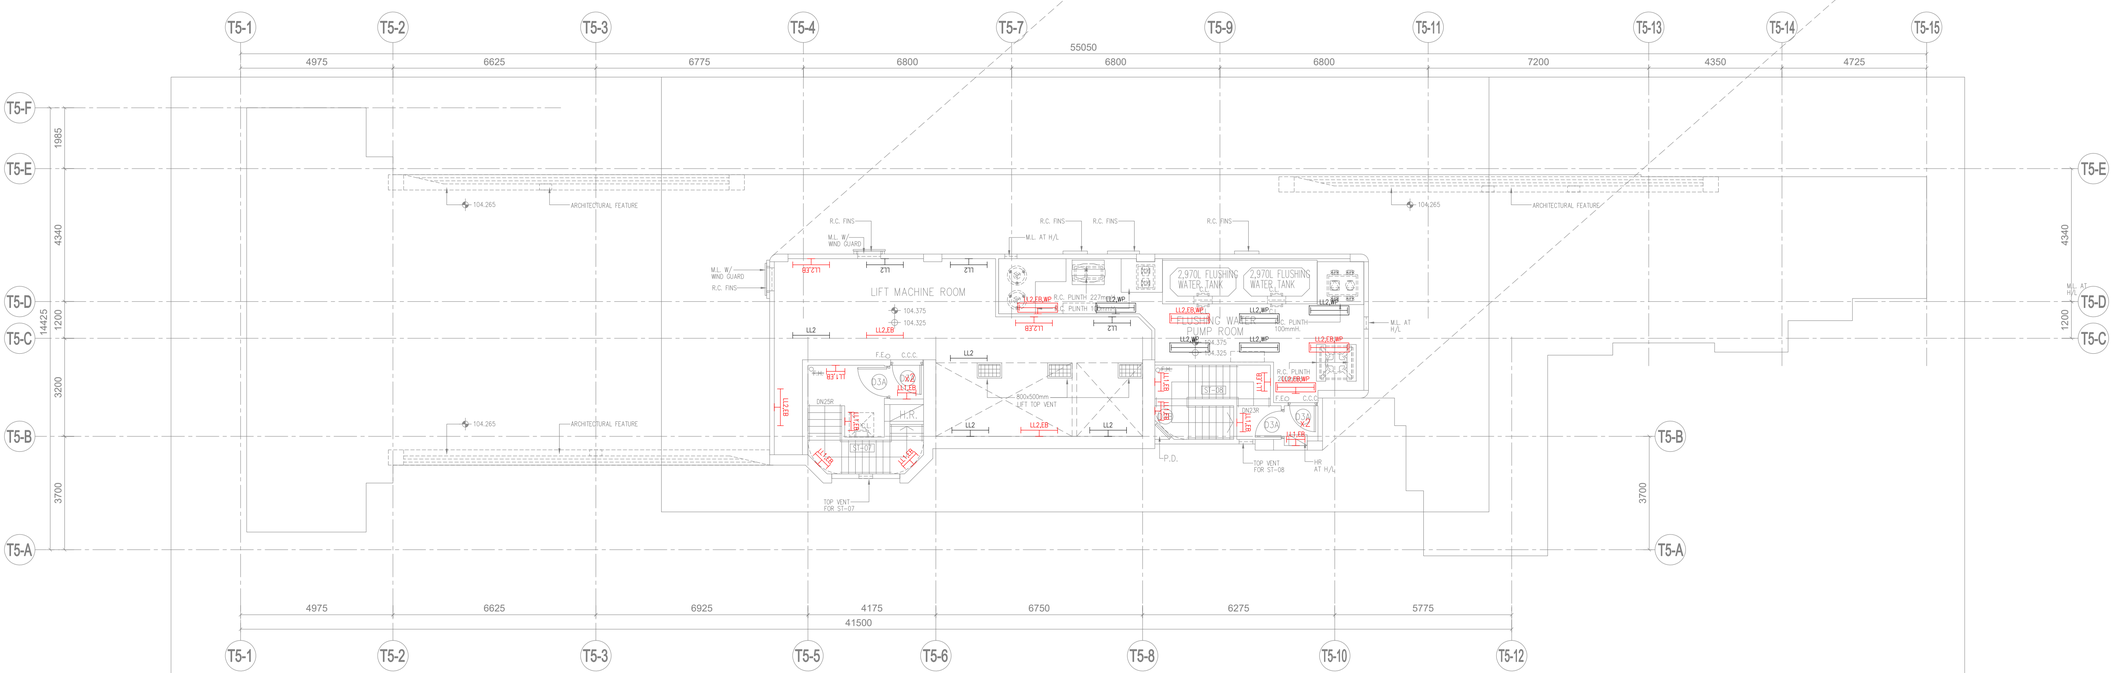

UPPER ROOF PLAN – TOWER 5

LEGEND :

L1 / L1.EB	600mm SINGLE BATTEN T5 LED FITTING, BUILT-IN LED DRIVER, CEILING / WALL MOUNTED TYPE WITH ESSENTIAL POWER
L1.EB.WP / L1.EB.WP	600mm SINGLE BATTEN T5 LED FITTING, BUILT-IN LED DRIVER, WATERPROOF TYPE, CEILING / WALL MOUNTED TYPE WITH ESSENTIAL POWER
L12 / L12	1200mm SINGLE BATTEN T5 LED FITTING, BUILT-IN LED DRIVER, CEILING / WALL MOUNTED TYPE
L12.EB / L12.EB	1200mm SINGLE BATTEN T5 LED FITTING, BUILT-IN LED DRIVER, CEILING / WALL MOUNTED TYPE WITH ESSENTIAL POWER
L12.WP / L12.WP	1200mm SINGLE BATTEN T5 LED FITTING, BUILT-IN LED DRIVER, WATERPROOF TYPE, CEILING / WALL MOUNTED TYPE
L12.EB.WP / L12.EB.WP	1200mm SINGLE BATTEN T5 LED FITTING, BUILT-IN LED DRIVER, WATERPROOF TYPE, CEILING / WALL MOUNTED TYPE WITH ESSENTIAL POWER
EXIT	HIGH LEVEL EXIT SIGN
EXIT / EXIT	HIGH LEVEL DIRECTIONAL SIGN
	10A 1-WAY SINGLE POLE LIGHTING SWITCH AT 1350mm A.F.F.L. UNLESS OTHERWISE SPECIFIED
	10A 1-WAY SINGLE POLE WEATHERPROOF LIGHTING SWITCH AT 1350mm A.F.F.L. UNLESS OTHERWISE SPECIFIED

ABBREVIATIONS :

E	ESSENTIAL POWER FROM EMERGENCY GENERATOR TO BE PROVIDED
B	BATTERY KIT FOR 2-HOURS
WP	WATERPROOF TYPE, IP65 UNLESS OTHERWISE SPECIFY
P	PENDANT TYPE, 2600 AFFL OR COORDINATION ON SITE
W	WALL MOUNTED TYPE, 2350 AFFL OR COORDINATION ON SITE

	"X"	"Y"
22/F TO 30/F	23F	22F
12/F TO 21/F	15F	12F
3/F TO 11/F	6F	5F

REV.	DESCRIPTION	BY	DATE
0	1ST SUBMISSION	AC	6/2025

	DRAWING REFERENCE	REV.	DATE
ARCHITECTURAL	A/GBP/18 (8th AMENDMENT)	F	5/2025
STRUCTURAL			

CLIENT
NATION STAR DEVELOPMENT LIMITED

ARCHITECT
RONALD LU & PARTNERS
Ronald Lu & Partners (Hong Kong) Ltd.
呂元祥建築師事務所(香港)有限公司
33rd Floor, Wu Chung House,
213 Queen's Road East,
Wanchai, Hong Kong

CONSULTANT
wsp
7/F, One Kowloon
1 Wang Yuen Street
Kowloon Bay, Hong Kong

MAIN CONTRACTOR
中國海外房屋工程有限公司
CHINA OVERSEAS BUILDING CONSTRUCTION LIMITED

E & M CONTRACTOR
卓裕工程有限公司
U-Tech Engineering Company Limited
Member of Towngas Group
6/F., 100 TO KWA WAN ROAD, KOWLOON, HONG KONG
TEL : (852) 2765 – 5666 ; FAX : (852) 2392 – 7422

PROJECT
PROPOSED DEVELOPMENT AT BAILEY STREET & WING KWONG STREET, TO KWA WAN, KLN.
INLAND LOT NO. 11279
(URA PROJECT KC-009)

TITLE
ELECTRICAL LIGHTING LAYOUT FOR R/F TO UR/F PLAN OF TOWER 5

	NAME	INITIAL	DATE
DESIGNED BY	RONALD WONG		18/6/2025
DRAWN BY	AAREN CHU		18/6/2025
CHECKED BY	SAM KWOK		18/6/2025
APPROVED BY	WILSON YUEN		18/6/2025

DRAWING NO.	DATE (DD/MM/YY)	REV.
D/EE/616	31/10/2026	0
STATUS	SCALE 1:100 @ A1	
	DO NOT SCALE THE DRAWING	