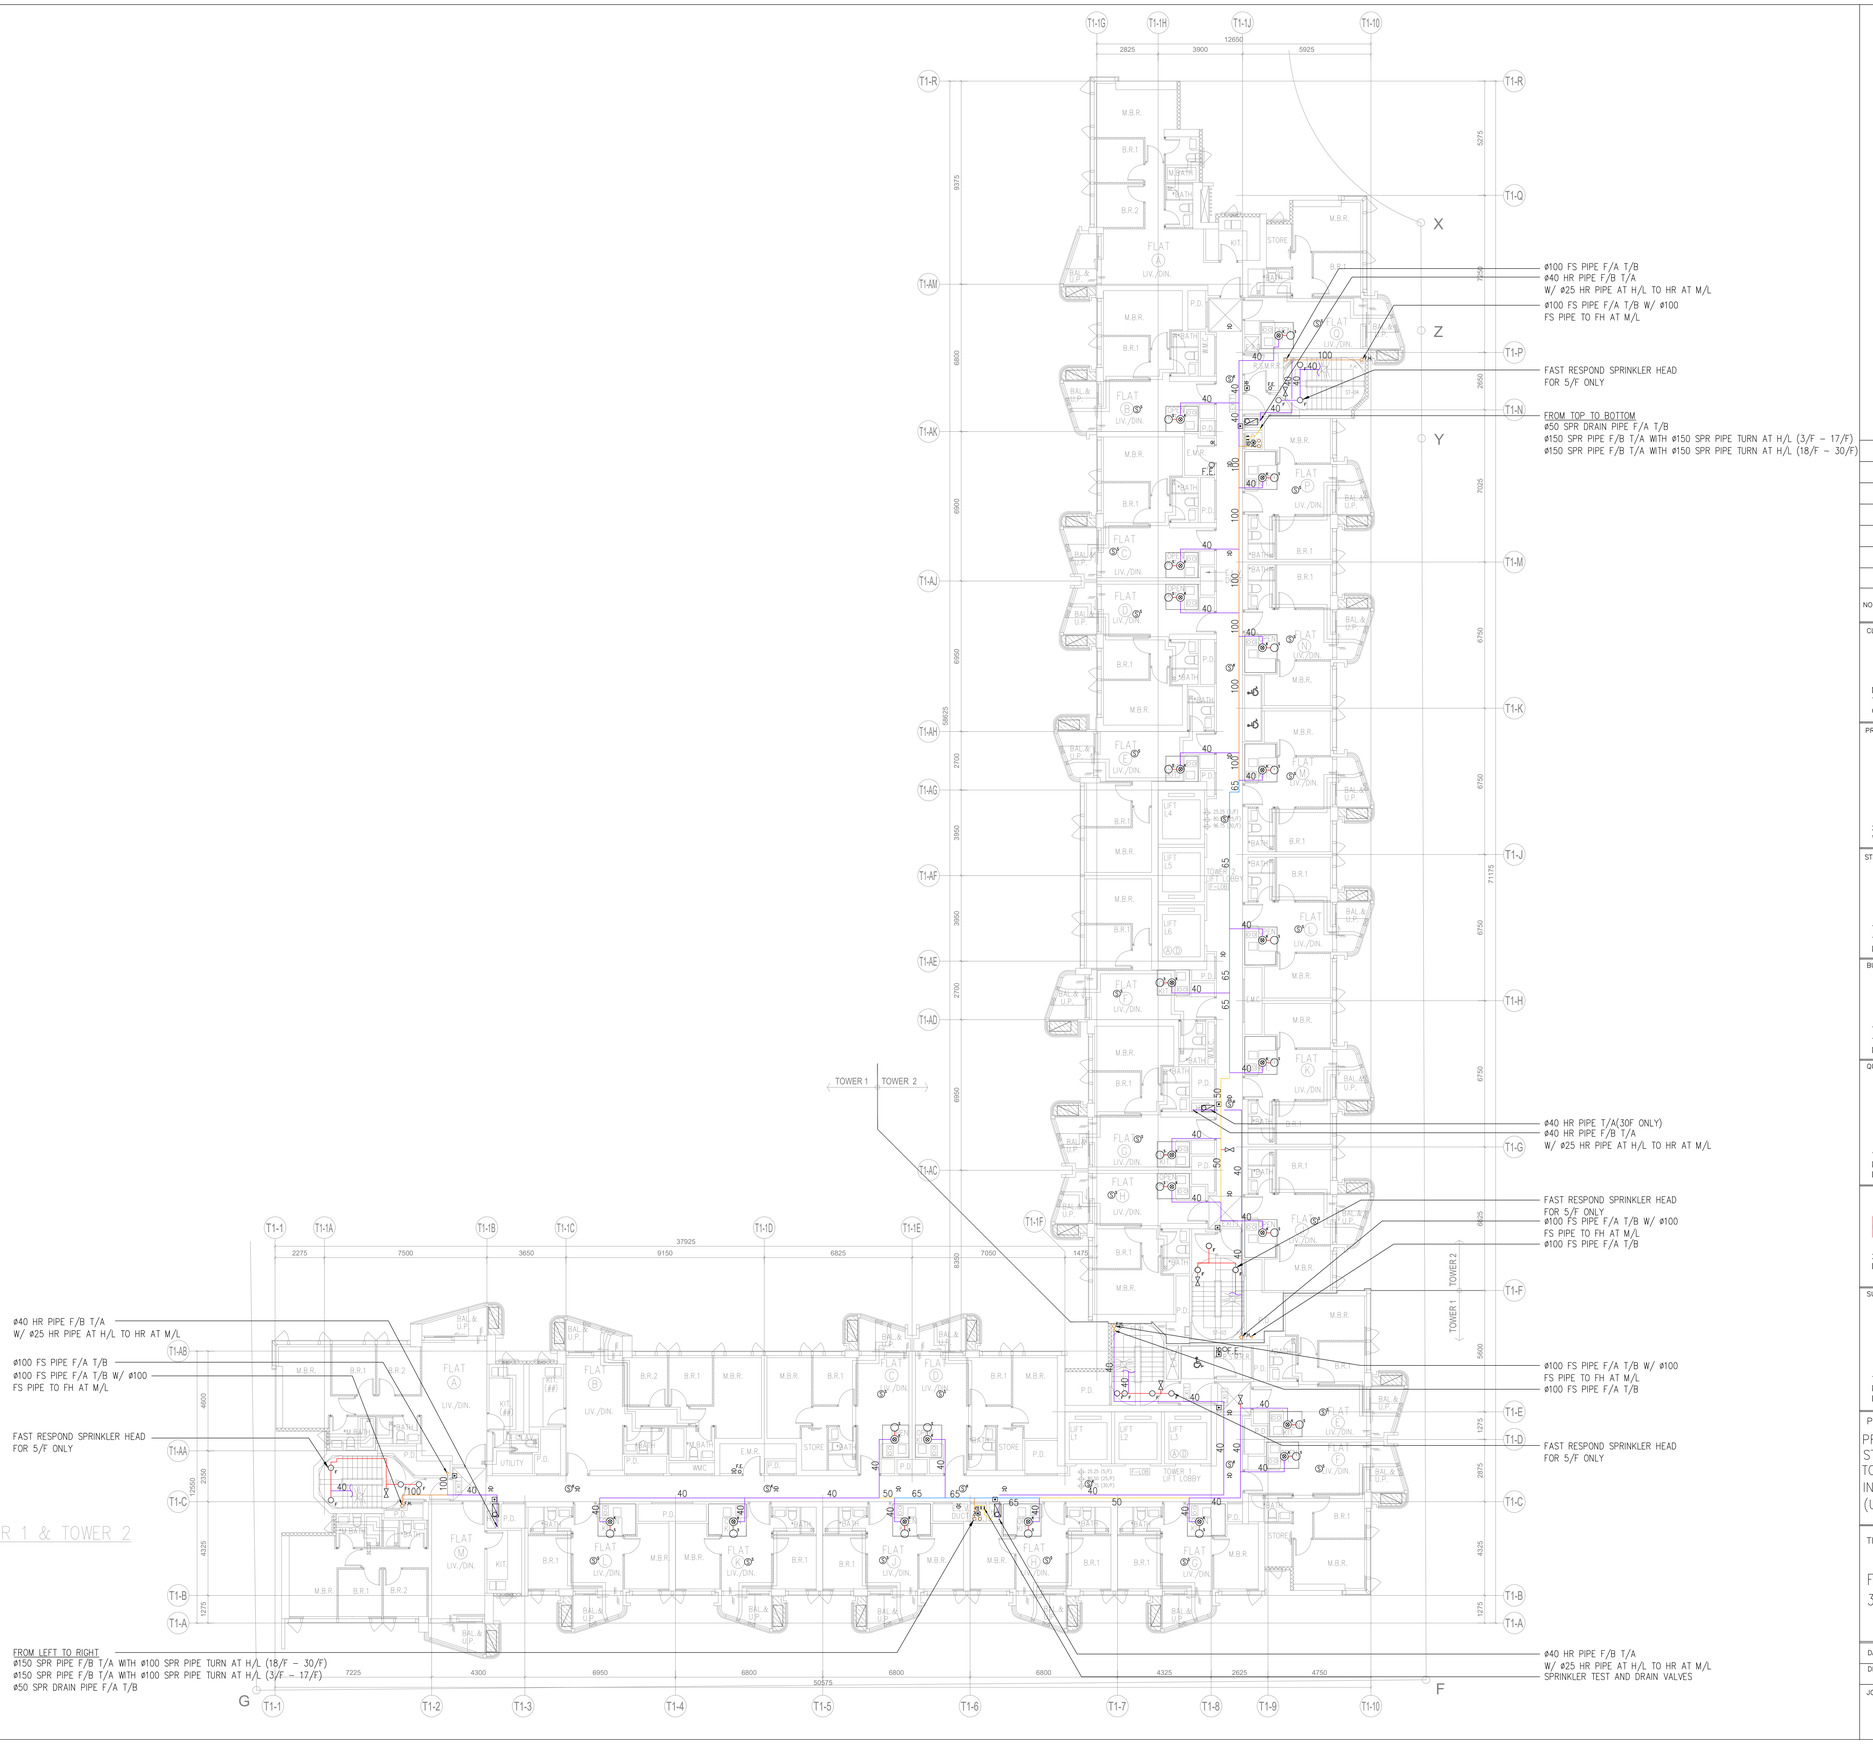


5TH TO 30TH FLOOR PLAN – TOWER 1 & TOWER 2
(23 STOREYS)

NO.	DATE	REVISIONS	DRAFTED	CHECKED	DESIGNED	REVIEWED

CLIENT:

NATION STAR DEVELOPMENT LIMITED
75/F, 8 Finance Street,
Central, Hong Kong

PROJECT ARCHITECT & AUTHORIZED PERSON:

RONALD LU & PARTNERS
呂元祥建築師事務所
33rd Floor, Wu Chung house, 213 Queen's Road East,
Wanchai, Hong Kong

STRUCTURAL/GEOTECHNICAL

wsp
7/F, One Kowloon
1 Wang Yuen Street
Kowloon Bay, Hong Kong

BUILDING SERVICES ENGINEER:

wsp
7/F, One Kowloon
1 Wang Yuen Street
Kowloon Bay, Hong Kong

QUANTITY SURVEYOR:

ARCADIS
17/F, Two Harbour Square, 180 Wai Yip Street,
Kwun Tong, Kowloon
Hong Kong

中國海外房屋工程有限公司
CHINA OVERSEAS BUILDING CONSTRUCTION LIMITED
29/F, China Overseas Building, 139 Hennessy Road,
Hong Kong

SUB CONTRACTOR:

Majestic Engineering Co Ltd
定安工程有限公司
A Member of FSE Lifestyle
17/F, Chevalier Commercial Centre, 8 Wang Hoi Road,
Kowloon Bay, Kowloon
Hong Kong

PROJECT:

PROPOSED DEVELOPMENT AT BAILEY STREET & WING KWONG STREET, TO KWA WAN, KOWLOON
INLAND LOT NO. 11279
(URA PROJECT KC-009)

TITLE:

FIRE SERVICE LAYOUT OF 5/F TO 30/F – TOWER 1 & TOWER 2

DATE: SEP 2026		SCALE: 1:100	
DRAFTED: ALVIN	CHECKED: PETER	DESIGNED: PHILIP	REVIEWED: PHILIP
JOB NO. –	DRAWING NO. FS-FSD-217		REV. NO. 0