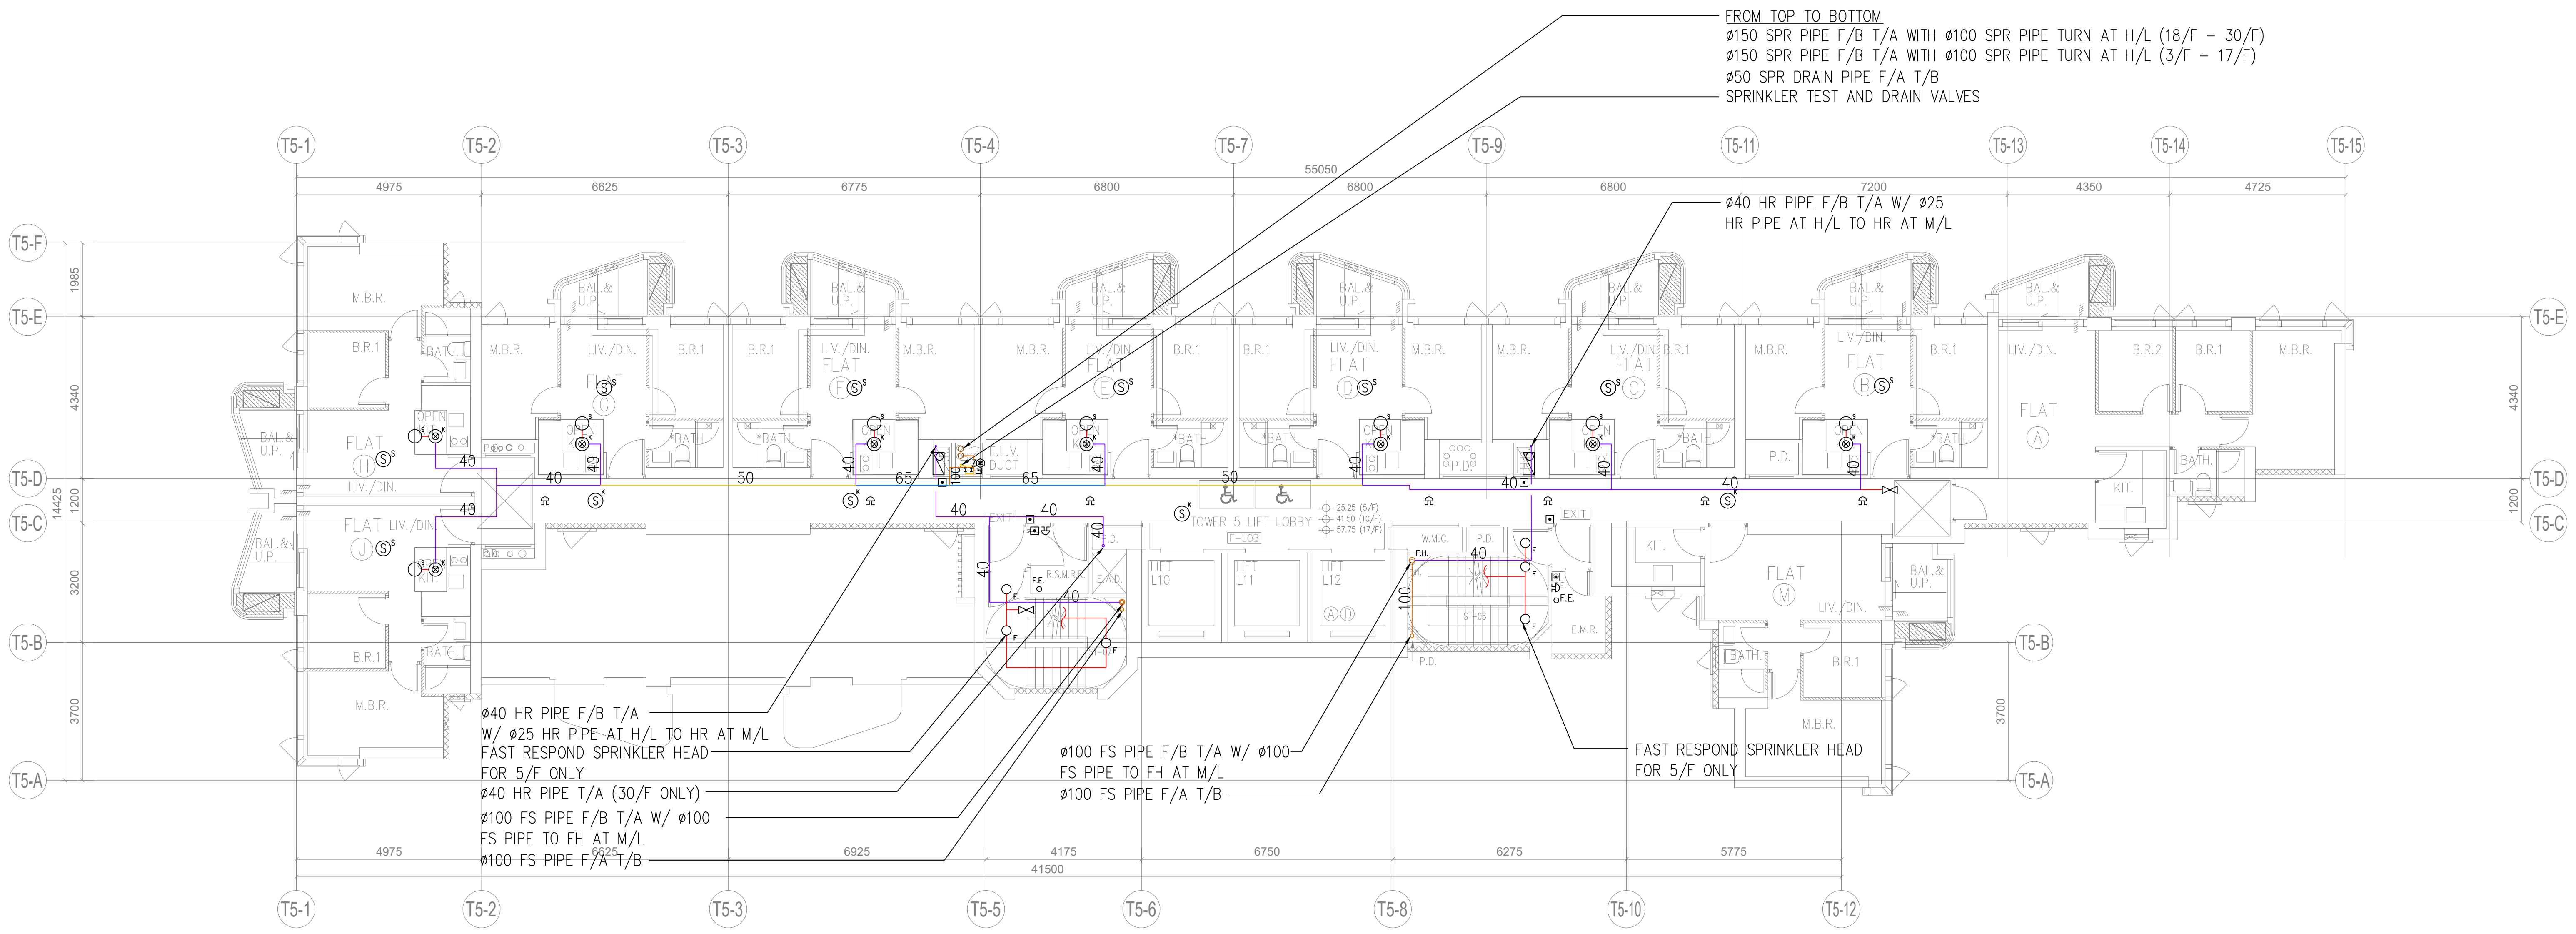

FROM TOP TO BOTTOM
ø150 SPR PIPE F/B T/A WITH ø100 SPR PIPE TURN AT H/L (18/F – 30/F)
ø150 SPR PIPE F/B T/A WITH ø100 SPR PIPE TURN AT H/L (3/F – 17/F)
ø50 SPR DRAIN PIPE F/A T/B
SPRINKLER TEST AND DRAIN VALVES

ø40 HR PIPE F/B T/A W/ ø25
HR PIPE AT H/L TO HR AT M/L

ø40 HR PIPE F/B T/A
W/ ø25 HR PIPE AT H/L TO HR AT M/L
FAST RESPOND SPRINKLER HEAD
FOR 5/F ONLY
ø40 HR PIPE T/A (30/F ONLY)
ø100 FS PIPE F/B T/A W/ ø100
FS PIPE TO FH AT M/L
ø100 FS PIPE F/A T/B

ø100 FS PIPE F/B T/A W/ ø100
FS PIPE TO FH AT M/L
ø100 FS PIPE F/A T/B

FAST RESPOND SPRINKLER HEAD
FOR 5/F ONLY

5th TO 17th FLOOR PLAN – TOWER 5
(11 STOREYS)

NO.	DATE	REVISIONS	DRAFTED	CHECKED	DESIGNED	REVIEWED

CLIENT:

NATION STAR DEVELOPMENT LIMITED
75/F, 8 Finance Street,
Central, Hong Kong

PROJECT ARCHITECT & AUTHORIZED PERSON:

RONALD LU & PARTNERS
呂元祥建築師事務所

33rd Floor, Wu Chung house, 213 Queen's Road East,
Wanchai, Hong Kong

STRUCTURAL/GEOTECHNICAL

wsp

7/F, One Kowloon
1 Wang Yuen Street
Kowloon Bay, Hong Kong

BUILDING SERVICES ENGINEER:

wsp

7/F, One Kowloon
1 Wang Yuen Street
Kowloon Bay, Hong Kong

QUANTITY SURVEYOR:

ARCADIS

17/F, Two Harbour Square, 180 Wai Yip Street,
Kwun Tong, Kowloon
Hong Kong

中國海外房屋工程有限公司
CHINA OVERSEAS BUILDING CONSTRUCTION LIMITED

29/F, China Overseas Building, 139 Hennessy Road,
Hong Kong

SUB CONTRACTOR:

Majestic Engineering Co Ltd
定安工程有限公司
A Member of FSE Lifestyle

17/F, Chevalier Commercial Centre, 8 Wang Hoi Road,
Kowloon Bay, Kowloon
Hong Kong

PROJECT:

PROPOSED DEVELOPMENT AT BAILEY
STREET & WING KWONG STREET,
TO KWA WAN, KOWLOON
INLAND LOT NO. 11279
(URA PROJECT KC–009)

TITLE:

FIRE SERVICE LAYOUT OF 5/F TO 17/F – TOWER 5

DATE: SEP 2026		SCALE: 1:100	
DRAFTED: ALVIN	CHECKED: PETER	DESIGNED: PHILIP	REVIEWED: PHILIP
JOB NO. –	DRAWING NO. FS–FSD–224		REV. NO. 0