SMOKE VENT CALCULATION (NOT FOR FSD APPROVAL):

(COMPARTMENT (B1−4))
AREA REFER DWG. NO. A/GBP/35)
NOTE : DYNAMIC SMOKE EXTRACTION TO BE PROVIDED.

NO.	SIZE	TOTAL
VB1−1	1.000 X 1.000 = 1.000 s.m.	4
VB1−2	1.000 X 1.000 = 1.000 s.m.	
VB1−3	1.000 X 1.000 = 1.000 s.m.	
VB1−4	1.000 X 1.000 = 1.000 s.m.	

SMOKE VENT AREA CALCULATION :

FIRE COMPARTMENT VOLUME = 11185.375 m^3
SMOKE OUTLET Nos. REQ. = 11185.375 / 3500 = 3.196
SMOKE OUTLET Nos. PROV. = 4 Nos.

(COMPARTMENT (B2−4) + (B1−6) + (G−9) + (B1−2))
AREA REFER DWG. NO. A/GBP/35)

NO.	SIZE	TOTAL
VB1−11	1.000 X 2.150 = 2.150 s.m.	9.050
VB1−12	1.900 X 1.000 = 1.900 s.m.	
VB1−13	1.000 X 1.000 = 1.000 s.m.	
VB1−14	1.000 X 1.500 = 1.500 s.m.	
VB1−15	1.000 X 1.000 = 1.000 s.m.	
VB1−16	1.000 X 1.500 = 1.500 s.m.	

SMOKE VENT AREA CALCULATION :

COMPARTMENT FLOOR AREA = 1699.560 m^2
SMOKE OUTLET AREA REQ. = 1699.560 x 0.5% = 8.498 m^2
SMOKE OUTLET AREA PROV. = 9.050 m^2 > 8.498 m^2

(COMPARTMENT (B1−3))
AREA REFER DWG. NO. A/GBP/35)
NOTE : DYNAMIC SMOKE EXTRACTION TO BE PROVIDED.

NO.	SIZE	TOTAL
VB1−21	1.000 X 1.000 = 1.000 s.m.	2
VB1−22	1.000 X 1.000 = 1.000 s.m.	

SMOKE VENT AREA CALCULATION :

FIRE COMPARTMENT VOLUME = 3716.416 m^3
SMOKE OUTLET Nos. REQ. = 3716.416 / 3500 = 1.062
SMOKE OUTLET Nos. PROV. = 2 Nos.

(COMPARTMENT (B1−5)
AREA REFER DWG. NO. A/GBP/35)

NO.	SIZE	TOTAL
VB1−31	4.000 X 1.000 = 4.000 s.m.	5.595 s.m.
VB1−32	1.595 X 1.000 = 1.595 s.m.	

SMOKE VENT AREA CALCULATION :

COMPARTMENT FLOOR AREA = 1086.560 m^2
SMOKE OUTLET AREA REQ. = 1086.560 x 0.5% = 5.433 m^2
SMOKE OUTLET AREA PROV. = 5.595 m^2 > 5.433 m^2

NOTES:

ALL SMOKE VENT ENCLOSURE TO BE −/240/240 FRR
ALL S.E.S. A.D. WITHIN THE SAME COMPARTMENT.

COMMERCIAL CAR PARKING SPACE (2.5mx5.0mx2.4m HEADROOM)			M−EV	EV
	C101 − C112	12 Nos.	4 #	8
COMMERCIAL MOTOR CYCLE PARKING SPACE (1.0mx2.4mx2.4m HEADROOM)				
	CM01 − CM06	6 Nos.	−	6
LOADING/UN−LOADING ** (11mx3.5mx4.7m HEADROOM) / (7mx3.5mx3.6m HEADROOM)				
NON−INDUSTRIAL	HG01 − HG06	6 Nos.	−	
NON−INDUSTRIAL	LG012	1 Nos.	−	

# (NOT LESS THAN 30% OF THE PARKING SPACES PROVIDED)

** LOADING/UN−LOADING SPACE WHICH SHALL BE DESIGNATED AS "COMMON AREA" IN DEED OF MUTUAL COVENANT "DMC" OR SUB−DEED OF MUTUAL CONVENT "SUB−DMC" (IF ANY)

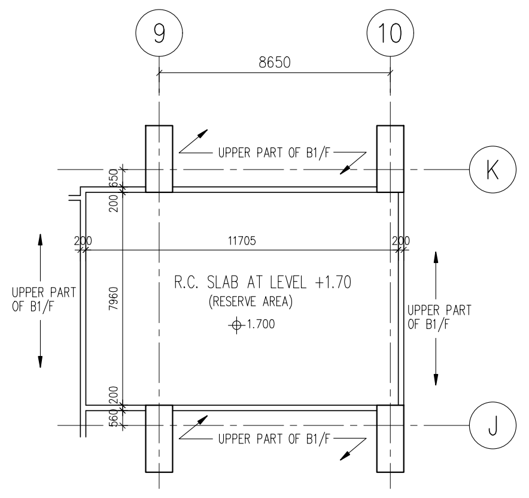

PART PLAN FOR RC SLAB
AT LEVEL +1.70 & +0.80

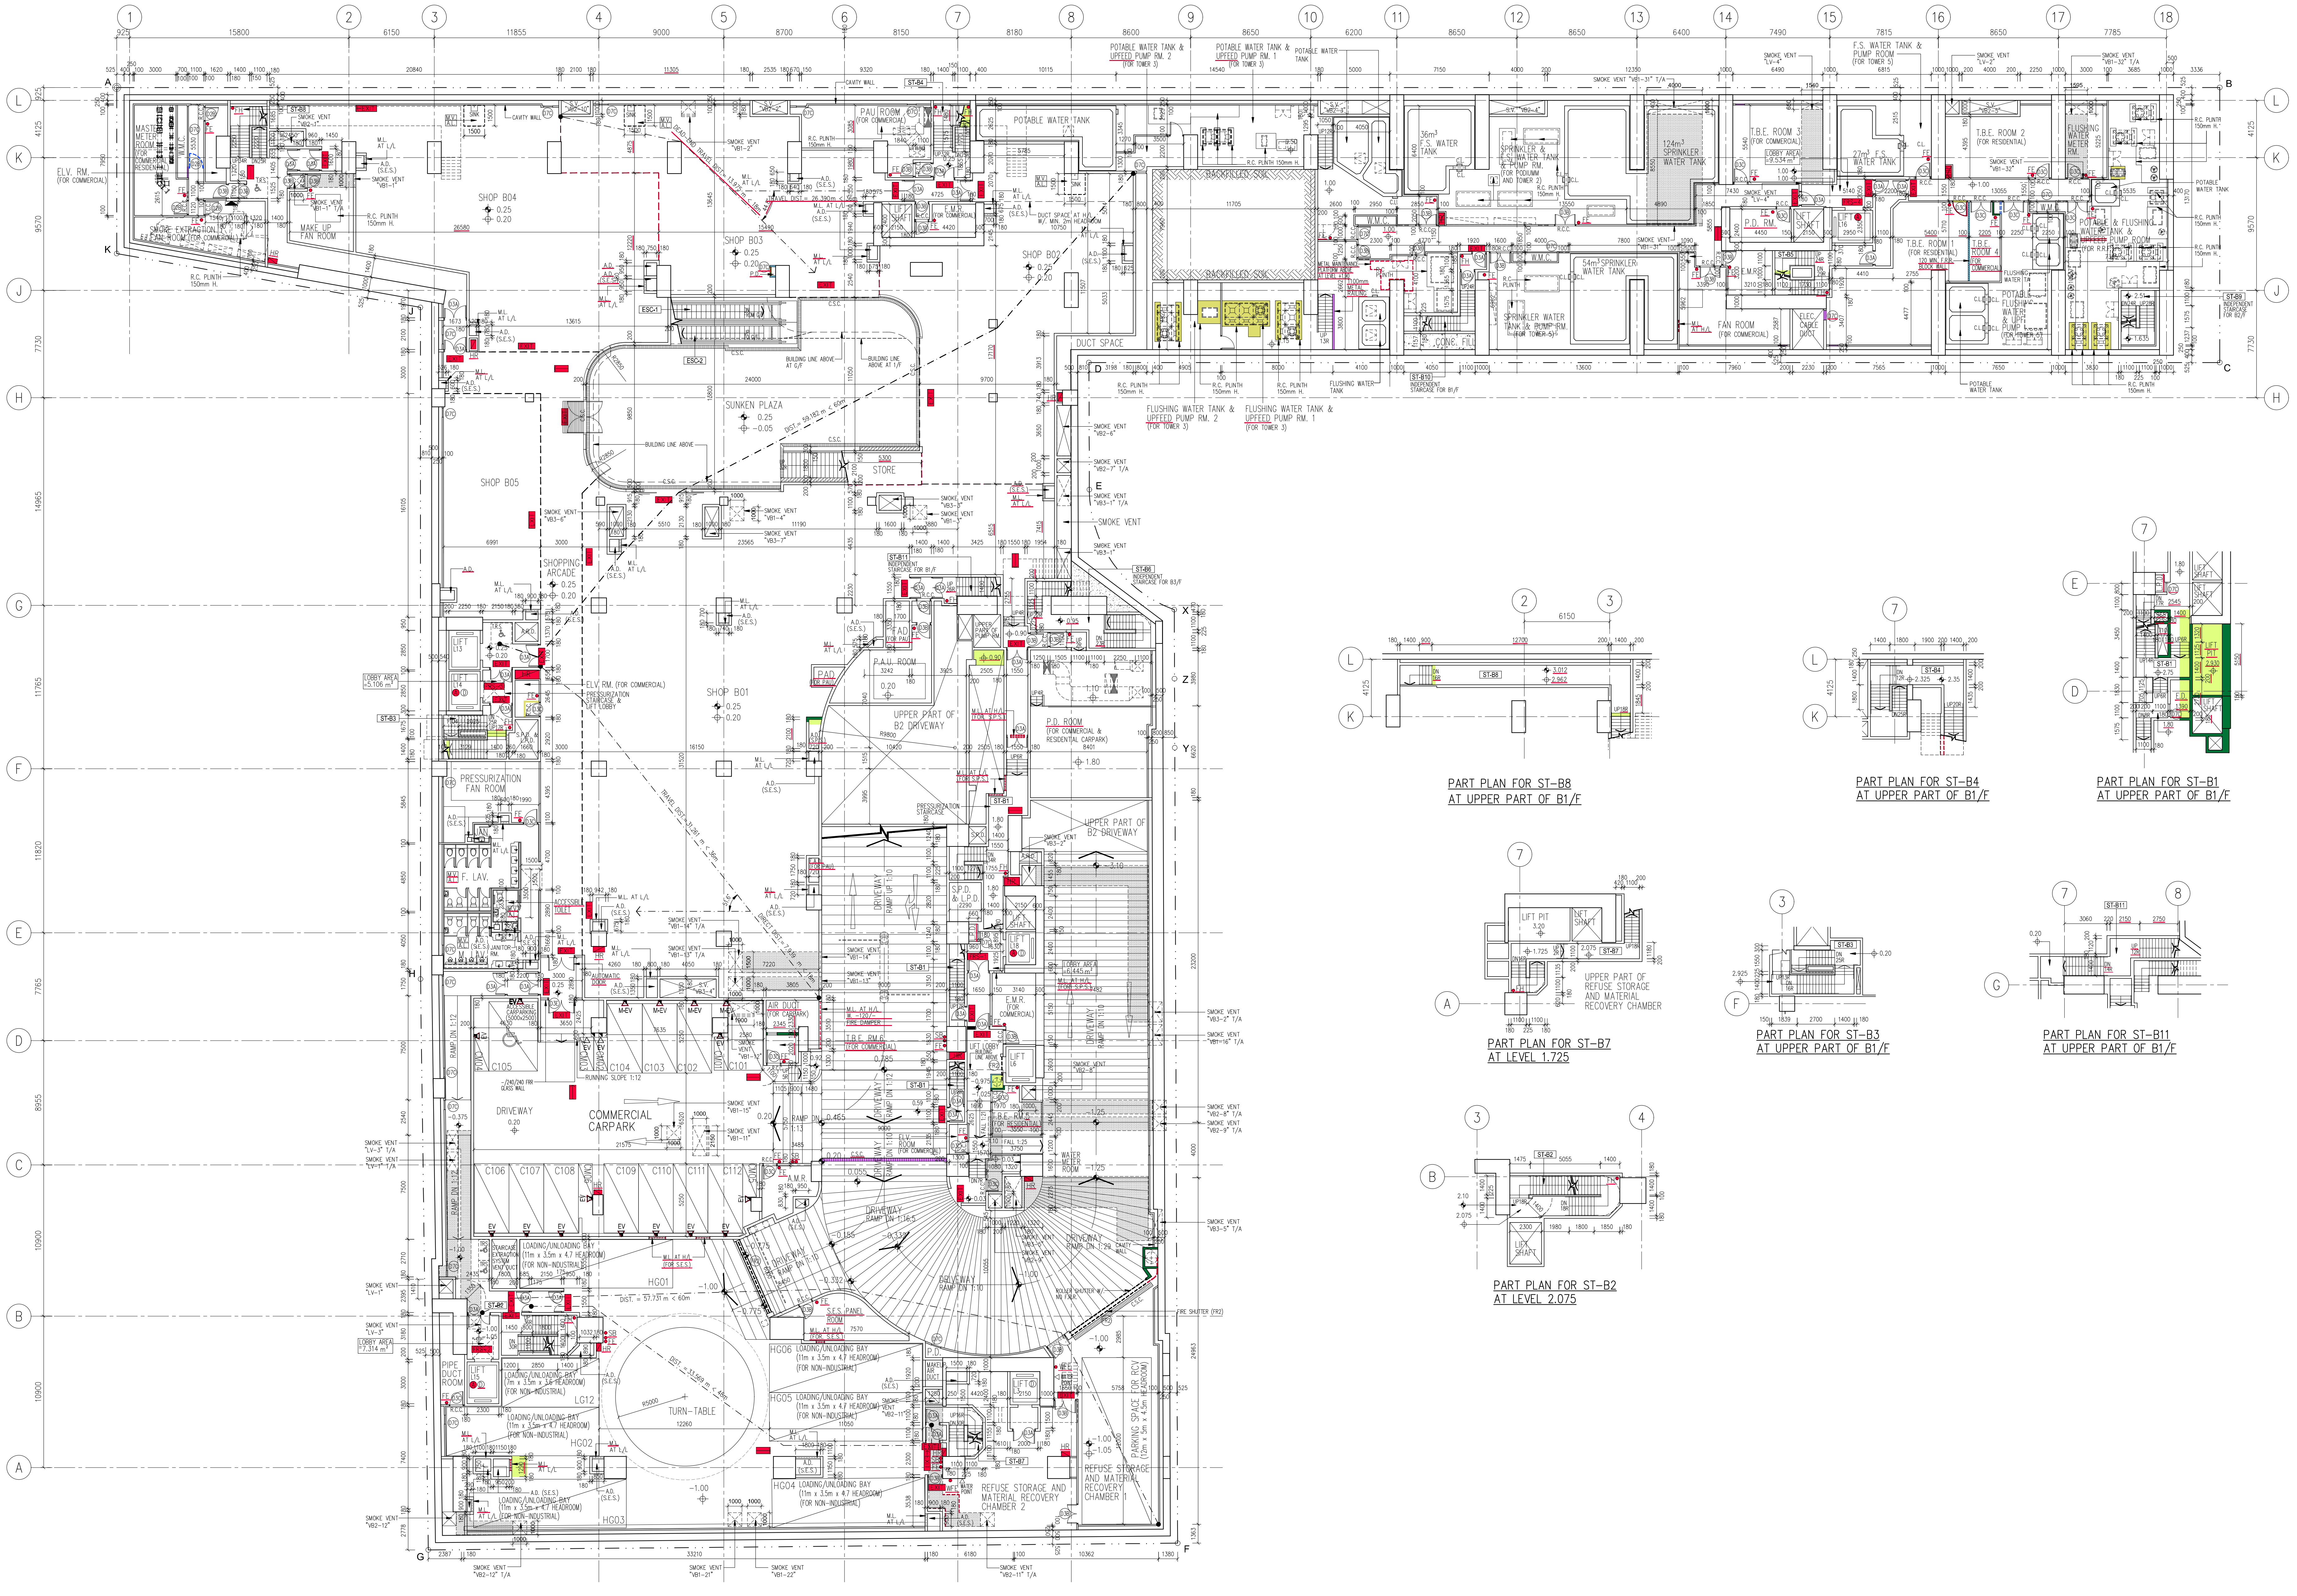

PART PLAN FOR ST−B8
AT UPPER PART OF B1/F

PART PLAN FOR ST−B4
AT UPPER PART OF B1/F

PART PLAN FOR ST−B1
AT UPPER PART OF B1/F

PART PLAN FOR ST−B7
AT LEVEL 1.725

PART PLAN FOR ST−B3
AT UPPER PART OF B1/F

PART PLAN FOR ST−B11
AT UPPER PART OF B1/F

PART PLAN FOR ST−B2
AT LEVEL 2.075

BASEMENT 1 FLOOR PLAN

LEGEND

▨ P − PINK HATCHED BLACK (UNDER LEASE)

△ EV CARPARKING SPACES & MOTORCYCLE PARKING SPACES TO BE PROVIDED AND INSTALLED CHARGING FACILITIES FOR ELECTRIC VEHICLES

△ M−EV CARPARKING SPACES TO BE PROVIDE AND INSTALL ELECTRIC VEHICLE MEDIUM CHARGER

B.D. Ref : BD 2/4024/21
BIM Ref : - --
F.S.D. Ref : - --
D.L.O. Ref : - --

Rev.	Description	Drawn	Checked	Approved	Date
-	1st Submission	WY	AW	AL	07/2022
A	2nd Submission	WY	AW	AL	11/2022
B	1st Amendment	TWM	AW	AL	04/2023
C	2nd Amendment	TWM	AW	AL	12/2023
D	3rd Amendment	TWM	AW	AL	04/2024
D	3rd Amendment (Re-submission)	TWM	AW	AL	05/2024
E	5th Amendment	TWM	AW	AL	12/2024
E	5th Amendment (Re-submission)	TWM	AW	AL	02/2025
F	8th Amendment	TWM	AW	AL	05/2025
G	9th Amendment	TWM	AW	AL	08/2025
H	11th Amendment	TWM	AW	AL	02/2026

RONALD LU & PARTNERS

呂 元 祥 建 築 師 事 務 所

Check all measurements on site. Do not scale off drawings.
This drawing is to be read in conjunction with the specification and any discrepancies are to be immediately reported to the Architect.
This drawing remains the copyright property of the Architect and is not to be reproduced in whole or in part without permission of the Architect.

Project Title :
PROPOSED DEVELOPMENT
AT BAILEY STREET
& WING KWONG STREET
TO KWA WAN, KOWLOON

Drawing Title :
BASEMENT 1 FLOOR PLAN

Drawn By	TWM	Date	08/2025
Checked By	AW	Date	08/2025
Approved By	AL	Date	08/2025
Project No.	21163KL	Issue Date	08/2025

File Path :
U:\Studio_B\Proj_Data\2021\21163KL_Bailey Street & Wing Kwong Street\DRAWING\SUB\BD\GBP_13 (Final Amendment)_Hand Amend\PLOT_FS\A_GBP_05.dwg

Scale 1:200 By CAD

Drawing Number : A/GBP/05
Revision Number : H

Drawing Purpose
Fire Services Department
Amended Plan

FIRE SERVICE REQUIRE-
MENTS INCORPORATED
Date: 12 JUN 2026
(LEUNG KA HAY)
SStnO(NP)