B.D. Ref :	BD 2/4024/21
BIM Ref :	- --
F.S.D. Ref :	- --
D.L.O. Ref :	- --

Rev.	Description	Drawn	Checked	Approved	Date
-	1st Submission	WY	AW	AL	07/2022
A	2nd Submission	WY	AW	AL	11/2022
B	1st Amendment	TWM	AW	AL	04/2023
C	2nd Amendment	TWM	AW	AL	12/2023
D	3rd Amendment	TWM	AW	AL	04/2024
D	3rd Amendment (Re-submission)	TWM	AW	AL	05/2024
E	5th Amendment	TWM	AW	AL	12/2024
E	5th Amendment (Re-submission)	TWM	AW	AL	02/2025
F	8th Amendment	TWM	AW	AL	05/2025
G	9th Amendment	TWM	AW	AL	08/2025
H	10th Amendment	TWM	AW	AL	12/2025
I	11th Amendment	TWM	AW	AL	02/2026

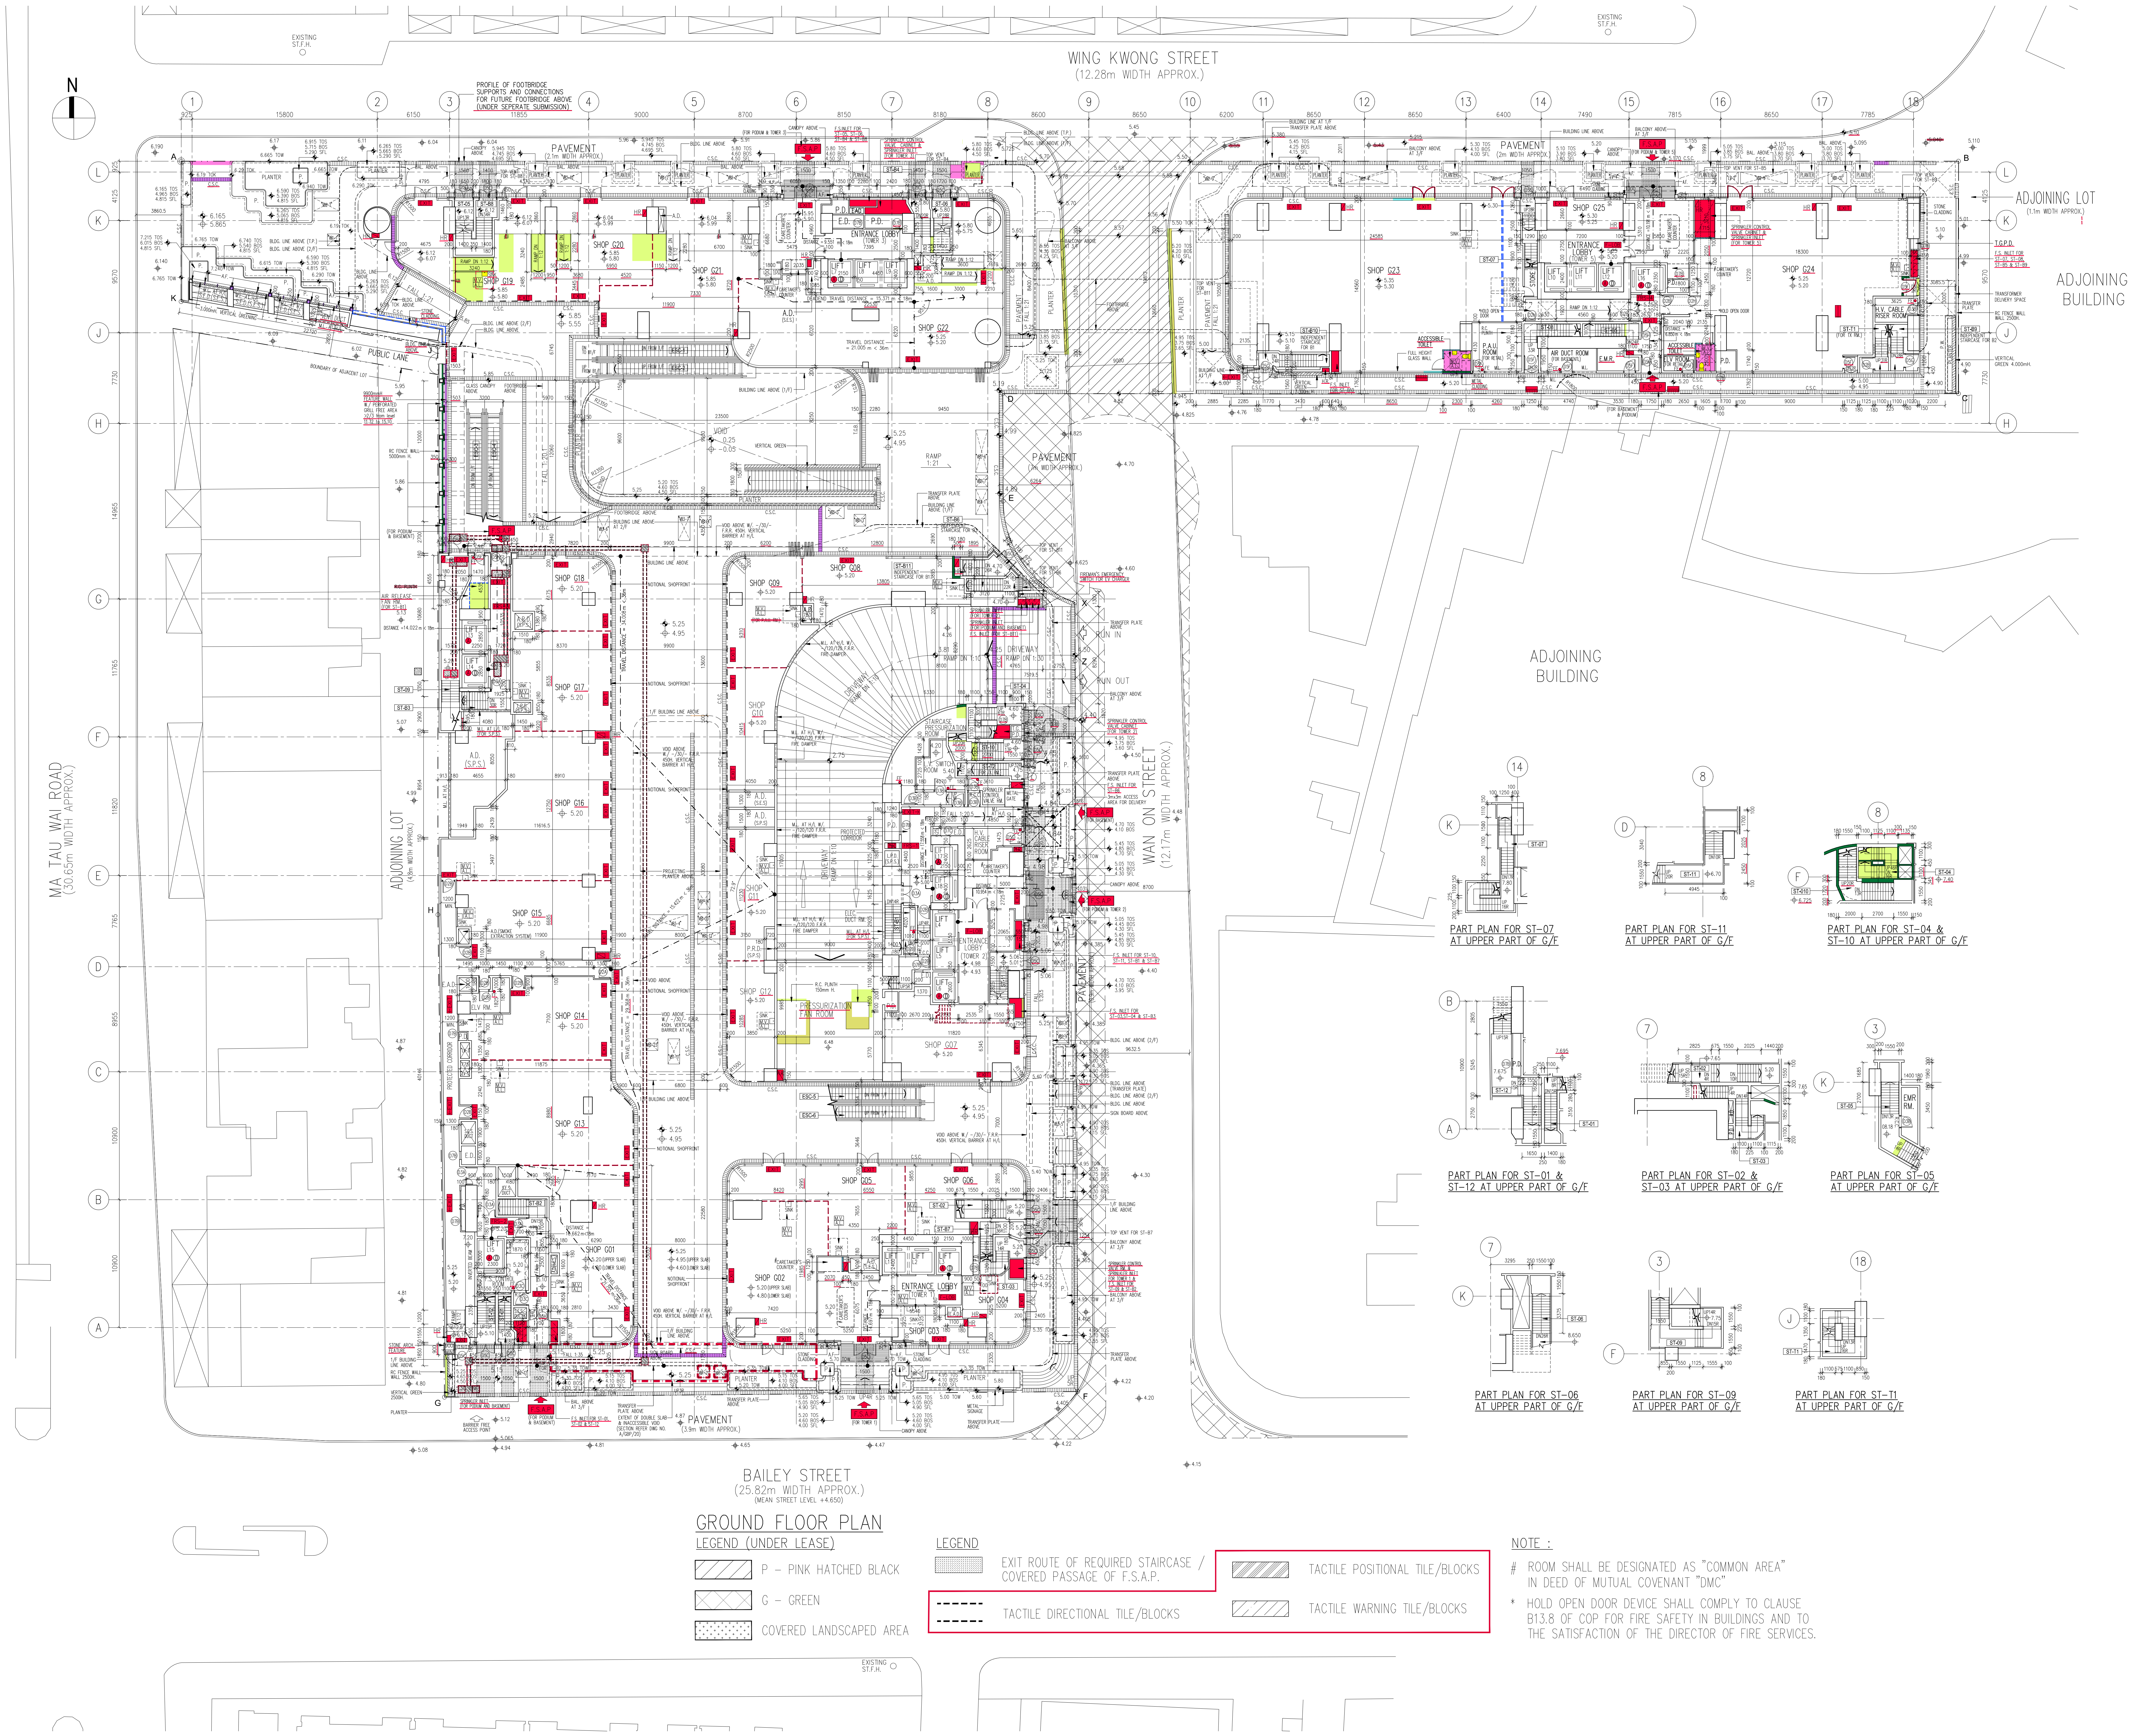
N
WING KWONG STREET
(12.28m WIDTH APPROX.)
EXISTING ST.F.H.
PROFILE OF FOOTBRIDGE SUPPORTS AND CONNECTIONS FOR FUTURE FOOTBRIDGE ABOVE (UNDER SEPERATE SUBMISSION)
PAVEMENT
PUBLIC LANE
ADJOINING LOT
ADJOINING BUILDING
MA TAU WAI ROAD
(30.65m WIDTH APPROX.)
ADJOINING LOT
(4.5m WIDTH APPROX.)
WAN ON STREET
(12.17m WIDTH APPROX.)
BAILEY STREET
(25.82m WIDTH APPROX.)
(MEAN STREET LEVEL +4.650)
PART PLAN FOR ST-07 AT UPPER PART OF G/F
PART PLAN FOR ST-11 AT UPPER PART OF G/F
PART PLAN FOR ST-04 & ST-10 AT UPPER PART OF G/F
PART PLAN FOR ST-01 & ST-12 AT UPPER PART OF G/F
PART PLAN FOR ST-02 & ST-03 AT UPPER PART OF G/F
PART PLAN FOR ST-05 AT UPPER PART OF G/F
PART PLAN FOR ST-06 AT UPPER PART OF G/F
PART PLAN FOR ST-09 AT UPPER PART OF G/F
PART PLAN FOR ST-T1 AT UPPER PART OF G/F

GROUND FLOOR PLAN

LEGEND (UNDER LEASE)

- ▨ P – PINK HATCHED BLACK
- ▨ G – GREEN
- ▨ COVERED LANDSCAPED AREA

LEGEND

- ▨ EXIT ROUTE OF REQUIRED STAIRCASE / COVERED PASSAGE OF F.S.A.P.
- ▨ TACTILE POSITIONAL TILE/BLOCKS
- - - - TACTILE DIRECTIONAL TILE/BLOCKS
- ▨ TACTILE WARNING TILE/BLOCKS

NOTE :

# ROOM SHALL BE DESIGNATED AS "COMMON AREA" IN DEED OF MUTUAL COVENANT "DMC"

* HOLD OPEN DOOR DEVICE SHALL COMPLY TO CLAUSE B13.8 OF COP FOR FIRE SAFETY IN BUILDINGS AND TO THE SATISFACTION OF THE DIRECTOR OF FIRE SERVICES.

RONALD LU & PARTNERS

呂 元 祥 建 築 師 事 務 所

Check all measurements on site. Do not scale off drawings.
This drawing is to be read in conjunction with the specification and any discrepancies are to be immediately reported to the Architect.
This drawing remains the copyright property of the Architect and is not to be reproduced in whole or in part without permission of the Architect.

Project Title :
PROPOSED DEVELOPMENT
AT BAILEY STREET
& WING KWONG STREET
TO KWA WAN, KOWLOON

Drawing Title :
GROUND FLOOR PLAN

Drawn By	TWM	Date	08/2025
Checked By	AW	Date	08/2025
Approved By	AL	Date	08/2025
Project No.	21163KL	Issue Date	08/2025

File Path :
U:\Studio_B\Proj_Data\2021\21163KL_Bailey Street & Wing Kwong Street\DRAWING\SUB\BD\GBP_13 (Final Amendment)_Hand Amend\PLOT_FS\A_GBP_06.dwg

Scale 1:200 By CAD

Drawing Number : A/GBP/06
Revision Number : I

Drawing Purpose
Fire Services Department
Amended Plan

FIRE SERVICE REQUIREMENTS INCORPORATED
Date: 12 JUN 2026
(LEUNG KA HAY)
SStnO(NP)