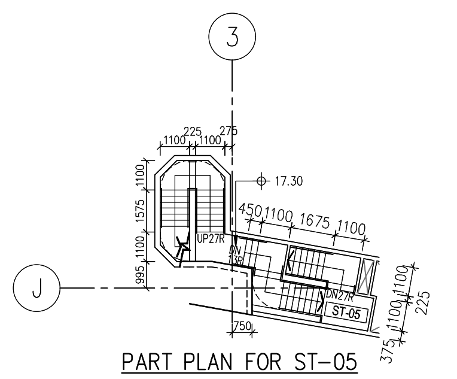

PART PLAN FOR ST-05
AT UPPER PART OF 2/F

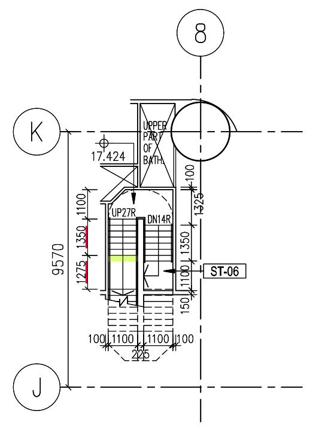

PART PLAN FOR ST-06
AT LEVEL +17.424

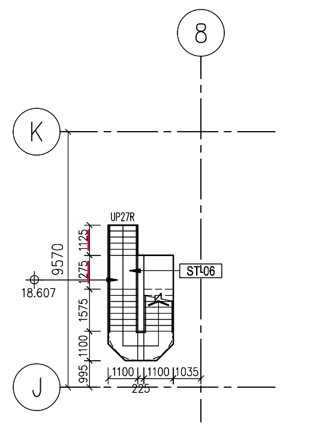

PART PLAN FOR ST-06
AT UPPER PART OF 2/F

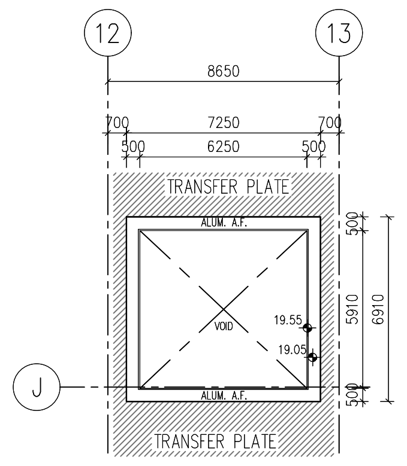

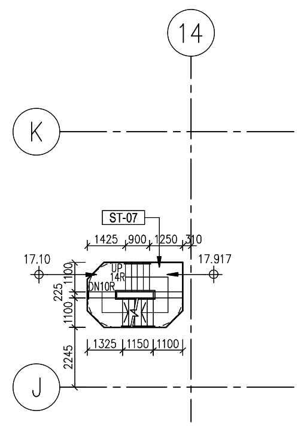

PART PLAN FOR ST-07
AT LEVEL +17.10

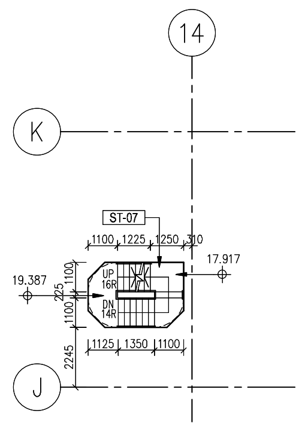

PART PLAN FOR ST-07
AT UPPER PART OF 2/F

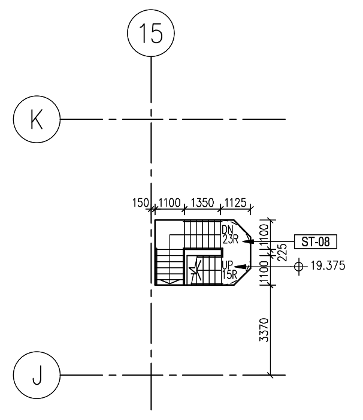

PART PLAN FOR ST-08
AT UPPER PART OF 2/F

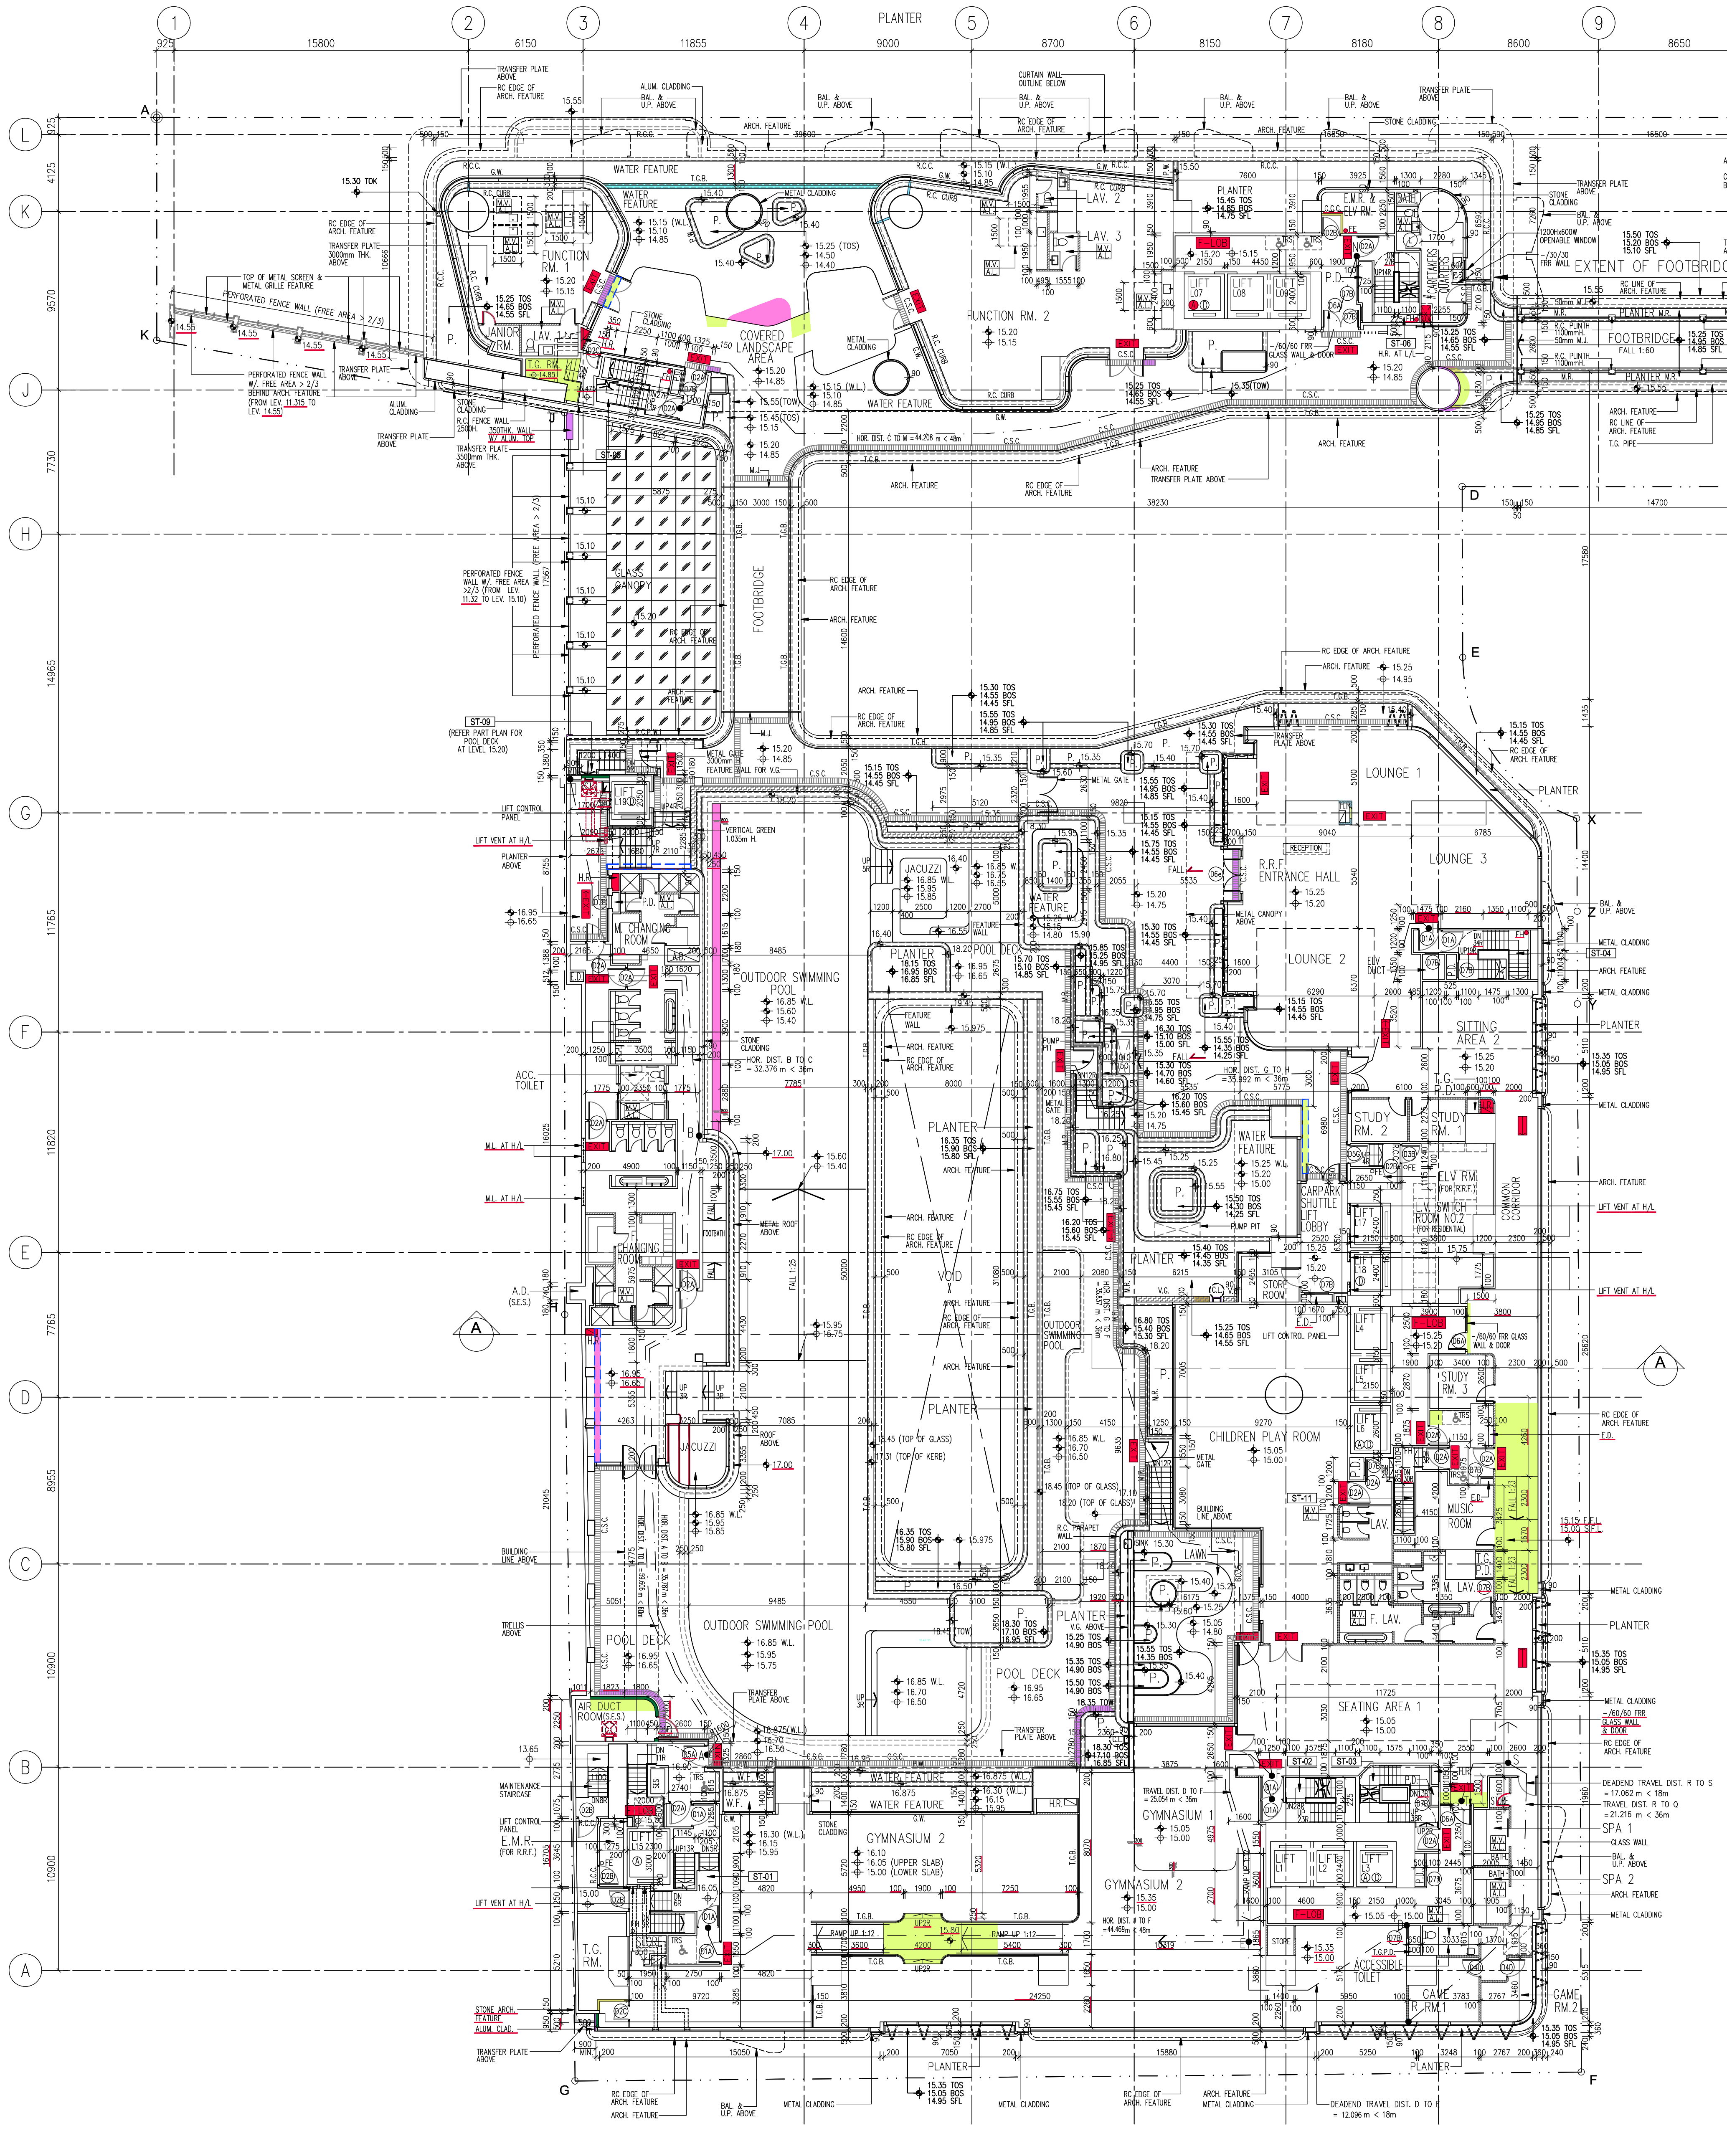

2ND FLOOR PLAN

LEGEND

▨ COVERED LANDSCAPE AREA

NOTE :

# ROOM SHALL BE DESIGNATED AS "COMMON AREA"
IN DEED OF MUTUAL COVENANT "DMC"

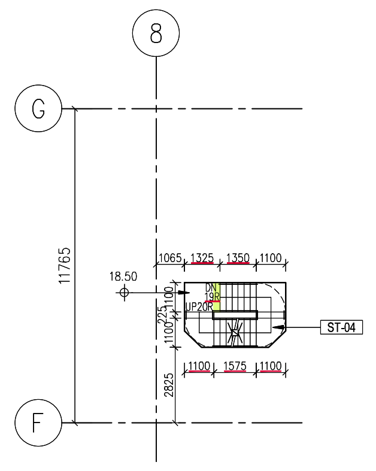

PART PLAN FOR ST-04
AT UPPER PART OF 2/F

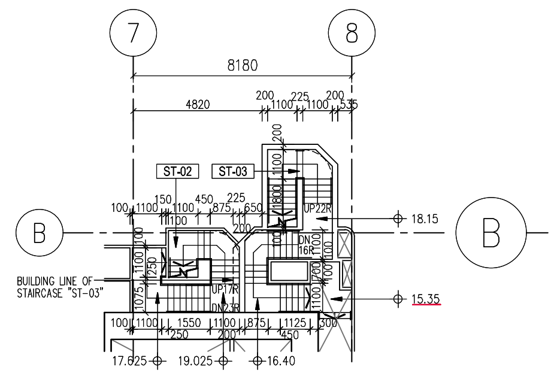

PART PLAN FOR ST-02 & ST-03
AT UPPER PART OF 2/F

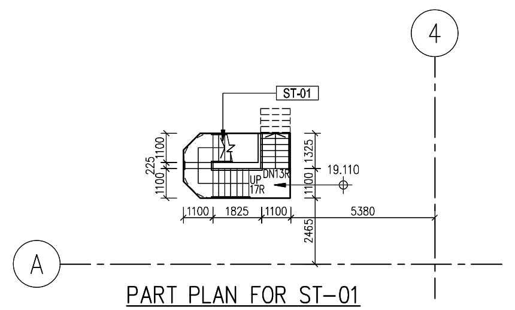

PART PLAN FOR ST-01
AT UPPER PART OF 2/F

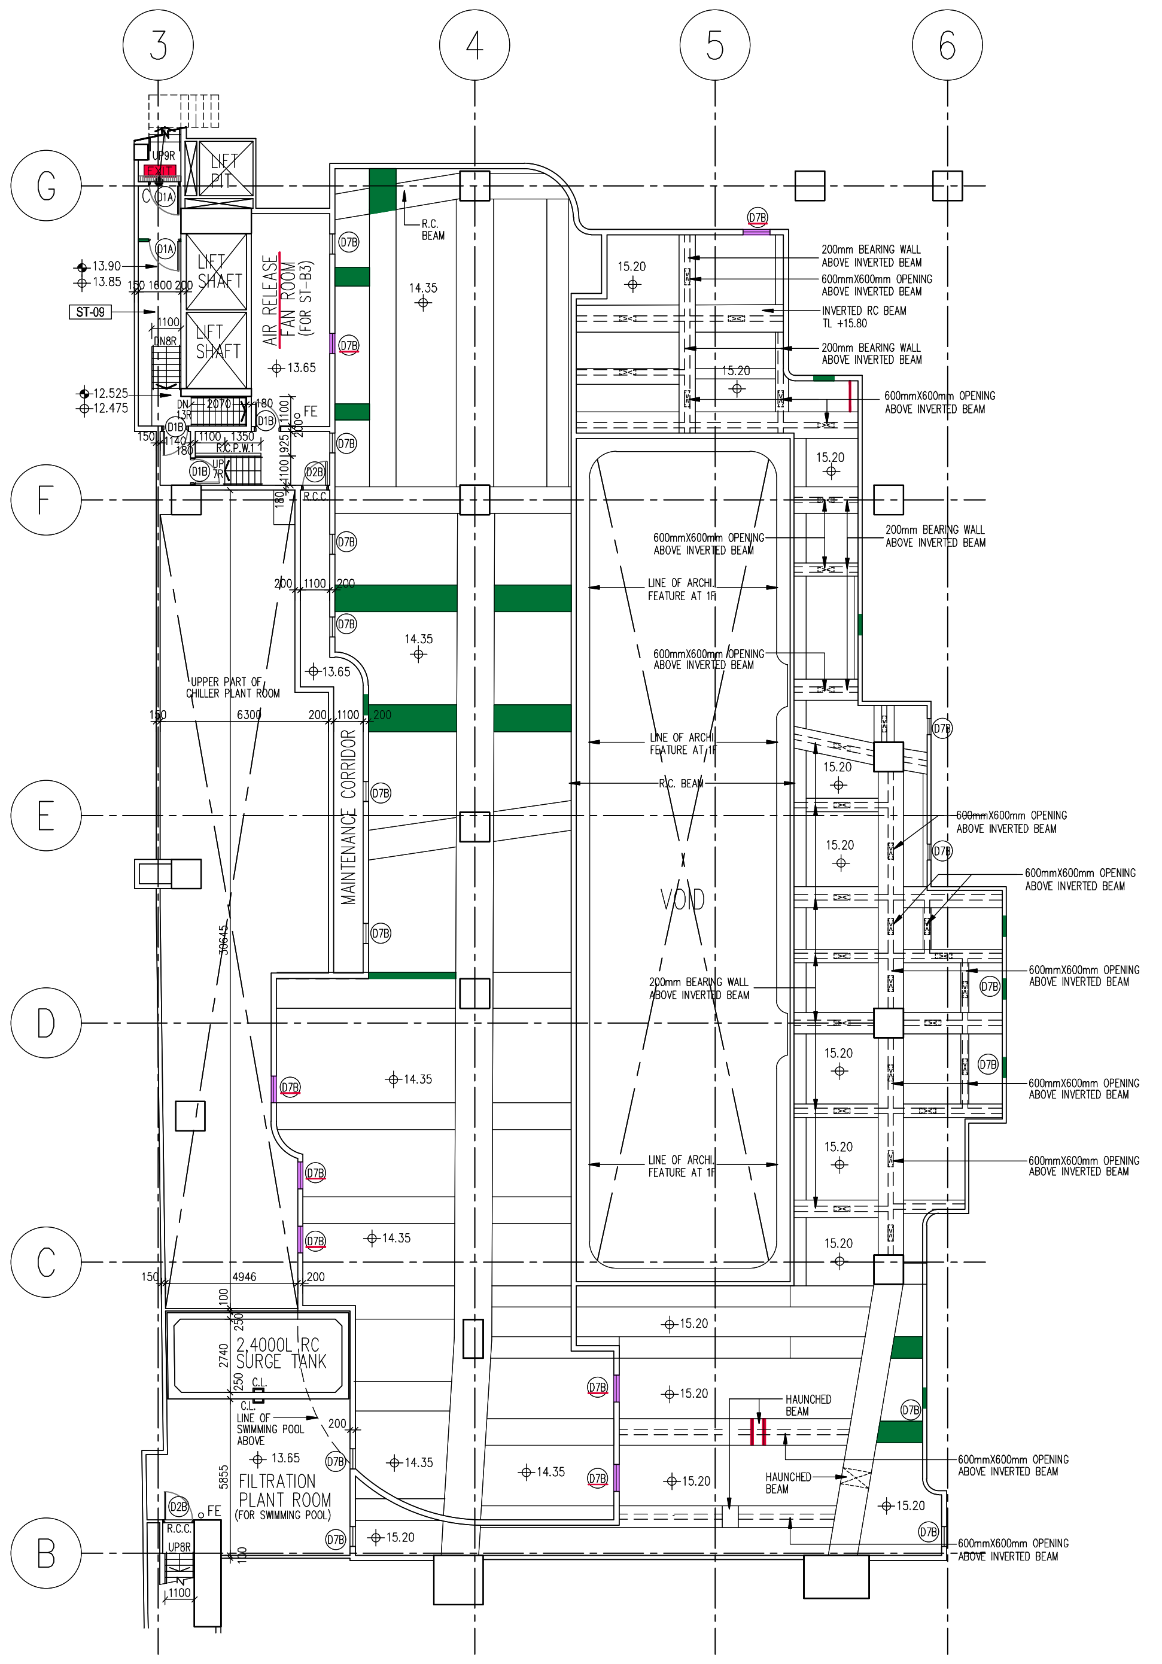

PART PLAN FOR POOL DECK
AT LEVEL 15.20

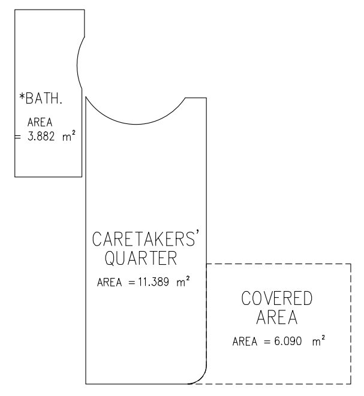

CARETAKERS' QUARTER AREA

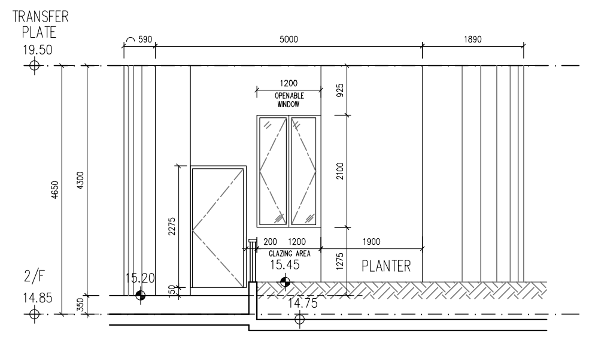

FLOOR AREA = 11.389 s.m. + 6.090 s.m.
= 17.479 s.m.

WINDOW AREA REQ'D = 17.479 / 10 = 1.748 s.m.
WINDOW AREA PROV'D = 1.200 x 2.100 x 0.70
= 1.764 s.m. > 1.748 s.m. (REQUIRED)

OPENABLE WINDOW AREA REQ'D = 17.479 /16 + 3.882 / 10 = 1.481 s.m.
OPENABLE WINDOW AREA PROV'D = 1.200 x 2.100 x 0.70
= 1.764 s.m. >1.481 s.m. (REQUIRED)

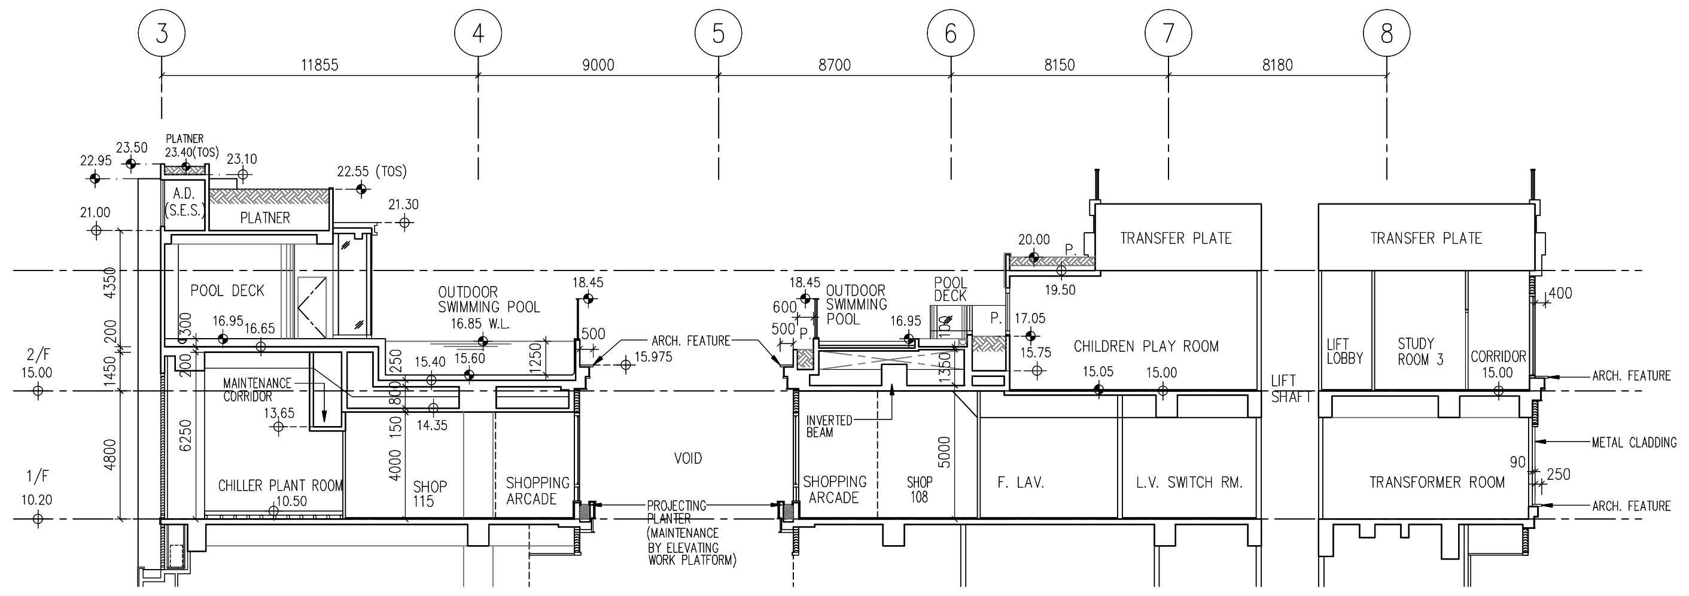

PART SECTION A

B.D. Ref : BD 2/4024/21
BIM Ref : - –
F.S.D. Ref : - –
D.L.O. Ref : - –

Rev.	Description	Drawn	Checked	Approved	Date
-	1st Submission	WY	AW	AL	07/2022
A	2nd Submission	WY	AW	AL	11/2022
B	1st Amendment	TWM	AW	AL	04/2023
C	2nd Amendment	TWM	AW	AL	12/2023
D	3rd Amendment	TWM	AW	AL	04/2024
D	3rd Amendment (Re-submission)	TWM	AW	AL	05/2024
E	5th Amendment	TWM	AW	AL	12/2024
E	5th Amendment (Re-submission)	TWM	AW	AL	02/2025
F	8th Amendment	TWM	AW	AL	05/2025
G	9th Amendment	TWM	AW	AL	08/2025
H	10th Amendment	TWM	AW	AL	12/2025
I	11th Amendment	TWM	AW	AL	02/2026

RONALD LU
& PARTNERS

呂元祥建築師事務所

Check all measurements on site. Do not scale off drawings.
This drawing is to be read in conjunction with the specification and any discrepancies are to be immediately reported to the Architect.
This drawing remains the copyright property of the Architect and is not to be reproduced in whole or in part without permission of the Architect.

Project Title :
PROPOSED DEVELOPMENT
AT BAILEY STREET
& WING KWONG STREET
TO KWA WAN, KOWLOON

Drawing Title :
2ND FLOOR PLAN

Drawn By	TWM	Date	08/2025
Checked By	AW	Date	08/2025
Approved By	AL	Date	08/2025
Project No.	21163KL	Issue Date	08/2025

File Path :
U:\Studio_B\Proj_Data\2021\21163KL_Bailey Street & Wing Kwong Street\DRAWING\SUB\BD\GBP_13 (Final Amendment)_Hand Amend (FSD)\PLOT_FS\A_GBP_08.dwg

Scale 1:200 By CAD

Drawing Number : A/GBP/08
Revision Number : I

Drawing Purpose

Fire Services Department
Amended Plan

FIRE SERVICE REQUIREMENTS INCORPORATED
Date: 12 JUN 2026
(LEUNG KA HAY)
SStnO(NP)