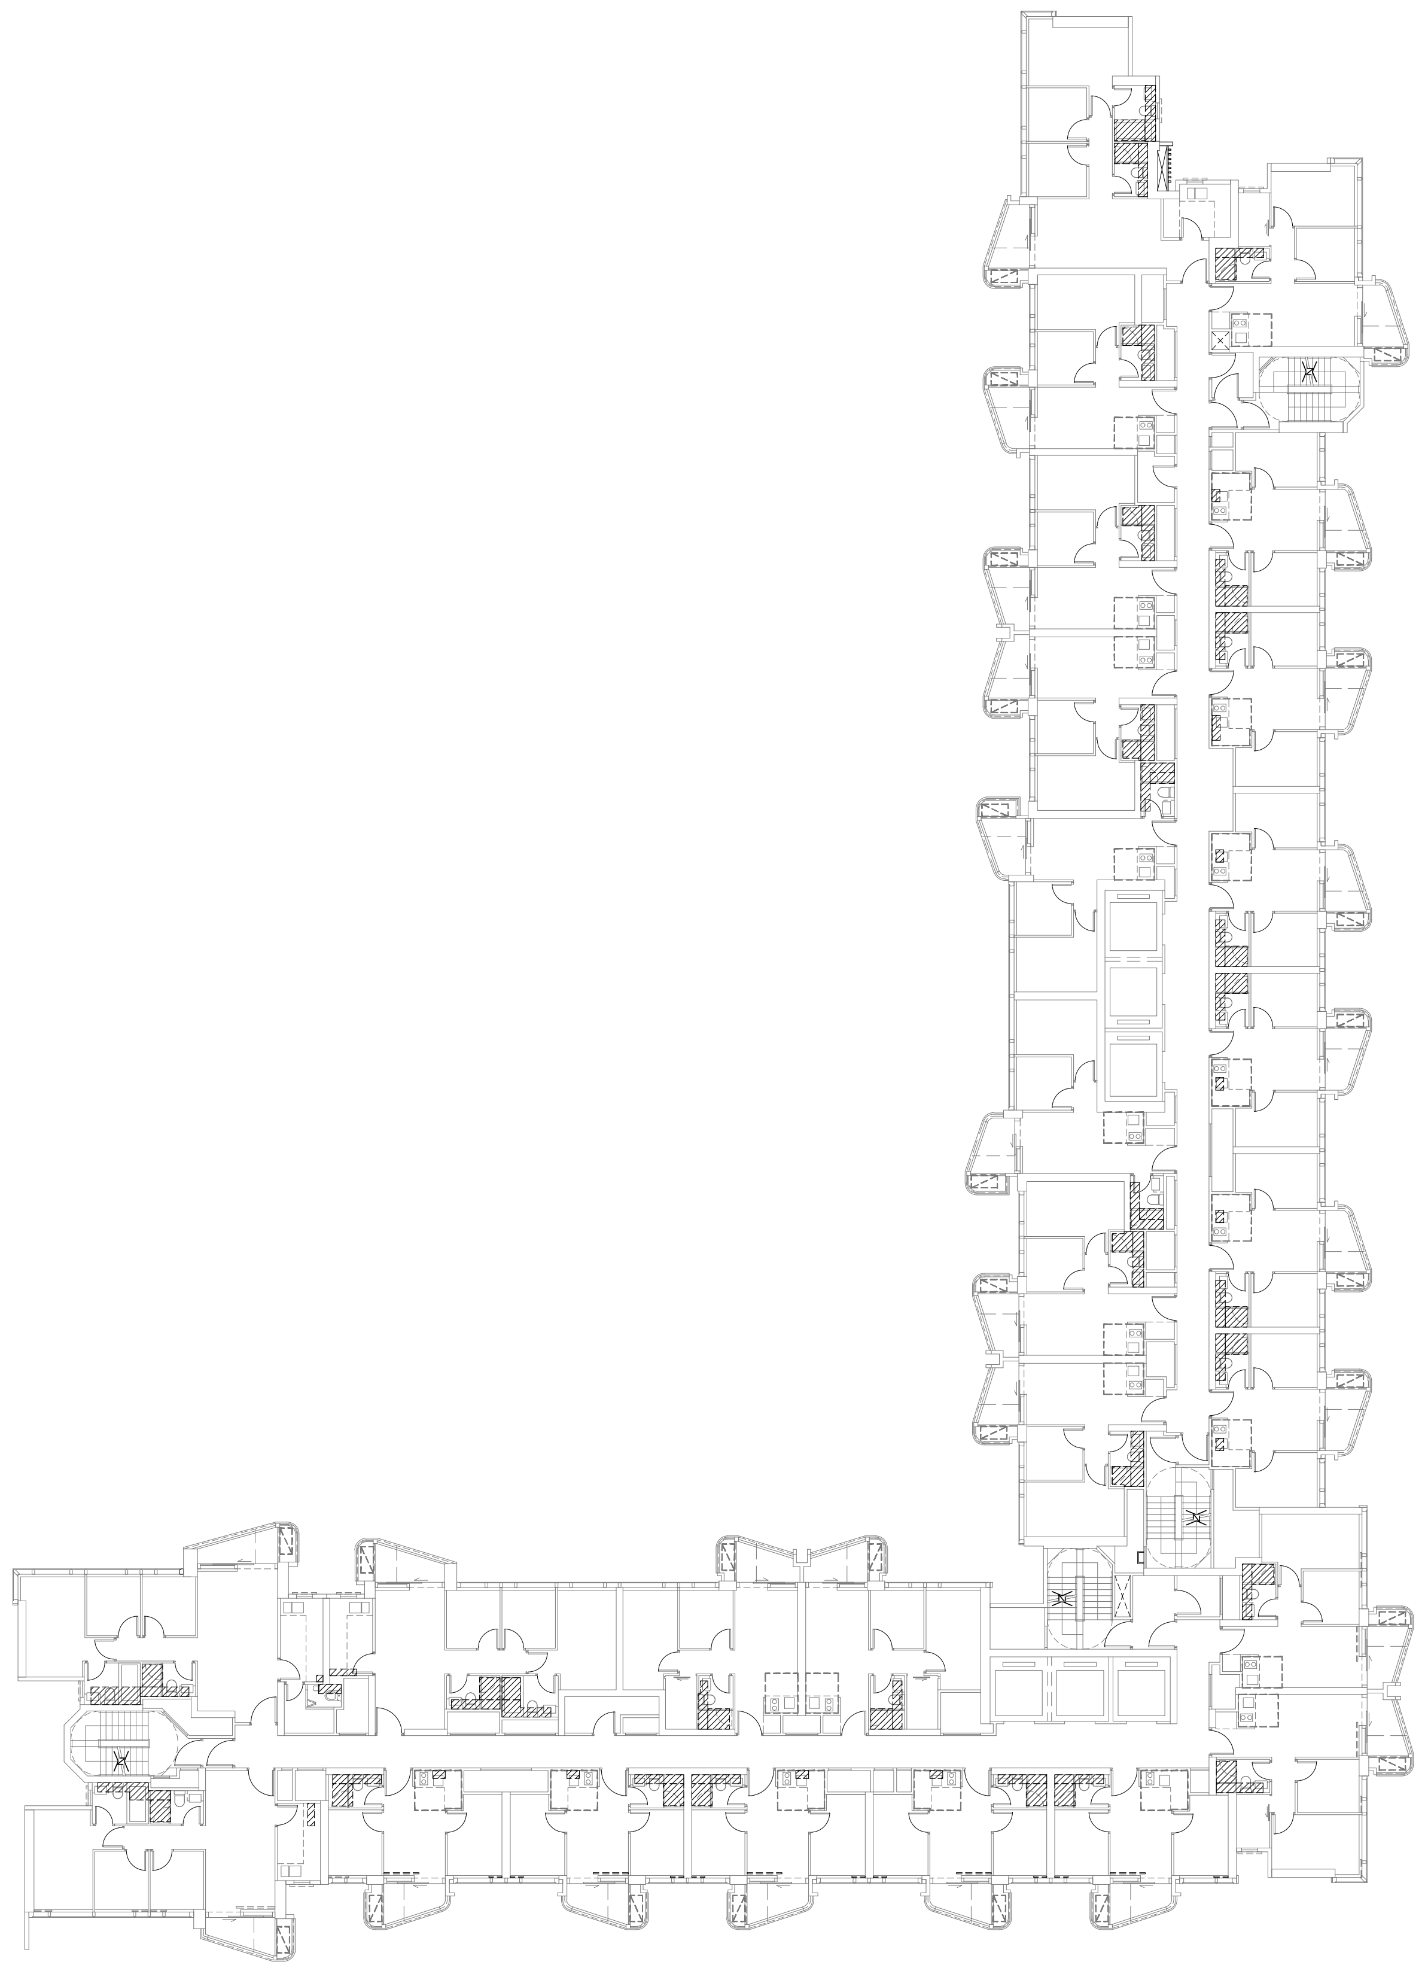

## DIAGRAM OF SUNKEN SLAB EXTENT (5th TO 30th FLOOR)

SCALE 1:200

LEGEND:

▨ SUNKEN SLAB

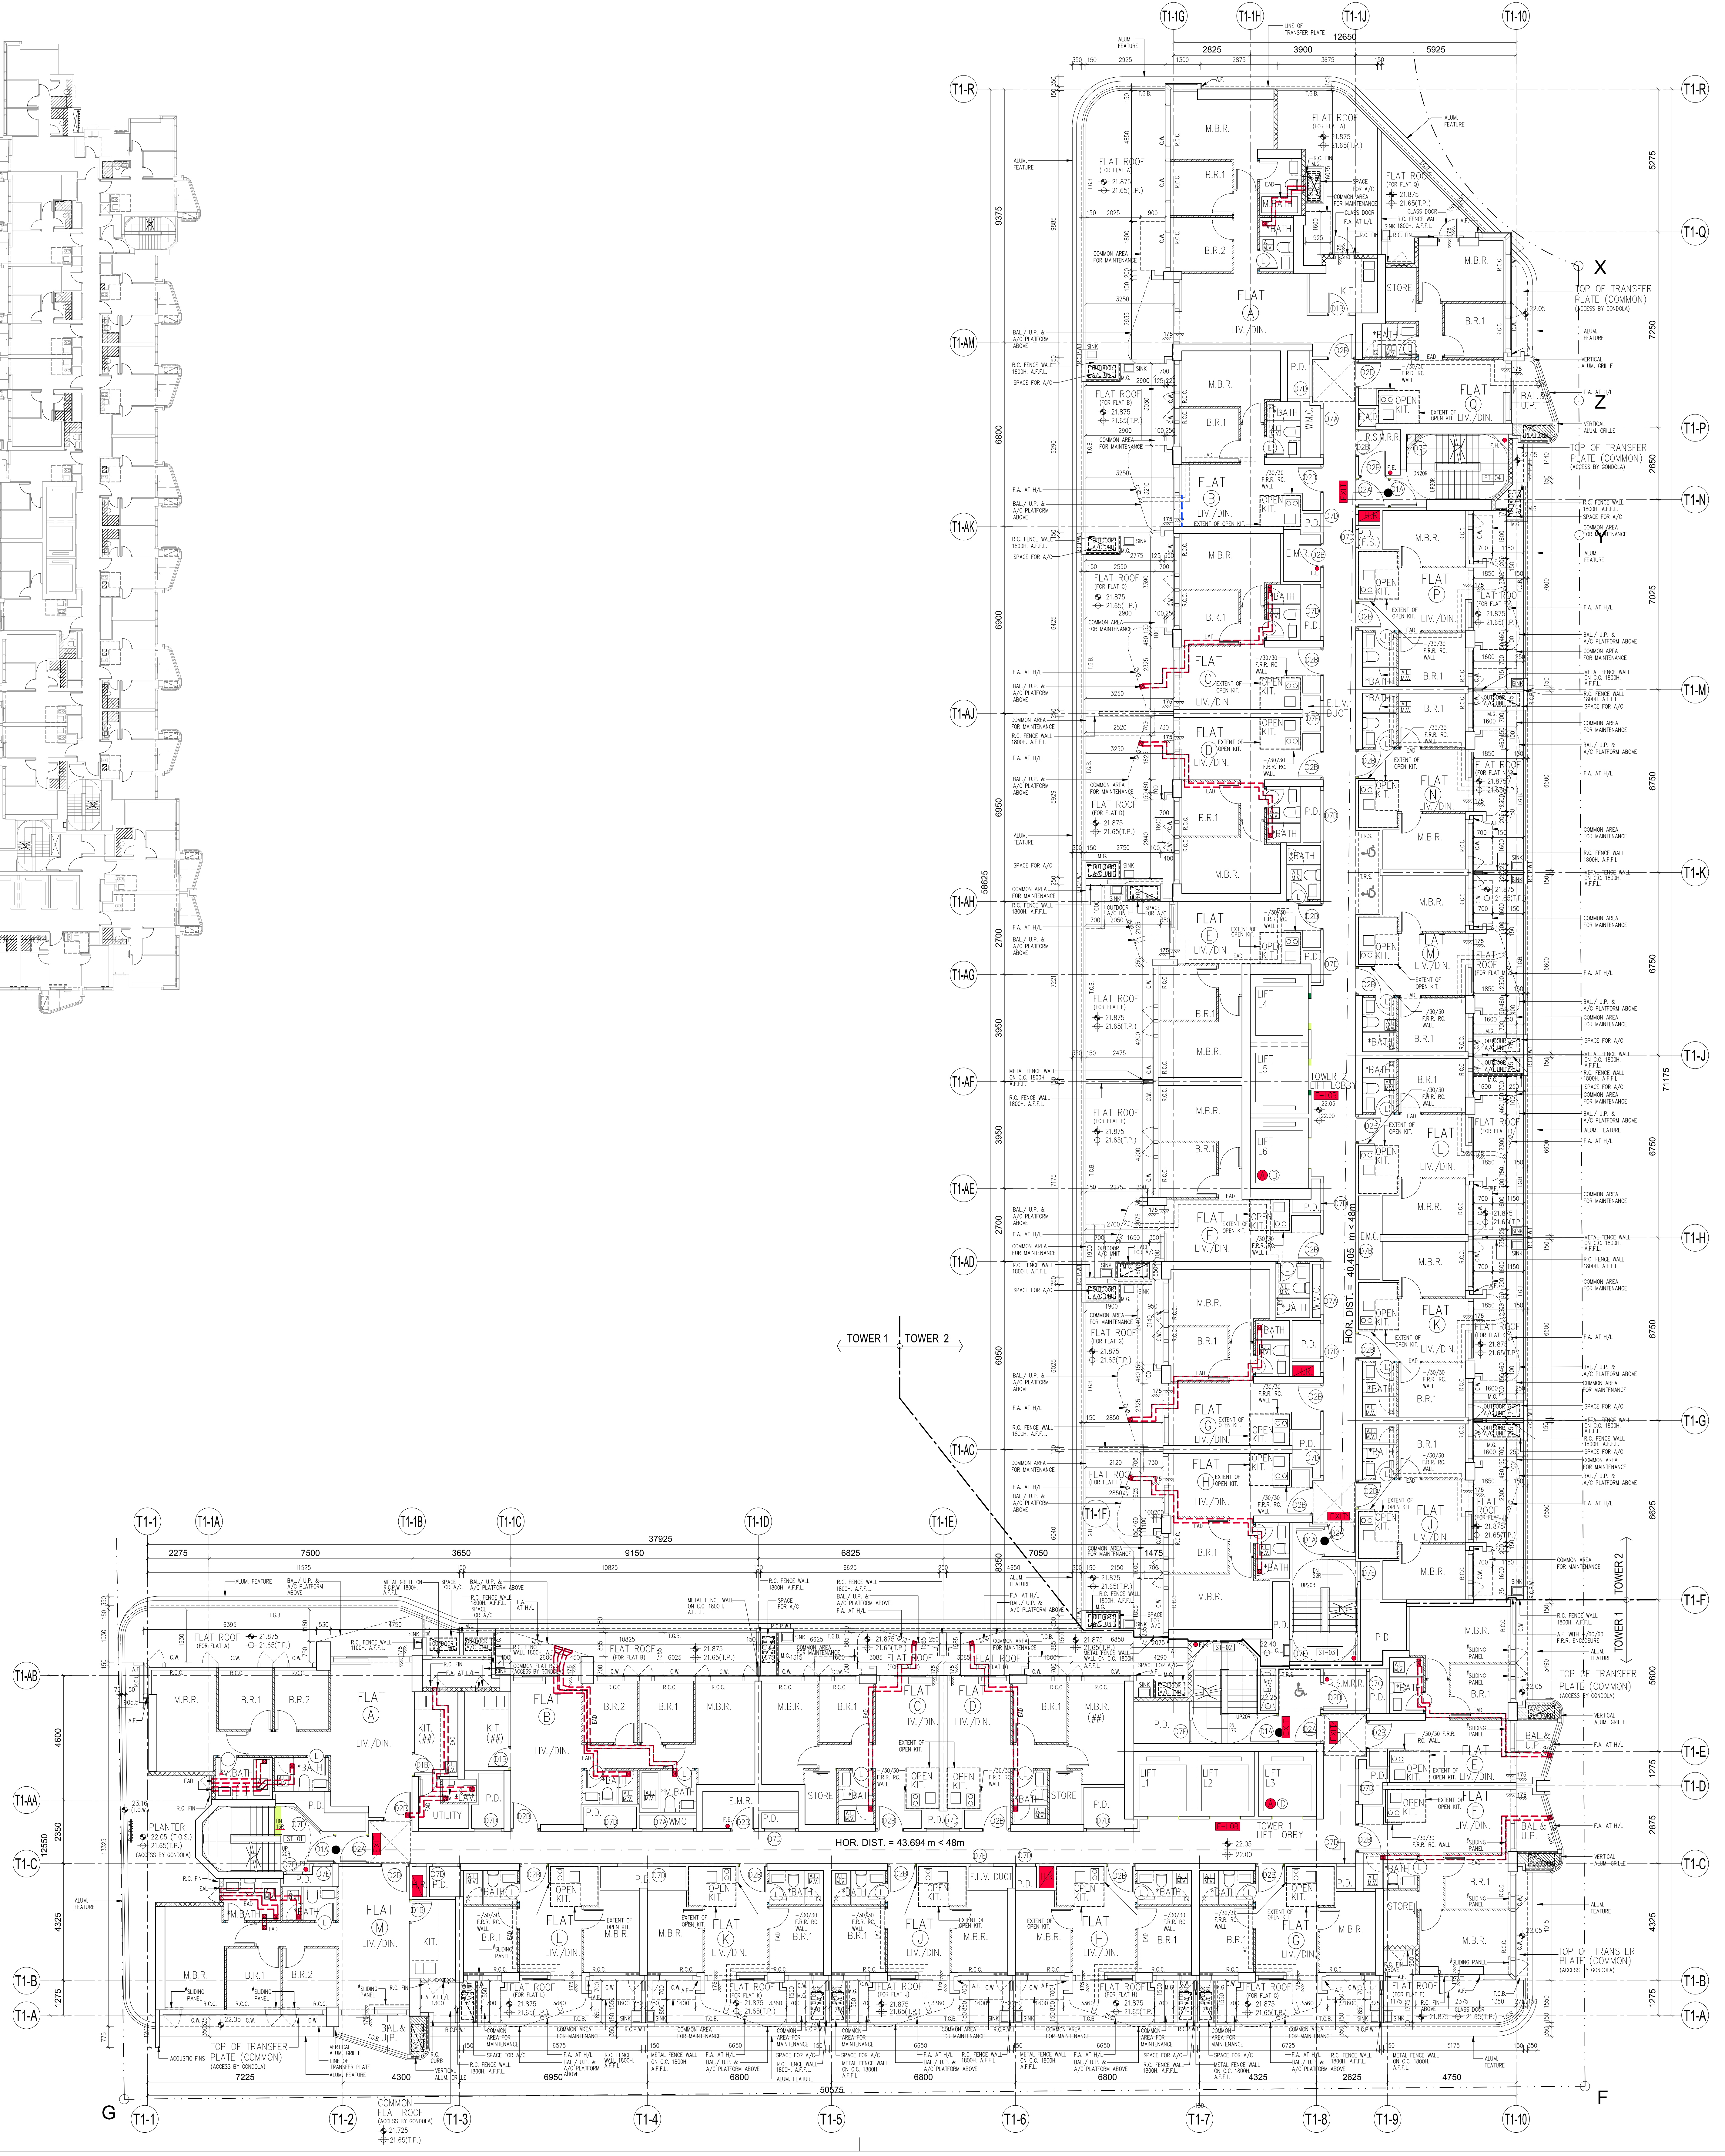

T1-1G
T1-1H
T1-1J
T1-10
T1-R
T1-Q
T1-P
T1-N
T1-M
T1-K
T1-J
T1-H
T1-G
T1-F
T1-E
T1-D
T1-C
T1-B
T1-A
T1-AM
T1-AK
T1-AJ
T1-AH
T1-AG
T1-AF
T1-AE
T1-AD
T1-AC
T1-1F
T1-1
T1-1A
T1-1B
T1-1C
T1-1D
T1-1E
T1-AB
T1-AA
T1-2
T1-3
T1-4
T1-5
T1-6
T1-7
T1-8
T1-9
X
Z
Y
G
F
12650
2825
3900
5925
37925
2275
7500
3650
9150
6825
7050
1475
71175
50525
7225
4300
6950
6800
6800
4325
2625
4750
FLAT A
FLAT B
FLAT C
FLAT D
FLAT E
FLAT F
FLAT G
FLAT H
FLAT J
FLAT K
FLAT L
FLAT M
FLAT N
FLAT P
FLAT Q
M.B.R.
B.R.1
B.R.2
LIV./DIN.
KIT.
BATH
STORE
UTILITY
LIFT L1
LIFT L2
LIFT L3
LIFT L4
LIFT L5
LIFT L6
TOWER 1 LIFT LOBBY
TOWER 2 LIFT LOBBY
TOWER 1
TOWER 2
HOR. DIST. = 43.694m < 48m
HOR. DIST. = 40.405 m < 48m
TOP OF TRANSFER PLATE (COMMON)
FLAT ROOF
COMMON AREA FOR MAINTENANCE
BAL./U.P. & A/C PLATFORM ABOVE
ALUM. FEATURE
SPACE FOR A/C
F.A. AT H/L
PLANTER
COMMON FLAT ROOF

## 3RD FLOOR PLAN – TOWER 1 & TOWER 2

NOTE:
1. MECHANICAL VENTILATION AND ARTIFICIAL LIGHTING WILL BE PROVIDED AT THE BATHROOM/ LAVATORY MARKED WITH " * " FOR OMISSION OF NATURAL LIGHTING AND VENTILATION.
2. ALL DIMENSION ARE SAME AS 5/F – 30/F, EXCEPT OTHERWISE NOTED.
3. SLIDING PANEL TO BE PROVIDED AT WHICH MARKED WITH "#" (REFER TO SLIDING PANEL SCHEDULE DWG. NO. A/GBP/11)
4. LIGHTING AND VENTILATION PROVISION TO ADOPT PERFORMANCE-BASED APPROACH FOR THE ROOM MARKED WITH (##) (REFER DWG. NO. A/GBP/10, A/GBP/10.1)
5. 5 ACH MECHANICAL VENTILATION SHALL BE PROVIDED TO KITCHENS USING UVA METHOD.

LEGEND:

▩ NON-STRUCTURAL PREFABRICATE EXTERNAL WALL (THICKNESS MAX. 150mm)

⬚ COMMON AREA FOR MAINTENANCE

▨ A/C PLATFORM

B.D. Ref : BD 2/4024/21
BIM Ref : - --
F.S.D. Ref : - --
D.L.O. Ref : - --

| Rev. | Description | Drawn | Checked | Approved | Date |
|---|---|---|---|---|---|
| - | 1st Submission | WY | AW | AL | 07/2022 |
| A | 2nd Submission | WY | AW | AL | 11/2022 |
| B | 1st Amendment | TWM | AW | AL | 04/2023 |
| C | 2nd Amendment | TWM | AW | AL | 12/2023 |
| D | 3rd Amendment | TWM | AW | AL | 04/2024 |
| D | 3rd Amendment<br>(Re-submission) | TWM | AW | AL | 05/2024 |
| E | 5th Amendment | TWM | AW | AL | 12/2024 |
| E | 5th Amendment<br>(Re-submission) | TWM | AW | AL | 02/2025 |
| F | 6th Amendment | TWM | AW | AL | 02/2025 |
| G | 8th Amendment | TWM | AW | AL | 05/2025 |
| H | 9th Amendment | TWM | AW | AL | 08/2025 |
| I | 10th Amendment | TWM | AW | AL | 12/2025 |
| J | 11th Amendment | TWM | AW | AL | 02/2026 |
|  |  |  |  |  |  |
|  |  |  |  |  |  |
|  |  |  |  |  |  |

**RONALD LU & PARTNERS**

呂元祥建築師事務所

Check all measurements on site. Do not scale off drawings.
This drawing is to be read in conjunction with the specification and any discrepancies are to be immediately reported to the Architect.
This drawing remains the copyright property of the Architect and is not to be reproduced in whole or in part without permission of the Architect.

Project Title :
PROPOSED DEVELOPMENT
AT BAILEY STREET
& WING KWONG STREET
TO KWA WAN, KOWLOON

Drawing Title :
3RD FLOOR PLAN
FOR TOWER 1 & TOWER 2

|  |  |  |  |
|---|---|---|---|
| Drawn By | TWM | Date | 08/2025 |
| Checked By | AW | Date | 08/2025 |
| Approved By | AL | Date | 08/2025 |
| Project No. | 21163KL | Issue Date | 08/2025 |

File Path :
U:\Studio_B\Proj_Data\2021\21163KL_Bailey Street & Wing Kwong Street\DRAWING\SUB\BD\GBP_13 (Final Amendment)_Hand Amend\PLOT_FS\A_GBP_11.dwg

Scale 1:100 By CAD

Drawing Number : A/GBP/11
Revision Number : J

Drawing Purpose

**Fire Services Department**
Amended Plan

FIRE SERVICE REQUIRE-
MENTS INCORPORATED
Date: 12 JUN 2026
(LEUNG KA HAY)
SStnO(NP)