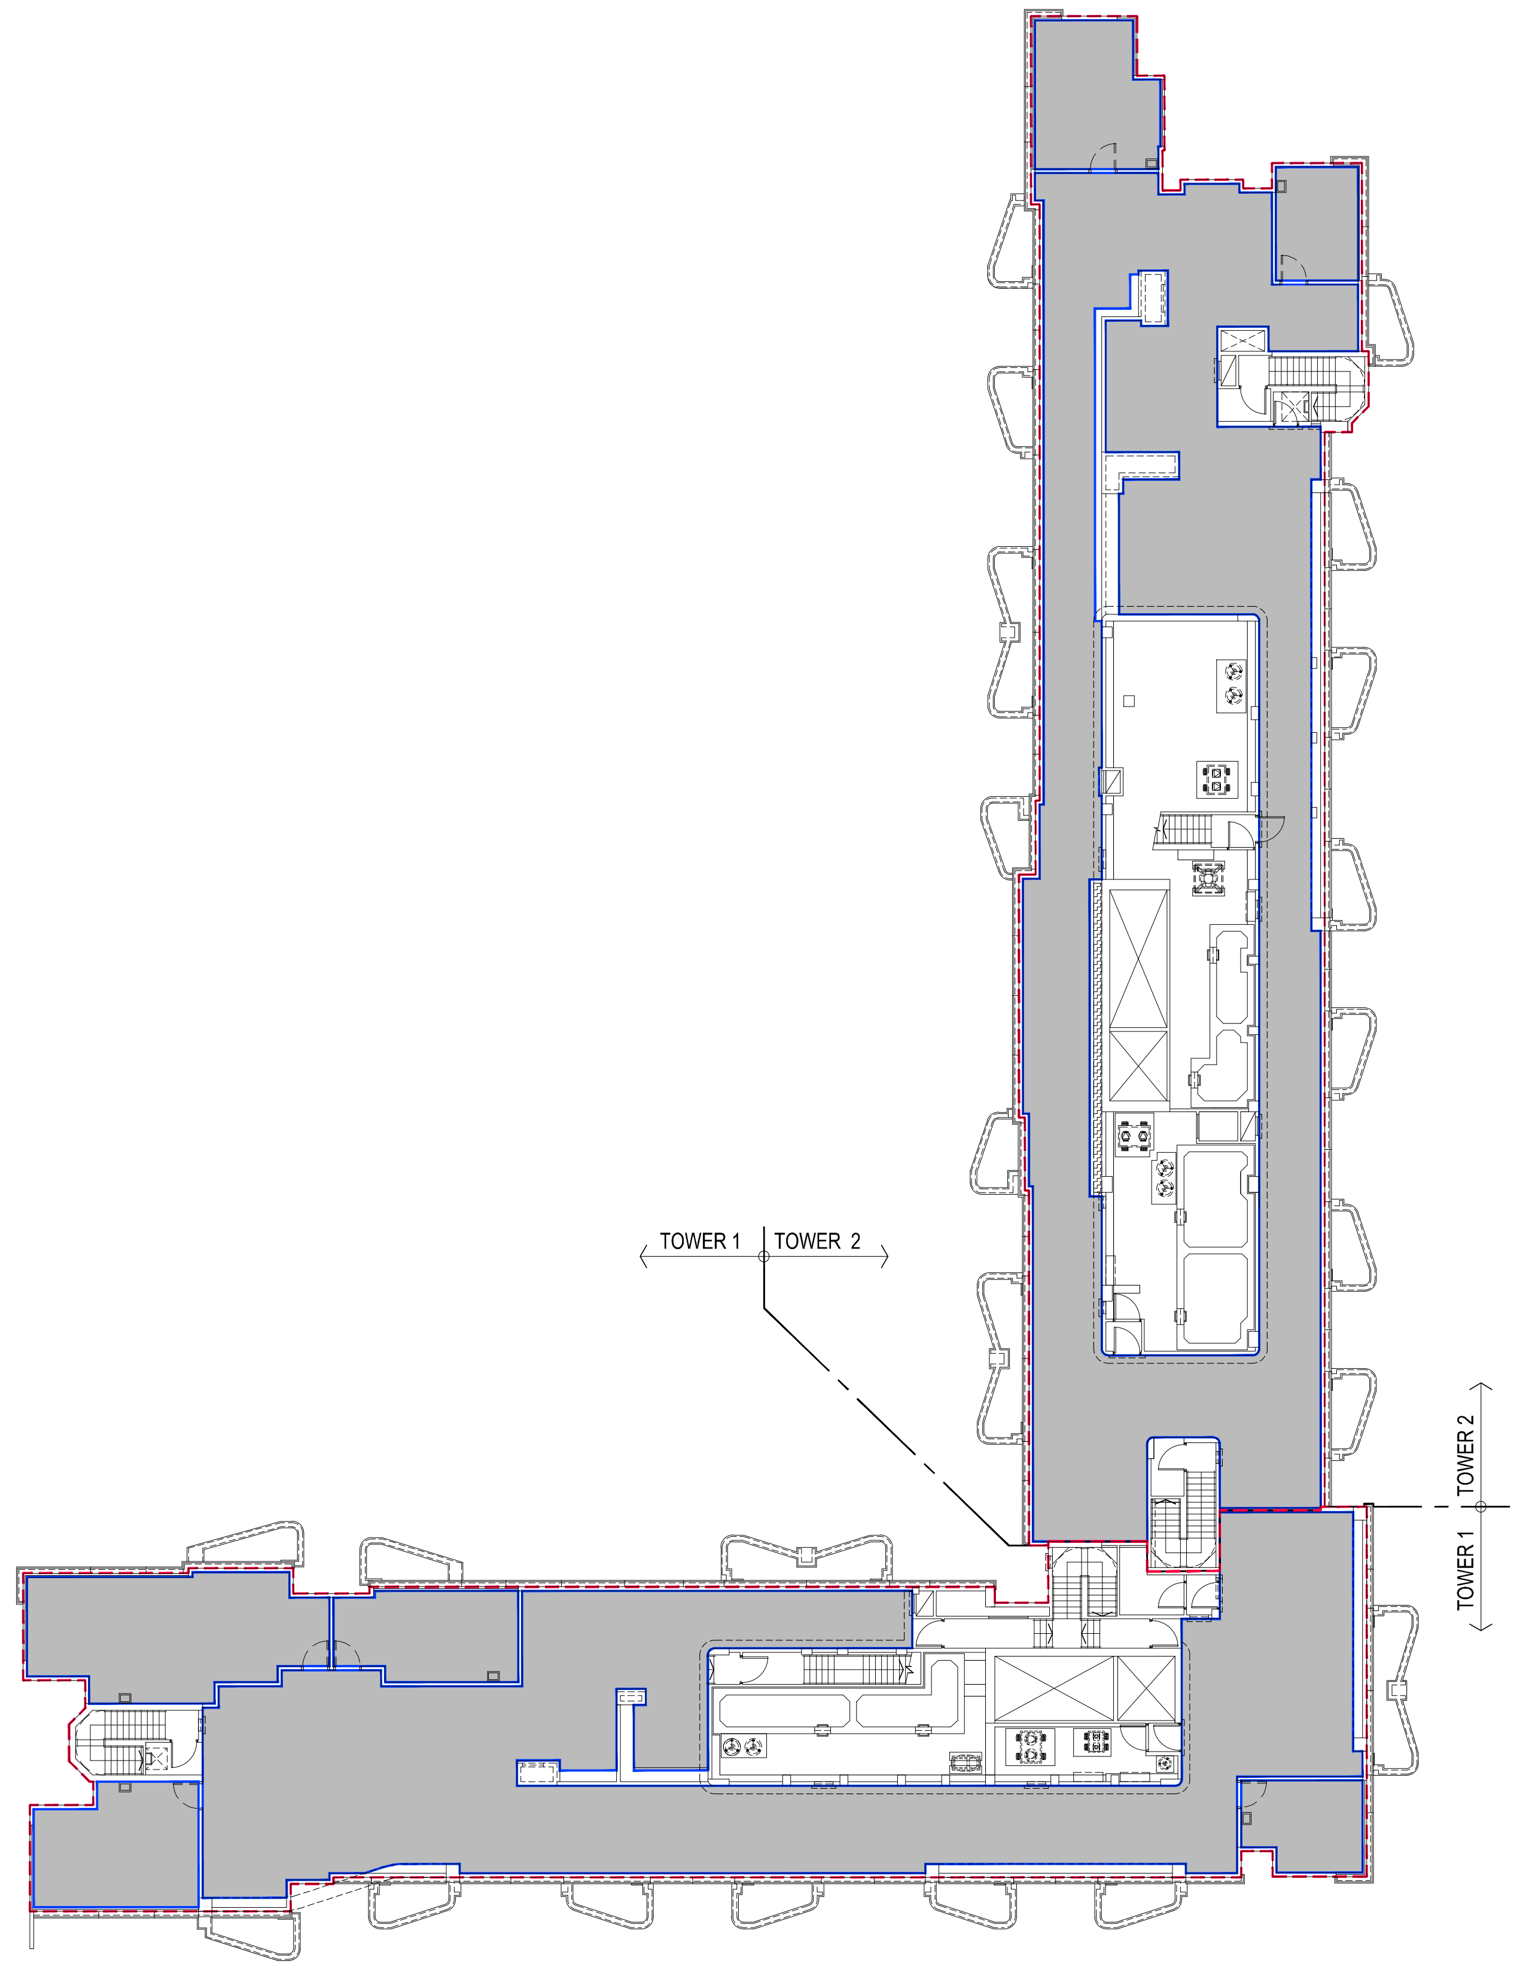

TOWER 1 & TOWER 2 ROOF FLOOR DIAGRAM

(UNDER PLANNING DEPARTMENT)
SCALE 1:200

	TOWER 1	TOWER 2
— — AREA OF ROOF	576.291 m²	600.794 m²
▨ AREA OF ROOF W/O. ROOF TOP STRUCTURE	400.750 m² (69.540 % OF ROOF AREA)	360.058 m² (59.930 % OF ROOF AREA)

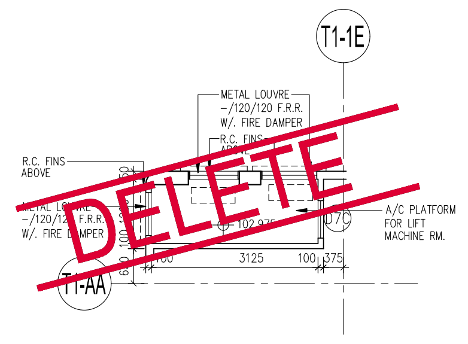

PART PLAN AT LEVEL 102.975

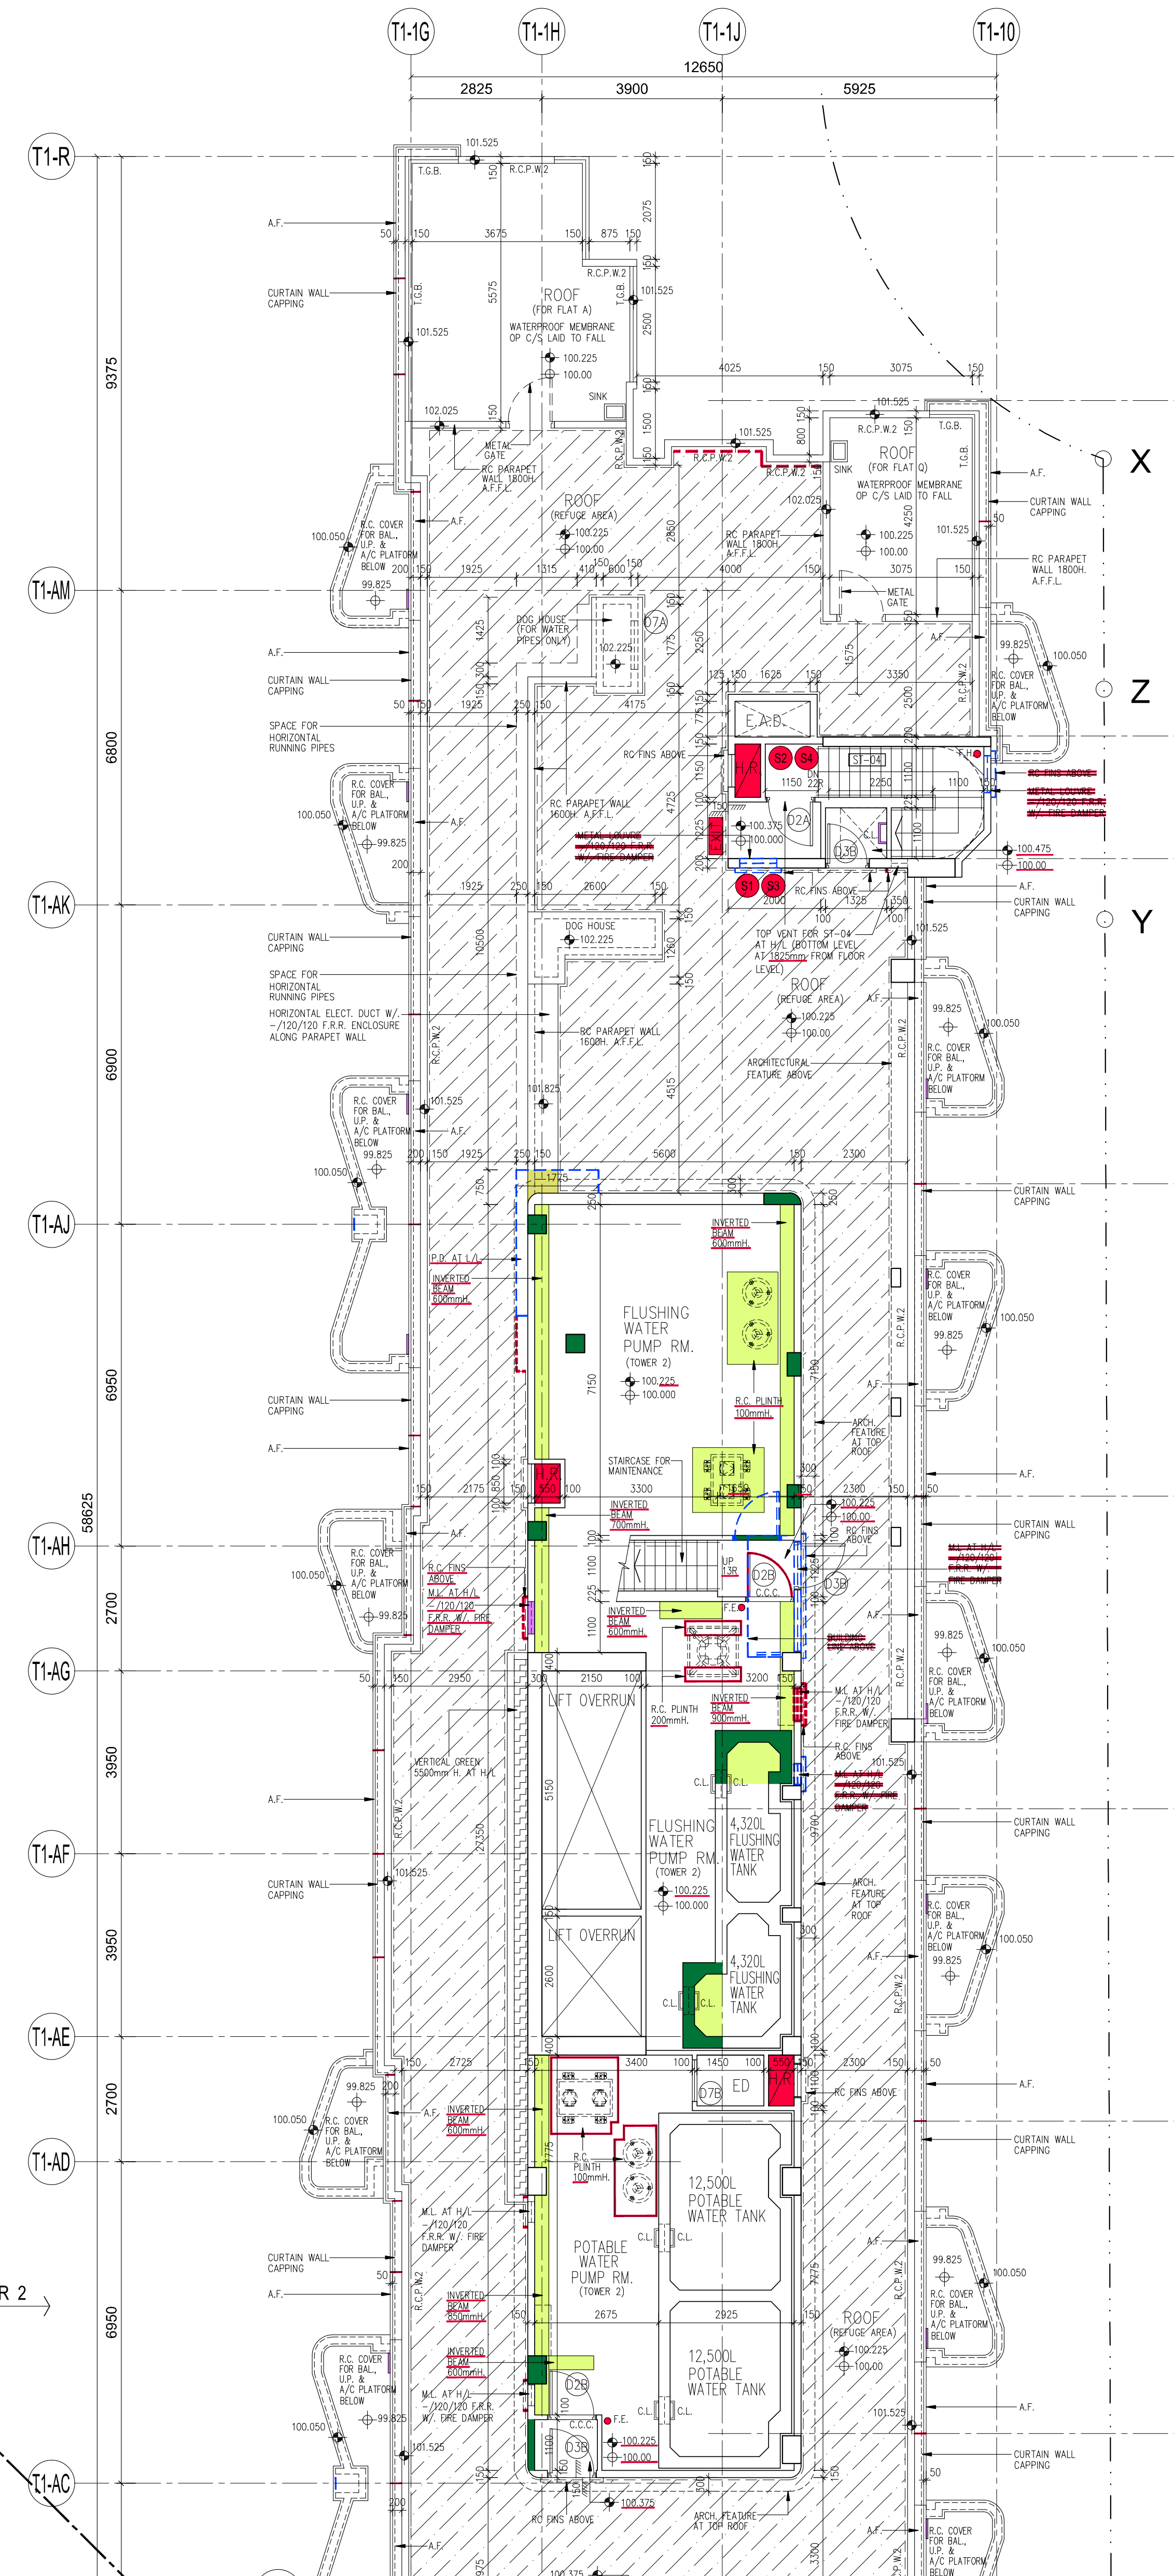

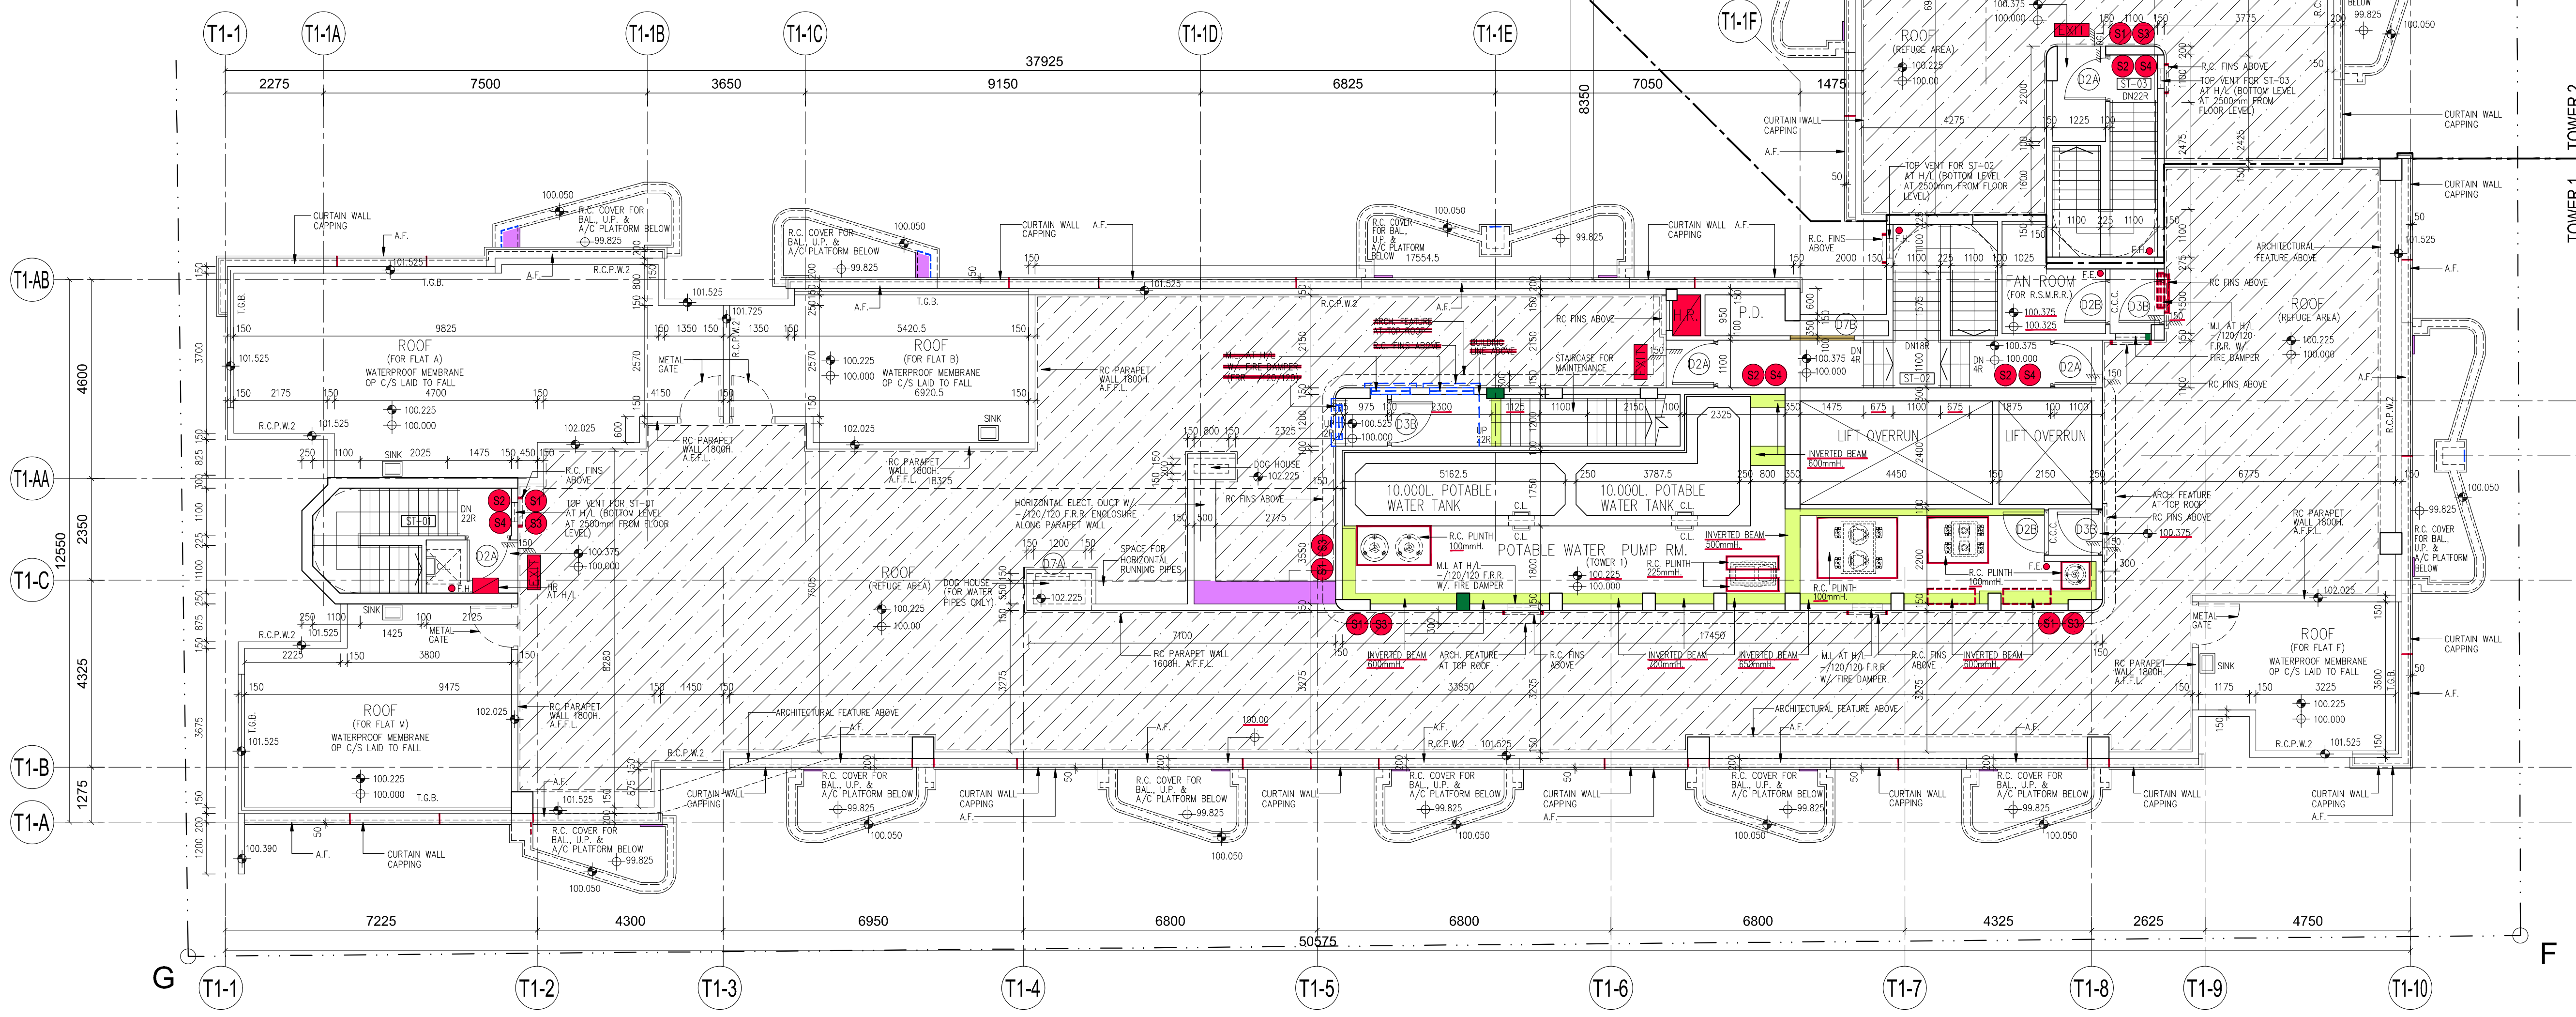

ROOF PLAN – TOWER 1 & TOWER 2

LEGEND:

S1	REFUGE FLOOR NOTICE
S2	STAIR NO. SIGN
S3	DIRECTIONAL SIGN TO EXIT STAIRCASE
S4	A SIGN INDICATING THE ENTRANCE TO THE REFUGE FLOOR
▨	NET REFUGE AREA : TOWER 1 = 282.767 m², TOWER 2 = 310.287 m²

THE PERCENTAGE OF THE NET REFUGE AREA

	TOWER 1	TOWER 2
THE G.F.A. OF THE LARGEST FLOOR PLATE	561.518 m²	608.058 m²2
PERCENTAGE OF REFUGE AREA PROVIDED	282.767 / 561.518 x 100% 50.358 % > 50% (REQUIRED)	310.287 / 608.058 x 100% 51.029 % > 50% (REQUIRED)

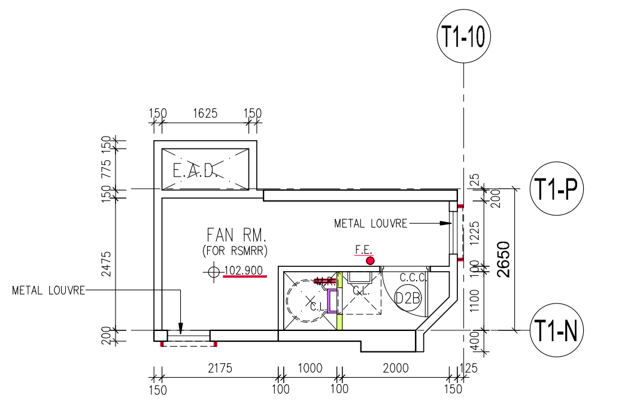

PART PLAN AT LEVEL 102.90

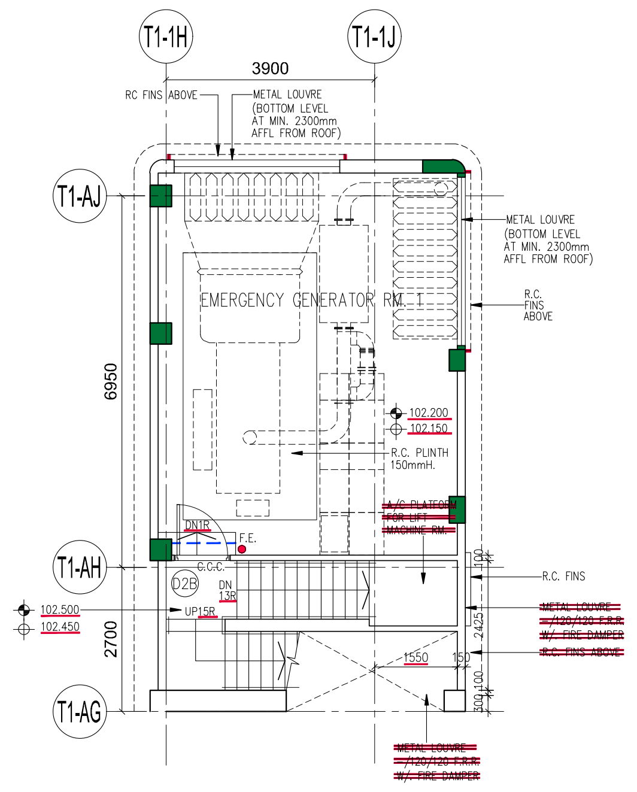

PART PLAN AT LEVEL 102.150

B.D. Ref : BD 2/4024/21
BIM Ref : - --
F.S.D. Ref : - --
D.L.O. Ref : - --

Rev.	Description	Drawn	Checked	Approved	Date
-	1st Submission	WY	AW	AL	07/2022
A	2nd Submission	WY	AW	AL	11/2022
B	1st Amendment	TWM	AW	AL	04/2023
C	2nd Amendment	TWM	AW	AL	12/2023
D	3rd Amendment	TWM	AW	AL	04/2024
D	3rd Amendment	TWM	AW	AL	05/2024
	(Re-submission)				
E	5th Amendment	TWM	AW	AL	12/2024
E	5th Amendment	TWM	AW	AL	02/2025
	(Re-submission)				
F	8th Amendment	TWM	AW	AL	05/2025
G	9th Amendment	TWM	AW	AL	08/2025
H	10th Amendment	TWM	AW	AL	12/2025
I	11th Amendment	TWM	AW	AL	02/2026

RONALD LU & PARTNERS
呂 元 祥 建 築 師 事 務 所

Check all measurements on site. Do not scale off drawings.
This drawing is to be read in conjunction with the specification and any discrepancies are to be immediately reported to the Architect.
This drawing remains the copyright property of the Architect and is not to be reproduced in whole or in part without permission of the Architect.

Project Title :
PROPOSED DEVELOPMENT
AT BAILEY STREET
& WING KWONG STREET
TO KWA WAN, KOWLOON

Drawing Title :
ROOF FLOOR PLAN
FOR TOWER 1 & TOWER 2

Drawn By	TWM	Date	08/2025
Checked By	AW	Date	08/2025
Approved By	AL	Date	08/2025
Project No.	21163KL	Issue Date	08/2025

File Path :
U:\Studio_B\Proj_Data\2021\21163KL_Bailey Street & Wing Kwong Street\DRAWING\SUB\BD\GBP_13 (Final Amendment)_Hand Amend\PLOT_FS\A_GBP_13.dwg

Scale 1:100 By CAD

Drawing Number : A/GBP/13
Revision Number : I

Drawing Purpose
Fire Services Department
Amended Plan

FIRE SERVICE REQUIRE-
MENTS INCORPORATED
Date: 12 JUN 2026
(LEUNG KA HAY)
SStnO(NP)