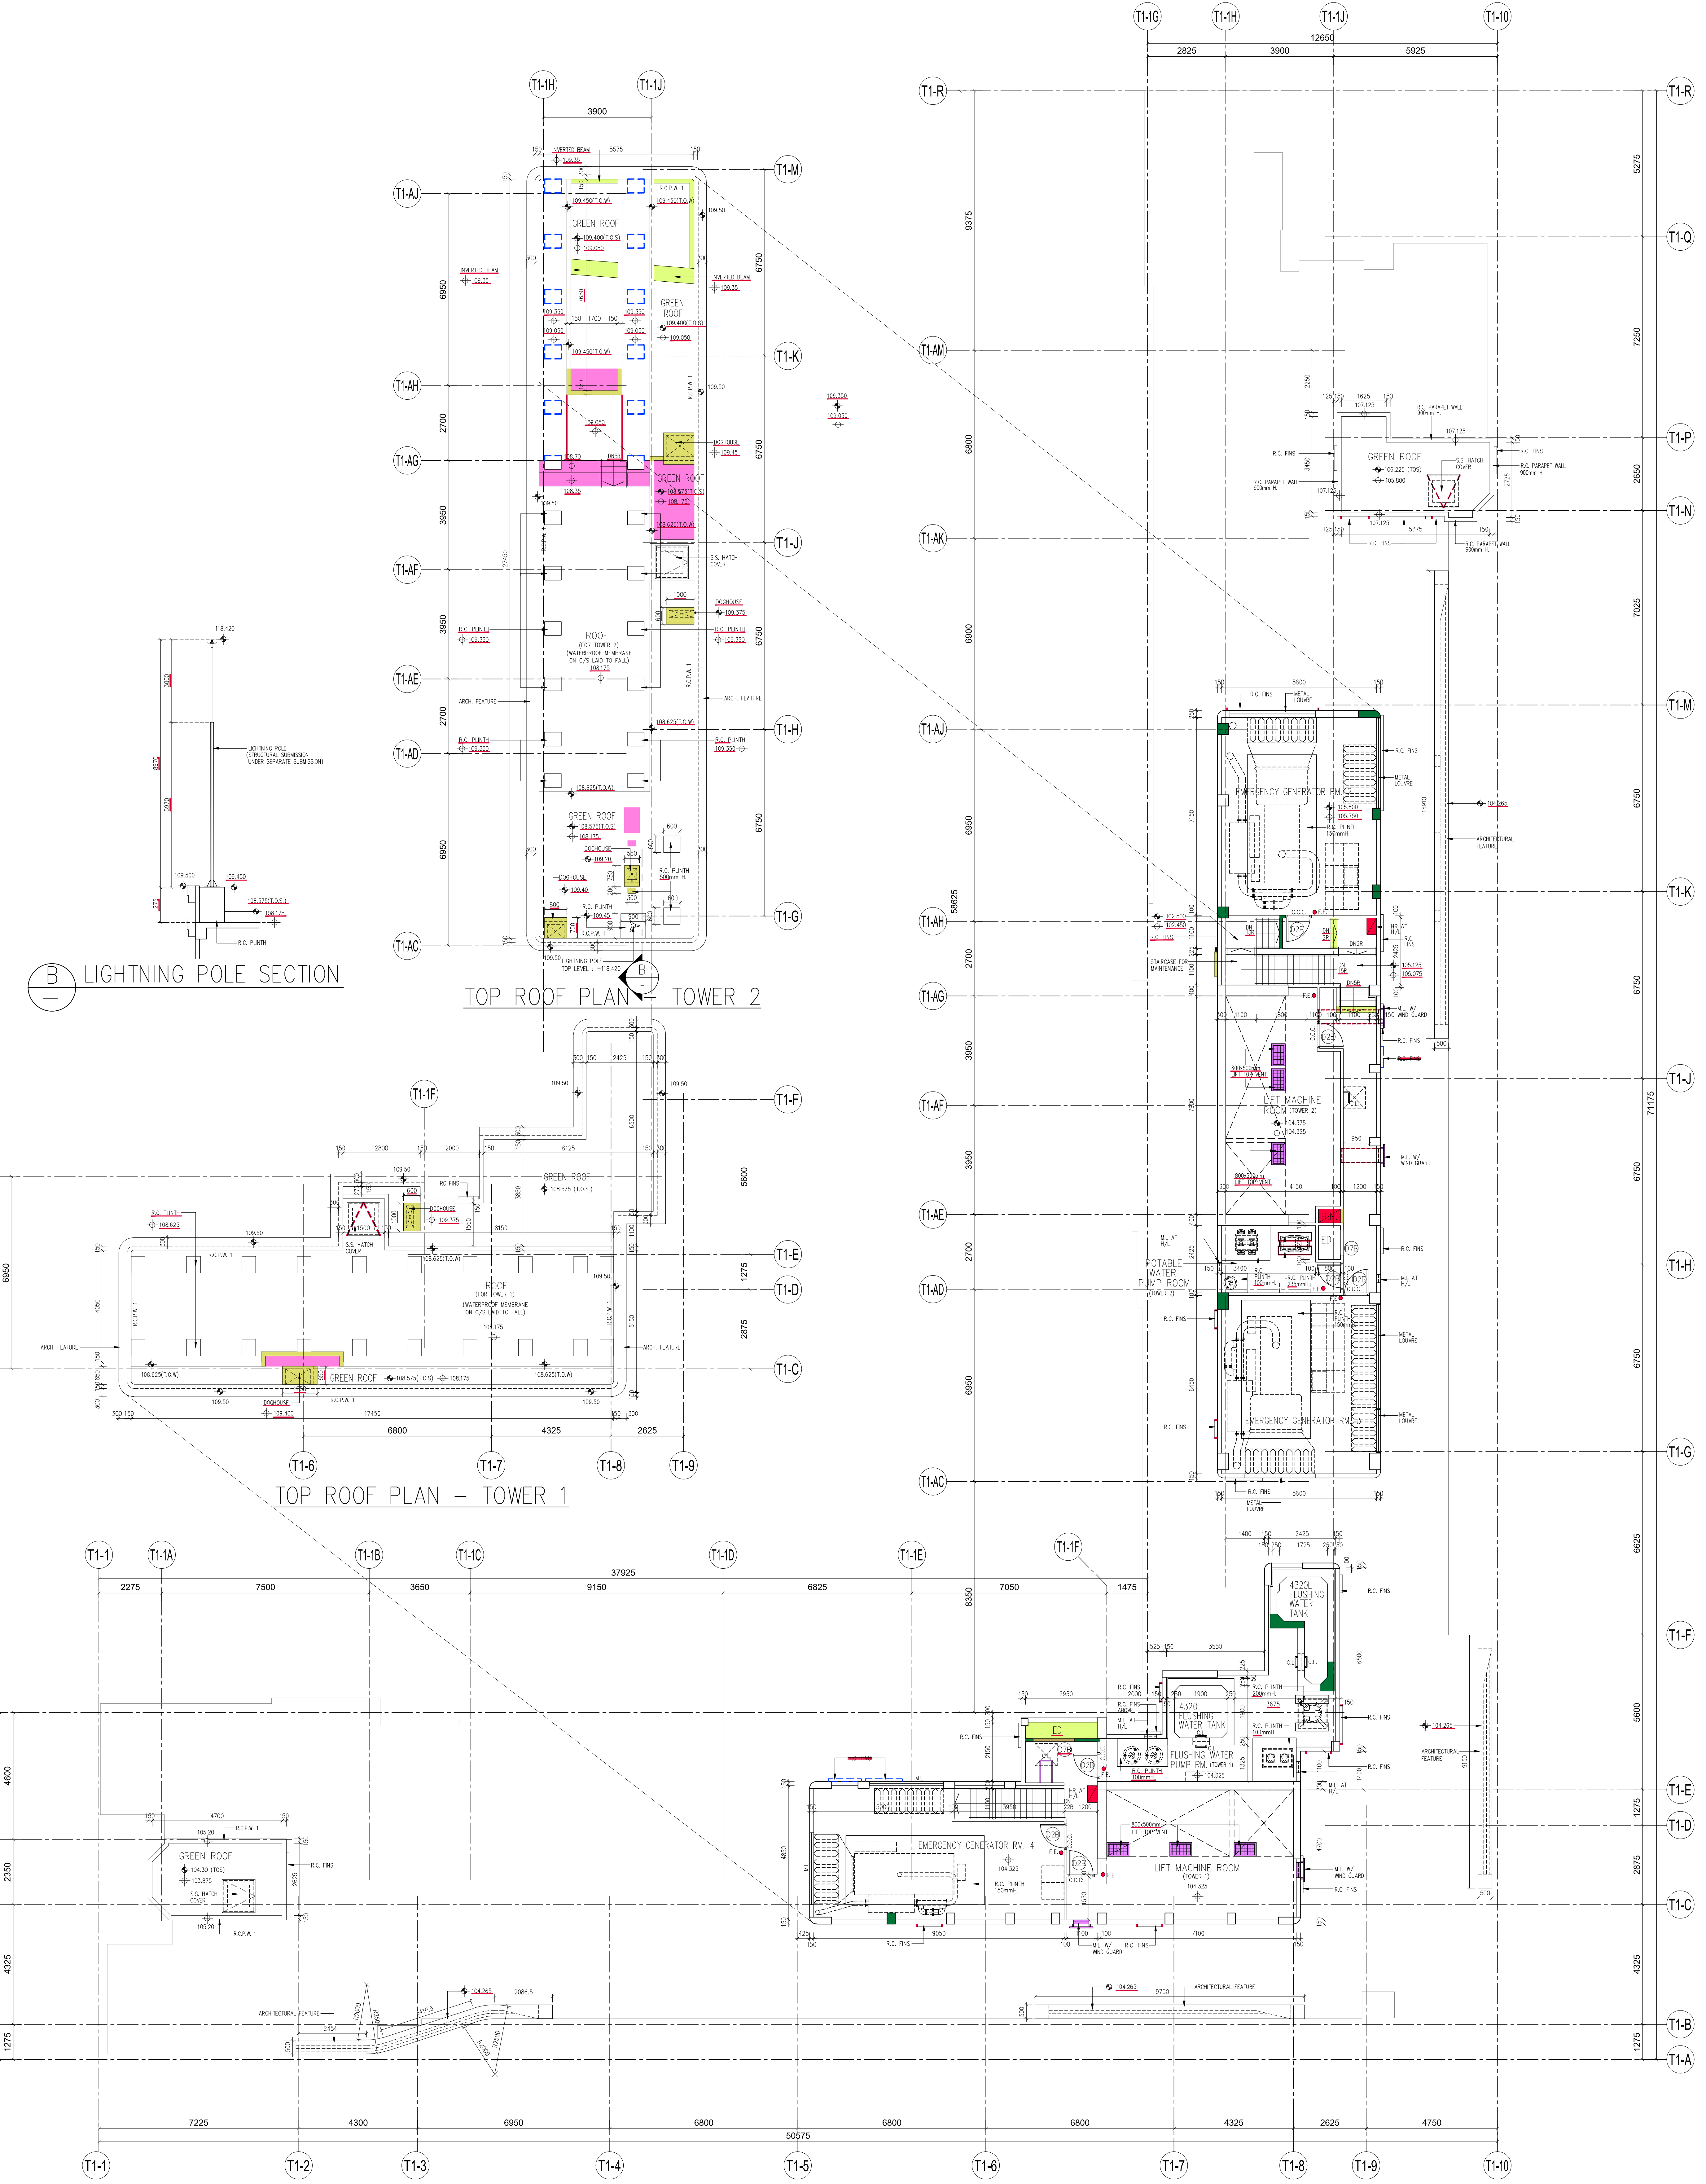
T1-1
T1-1A
T1-1B
T1-1C
T1-1D
T1-1E
T1-1F
T1-1G
T1-1H
T1-1J
T1-2
T1-3
T1-4
T1-5
T1-6
T1-7
T1-8
T1-9
T1-10
T1-A
T1-B
T1-C
T1-D
T1-E
T1-F
T1-G
T1-H
T1-J
T1-K
T1-M
T1-N
T1-P
T1-Q
T1-R
T1-AA
T1-AB
T1-AC
T1-AD
T1-AE
T1-AF
T1-AG
T1-AH
T1-AJ
T1-AK
T1-AM
37925
50575
12650
71175
GREEN ROOF
ROOF (FOR TOWER 2) (WATERPROOF MEMBRANE ON C/S LAID TO FALL)
ROOF (FOR TOWER 1) (WATERPROOF MEMBRANE ON C/S LAID TO FALL)
EMERGENCY GENERATOR RM.
LIFT MACHINE ROOM (TOWER 2)
POTABLE WATER PUMP ROOM (TOWER 2)
STAIRCASE FOR MAINTENANCE
43200L FLUSHING WATER TANK
FLUSHING WATER PUMP RM (TOWER 1)
EMERGENCY GENERATOR RM. 4
LIFT MACHINE ROOM (TOWER 1)
R.C. FINS
METAL LOUVRE
ARCH. FEATURE
ARCHITECTURAL FEATURE
R.C. PARAPET WALL
S.S. HATCH COVER
R.C. PLINTH
DOGHOUSE
LIGHTNING POLE (STRUCTURAL SUBMISSION UNDER SEPARATE SUBMISSION)
119.420

B LIGHTNING POLE SECTION

TOP ROOF PLAN – TOWER 2

TOP ROOF PLAN – TOWER 1

UPPER ROOF PLAN – TOWER 1 & TOWER 2

B.D. Ref : BD 2/4024/21
BIM Ref : - --
F.S.D. Ref : - --
D.L.O. Ref : - --

Rev.	Description	Drawn	Checked	Approved	Date
-	1st Submission	WY	AW	AL	07/2022
A	2nd Submission	WY	AW	AL	11/2022
B	1st Amendment	TWM	AW	AL	04/2023
C	2nd Amendment	TWM	AW	AL	12/2023
D	3rd Amendment	TWM	AW	AL	04/2024
D	3rd Amendment (Re-submission)	TWM	AW	AL	05/2024
E	5th Amendment	TWM	AW	AL	12/2024
E	5th Amendment (Re-submission)	TWM	AW	AL	02/2025
F	8th Amendment	TWM	AW	AL	05/2025
G	9th Amendment	TWM	AW	AL	08/2025
G	9th Amendment (Re-submission)	TWM	AW	AL	10/2025
H	10th Amendment	TWM	AW	AL	12/2025
I	11th Amendment	TWM	AW	AL	02/2026

RONALD LU & PARTNERS

呂 元 祥 建 築 師 事 務 所

Check all measurements on site. Do not scale off drawings.
This drawing is to be read in conjunction with the specification and any discrepancies are to be immediately reported to the Architect.
This drawing remains the copyright property of the Architect and is not to be reproduced in whole or in part without permission of the Architect.

Project Title :
PROPOSED DEVELOPMENT
AT BAILEY STREET
& WING KWONG STREET
TO KWA WAN, KOWLOON

Drawing Title :
UPPER ROOF FLOOR PLAN
FOR TOWER 1 & TOWER 2

Drawn By	TWM	Date	08/2025
Checked By	AW	Date	08/2025
Approved By	AL	Date	08/2025
Project No.	21163KL	Issue Date	08/2025

File Path :
U:\Studio_B\Proj_Data\2021\21163KL_Bailey Street & Wing Kwong Street\DRAWING\SUB\BD\GBP_13 (Final Amendment)_Hand Amend (FSD)\PLOT_FS\A_GBP_14.dwg

Scale 1:100 By CAD

Drawing Number : A/GBP/14
Revision Number : I

Drawing Purpose
Fire Services Department
Amended Plan

FIRE SERVICE REQUIRE-
MENTS INCORPORATED
Date: 12 JUN 2026
(LEUNG KA HAY)
SStnO(NP)