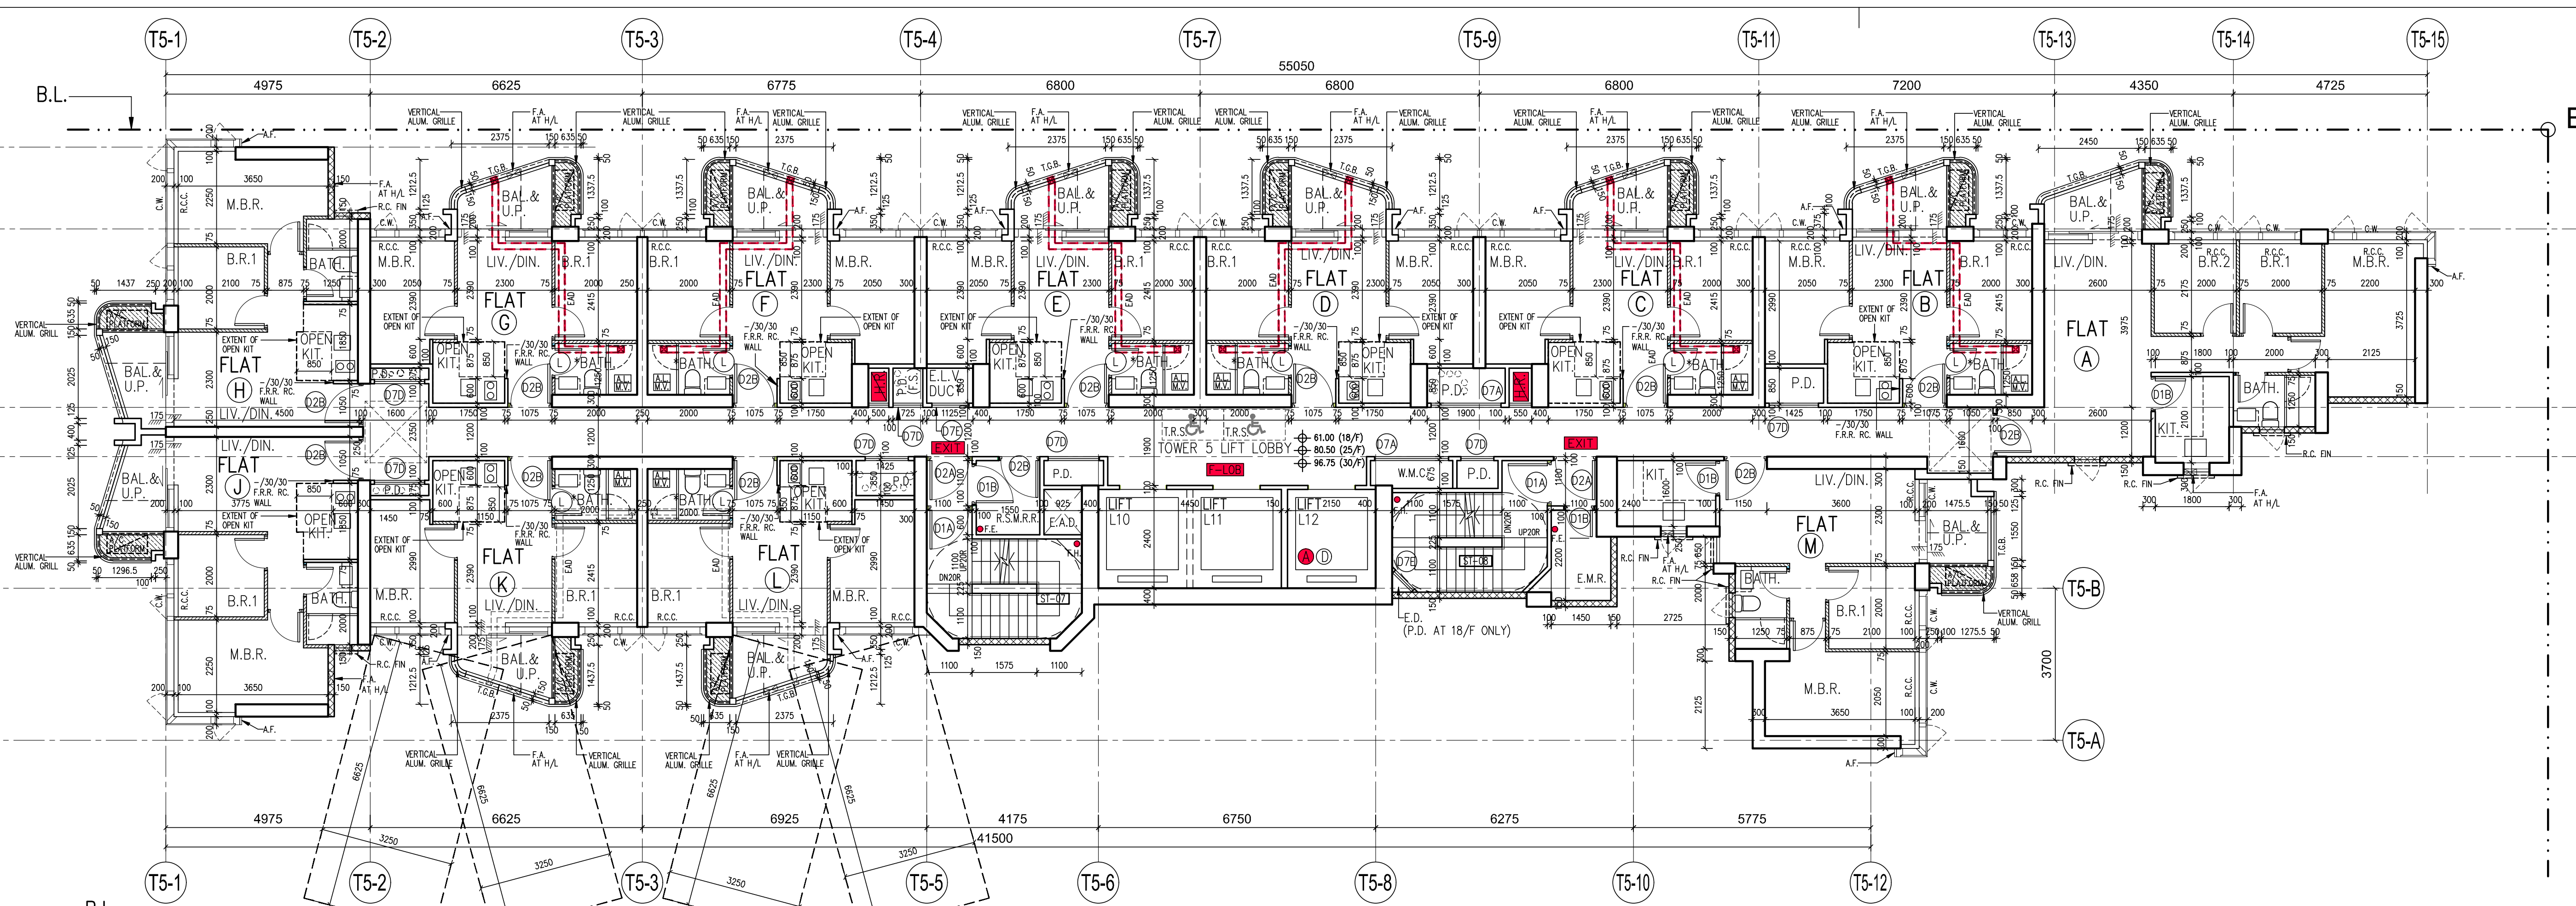

18th TO 30th FLOOR PLAN – TOWER 5
(12 STOREYS)

UNDER BUILDING (PLANNING) REG. 31
LEVEL OF MAIN ROOF PARAPET : 101.725
LEVEL OF WINDOW SILL AT 18/F : 62.00
REQUIRED LENGTH OF HORIZONTAL PLANE
= (101.725 – 62.00) / 6 = 6.621
HORIZONTAL PLANE AREA PROVIDED
= 6.625 x 3.250 =21.531 > 21 m² (REQUIRED)

NOTE:
1. MECHANICAL VENTILATION AND ARTIFICIAL LIGHTING WILL BE PROVIDED AT THE BATHROOM/ LAVATORY MARKED WITH " * " FOR OMISSION OF NATURAL LIGHTING AND VENTILATION.
2. THERE WILL BE NO 13/F, 14/F & 24/F IN THE NOMENCLATURE SYSTEM FOR NUMBERING OF FLOORS.

LEGEND:
▨ A/C PLATFORM

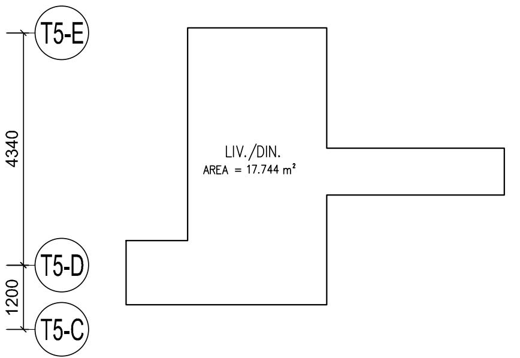
LIV./DIN.
AREA = 17.744 m²

3/F – 30/F FLAT A (LIV./DIN.) ROOM AREA

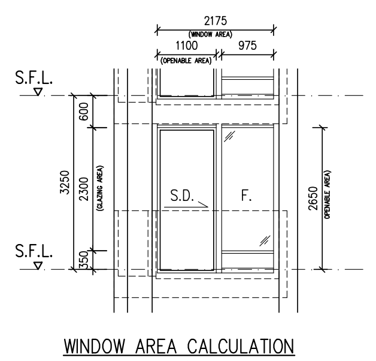

WINDOW AREA CALCULATION
FOR FLAT A (LIV./DIN.)
(FOR FLAT B TO H, J TO M (LIV./DIN.))
ROOM AREA = 17.744 s.m.
WINDOW AREA REQ'D = 17.744 / 10 = 1.774 s.m.
WINDOW AREA PROV'D = (2.175 x 2.300 x 0.70)
= 3.502 s.m. > 1.774 s.m. (REQUIRED)
OPENABLE WINDOW AREA REQ'D = 17.744 /16 = 1.109 s.m.
OPENABLE WINDOW AREA PROV'D = 1.100 x 2.650 x 0.70
= 2.041 s.m. > 1.109 s.m. (REQUIRED)

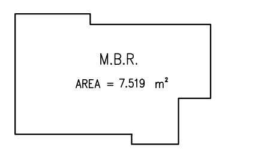
M.B.R.
AREA = 7.519 m²

3/F – 30/F FLAT H (M.B.R.) AREA

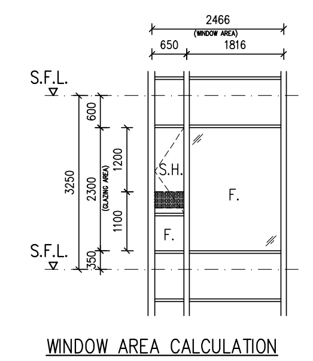

WINDOW AREA CALCULATION
FOR FLAT H (M.B.R.)
(FOR FLAT A TO G, J TO M (M.B.R.))
ROOM AREA = 7.519 s.m.
WINDOW AREA REQ'D = 7.519 / 10 = 0.752 s.m.
WINDOW AREA PROV'D = 2.466 x 2.300 x 0.70
= 3.970 s.m. > 0.752 s.m. (REQUIRED)
OPENABLE WINDOW AREA REQ'D = 7.519 /16 = 0.470 s.m.
OPENABLE WINDOW AREA PROV'D = 0.65 x 1.200 x 0.70
= 0.546 s.m. > 0.470 s.m. (REQUIRED)

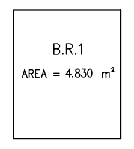
B.R.1
AREA = 4.830 m²

3/F – 30/F FLAT B (B.R.1) ROOM AREA

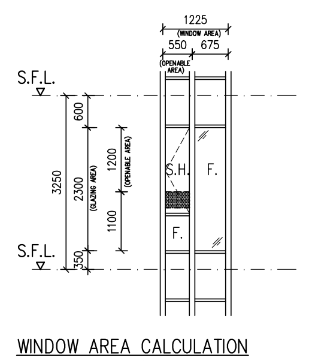

WINDOW AREA CALCULATION
FOR FLAT B (B.R.1)
(FOR FLAT A, C TO G, J TO M (B.R.1))
ROOM AREA = 4.830 s.m.
WINDOW AREA REQ'D = 4.830 / 10 = 0.483 s.m.
WINDOW AREA PROV'D = (1.225 x 2.300 x 0.70)
= 1.972 s.m. > 0.483 s.m. (REQUIRED)
OPENABLE WINDOW AREA REQ'D = 4.830 /16 = 0.302 s.m.
OPENABLE WINDOW AREA PROV'D = (0.550 x 1.200 x 0.70)
= 0.462 s.m. > 0.302 s.m. (REQUIRED)

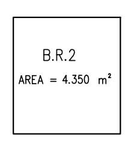
B.R.2
AREA = 4.350 m²

3/F – 30/F FLAT A (B.R.2) ROOM AREA

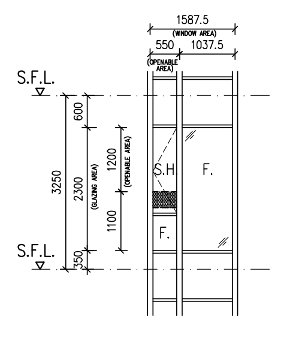

WINDOW AREA CALCULATION
FOR FLAT A (B.R.2)
ROOM AREA = 4.350 s.m.
WINDOW AREA REQ'D = 4.350 / 10 = 0.435 s.m.
WINDOW AREA PROV'D = (1.5875 x 2.300 x 0.70)
= 2.556 s.m. > 0.435 s.m. (REQUIRED)
OPENABLE WINDOW AREA REQ'D = 4.350 /16 = 0.272 s.m.
OPENABLE WINDOW AREA PROV'D = (0.550 x 1.200 x 0.70)
= 0.462 s.m. > 0.272 s.m. (REQUIRED)

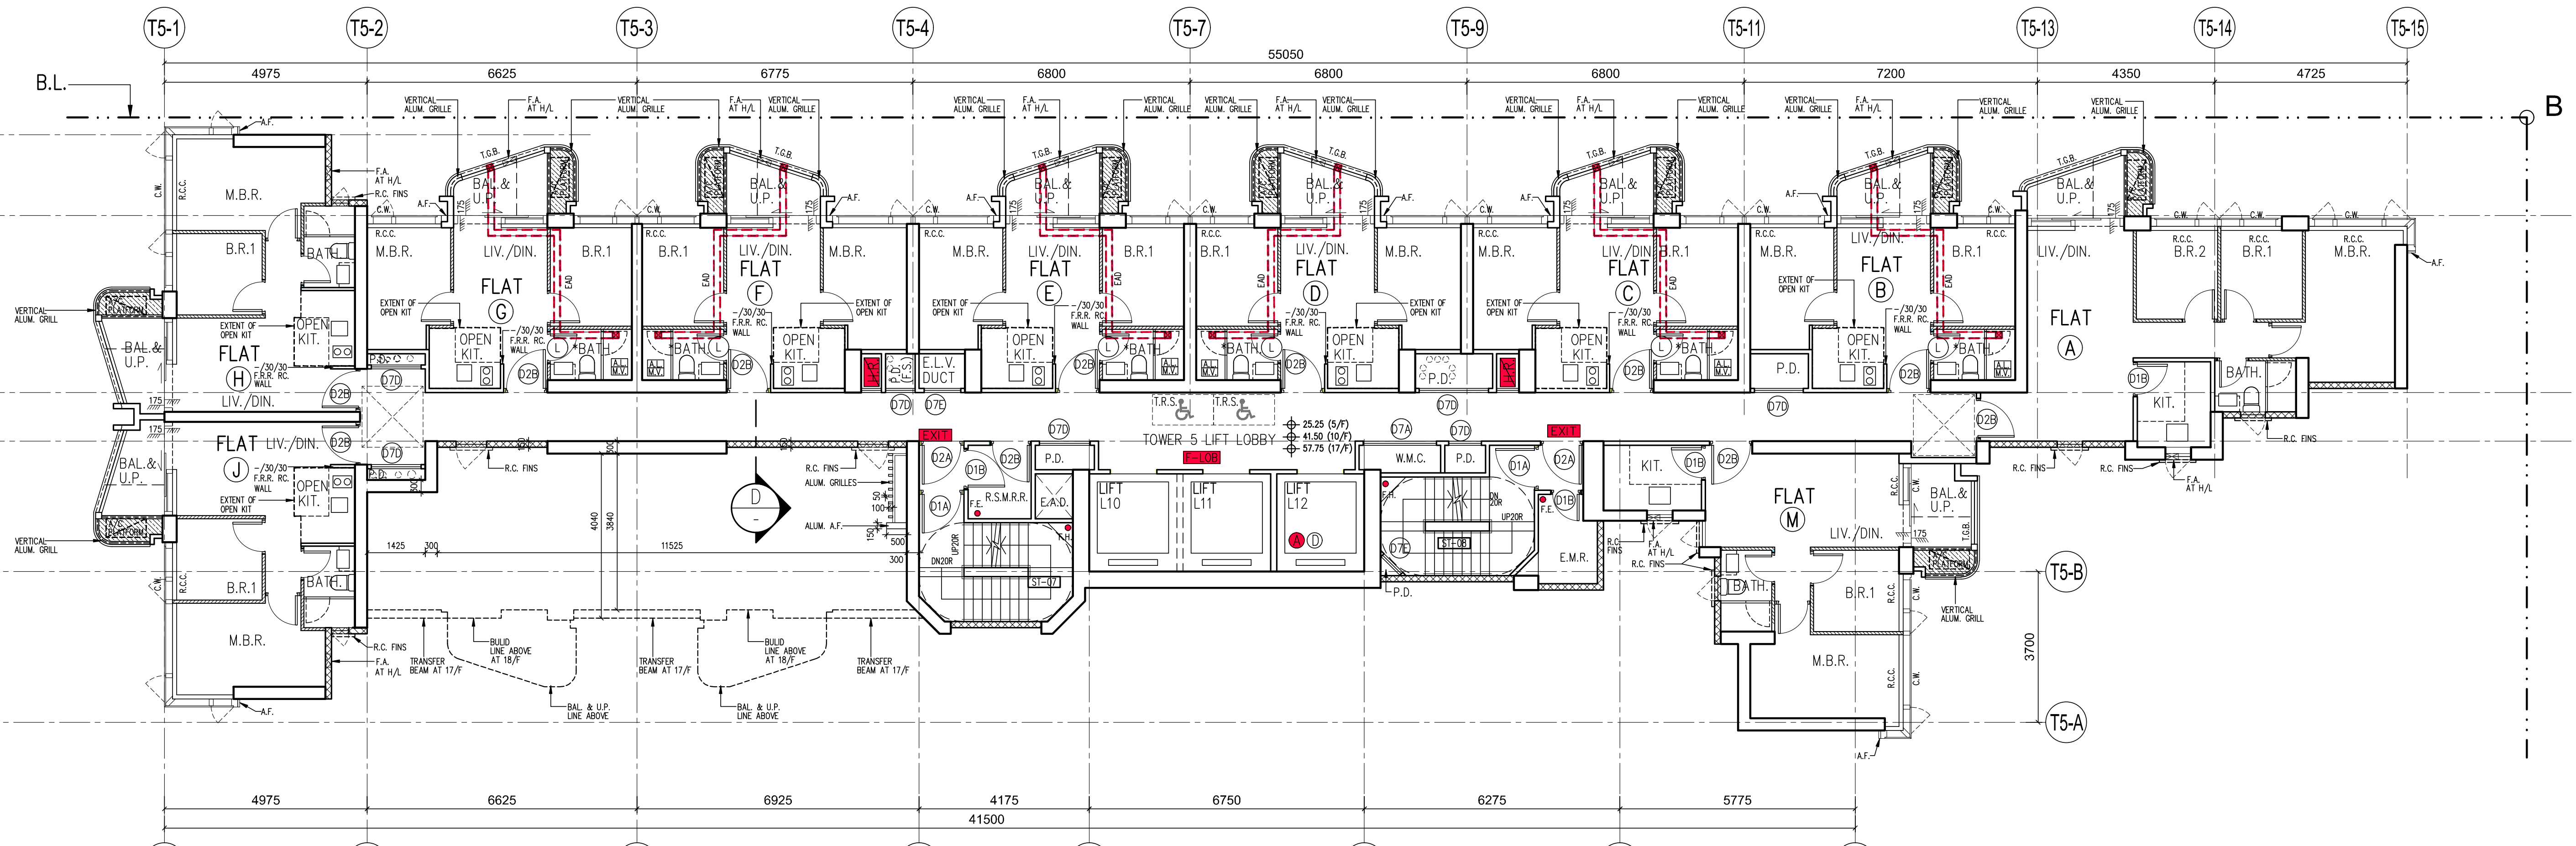

5th TO 17th FLOOR PLAN – TOWER 5
(11 STOREYS)

NOTE:
1. MECHANICAL VENTILATION AND ARTIFICIAL LIGHTING WILL BE PROVIDED AT THE BATHROOM/ LAVATORY MARKED WITH " * " FOR OMISSION OF NATURAL LIGHTING AND VENTILATION.
2. THERE WILL BE NO 13/F, 14/F & 24/F IN THE NOMENCLATURE SYSTEM FOR NUMBERING OF FLOORS.

LEGEND:
▨ A/C PLATFORM

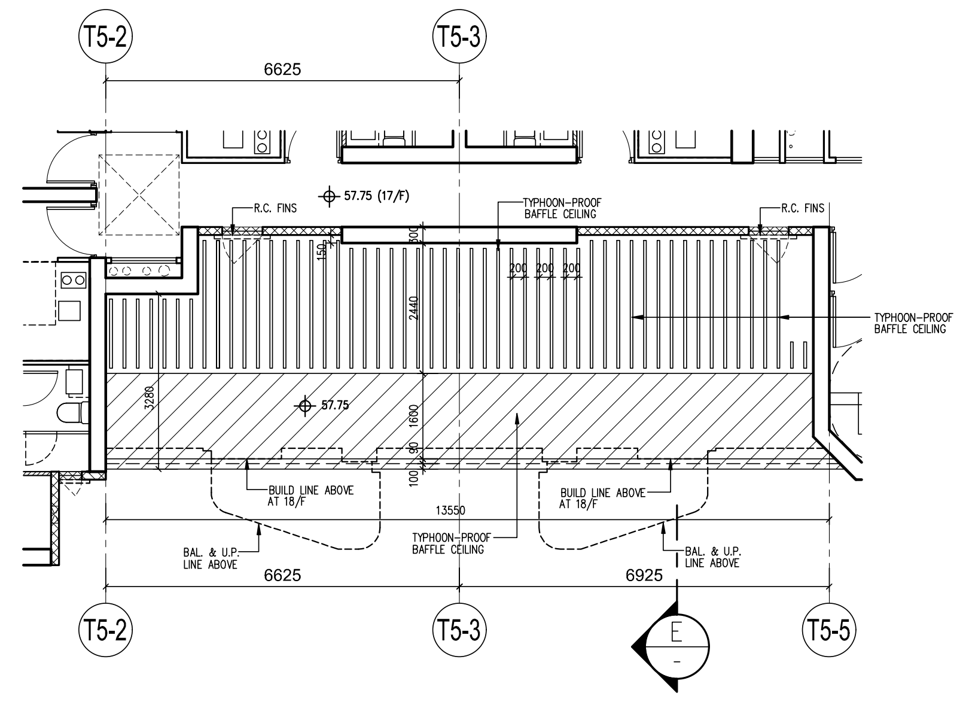

PART PLAN AT 17th FLOOR PLAN – TOWER 5

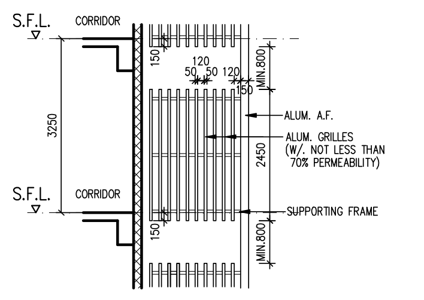
S.F.L.
CORRIDOR
3250
ALUM. A.F.
ALUM. GRILLES (W/. NOT LESS THAN 70% PERMEABILITY)
2450
SUPPORTING FRAME
MIN.800

D – TYPICAL DETAIL OF ALUM. GRILLES. FOR SCREENING OF EXTERNAL PIPES AT T2

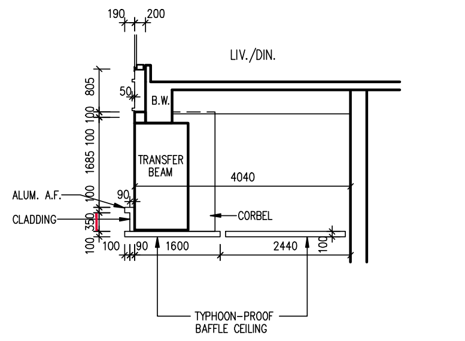
LIV./DIN.
B.W.
TRANSFER BEAM
4040
ALUM. A.F.
CLADDING
CORBEL
TYPHOON–PROOF BAFFLE CEILING

E – TYPICAL DETAIL OF CLADDING & TYPHOON–PROOF BAFFLE CEILING
(STRUCTURAL SUBMISSION UNDER SEPARATE SUBMISSION)

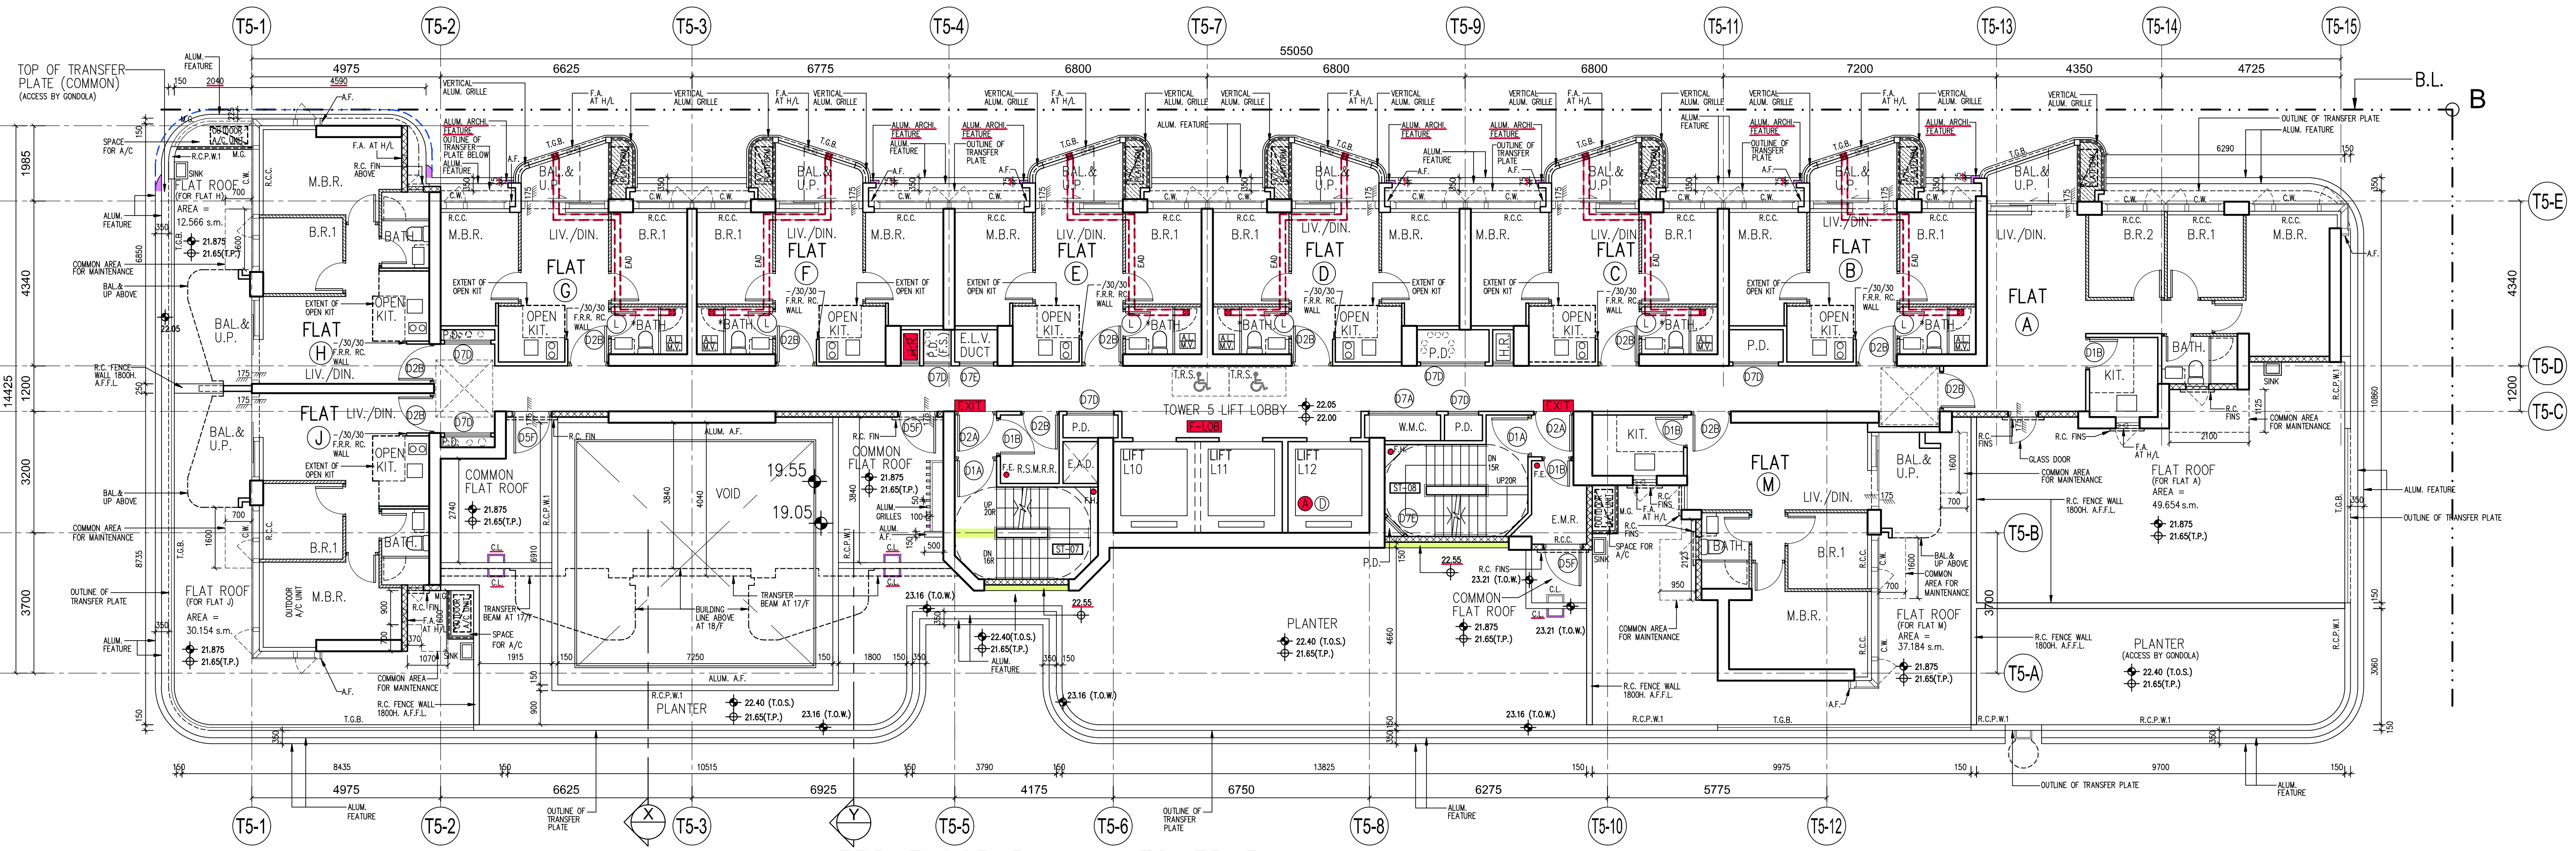

3RD FLOOR PLAN – TOWER 5

NOTE:
1. MECHANICAL VENTILATION AND ARTIFICIAL LIGHTING WILL BE PROVIDED AT THE BATHROOM/ LAVATORY MARKED WITH " * " FOR OMISSION OF NATURAL LIGHTING AND VENTILATION.
2. ALL DIMENSION ARE SAME AS 5/F – 30/F, EXCEPT OTHERWISE NOTED.

LEGEND:
▨ A/C PLATFORM

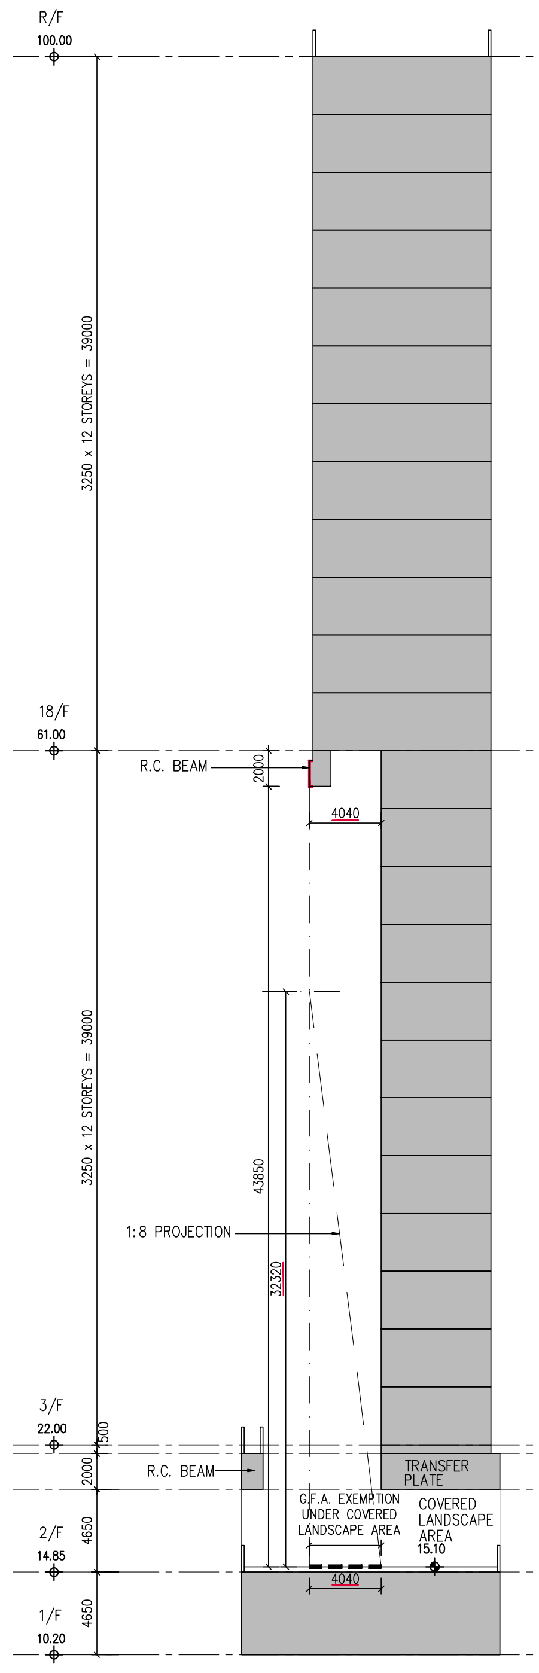
R/F
100.00
18/F
61.00
R.C. BEAM
1:8 PROJECTION
3/F
22.00
2/F
14.85
1/F
10.20
TRANSFER PLATE
G.F.A. EXEMPTION UNDER COVERED LANDSCAPE AREA
COVERED LANDSCAPE AREA
15.10
4040

DIAGRAMMATIC SECTION X
SCALE 1:300

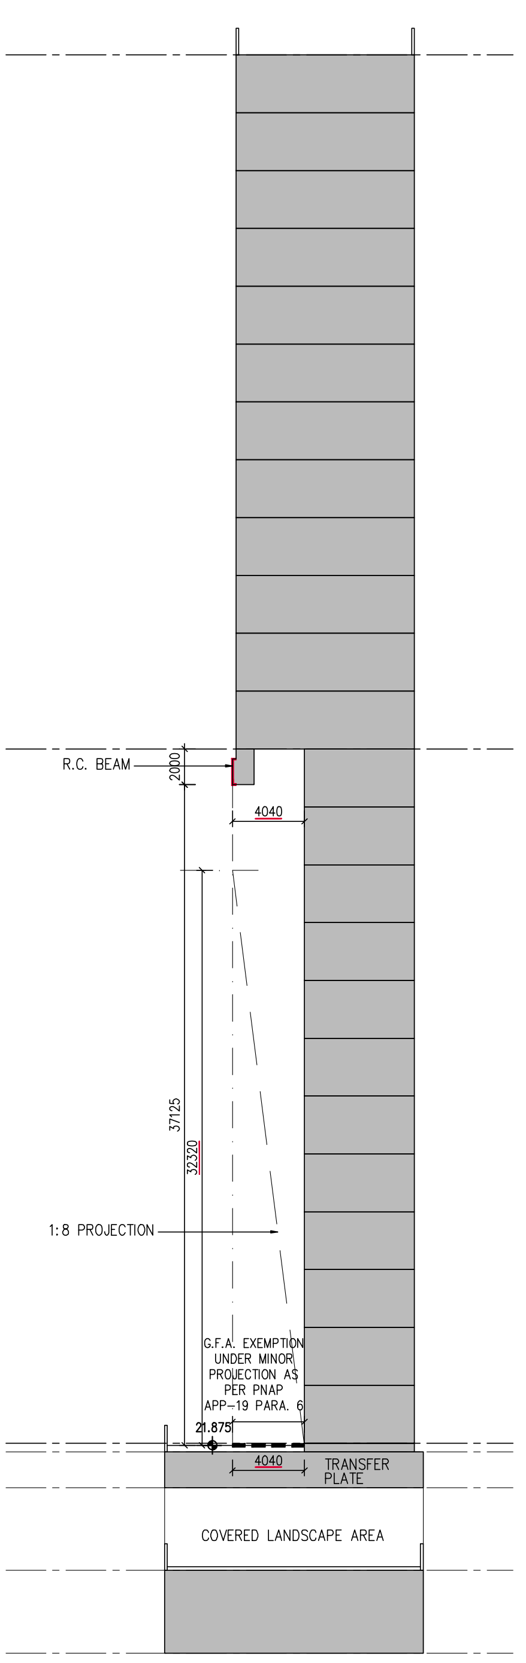
R.C. BEAM
1:8 PROJECTION
G.F.A. EXEMPTION UNDER MINOR PROJECTION AS PER PNAP APP–19 PARA. 6
4040
TRANSFER PLATE
COVERED LANDSCAPE AREA

DIAGRAMMATIC SECTION Y
SCALE 1:300

B.D. Ref : BD 2/4024/21
BIM Ref : - --
F.S.D. Ref : - --
D.L.O. Ref : - --

Rev.	Description	Drawn	Checked	Approved	Date
-	1st Submission	WY	AW	AL	07/2022
A	2nd Submission	WY	AW	AL	11/2022
B	1st Amendment	TWM	AW	AL	04/2023
C	2nd Amendment	TWM	AW	AL	12/2023
D	3rd Amendment	TWM	AW	AL	04/2024
E	4th Amendment	TWM	AW	AL	08/2024
F	5th Amendment	TWM	AW	AL	12/2024
F	5th Amendment (Re-submission)	TWM	AW	AL	02/2025
G	6th Amendment	TWM	AW	AL	02/2025
H	8th Amendment	TWM	AW	AL	05/2025
I	9th Amendment	LKM	AW	AL	08/2025
J	10th Amendment	TWM	AW	AL	12/2025
K	11th Amendment	TWM	AW	AL	02/2026

RONALD LU & PARTNERS
呂元祥建築師事務所

Check all measurements on site. Do not scale off drawings.
This drawing is to be read in conjunction with the specification and any discrepancies are to be immediately reported to the Architect.
This drawing remains the copyright property of the Architect and is not to be reproduced in whole or in part without permission of the Architect.

Project Title :
PROPOSED DEVELOPMENT
AT BAILEY STREET
& WING KWONG STREET
TO KWA WAN, KOWLOON

Drawing Title :
3RD - 30TH FLOOR PLAN
FOR TOWER 5

Drawn By	TWM	Date	08/2025
Checked By	AW	Date	08/2025
Approved By	AL	Date	08/2025
Project No.	21163KL	Issue Date	08/2025

File Path :
U:\Studio_B\Proj_Data\2021\21163KL_Bailey Street & Wing Kwong Street\DRAWING\SUB\BD\GBP_13 (Final Amendment)_Hand Amend\PLOT_FS\A_GBP_17.dwg

Scale 1:100 By CAD

Drawing Number : A/GBP/17
Revision Number : K

Drawing Purpose
Fire Services Department
Amended Plan

FIRE SERVICE REQUIRE-
MENTS INCORPORATED
Date: 12 JUN 2026
(LEUNG KA HAY)
SStnO(NP)