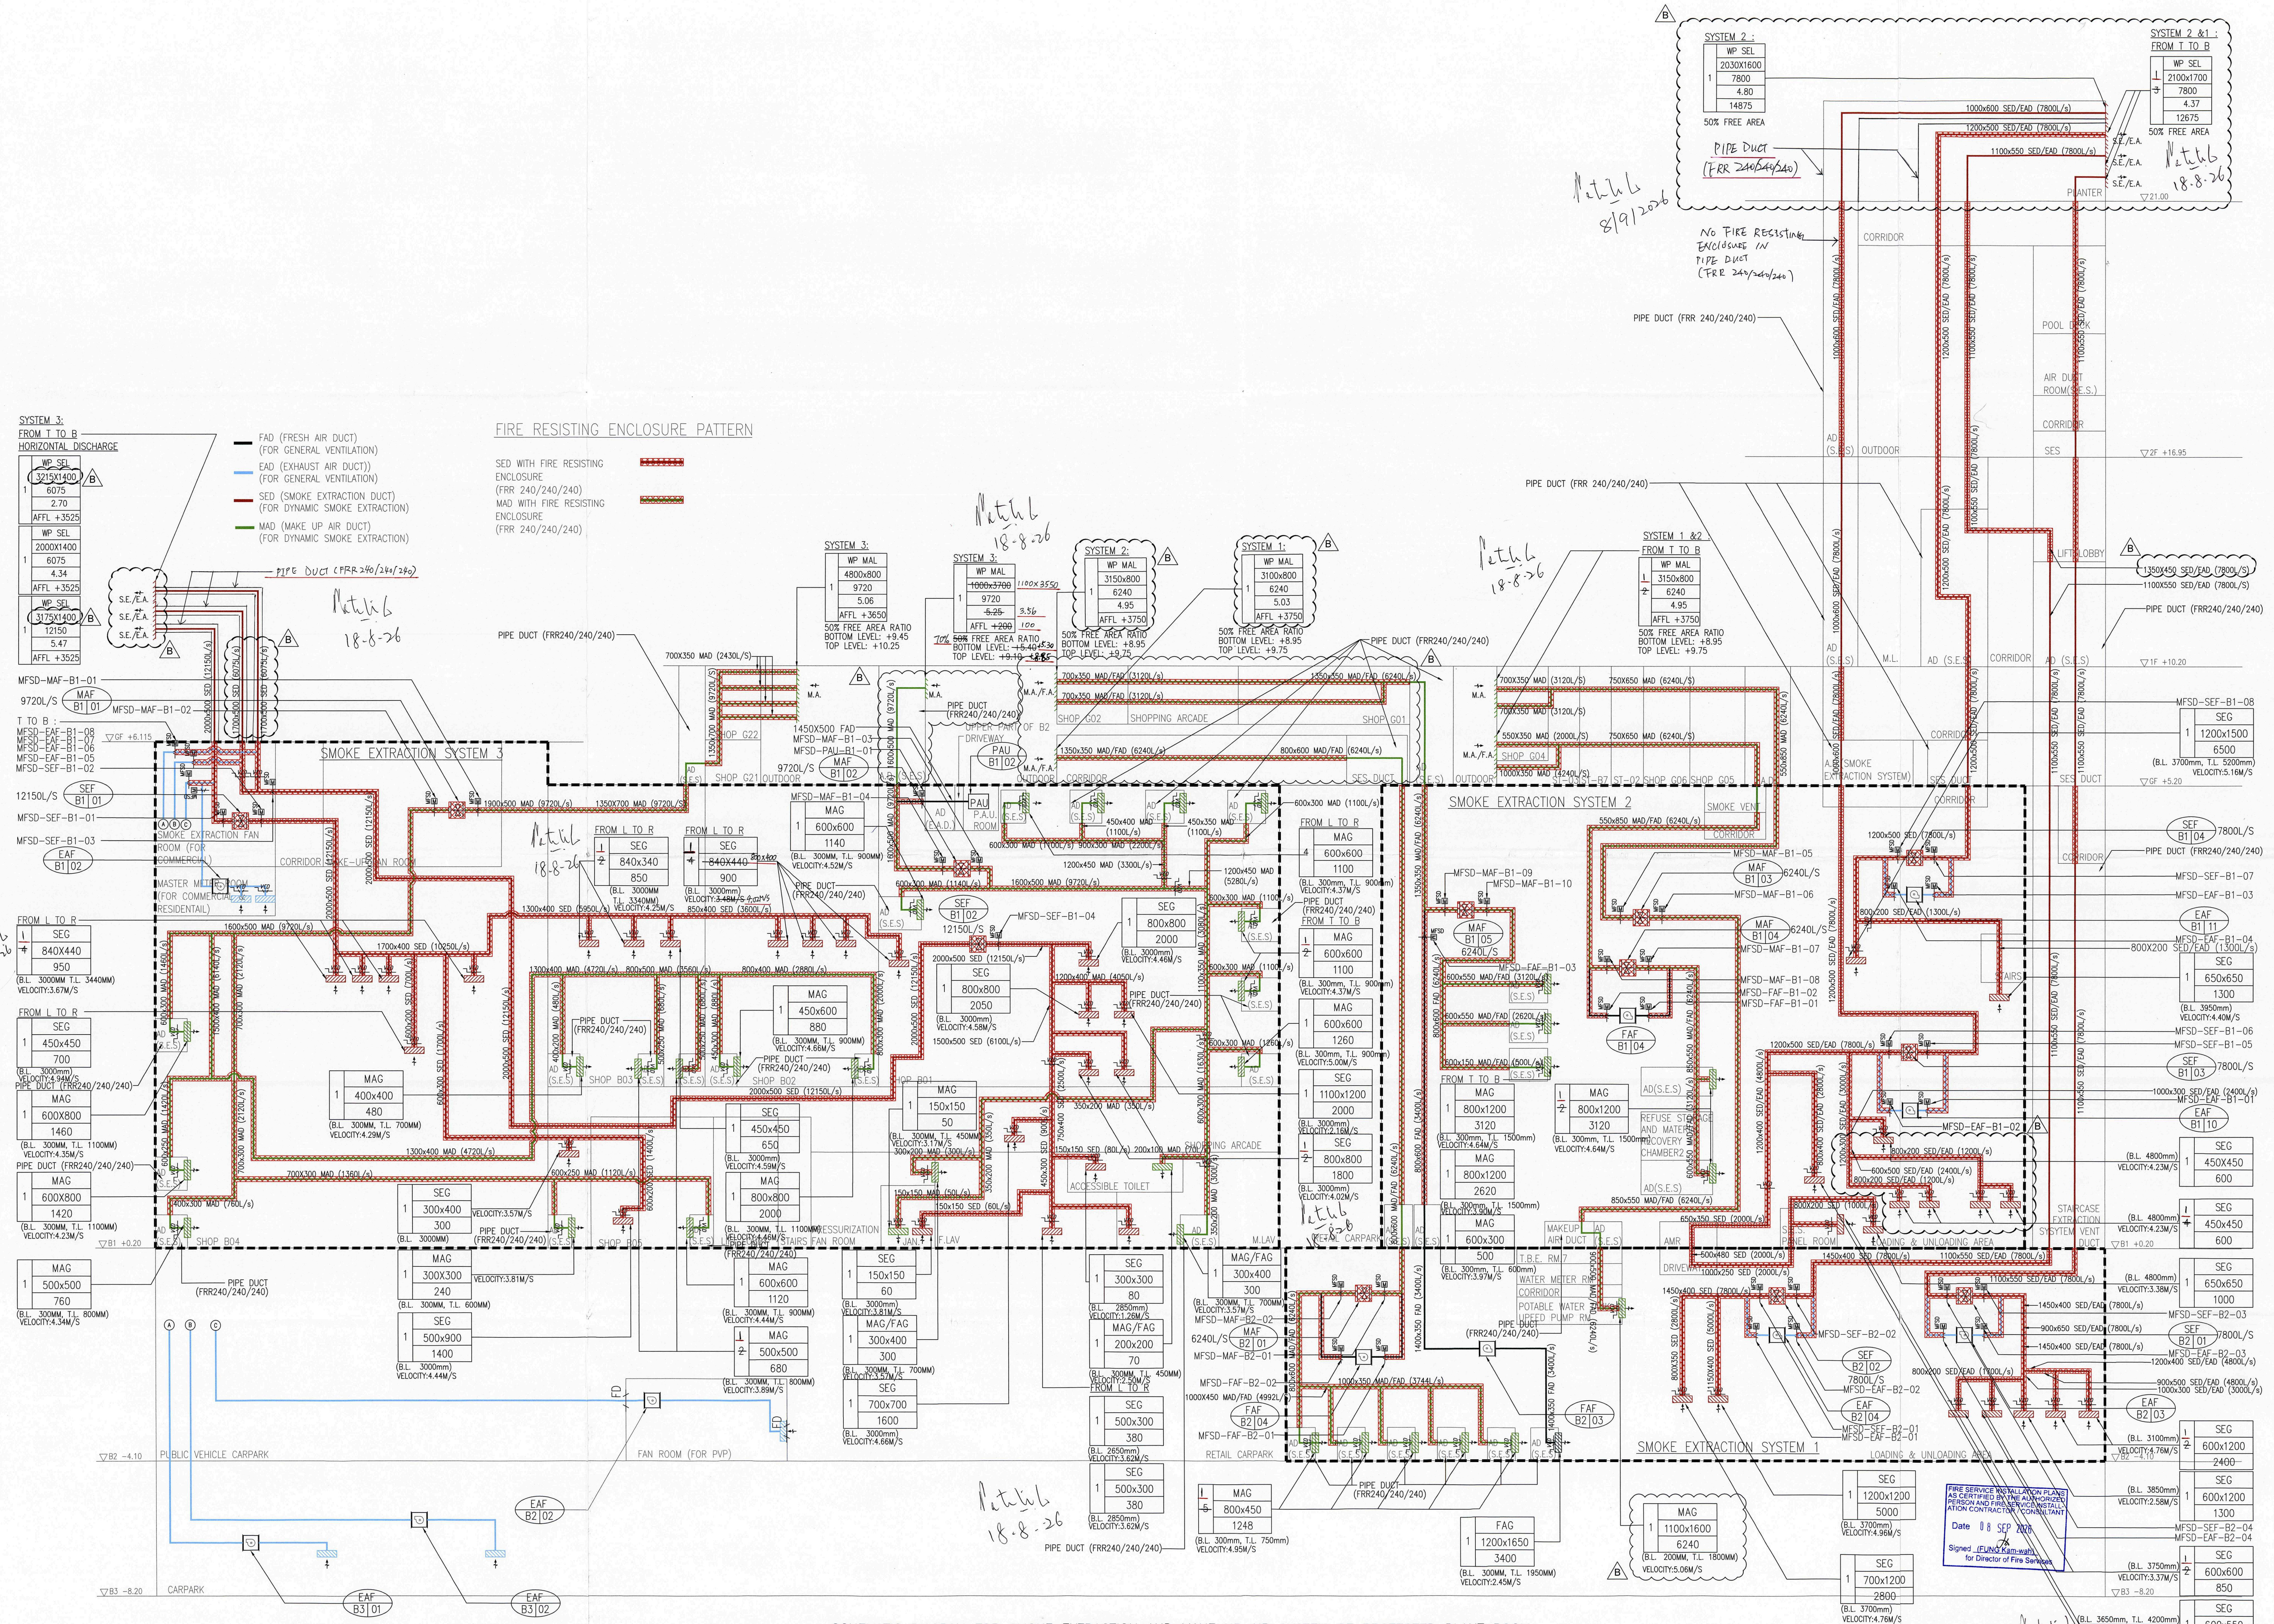
FAD (FRESH AIR DUCT) (FOR GENERAL VENTILATION)
EAD (EXHAUST AIR DUCT)) (FOR GENERAL VENTILATION)
SED (SMOKE EXTRACTION DUCT) (FOR DYNAMIC SMOKE EXTRACTION)
MAD (MAKE UP AIR DUCT) (FOR DYNAMIC SMOKE EXTRACTION)
FIRE RESISTING ENCLOSURE PATTERN
SED WITH FIRE RESISTING ENCLOSURE (FRR 240/240/240)
MAD WITH FIRE RESISTING ENCLOSURE (FRR 240/240/240)
SYSTEM 3: FROM T TO B HORIZONTAL DISCHARGE
SYSTEM 2 :
SYSTEM 2 &1 : FROM T TO B
SYSTEM 1 &2 FROM T TO B
SYSTEM 1:
SYSTEM 2:
SYSTEM 3:
SMOKE EXTRACTION SYSTEM 1
SMOKE EXTRACTION SYSTEM 2
SMOKE EXTRACTION SYSTEM 3
PIPE DUCT (FRR 240/240/240)
No fire resisting enclosure in pipe duct (FRR 240/240/240)
50% FREE AREA RATIO
PUBLIC VEHICLE CARPARK
CARPARK
FAN ROOM (FOR PVP)
RETAIL CARPARK
LOADING & UNLOADING AREA
SHOPPING ARCADE
CORRIDOR
OUTDOOR
LIFT LOBBY
POOL DECK
PLANTER
18-8-26
8/9/2026

SCHEMATIC DIAGRAM FOR SMOKE EXTRACTION AND MAKE UP AIR SYSTEM OF PROTECTED PLANT ROOM

FIRE SERVICE INSTALLATION PLANS AS CERTIFIED BY THE AUTHORIZED PERSON AND FIRE SERVICE INSTALLATION CONTRACTOR / CONSULTANT
Date 08 SEP 2026
Signed (FUNG Kam-wah)
for Director of Fire Services

LOO Kwan Wai
(RPE No.: RP0260258)

NO.	DATE	REVISIONS	DRAFTED	CHECKED	DESIGNED	REVIEWED
B	06/2026	FSD THIRD SUBMISSION	HYH	WWC	HYH	TKL
A	09/2025	FSD SECOND SUBMISSION	HYH	WWC	HYH	TKL
0	05/2025	FSD FIRST SUBMISSION	HYH	WWC	HYH	TKL

CLIENT:

NATION STAR DEVELOPMENT LIMITED
75/F, 8 Finance Street,
Central, Hong Kong

PROJECT ARCHITECT & AUTHORIZED PERSON:

RONALD LU & PARTNERS
呂元祥建築師事務所
33rd Floor, Wu Chung house, 213 Queen's Road East,
Wanchai, Hong Kong

STRUCTURAL/GEOTECHNICAL

wsp
7/F, One Kowloon
1 Wang Yuen Street
Kowloon Bay, Hong Kong

BUILDING SERVICES ENGINEER:

wsp
7/F, One Kowloon
1 Wang Yuen Street
Kowloon Bay, Hong Kong

QUANTITY SURVEYOR:

ARCADIS
17/F, Two Harbour Square, 180 Wai Yip Street,
Kwun Tong, Kowloon
Hong Kong

FIRE SERVICES CONTRACTOR:

開創工程有限公司
GRAND CREATIVE ENGINEERS LIMITED

PROJECT:

PROPOSED DEVELOPMENT AT BAILEY STREET & WING KWONG STREET, TO KWA WAN, KOWLOON
INLAND LOT NO. 11279
(URA PROJECT KC-009)

TITLE:

SMOKE EXTRACTION SYSTEM- SCHEMATIC DRAWING

④

DATE: 06/2026		SCALE: NTS@A0	
DRAFTED: HYH	CHECKED: WWC	DESIGNED: HYH	REVIEWED: TKL
JOB NO. 2503373A	DRAWING NO. 2503373A/SES/101		REV. NO. B