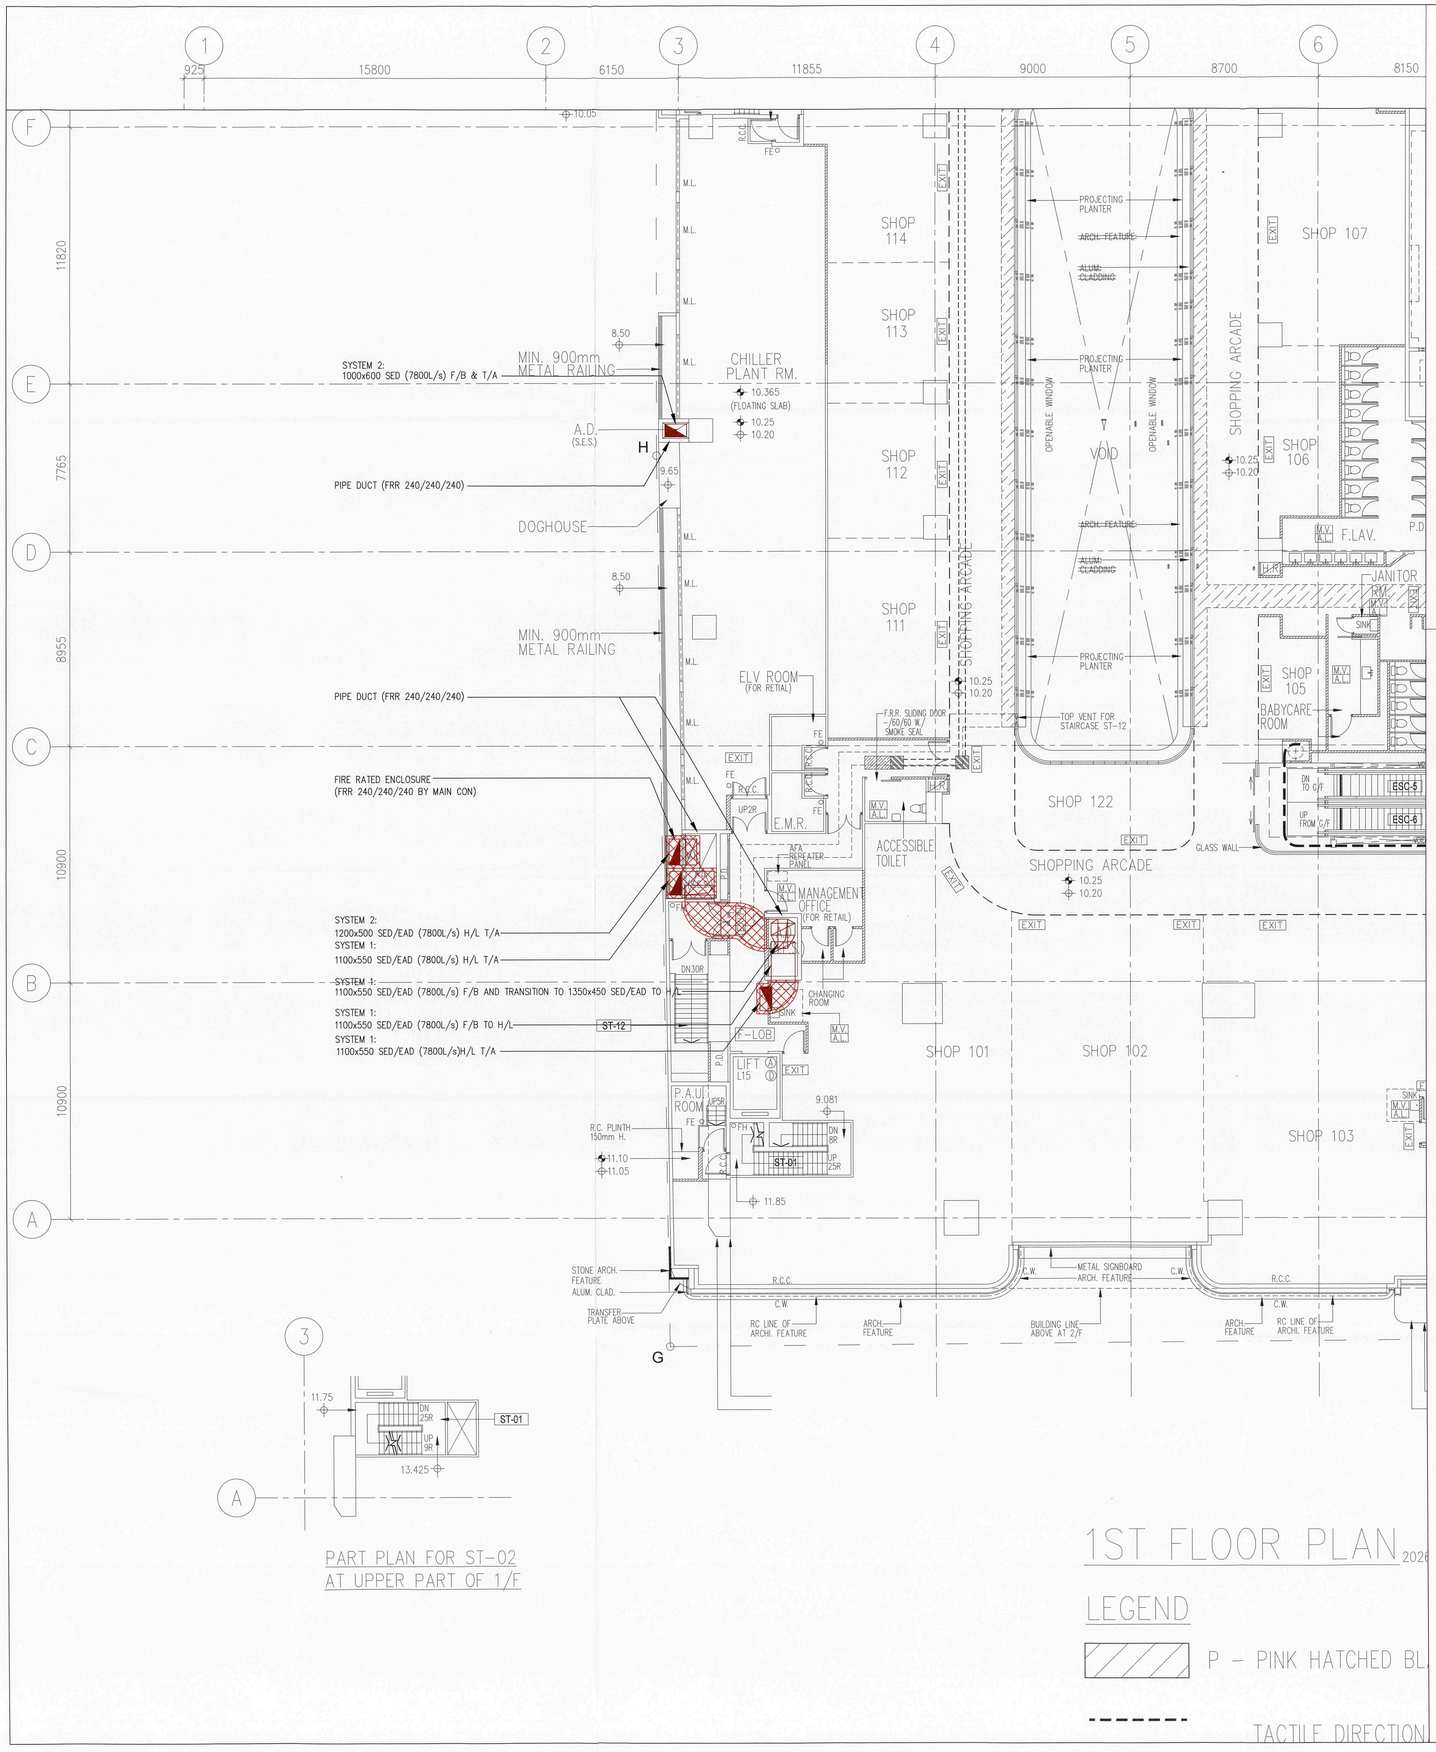



PART PLAN FOR ST-02
AT UPPER PART OF 1/F

1ST FLOOR PLAN 2026

LEGEND

P - PINK HATCHED BL

TACTILE DIRECTION

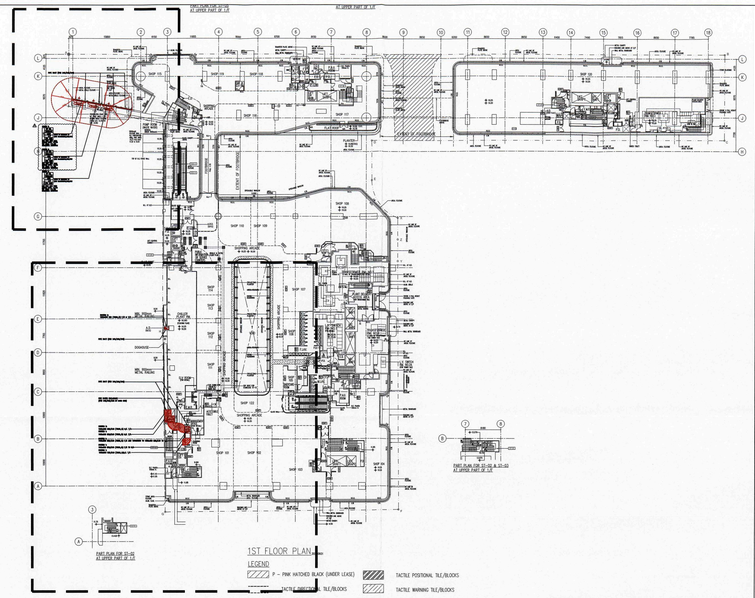

1ST FLOOR PLAN

LEGEND


P - PINK HATCHED BLACK (UNDER LEASE)

TACTILE POSITIONAL TILE/BLOCKS

TACTILE TILE/BLOCKS

TACTILE WARNING TILE/BLOCKS

KEY PLAN 1:500

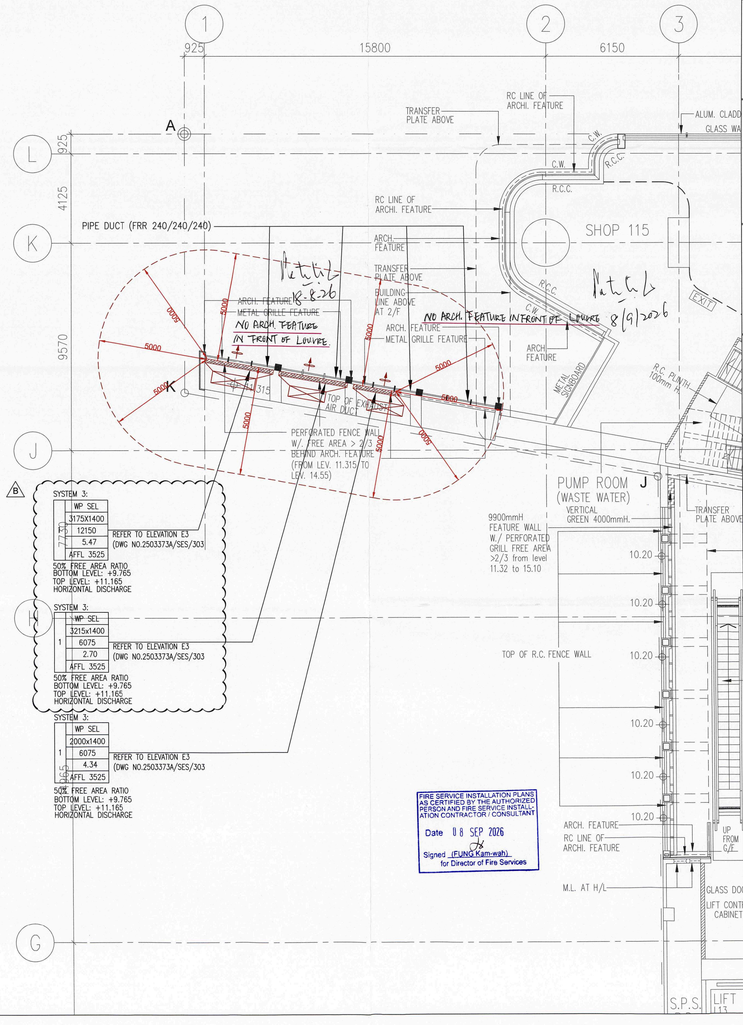

FIRE SERVICE INSTALLATION PLANS AS CERTIFIED BY THE AUTHORIZED PERSON AND FIRE SERVICE INSTALLATION CONTRACTOR / CONSULTANT
Date 08 SEP 2026
Signed (ELING Kam-wah)
for Director of Fire Services

LOO Kwan Wai
(RPE No.: RP0260258)

NO.	DATE	REVISIONS	DRAFTED	CHECKED	DESIGNED	REVIEWED
B	06/2026	FSD THIRD SUBMISSION	HYH	MWC	HYH	TKL
A	09/2025	FSD SECOND SUBMISSION	HYH	MWC	HYH	TKL
0	05/2025	FSD FIRST SUBMISSION	HYH	MWC	HYH	TKL

CLIENT:

NATION STAR DEVELOPMENT LIMITED
75/F, 8 Finance Street,
Central, Hong Kong

PROJECT ARCHITECT & AUTHORIZED PERSON:

RONALD LU & PARTNERS
呂元祥建築師事務所
33rd Floor, Wu Chung house, 213 Queen's Road East, Wanchai, Hong Kong

STRUCTURAL/GEOTECHNICAL

wsp
7/F, One Kowloon
1 Wang Yuen Street
Kowloon Bay, Hong Kong

BUILDING SERVICES ENGINEER:

wsp
7/F, One Kowloon
1 Wang Yuen Street
Kowloon Bay, Hong Kong

QUANTITY SURVEYOR:

ARCADIS
17/F, Two Harbour Square, 180 Wai Yip Street, Kwun Tong, Kowloon
Hong Kong

FIRE SERVICES CONTRACTOR:

開創工程有限公司
GRAND CREATIVE ENGINEERS LIMITED

PROJECT:

PROPOSED DEVELOPMENT AT BAILEY STREET & WING KWONG STREET, TO KWA WAN, KOWLOON
INLAND LOT NO. 11279
(URA PROJECT KC-009)

TITLE:

SMOKE EXTRACTION SYSTEM - 1/F LAYOUT

12

DATE: 06/2026		SCALE: 1:100@A0	
DRAFTED: HYH	CHECKED: MWC	DESIGNED: HYH	REVIEWED: TKL
JOB NO. 2503373A	DRAWING NO. 2503373A/SES/203		REV. NO. B