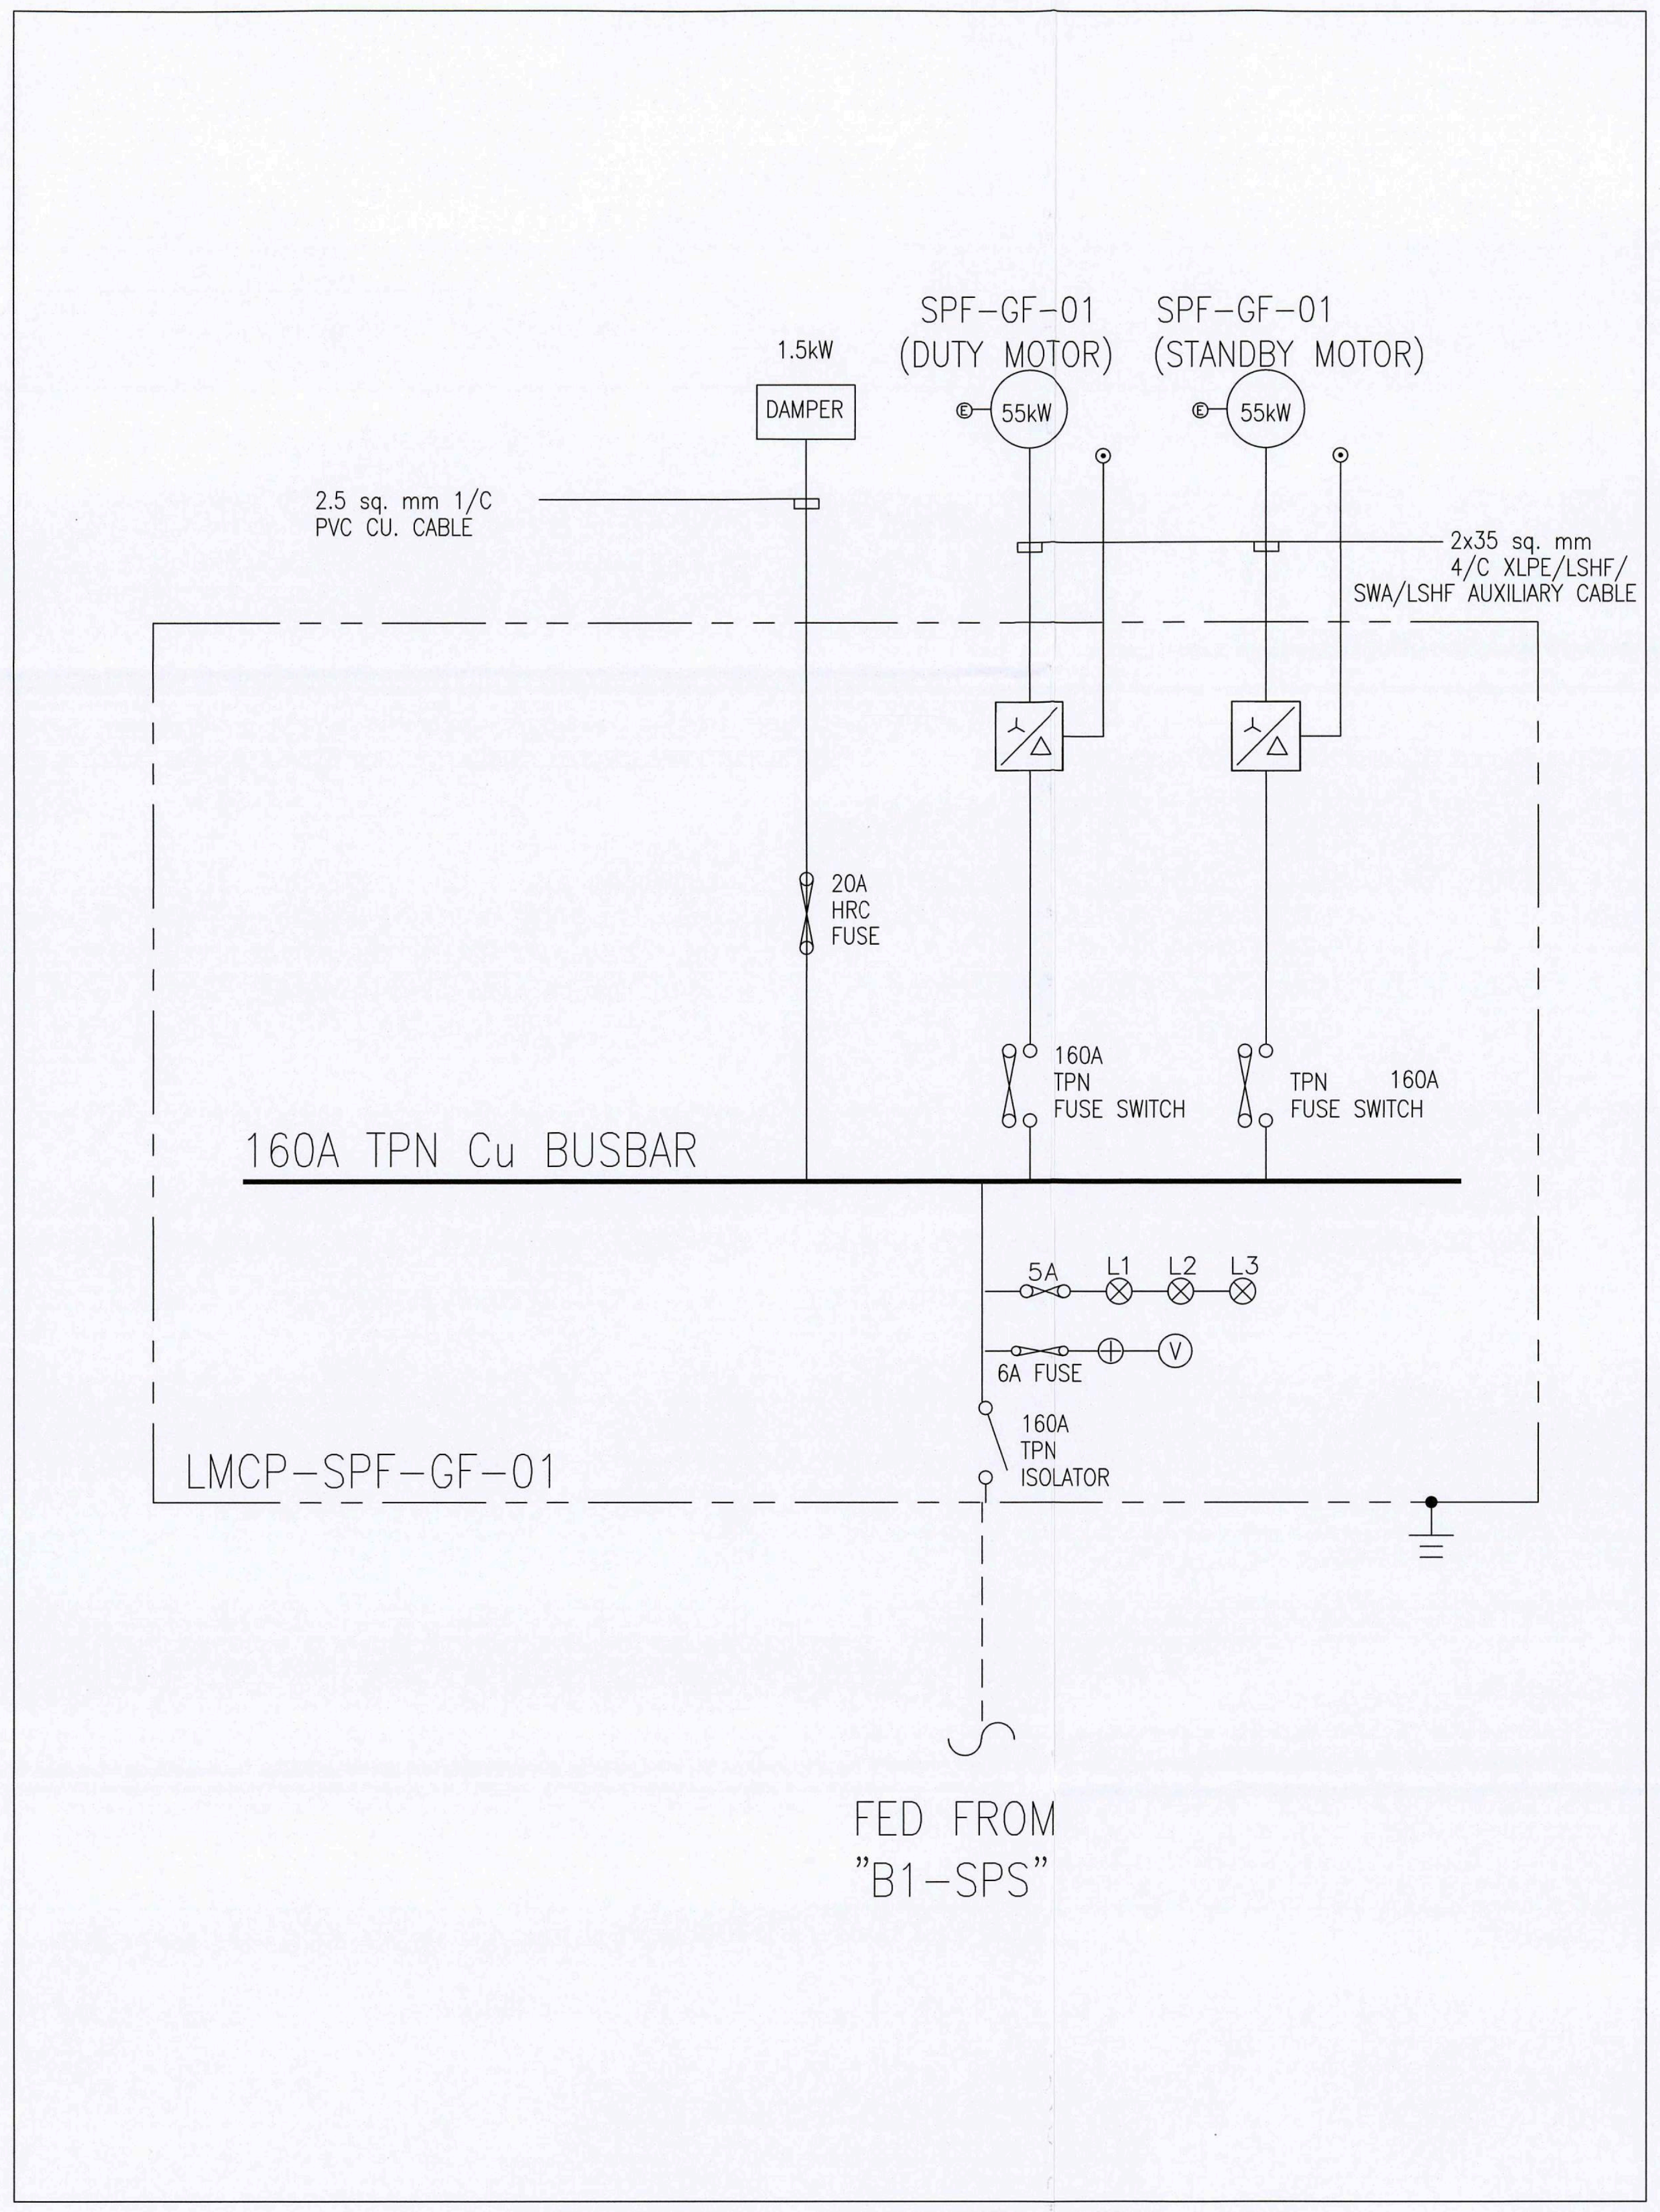
SPF-GF-01
(DUTY MOTOR)
SPF-GF-01
(STANDBY MOTOR)
1.5kW
DAMPER
55kW
55kW
2.5 sq. mm 1/C
PVC CU. CABLE
2x35 sq. mm
4/C XLPE/LSHF/
SWA/LSHF AUXILIARY CABLE
20A
HRC
FUSE
160A
TPN
FUSE SWITCH
TPN 160A
FUSE SWITCH
160A TPN Cu BUSBAR
5A
L1
L2
L3
6A FUSE
V
160A
TPN
ISOLATOR
LMCP-SPF-GF-01
FED FROM
"B1-SPS"


LPF-GF-01
(DUTY MOTOR)
LPF-GF-01
(STANDBY MOTOR)
1.5kW
DAMPER
7.5kW
7.5kW
2.5 sq. mm 1/C
PVC CU. CABLE
2x2.5 sq. mm
4/C XLPE/LSHF/
SWA/LSHF AUXILIARY CABLE
20A
HRC
FUSE
32A
TPN
FUSE SWITCH
32A
TPN
FUSE SWITCH
32A TPN Cu BUSBAR
5A
L1
L2
L3
6A FUSE
V
32A
TPN
ISOLATOR
LMCP-LPF-GF-01
FED FROM
"B1-SPS"

ABBREVATION

NO	NORMAL OPEN
NC	NORMAL CLOSE
LMCP	LOCAL MOTOR CONTROL PANEL
ATS	AUTOMATIC CHANGEOVER SWITCH

LEGEND

	TPN MCCB - TRIPLE POLE & NEUTRAL MOULDED CASE CIRCUIT BREAKER
	SPN MCB - SINGLE POLE & NEUTRAL MINIATURE CIRCUIT BREAKER
	TPN F/S OR TPN S/F - TRIPLE POLE & NEUTRAL FUSE SWITCH / SWITCHED FUSE
Ⓐ	AMMETER (240° SCALE)
Ⓥ	VOLTMETER (240° SCALE)
(PF)	POWER FACTOR METER (240° SCALE)
3xO/C 1xE/F	IDMT OVERCURRNT PROTECTION RELAY AND EARTH FAULT RELAY
	AMMETER SELECTOR
⊕	VOLTMETER SELECTOR
	AUTOMATIC STAR-DELTA STARTER
E/F	EARTH FAULT
ε	MCT - MEASURING CURRENT TRANSFORMER PCT - PROTECTION CURRENT TRANSFORMER
	HRC CONTROL FUSE
	INDICATING LAMP 'R' RED 'Y' YELLOW 'B' BLUE
	CAPACITOR, 5-STEP AUTOMATIC POWER FACTOR REGULATOR
BBC	BUSBAR CHAMBER
Ⓔ	EMERGENCY STOP PUSH BOTTON
UV	UNDERVOLTAGE RELAY
FI	FREQUENCY INVERTOR (SHALL REPEAT TO BMS FOR CONTROL AND MONITORING)
N.C. N.O.	AUTOMATIC CHANGEOVER CONTACTOR
H	HEAT OR OVERLOAD

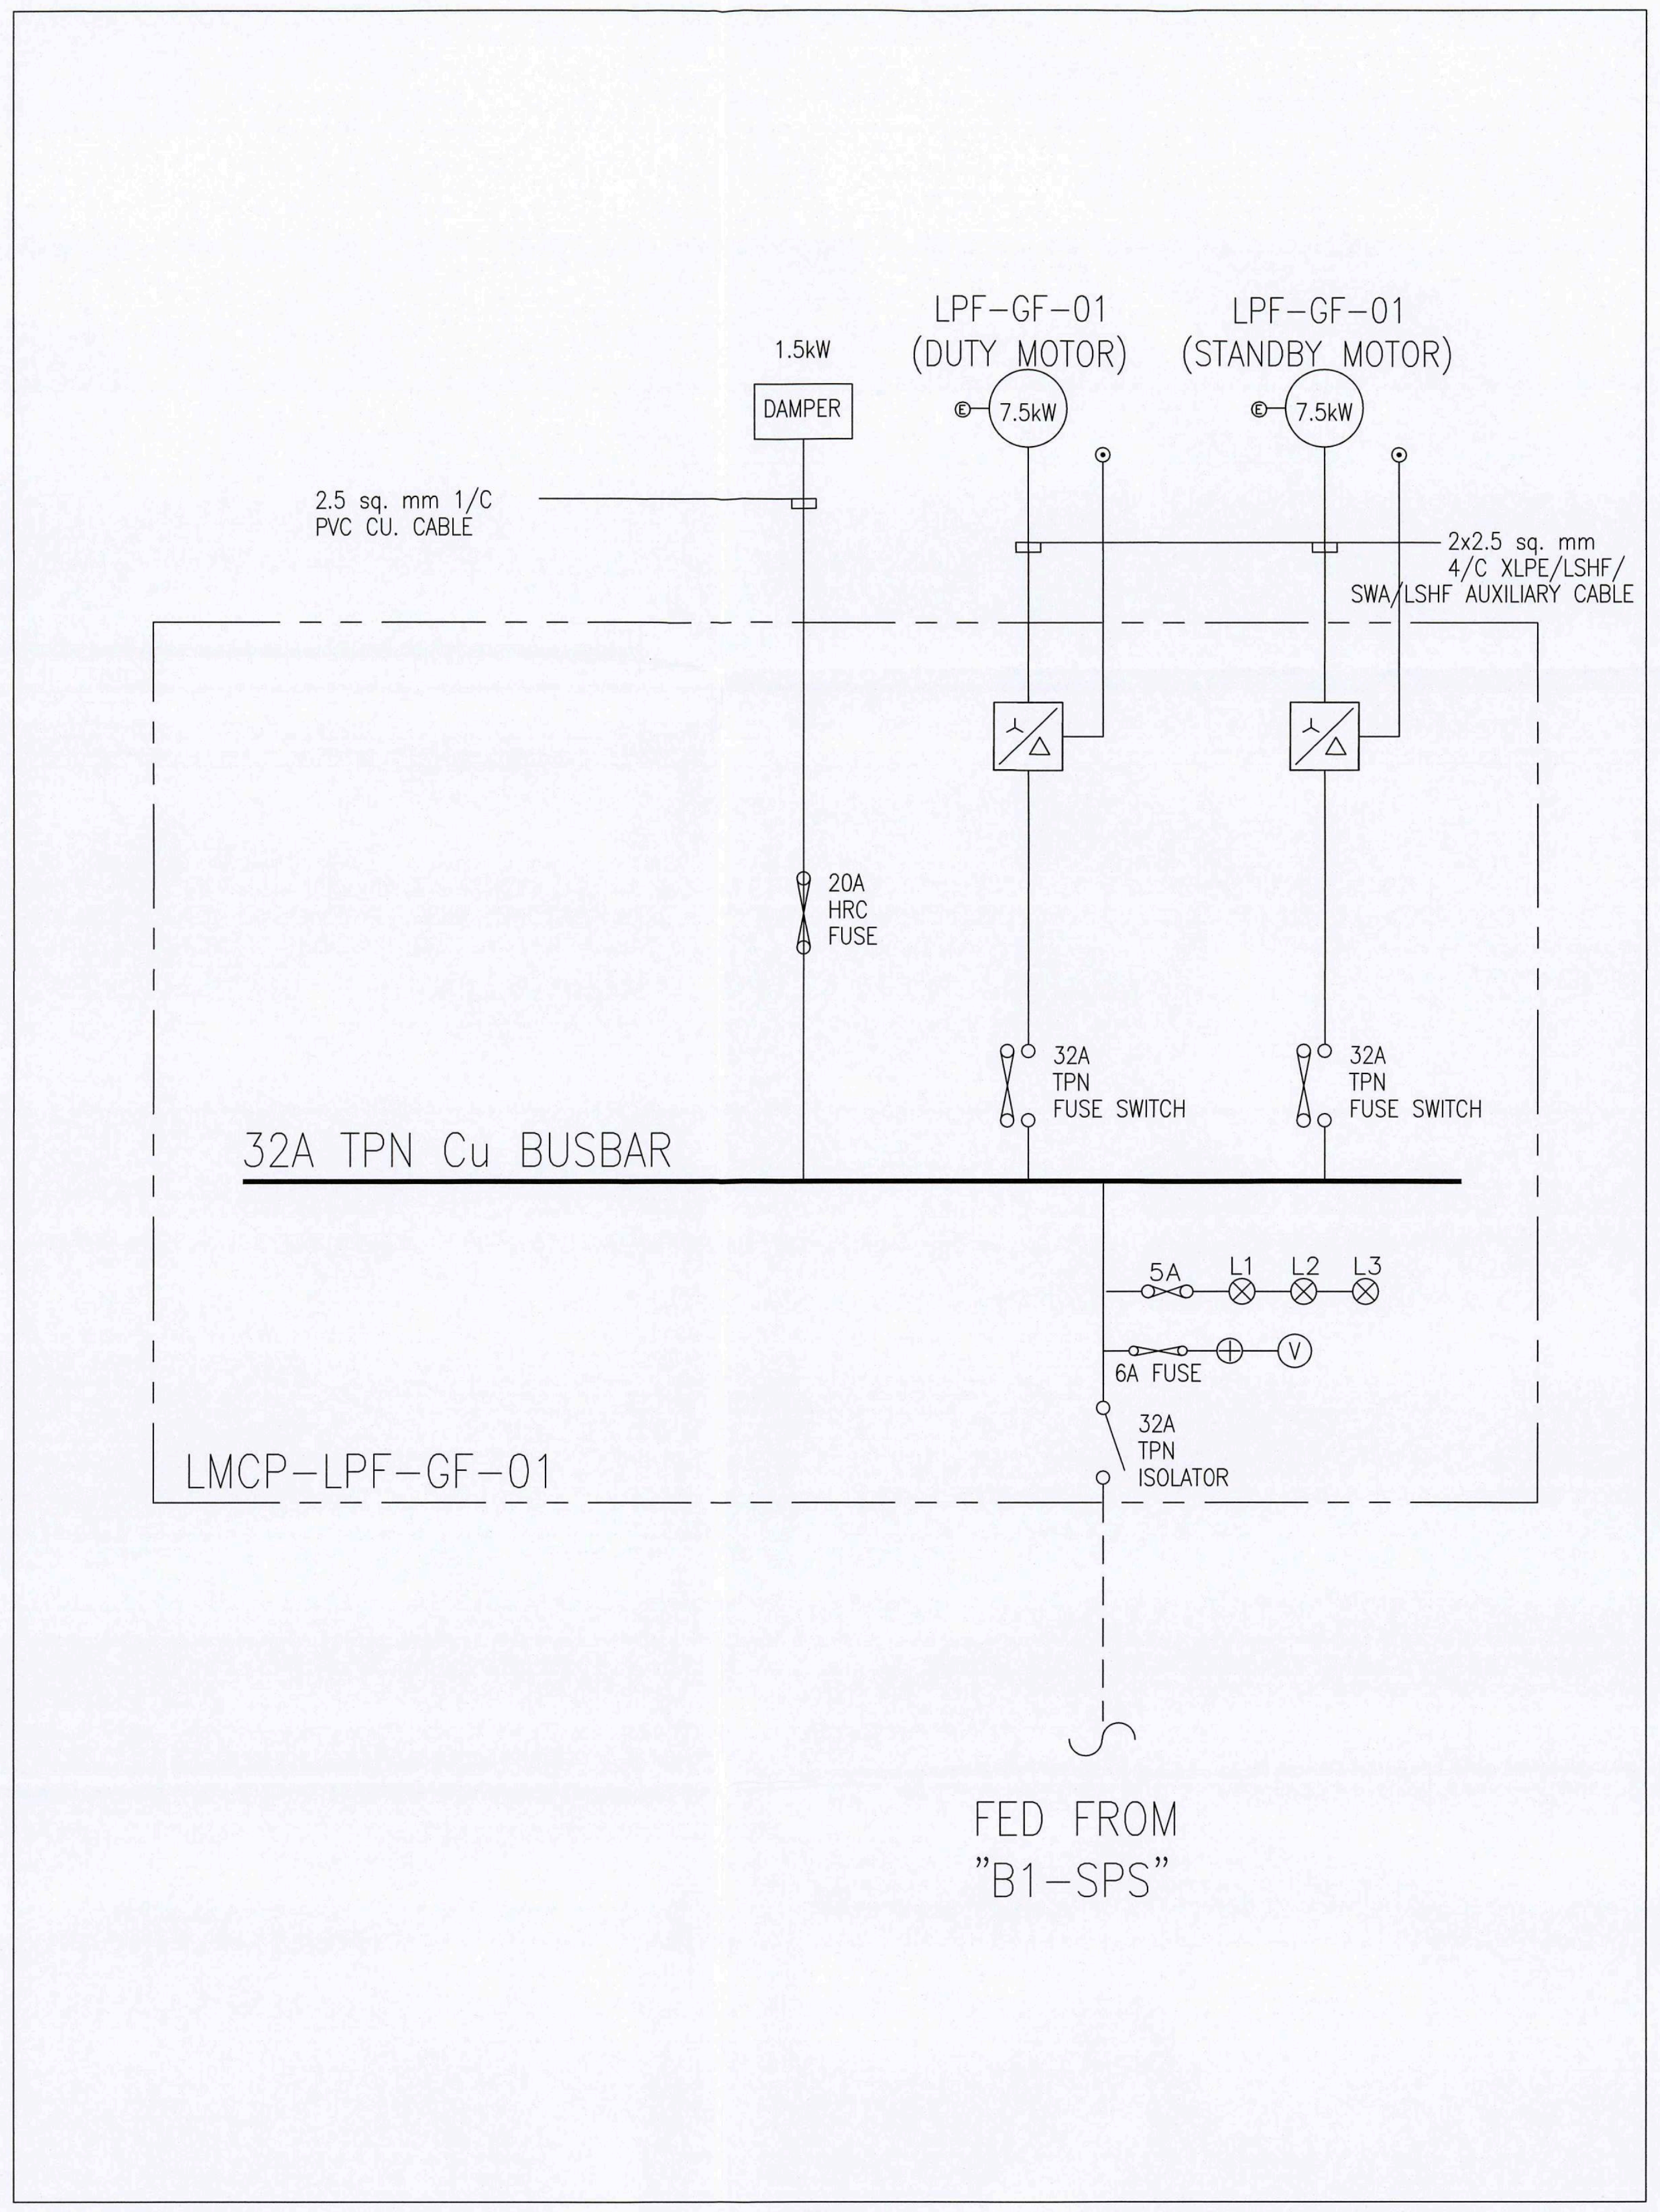FIRE SERVICE INSTALLATION PLANS AS CERTIFIED BY THE AUTHORIZED PERSON AND FIRE SERVICE INSTALLATION CONTRACTOR / CONSULTANT

Date 27 AUG 2026

Signed (FUNG Kam-wah)
for Director of Fire Services

FOR INFORMATION ONLY

LOO Kwan Wai
(RPE No.: RP0260258)

NO.	DATE	REVISIONS	DRAFTED	CHECKED	DESIGNED	REVIEWED
A	07/2025	FSD SECOND SUBMISSION	HYH	WWC	HYH	TKL
0	03/2025	FSD FIRST SUBMISSION	HYH	WWC	HYH	TKL

CLIENT:

NATION STAR DEVELOPMENT LIMITED
75/F, 8 Finance Street,
Central, Hong Kong

PROJECT ARCHITECT & AUTHORIZED PERSON:

RONALD LU & PARTNERS
呂元祥建築師事務所
33rd Floor, Wu Chung house, 213 Queen's Road East,
Wanchai, Hong Kong

STRUCTURAL/GEOTECHNICAL

wsp
7/F, One Kowloon
1 Wang Yuen Street
Kowloon Bay, Hong Kong

BUILDING SERVICES ENGINEER:

wsp
7/F, One Kowloon
1 Wang Yuen Street
Kowloon Bay, Hong Kong

QUANTITY SURVEYOR:

ARCADIS
17/F, Two Harbour Square, 180 Wai Yip Street,
Kwun Tong, Kowloon
Hong Kong

FIRE SERVICES CONTRACTOR:

開創工程有限公司
GRAND CREATIVE ENGINEERS LIMITED
CLASS 1, 2, 3 REGISTERED FIRE SERVICES CONTRACTOR
WSD LICENSED PLUMBER (GRADE 1)
EMSD REGISTERED ELECTRICAL CONTRACTOR

陳廣開
Chan Kwong Hoi
Director

Unit D, 2/F, Cheong Wah Comm. Bldg., 900-904 Canton Road, Kowloon.
Mobile : 9015 9586 Tel : 3612 5782 Fax : 3612 5785
Email : info@grandcreative.com.hk

PROJECT:

PROPOSED DEVELOPMENT AT BAILEY
STREET & WING KWONG STREET,
TO KWA WAN, KOWLOON
INLAND LOT NO. 11279
(URA PROJECT KC-009)

TITLE:

STAIRCASE PRESSURIZATION SYSTEM –
ELECTRICAL & LMCP WIRING DIAGRAM
(SHEET 1 OF 4) (ST-B1)

DATE: 06/2026		SCALE: NTS@A0	
DRAFTED: HYH	CHECKED: WWC	DESIGNED: HYH	REVIEWED: TKL
JOB NO.	DRAWING NO.		REV. NO.
2503373A	2503373A/SPS/STB1/401		A

14