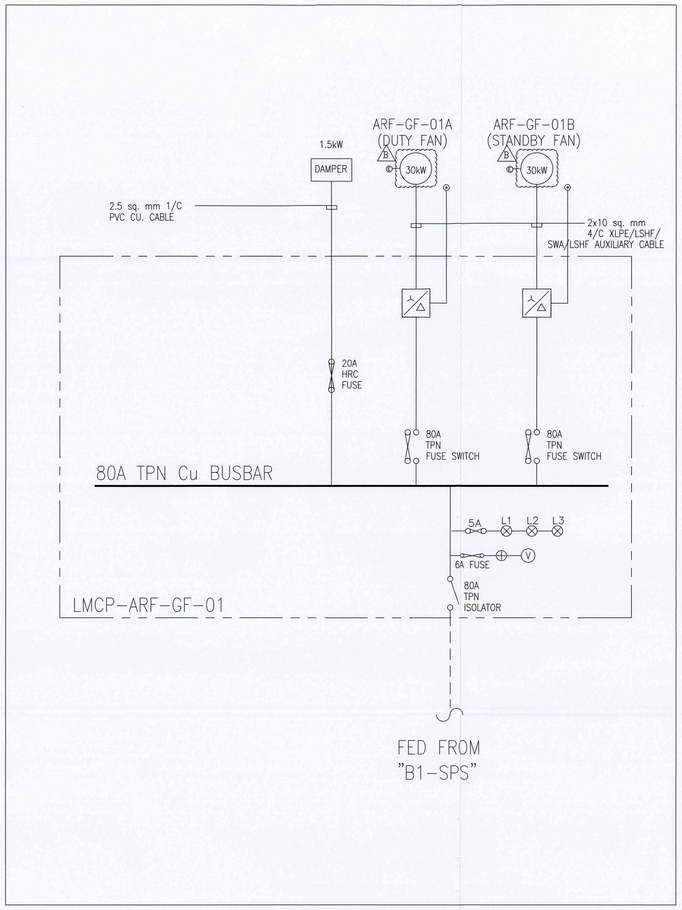


ABBREVATION

NO	NORMAL OPEN
NC	NORMAL CLOSE
LMCP	LOCAL MOTOR CONTROL PANEL
ATS	AUTOMATIC CHANGEOVER SWITCH

LEGEND

- TPN MCCB – TRIPLE POLE & NEUTRAL MOULDED CASE CIRCUIT BREAKER
- SPN MCB – SINGLE POLE & NEUTRAL MINIATURE CIRCUIT BREAKER
- TPN F/S OR TPN S/F – TRIPLE POLE & NEUTRAL FUSE SWITCH / SWITCHED FUSE
- (A) AMMETER (240° SCALE)
- (V) VOLTMETER (240° SCALE)
- (PF) POWER FACTOR METER (240° SCALE)
- IDMT OVERCURRNT PROTECTION RELAY AND EARTH FAULT RELAY
- AMMETER SELECTOR
- VOLTMETER SELECTOR
- AUTOMATIC STAR-DELTA STARTER
- E/F EARTH FAULT
- MCT – MEASURING CURRENT TRANSFORMER
  PCT – PROTECTION CURRENT TRANSFORMER
- HRC CONTROL FUSE
- INDICATING LAMP
  'R' RED
  'Y' YELLOW
  'B' BLUE
- CAPACITOR, 5-STEP AUTOMATIC POWER FACTOR REGULATOR
- BBC BUSBAR CHAMBER
- (E) EMERGENCY STOP PUSH BOTTON
- UV UNDERVOLTAGE RELAY
- FI FREQUENCY INVERTOR (SHALL REPEAT TO BMS FOR CONTROL AND MONITORING)
- AUTOMATIC CHANGEOVER CONTACTOR (N.C. N.O.)
- H HEAT OR OVERLOAD

FIRE SERVICE INSTALLATION PLANS IS CERTIFIED BY THE AUTHORIZED PERSON AND FIRE SERVICE INSTALLATION CONTRACTOR / CONSULTANT
Date 27 AUG 2026
Signed (FUNG Kam-wah)
for Director of Fire Services

FOR INFORMATION ONLY

LOO Kwan Wai
(RPE No.: RP0260258)

NO.	DATE	REVISIONS	DRAFTED	CHECKED	DESIGNED	REVIEWED
B	06/2026	FSD THIRD SUBMISSION	HYH	WWC	HYH	TKL
A	07/2025	FSD SECOND SUBMISSION	HYH	WWC	HYH	TKL
0	03/2025	FSD FIRST SUBMISSION	HYH	WWC	HYH	TKL

CLIENT:

NATION STAR DEVELOPMENT LIMITED
75/F, 8 Finance Street,
Central, Hong Kong

PROJECT ARCHITECT & AUTHORIZED PERSON:

RONALD LU & PARTNERS
呂元祥建築師事務所
33rd Floor, Wu Chung house, 213 Queen's Road East,
Wanchai, Hong Kong

STRUCTURAL/GEOTECHNICAL

wsp
7/F, One Kowloon
1 Wang Yuen Street
Kowloon Bay, Hong Kong

BUILDING SERVICES ENGINEER:

wsp
7/F, One Kowloon
1 Wang Yuen Street
Kowloon Bay, Hong Kong

QUANTITY SURVEYOR:

ARCADIS
17/F, Two Harbour Square, 180 Wai Yip Street,
Kwun Tong, Kowloon
Hong Kong

FIRE SERVICES CONTRACTOR:

開創工程有限公司
GRAND CREATIVE ENGINEERS LIMITED
CLASS I, II, III REGISTERED FIRE SERVICES CONTRACTOR
WSD LICENSED PLUMBER (GRADE 1)
EMSD REGISTERED ELECTRICAL CONTRACTOR
陳廣開
Chan Kwong Hoi
Director
Unit D, 2/F, Cheong Wah Comm. Bldg., 900-904 Canton Road, Kowloon.
Mobile : 9015 9586 Tel : 3612 5782 Fax : 3612 5785
Email : info@grandcreative.com.hk

PROJECT:

PROPOSED DEVELOPMENT AT BAILEY STREET & WING KWONG STREET, TO KWA WAN, KOWLOON
INLAND LOT NO. 11279
(URA PROJECT KC-009)

TITLE:

STAIRCASE PRESSURIZATION SYSTEM – ELECTRICAL & LMCP WIRING DIAGRAM (SHEET 2 OF 4) (ST-B1)

DATE: 06/2026		SCALE: NTS@A0	
DRAFTED: HYH	CHECKED: WWC	DESIGNED: HYH	REVIEWED: TKL
JOB NO. 2503373A	DRAWING NO. 2503373A/SPS/STB1/402		REV. NO. B

17