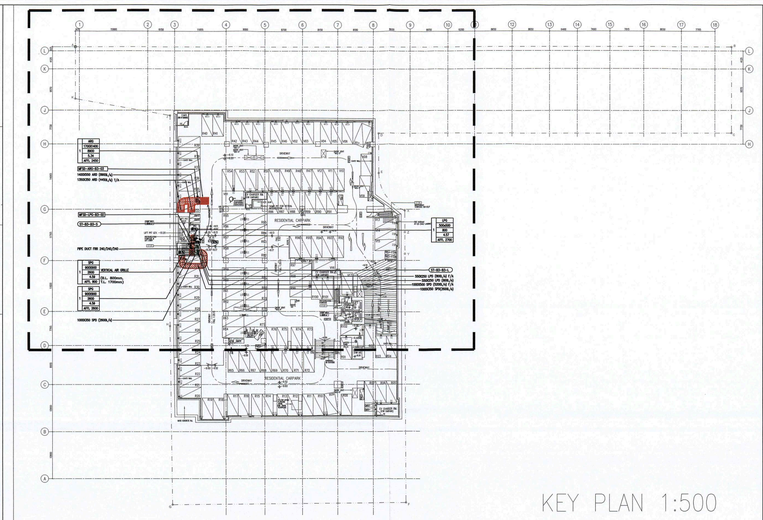


KEY PLAN 1:500

	ARG
1	1700X1400
	8900
	5.34
	AFFL 2450

MFSD-ARG-B3-03

1400X550 ARD (8900L/s)

1350X350 ARD (4450L/s) T/A

MFSD-LPG-B3-02

ST-B3-B3-S

PIPE DUCT FRR 240/240/240

	SPG
1	900X900
	2600
	4.59
	AFFL 800

VERTICAL AIR GRILLE

(B.L. 800mm, T.L. 1700mm)

	SPG
1	900X900
	2600
	4.59
	AFFL 2600

1000X350 SPD (2600L/s)

	LPG
1	500x500
	800
	4.57
	AFFL 2700

ST-B3-B3-L

550X250 LPD (800L/s) F/A

550X250 LPD (800L/s)

1000X500 SPD (5200L/s) F/A

1000X350 SPD(2600L/s)

LOO Kwan Wai
(RPE No.: RP0260258)

NO.	DATE	REVISIONS	DRAFTED	CHECKED	DESIGNED	REVIEWED
A	07/2025	FSD SECOND SUBMISSION	HYH	WWC	HYH	TKL
0	03/2025	FSD FIRST SUBMISSION	HYH	WWC	HYH	TKL

CLIENT:

NATION STAR DEVELOPMENT LIMITED
75/F, 8 Finance Street,
Central, Hong Kong

PROJECT ARCHITECT & AUTHORIZED PERSON:

RONALD LU & PARTNERS
呂元祥建築師事務所
33rd Floor, Wu Chung house, 213 Queen's Road East,
Wanchai, Hong Kong

STRUCTURAL/GEOTECHNICAL

wsp
7/F, One Kowloon
1 Wang Yuen Street
Kowloon Bay, Hong Kong

BUILDING SERVICES ENGINEER:

wsp
7/F, One Kowloon
1 Wang Yuen Street
Kowloon Bay, Hong Kong

QUANTITY SURVEYOR:

ARCADIS
17/F, Two Harbour Square, 180 Wai Yip Street,
Kwun Tong, Kowloon
Hong Kong

FIRE SERVICES CONTRACTOR:

開創工程有限公司
GRAND CREATIVE ENGINEERS LIMITED
CLASS 1 or 2 REGISTERED FIRE SERVICES CONTRACTOR
CLASS 1 REGISTERED ELECTRICAL CONTRACTOR
SIMEC REGISTERED ELECTRICAL CONTRACTOR

陳廣開
Chan Kwong Hoi
Director

Unit D, 2/F, Cheong Wah Comm. Bldg., 900-904 Canton Road, Kowloon.
Mobile : 9015 9586 Tel : 3612 5782 Fax : 3612 5785
Email : info@grandcreative.com.hk

PROJECT:

PROPOSED DEVELOPMENT AT BAILEY STREET & WING KWONG STREET, TO KWA WAN, KOWLOON
INLAND LOT NO. 11279
(URA PROJECT KC-009)

TITLE:

STAIRCASE PRESSURIZATION SYSTEM – B3 LAYOUT (ST-B3)

FIRE SERVICE INSTALLATION PLANS IS CERTIFIED BY THE AUTHORIZED PERSON AND FIRE SERVICE INSTALLATION CONTRACTOR / CONSULTANT

Date 27 AUG 2026

Signed (FUNG Kam-wah)
for Director of Fire Services

DATE: 06/2026		SCALE: 1:100@A0	
DRAFTED: HYH	CHECKED: WWC	DESIGNED: HYH	REVIEWED: TKL
JOB NO. 2503373A	DRAWING NO. 2503373A/SPS/STB3/201		REV. NO. A