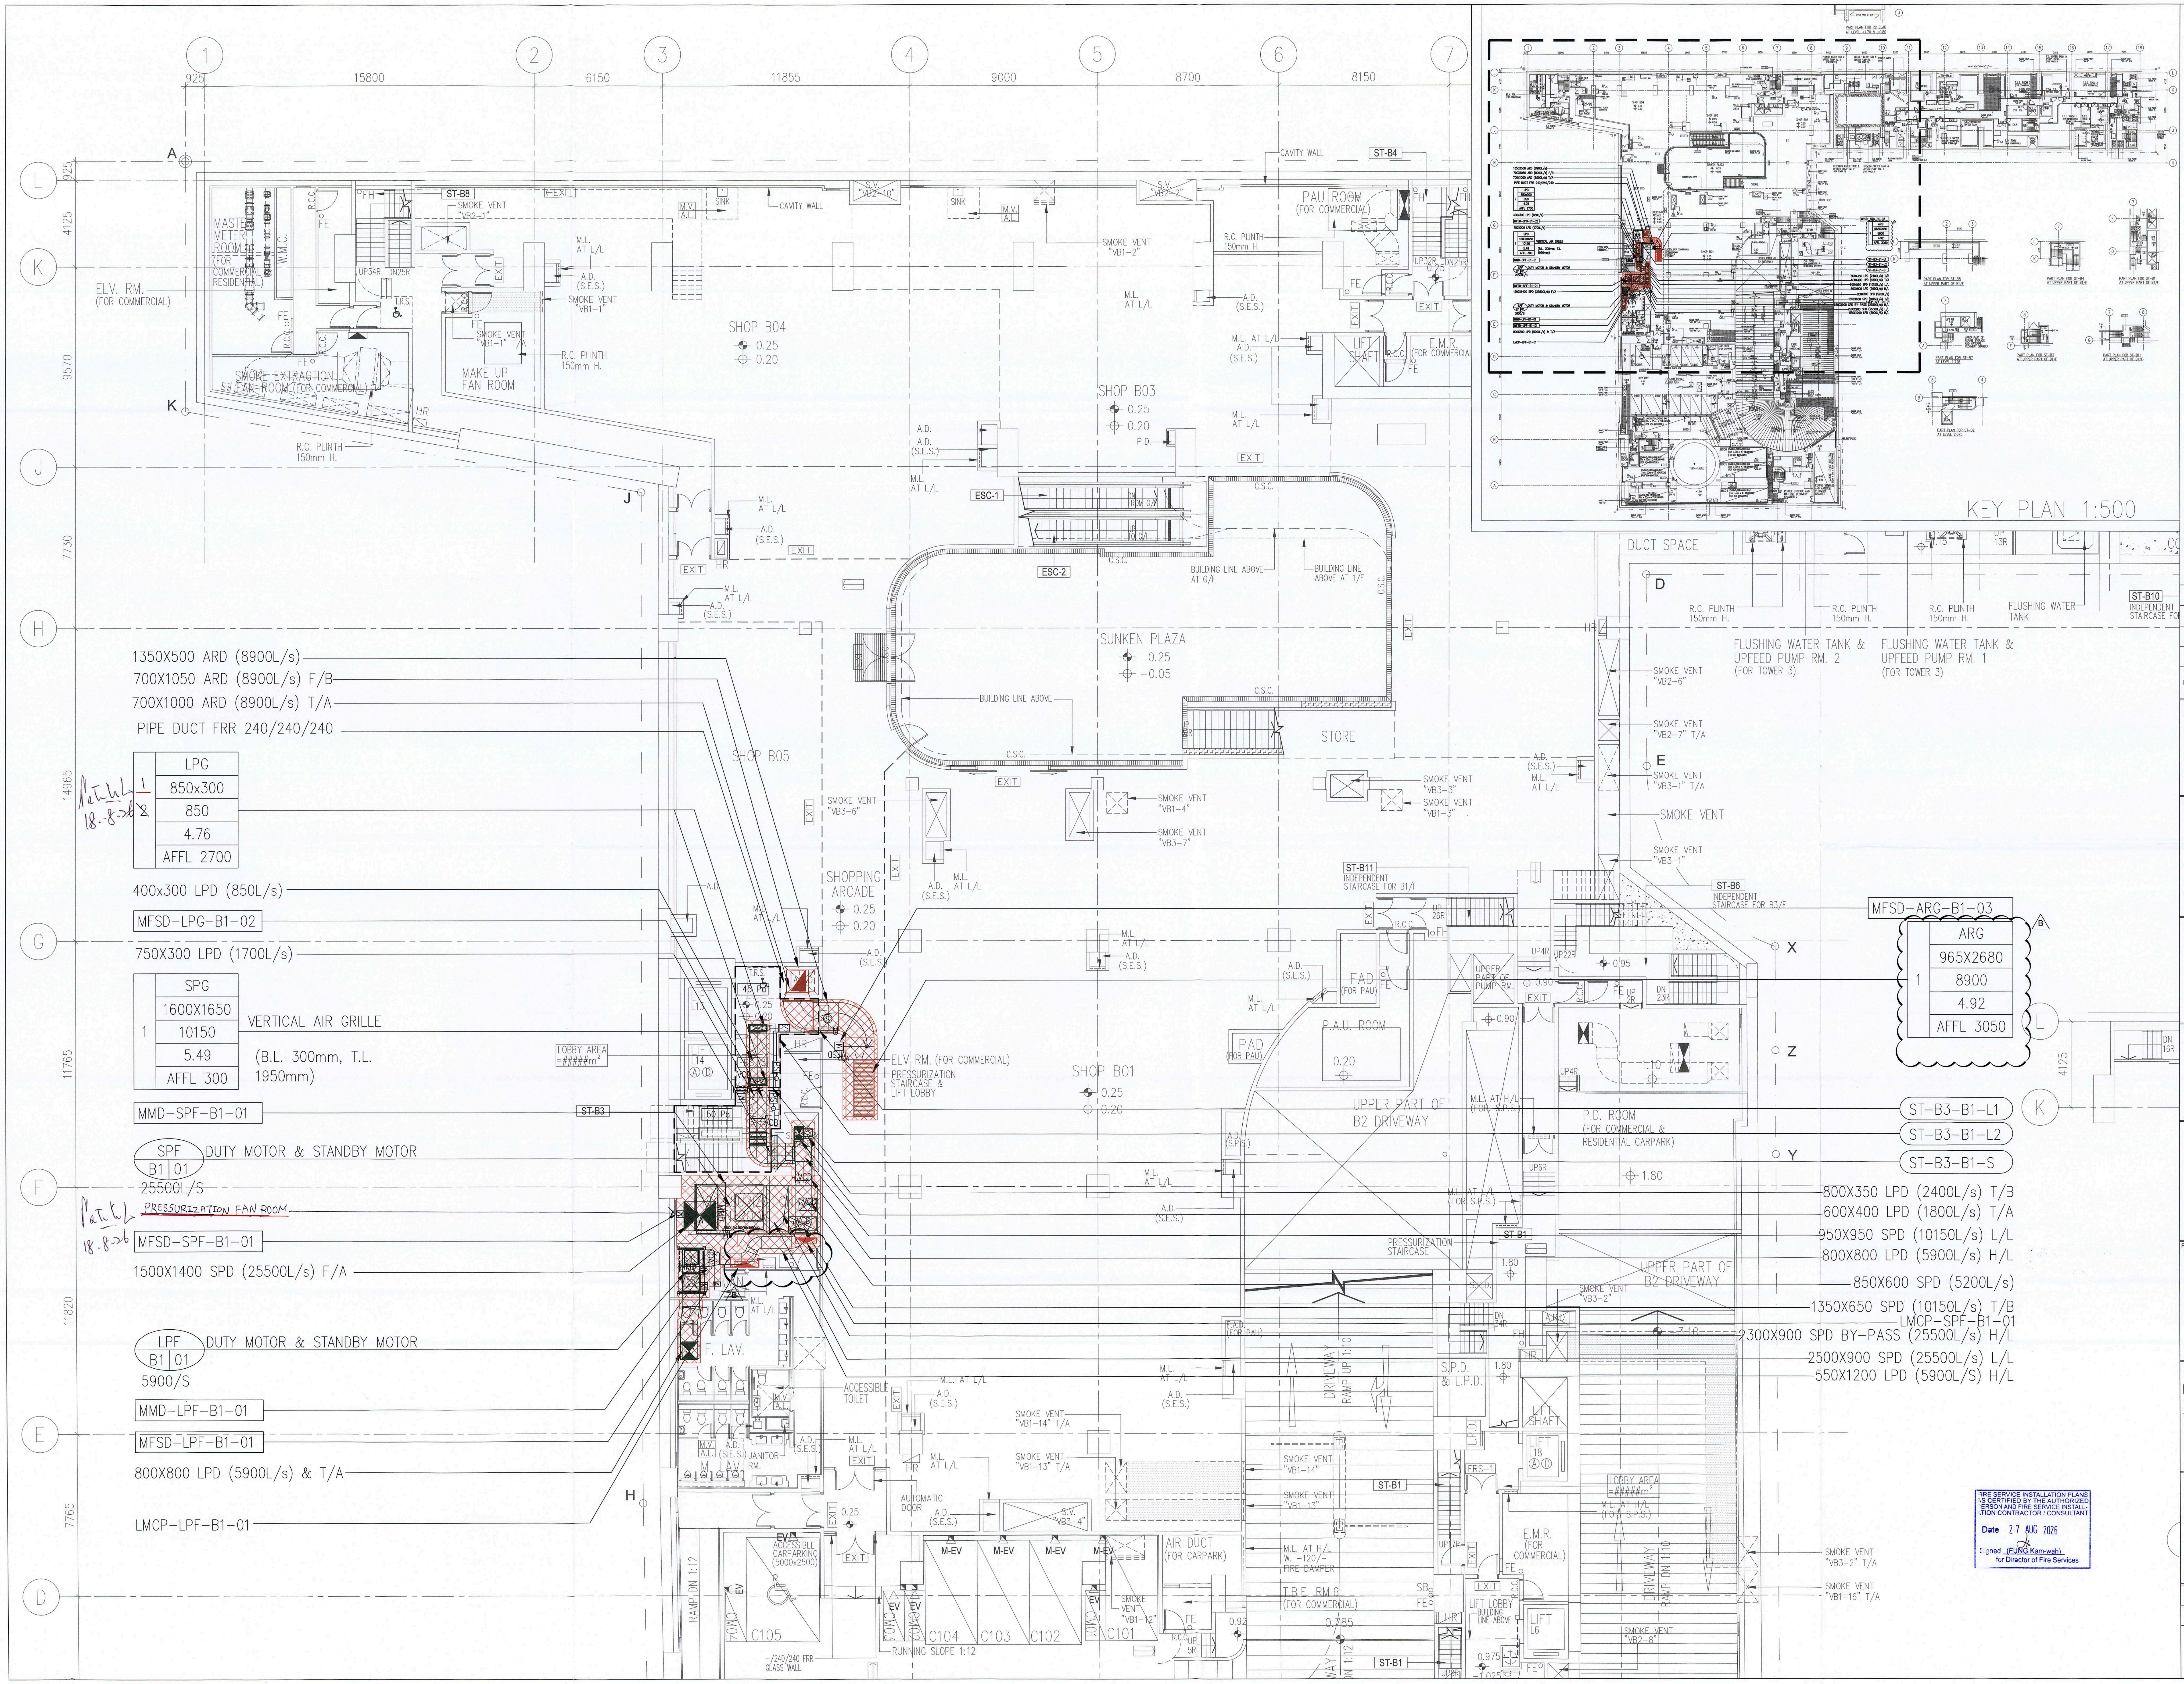
1
2
3
4
5
6
7
925
15800
6150
11855
9000
8700
8150
L
K
J
H
G
F
E
D
A
925
4125
9570
7730
14965
11765
11820
7765
ELV. RM.
(FOR COMMERCIAL)
MASTER METER ROOM (FOR COMMERCIAL/RESIDENTIAL)
W.M.C.
SMOKE EXTRACTION FAN ROOM (FOR COMMERCIAL)
MAKE UP FAN ROOM
R.C. PLINTH 150mm H.
SHOP B04
SHOP B03
SHOP B05
SHOP B01
SHOPPING ARCADE
SUNKEN PLAZA
STORE
ESC-1
ESC-2
PAU ROOM (FOR COMMERCIAL)
E.M.R. (FOR COMMERCIAL)
LIFT SHAFT
CAVITY WALL
ST-B8
ST-B4
ST-B3
ST-B1
ST-B6
INDEPENDENT STAIRCASE FOR B3/F
ST-B11
INDEPENDENT STAIRCASE FOR B1/F
ST-B10
INDEPENDENT STAIRCASE FOR B1/F
DUCT SPACE
FLUSHING WATER TANK & UPFEED PUMP RM. 2 (FOR TOWER 3)
FLUSHING WATER TANK & UPFEED PUMP RM. 1 (FOR TOWER 3)
FLUSHING WATER TANK
P.A.U. ROOM
P.D. ROOM (FOR COMMERCIAL & RESIDENTIAL CARPARK)
UPPER PART OF B2 DRIVEWAY
PRESSURIZATION STAIRCASE
ELV. RM. (FOR COMMERCIAL)
PRESSURIZATION STAIRCASE & LIFT LOBBY
LOBBY AREA
F. LAV.
ACCESSIBLE TOILET
JANITOR RM.
AUTOMATIC DOOR
ACCESSIBLE CARPARKING (5000x2500)
C105
C104
C103
C102
C101
AIR DUCT (FOR CARPARK)
T.B.E. RM.6 (FOR COMMERCIAL)
LIFT LOBBY
DRIVEWAY
RAMP DN 1:12
RUNNING SLOPE 1:12
KEY PLAN 1:500
1350X500 ARD (8900L/s)
700X1050 ARD (8900L/s) F/B
700X1000 ARD (8900L/s) T/A
PIPE DUCT FRR 240/240/240
LPG
1
~~2~~
850x300
850
4.76
AFFL 2700
400x300 LPD (850L/s)
MFSD-LPG-B1-02
750X300 LPD (1700L/s)
SPG
1
1600X1650
10150
5.49
AFFL 300
VERTICAL AIR GRILLE
(B.L. 300mm, T.L. 1950mm)
MMD-SPF-B1-01
SPF B1 01
DUTY MOTOR & STANDBY MOTOR
25500L/S
PRESSURIZATION FAN ROOM
MFSD-SPF-B1-01
1500X1400 SPD (25500L/s) F/A
LPF B1 01
DUTY MOTOR & STANDBY MOTOR
5900/S
MMD-LPF-B1-01
MFSD-LPF-B1-01
800X800 LPD (5900L/s) & T/A
LMCP-LPF-B1-01
MFSD-ARG-B1-03
B
ARG
1
965X2680
8900
4.92
AFFL 3050
ST-B3-B1-L1
ST-B3-B1-L2
ST-B3-B1-S
X
Z
Y
800X350 LPD (2400L/s) T/B
600X400 LPD (1800L/s) T/A
950X950 SPD (10150L/s) L/L
800X800 LPD (5900L/s) H/L
850X600 SPD (5200L/s)
1350X650 SPD (10150L/s) T/B
LMCP-SPF-B1-01
2300X900 SPD BY-PASS (25500L/s) H/L
2500X900 SPD (25500L/s) L/L
550X1200 LPD (5900L/S) H/L

18.8.26

18.8.26

FIRE SERVICE INSTALLATION PLANS AS CERTIFIED BY THE AUTHORIZED PERSON AND FIRE SERVICE INSTALLATION CONTRACTOR / CONSULTANT
Date 27 AUG 2026
Signed (FUNG Kam-wah)
for Director of Fire Services

LOO Kwan Wai
(RPE No.: RP0260258)

NO.	DATE	REVISIONS	DRAFTED	CHECKED	DESIGNED	REVIEWED
B	06/2026	FSD THIRD SUBMISSION	HYH	WWC	HYH	TKL
A	07/2025	FSD SECOND SUBMISSION	HYH	WWC	HYH	TKL
0	03/2025	FSD FIRST SUBMISSION	HYH	WWC	HYH	TKL

CLIENT:

NATION STAR DEVELOPMENT LIMITED
75/F, 8 Finance Street,
Central, Hong Kong

PROJECT ARCHITECT & AUTHORIZED PERSON:

RONALD LU & PARTNERS
呂元祥建築師事務所
33rd Floor, Wu Chung house, 213 Queen's Road East,
Wanchai, Hong Kong

STRUCTURAL/GEOTECHNICAL

wsp
7/F, One Kowloon
1 Wang Yuen Street
Kowloon Bay, Hong Kong

BUILDING SERVICES ENGINEER:

wsp
7/F, One Kowloon
1 Wang Yuen Street
Kowloon Bay, Hong Kong

QUANTITY SURVEYOR:

ARCADIS
17/F, Two Harbour Square, 180 Wai Yip Street,
Kwun Tong, Kowloon
Hong Kong

FIRE SERVICES CONTRACTOR:

開創工程有限公司
GRAND CREATIVE ENGINEERS LIMITED
CLASS 1, 2, 3 REGISTERED FIRE SERVICES CONTRACTOR
WSD LICENSED PLUMBER (GRADE 1)
EMSD REGISTERED ELECTRICAL CONTRACTOR

陳廣開
Chan Kwong Hoi
Director

Unit D, 2/F, Cheong Wah Comm. Bldg., 900-904 Canton Road, Kowloon.
Mobile : 9015 9586 Tel : 3612 5782 Fax : 3612 5785
Email : info@grandcreative.com.hk

PROJECT:

PROPOSED DEVELOPMENT AT BAILEY STREET & WING KWONG STREET,
TO KWA WAN, KOWLOON
INLAND LOT NO. 11279
(URA PROJECT KC-009)

TITLE:

STAIRCASE PRESSURIZATION SYSTEM – B1 LAYOUT (ST-B3)

⑦

DATE: 06/2026		SCALE: 1:100@A0	
DRAFTED: HYH	CHECKED: WWC	DESIGNED: HYH	REVIEWED: TKL
JOB NO. 2503373A	DRAWING NO. 2503373A/SPS/STB3/203		REV. NO. B