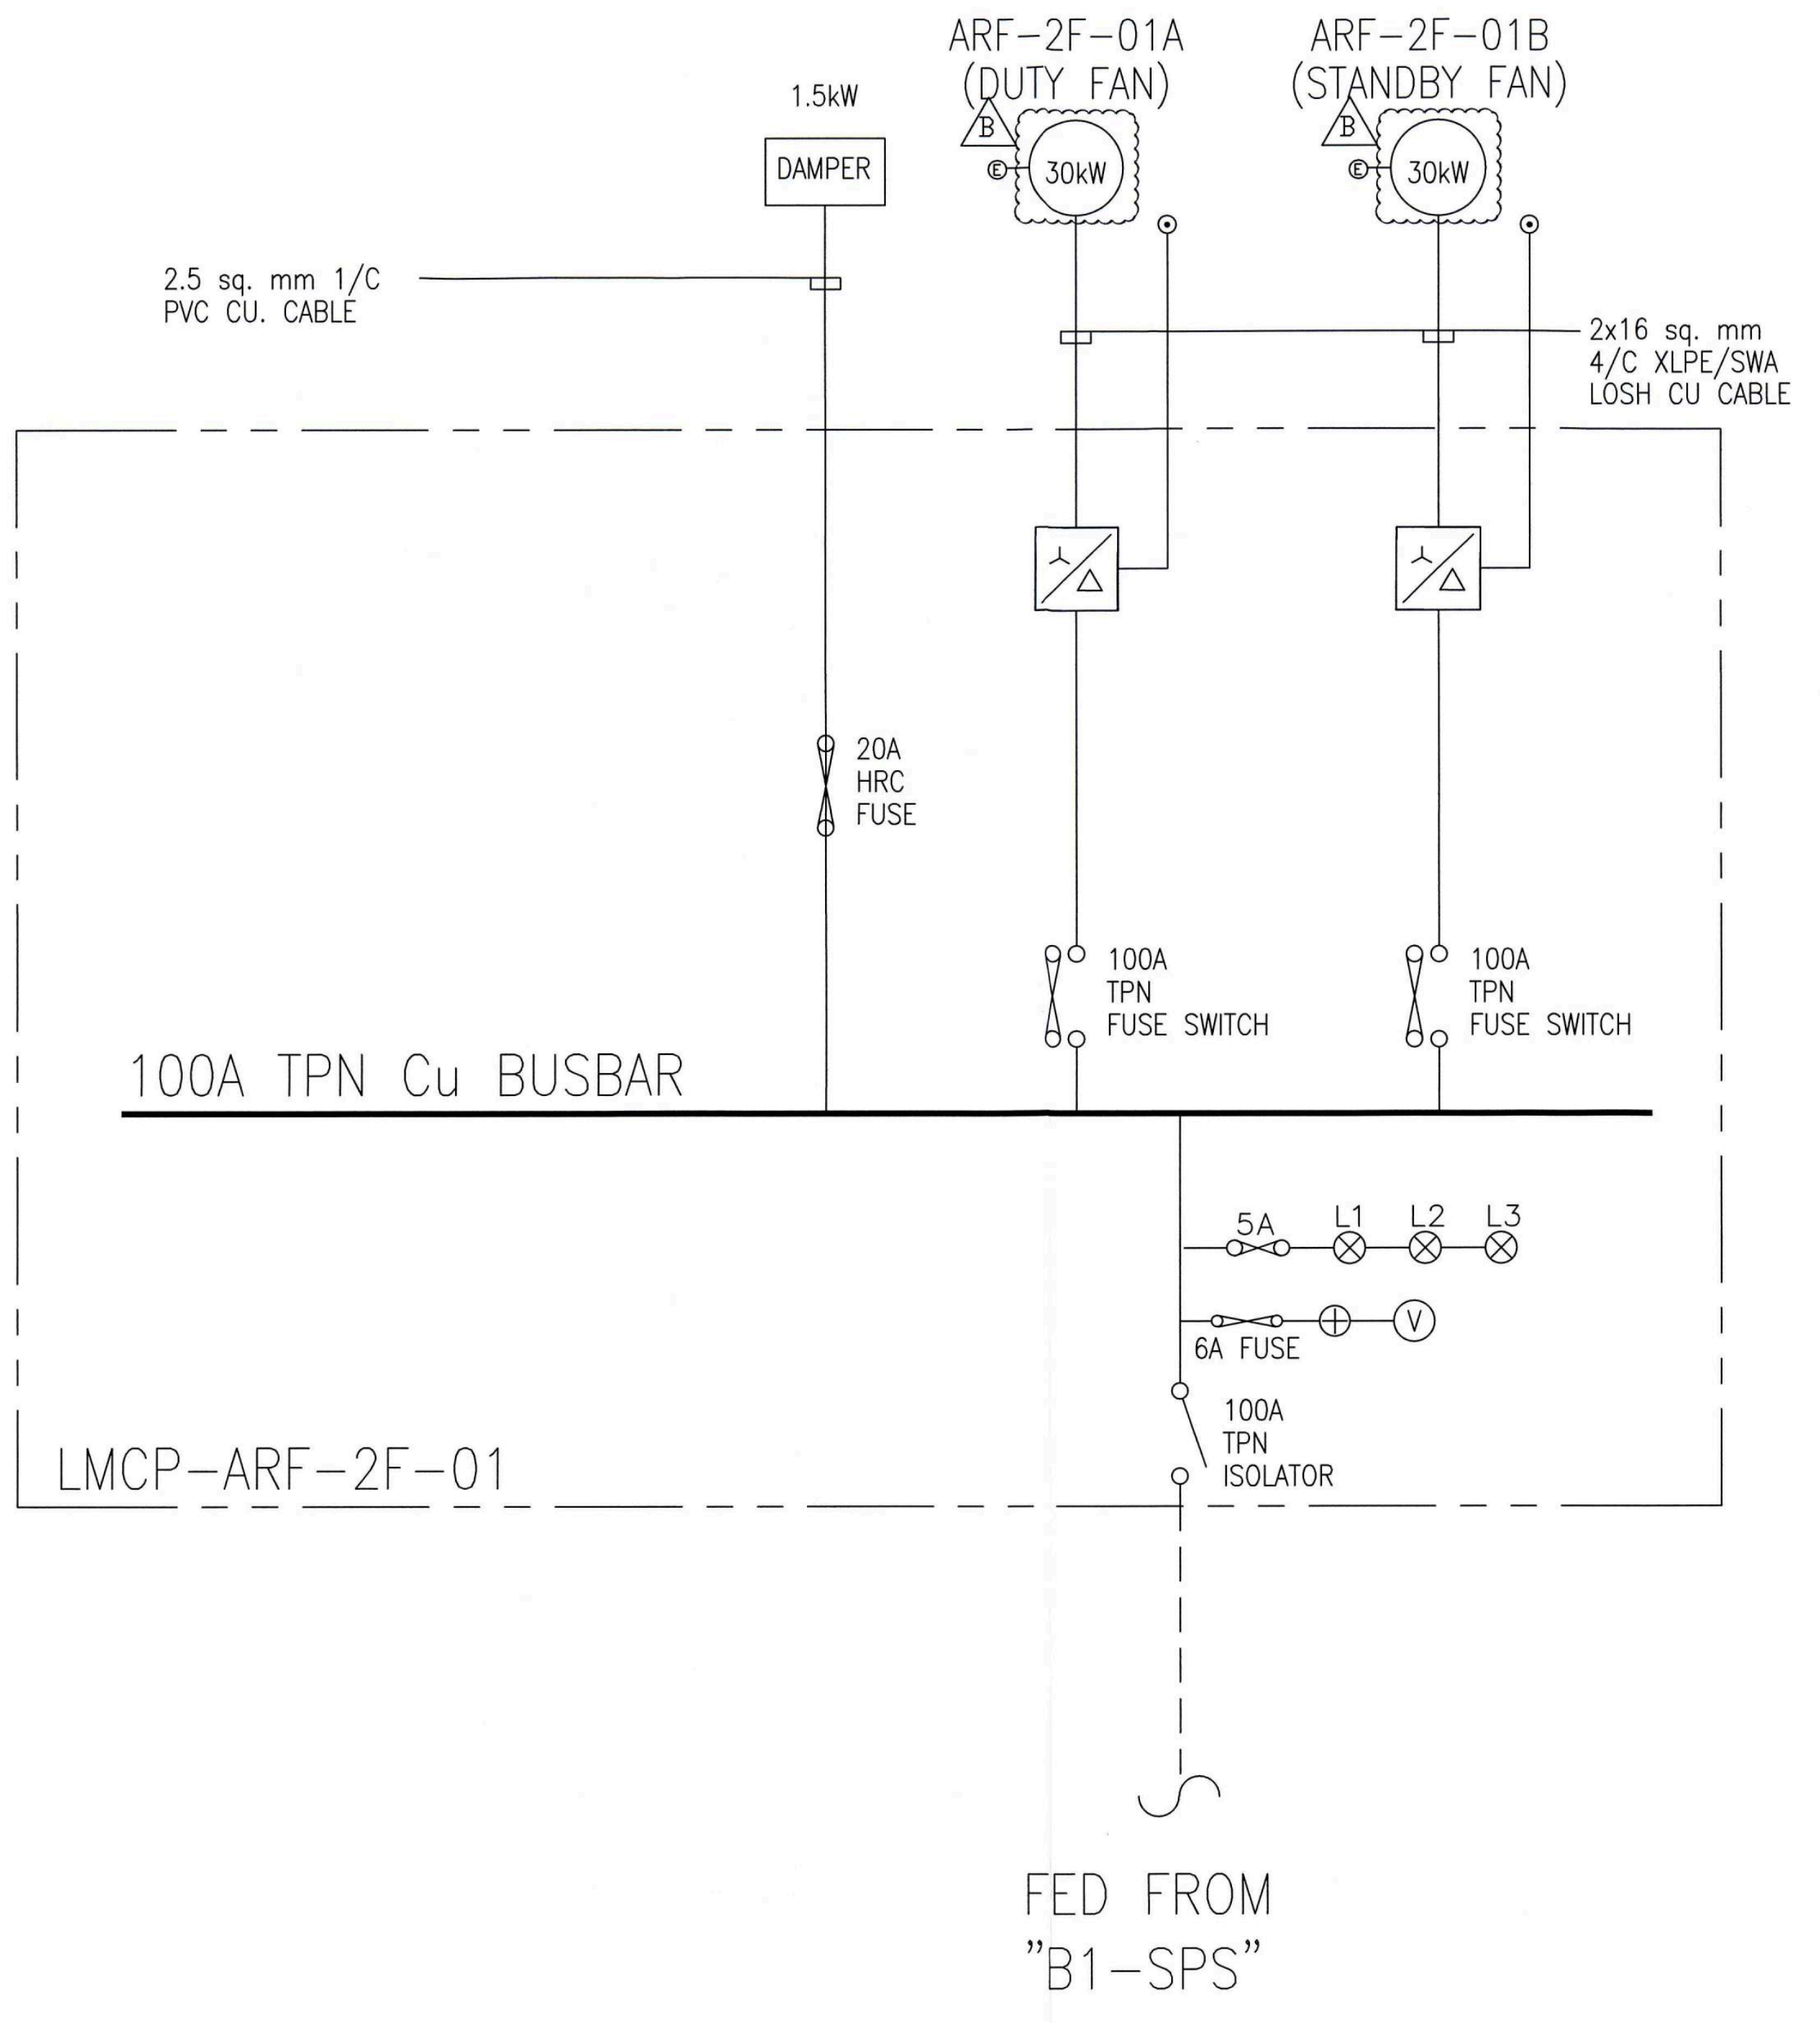

## ABBREVATION

| | |
|---|---|
| NO | NORMAL OPEN |
| NC | NORMAL CLOSE |
| LMCP | LOCAL MOTOR CONTROL PANEL |
| ATS | AUTOMATIC CHANGEOVER SWITCH |

## LEGEND

| | |
|---|---|
| | TPN MCCB<br>- TRIPLE POLE & NEUTRAL MOULDED CASE CIRCUIT BREAKER |
| | SPN MCB<br>- SINGLE POLE & NEUTRAL MINIATURE CIRCUIT BREAKER |
| | TPN F/S OR TPN S/F<br>- TRIPLE POLE & NEUTRAL FUSE SWITCH / SWITCHED FUSE |
| Ⓐ | AMMETER (240° SCALE) |
| Ⓥ | VOLTMETER (240° SCALE) |
| PF | POWER FACTOR METER (240° SCALE) |
| 3x0/C<br>1xE/F | IDMT OVERCURRNT PROTECTION RELAY AND EARTH FAULT RELAY |
| | AMMETER SELECTOR |
| ⊕ | VOLTMETER SELECTOR |
| | AUTOMATIC STAR-DELTA STARTER |
| E/F | EARTH FAULT |
| | MCT - MEASURING CURRENT TRANSFORMER<br>PCT - PROTECTION CURRENT TRANSFORMER |
| | HRC CONTROL FUSE |
| | INDICATING LAMP<br>'R' RED<br>'Y' YELLOW<br>'B' BLUE |
| | CAPACITOR, 5-STEP AUTOMATIC POWER FACTOR REGULATOR |
| BBC | BUSBAR CHAMBER |
| Ⓔ | EMERGENCY STOP PUSH BOTTON |
| UV | UNDERVOLTAGE RELAY |
| FI | FREQUENCY INVERTOR (SHALL REPEAT TO BMS FOR CONTROL AND MONITORING) |
| N.C. N.O. | AUTOMATIC CHANGEOVER CONTACTOR |
| H | HEAT OR OVERLOAD |

FIRE SERVICE INSTALLATION PLANS AS CERTIFIED BY THE AUTHORIZED PERSON AND FIRE SERVICE INSTALLATION CONTRACTOR / CONSULTANT
Date 27 AUG 2026
Signed (FUNG Kam-wah)
for Director of Fire Services

FOR INFORMATION ONLY

LOO Kwan Wai
(RPE No.: RP0260258)

| NO. | DATE | REVISIONS | DRAFTED | CHECKED | DESIGNED | REVIEWED |
|---|---|---|---|---|---|---|
| | | | | | | |
| B | 06/2026 | FSD THIRD SUBMISSION | HYH | WWC | HYH | TKL |
| A | 07/2025 | FSD SECOND SUBMISSION | HYH | WWC | HYH | TKL |
| 0 | 03/2025 | FSD FIRST SUBMISSION | HYH | WWC | HYH | TKL |

CLIENT:

NATION STAR DEVELOPMENT LIMITED
75/F, 8 Finance Street,
Central, Hong Kong

PROJECT ARCHITECT & AUTHORIZED PERSON:

RONALD LU & PARTNERS
呂元祥建築師事務所
33rd Floor, Wu Chung house, 213 Queen's Road East,
Wanchai, Hong Kong

STRUCTURAL/GEOTECHNICAL

wsp
7/F, One Kowloon
1 Wang Yuen Street
Kowloon Bay, Hong Kong

BUILDING SERVICES ENGINEER:

wsp
7/F, One Kowloon
1 Wang Yuen Street
Kowloon Bay, Hong Kong

QUANTITY SURVEYOR:

ARCADIS
17/F, Two Harbour Square, 180 Wai Yip Street,
Kwun Tong, Kowloon
Hong Kong

FIRE SERVICES CONTRACTOR:

開創工程有限公司
GRAND CREATIVE ENGINEERS LIMITED
CLASS 1, 2, 3 REGISTERED FIRE SERVICES CONTRACTOR
WSD LICENSED PLUMBER (GRADE 1)
EMSD REGISTERED ELECTRICAL CONTRACTOR

陳廣開
**Chan Kwong Hoi**
Director

Unit D, 2/F, Cheong Wah Comm. Bldg., 900-904 Canton Road, Kowloon.
Mobile : 9015 9586 Tel : 3612 5782 Fax : 3612 5785
Email : info@grandcreative.com.hk

PROJECT:

PROPOSED DEVELOPMENT AT BAILEY STREET & WING KWONG STREET,
TO KWA WAN, KOWLOON
INLAND LOT NO. 11279
(URA PROJECT KC-009)

TITLE:

STAIRCASE PRESSURIZATION SYSTEM – ELECTRICAL & LMCP WIRING DIAGRAM
(SHEET 2 OF 4) (ST-B3)

⑭

| | | | |
|---|---|---|---|
| DATE: 06/2026 | | SCALE: NTS@A0 | |
| DRAFTED: HYH | CHECKED: WWC | DESIGNED: HYH | REVIEWED: TKL |
| JOB NO. | DRAWING NO. | | REV. NO. |
| 2503373A | 2503373A/SPS/STB3/402 | | B |