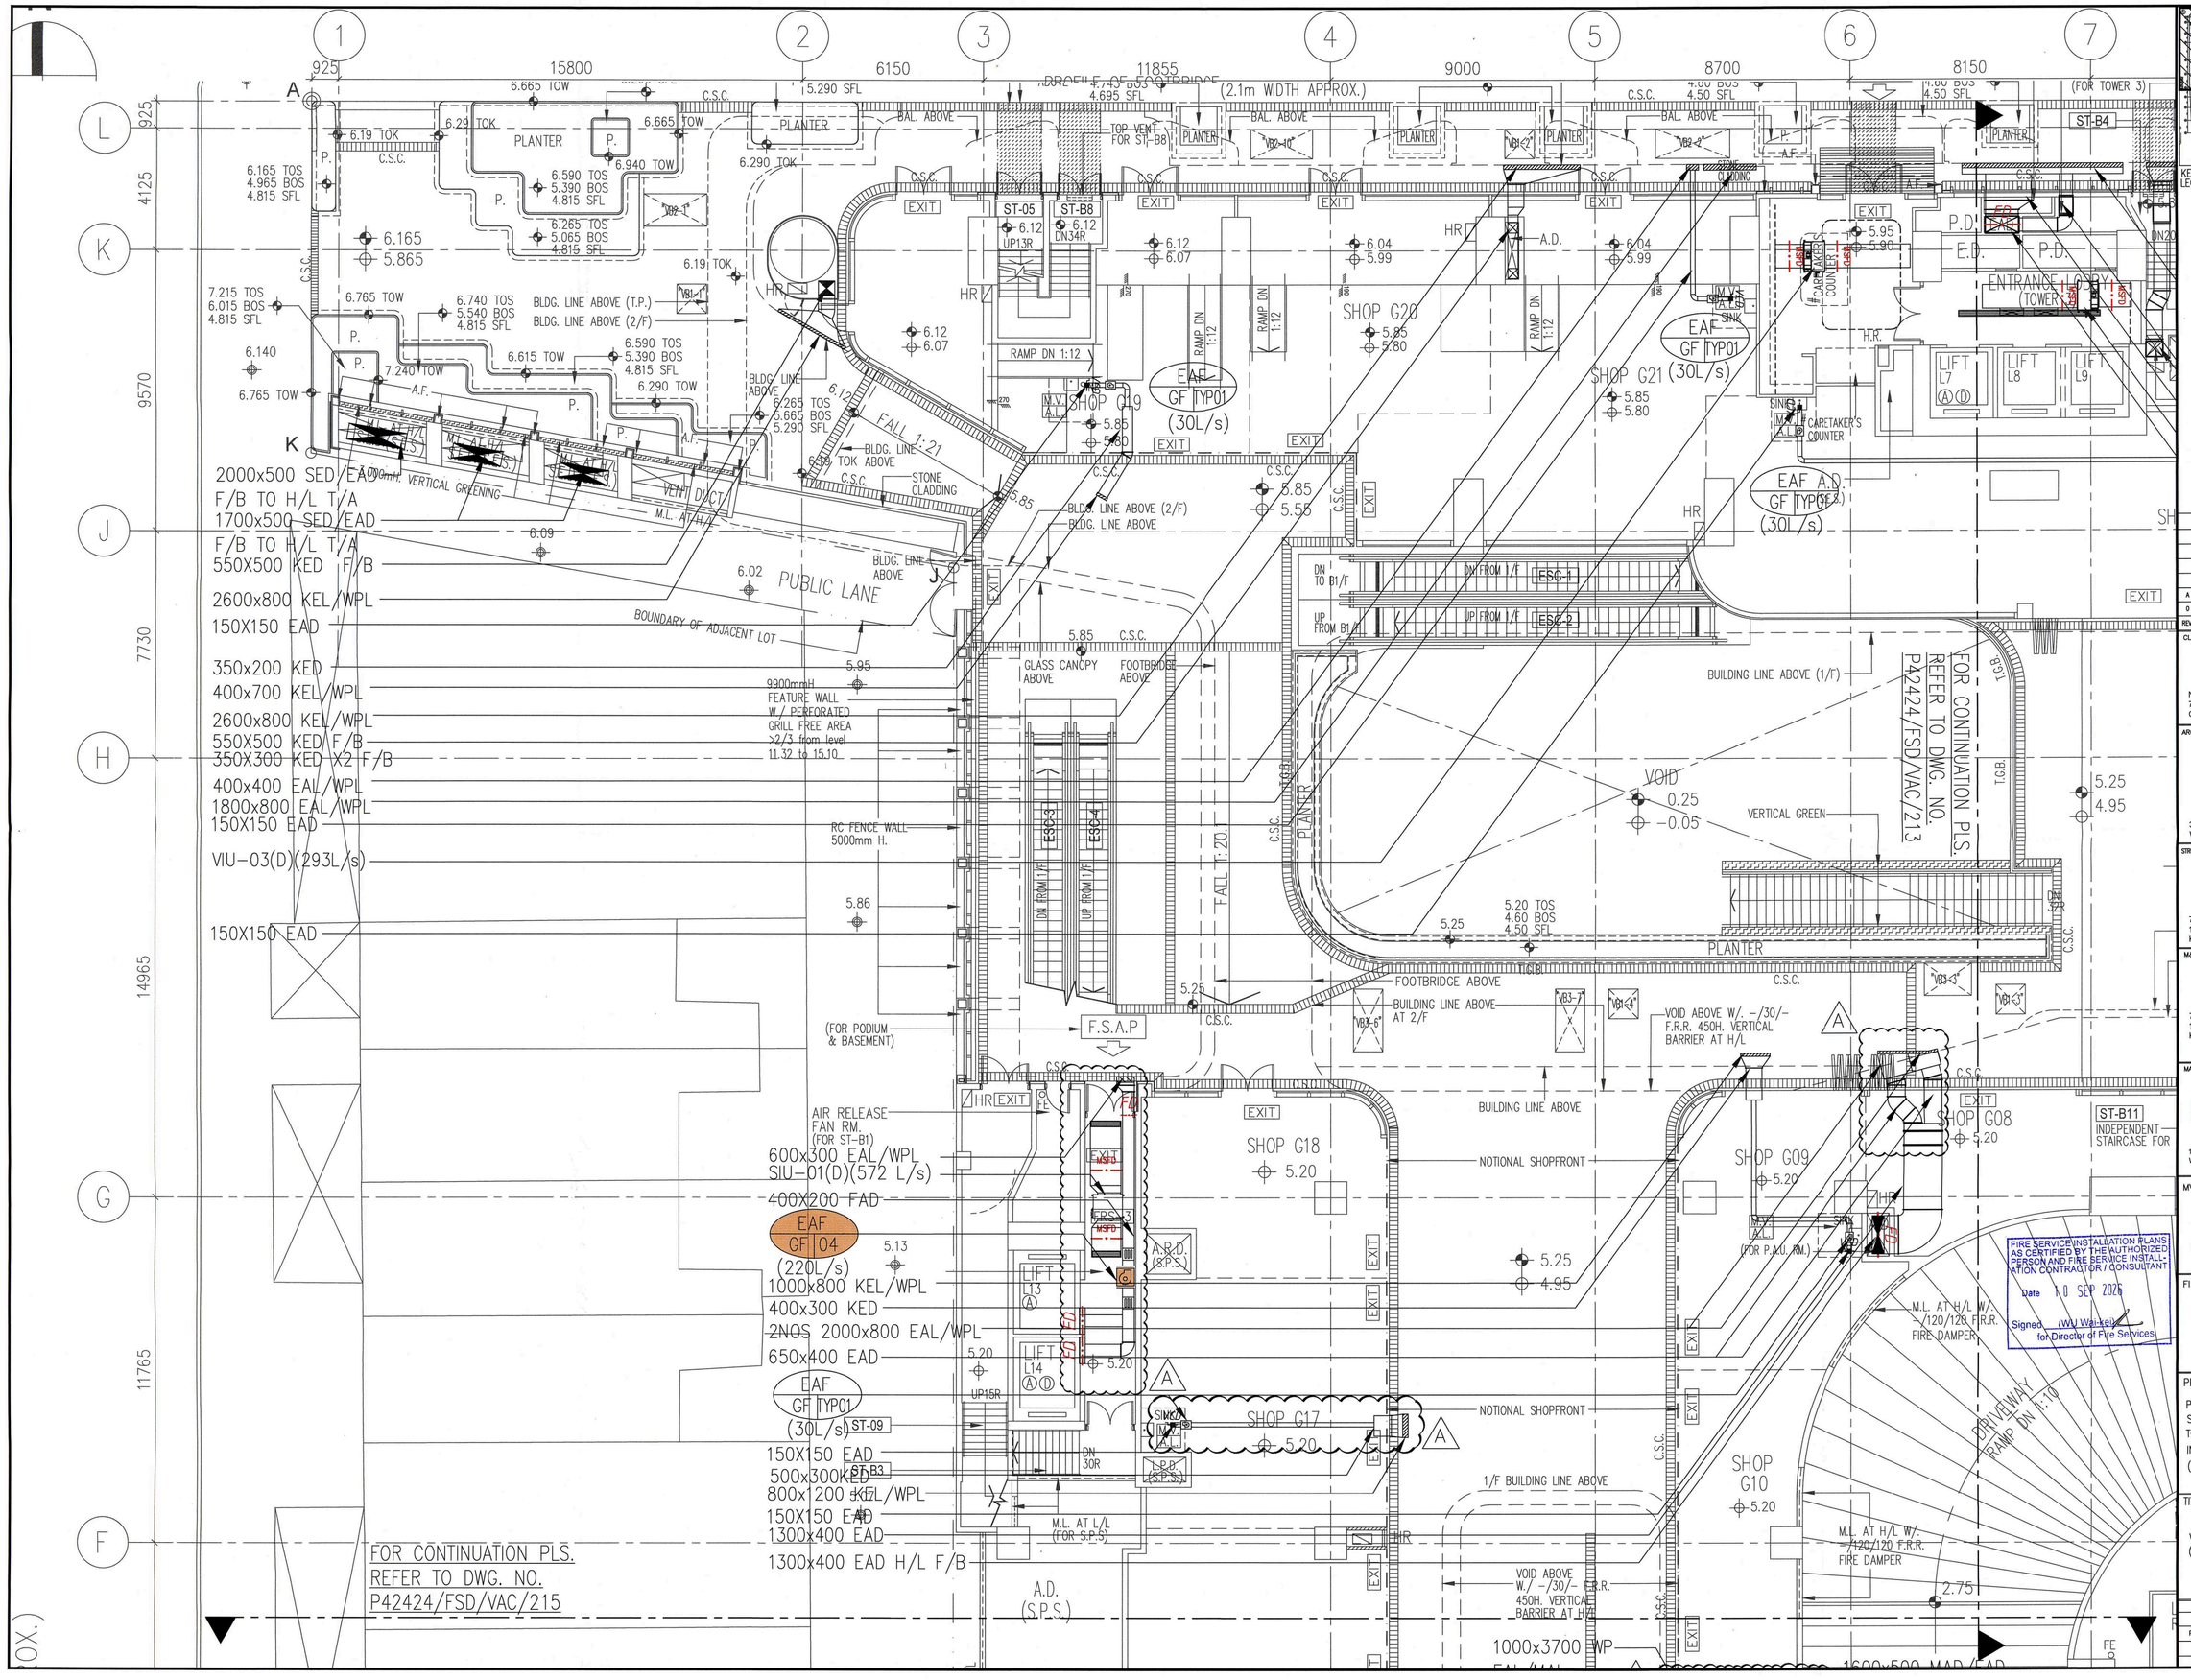


KEY PLAN
LEGEND REFER TO P42424-FSD-VAC-001

REV.	DESCRIPTION	DATE
A	SECOND SUBMISSION	17/06/2026
0	FIRST SUBMISSION	18/11/2025

CLIENT:

NATION STAR DEVELOPMENT LIMITED
75/F, 8 Finance Street,
Central, Hong Kong

ARCHITECT:

RONALD LU & PARTNERS
呂元祥建築師事務所
33rd Floor, Wu Chung house, 213 Queen's Road East,
Wanchai, Hong Kong

STRUCTURAL GEOTECHNICAL:

wsp
7/F, One Kowloon
1 Wang Yuen Street
Kowloon Bay, Hong Kong

M&E SERVICES CONSULTANT:

wsp
7/F, One Kowloon
1 Wang Yuen Street
Kowloon Bay, Hong Kong

MAIN CONTRACTOR

中國海外基建工程有限公司
CHINA OVERSEAS BUILDING CONSTRUCTION LIMITED
139, China Overseas Building, Hennessy Road
Wan Chai, Hong Kong

MVAC SUB-CONTRACTOR:

Sun Yu Chau Engineering Company Limited
12/F, Khoon Centre, No. 9 Hung To Road
Kwun Tong, Kowloon, Hong Kong
TEL : (852)2345 9255 FAX : (852)2797 0387

FIRE SERVICES CONTRACTOR:

開創工程有限公司
GRAND CREATIVE ENGINEERS LIMITED

PROJECT:

PROPOSED DEVELOPMENT AT BAILEY STREET & WING KWONG STREET, TO KWA WAN, KOWLOON
INLAND LOT NO. 11279
(URA PROJECT KC-009)

TITLE:

VAC LAYOUT PLAN AT G/F
(SHEET 1 OF 4)

JOB NO.	SCALE	DATE	DRAWING BY
P42424	1:100 @A1	17/06/2026	OY
P42424/FSD/VAC/212		CHECKED BY	APPROVED BY
		KM	WW

REV. 0 A