

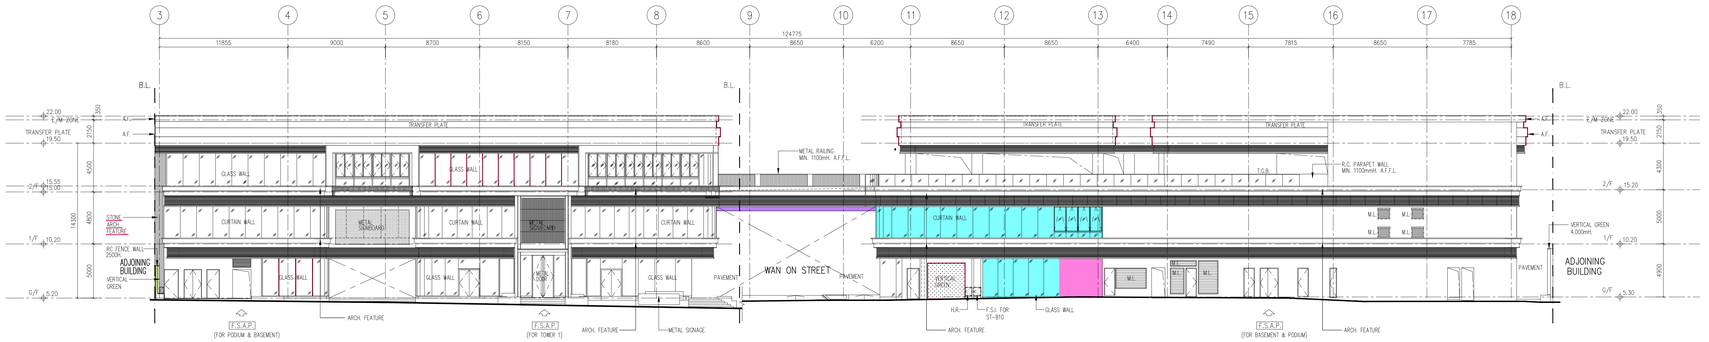



E1 ELEVATION (PODIUM)
SCALE :1:200

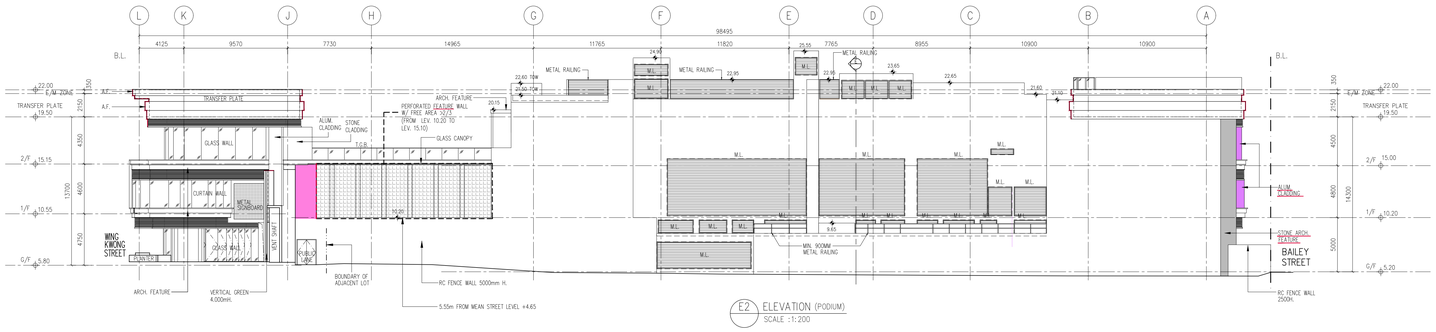


E2 ELEVATION (PODIUM)
SCALE :1:200

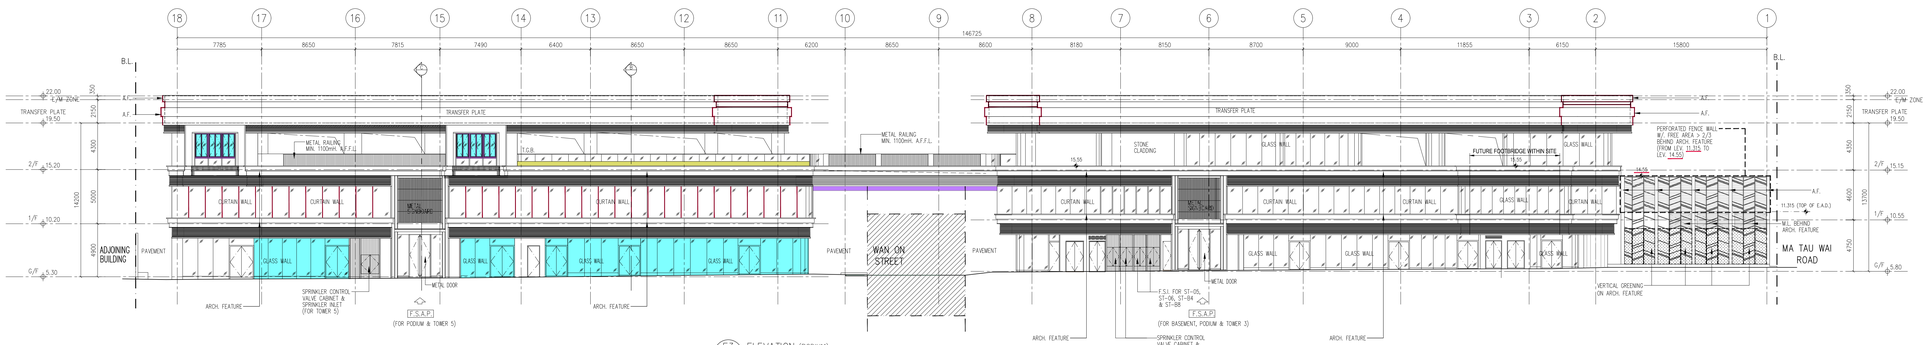

E3 ELEVATION (PODIUM)
SCALE :1:200

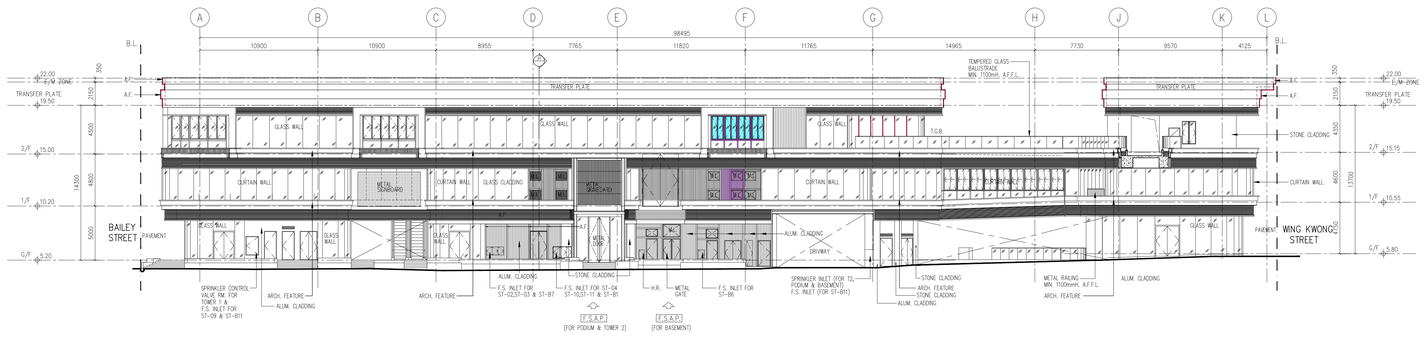

E4 ELEVATION (PODIUM)
SCALE :1:200

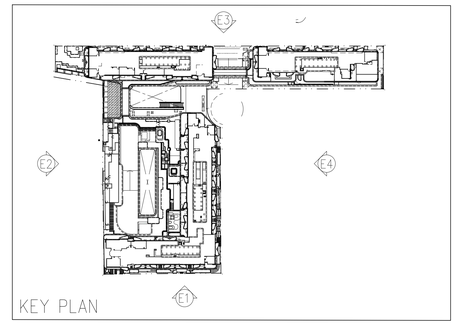

B.D. Ref : 80 2/4024/21

BIM Ref : - -

F.S.D. Ref : - -

D.L.O. Ref : - -

Rev.	Description	Drawn	Checked	Approved	Date
-	1st Submission	WY	AW	AL	07/2022
A	2nd Submission	WY	AW	AL	11/2022
B	1st Amendment	TWM	AW	AL	04/2023
C	2nd Amendment	TWM	AW	AL	12/2023
D	3rd Amendment	TWM	AW	AL	04/2024
D	3rd Amendment (Re-submission)	TWM	AW	AL	05/2024
E	5th Amendment	TWM	AW	AL	12/2024
E	5th Amendment (Re-submission)	TWM	AW	AL	02/2025
F	8th Amendment	LKM	AW	AL	05/2025
G	9th Amendment	LKM	AW	AL	08/2025
G	9th Amendment (Re-submission)	TWM	AW	AL	10/2025
H	10th Amendment	TWM	AW	AL	12/2025
I	11th Amendment	TWM	AW	AL	02/2026

Type II works
The works shown on these plans are Type II works (Building Amendment) in respect of which consent is applied for the purpose of Fast Track consent application under regulation 33 of the Building (Administration) Regulations.

RONALD LU & PARTNERS

呂元祥建築師事務所

Check all measurements on site. Do not scale off drawings. Discrepancies between drawings and site conditions and any discrepancies are to be immediately reported to the Architect.
This drawing remains the copyright property of the Architect and is not to be reproduced in whole or in part without permission of the Architect.

Project Title :
PROPOSED DEVELOPMENT AT BAILEY STREET & WING KWONG STREET TO KWA WAN, KOWLOON

Drawing Title :
PODIUM ELEVATION 1, 2, 3 & 4

Drawn By	TWM	Date	08/2025
Checked By	AW	Date	08/2025
Approved By	AL	Date	08/2025
Project No.	21163KL	Issue Date	08/2025

File Path :
I:\Bob Sha Jiao\2021\KL Bailey Street & Wing Kwong Street\DWG\SUBMISSION\[F-1-Final Amendment_Next Issue\(R)F2L-ZIP 2.dwg

Scale 1:200 By CAD

Drawing Number : A/GBP/21 Revision Number : I

Drawing Purpose
Buildings Department
Amended Plan


Digitally signed by LEUNG Kit Man Andy
APUN, BD(B)
16 March 2026

Received on 16 March 2026


Plan Approved
(Digitally Signed)
TSOI Lap-san, Lapson
Senior Building Surveyor
for BUILDING AUTHORITY
17 March 2026

Note: This plan has been processed on a curtailed check basis under the centralized processing system as promulgated in PNAP ADM-19. The duties of the authorized person, registered structural engineer and/or registered geotechnical engineer concerned as specified under section 4(3)(b) and the provision of section 14(2)(c) of the Buildings Ordinance are of particular relevance in this regard.

TOWER 1

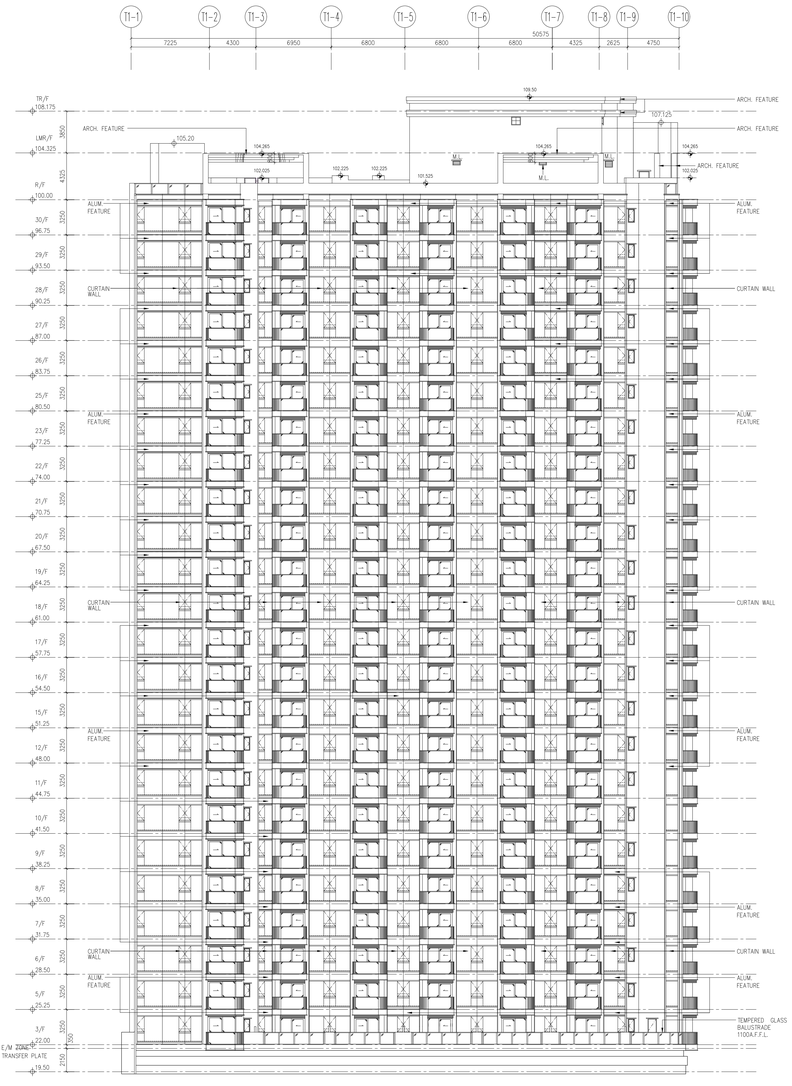
T1-1
T1-2
T1-3
T1-4
T1-5
T1-6
T1-7
T1-8
T1-9
T1-10
7225
4300
6950
6800
6800
6800
50575
4325
2625
4750
TR/F 108.175
LMR/F 104.325
R/F 100.00
30/F 96.75
29/F 93.50
28/F 90.25
27/F 87.00
26/F 83.75
25/F 80.50
23/F 77.25
22/F 74.00
21/F 70.75
20/F 67.50
19/F 64.25
18/F 61.00
17/F 57.75
16/F 54.50
15/F 51.25
12/F 48.00
11/F 44.75
10/F 41.50
9/F 38.25
8/F 35.00
7/F 31.75
6/F 28.50
5/F 25.25
3/F 22.00
E/M ZONE
TRANSFER PLATE
19.50
2650
4325
3250
2750
3250
3250
3250

TOWER 1 & TOWER 2

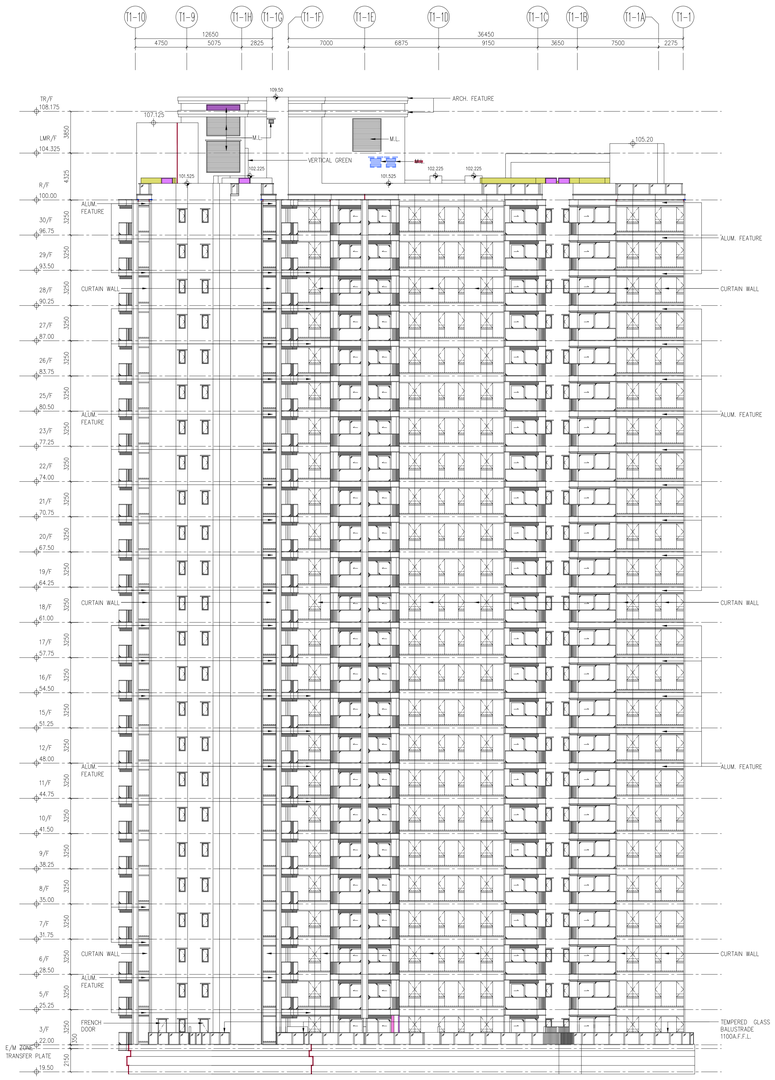


7 ELEVATION

TOWER 1 & TOWER 2



8 ELEVATION

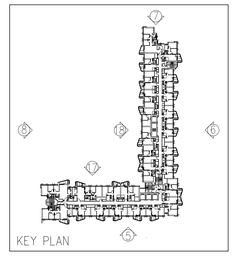

B.D. Ref : 80 2/4024/21

BIM Ref : - --

F.S.D. Ref : - --

D.L.O. Ref : - --

Rev.	Description	Drawn	Checked	Approved	Date
-	1st Submission	WY	AW	AL	07/2022
A	2nd Submission	WY	AW	AL	11/2022
B	1st Amendment	TWM	AW	AL	04/2023
C	2nd Amendment	TWM	AW	AL	12/2023
D	3rd Amendment	TWM	AW	AL	04/2024
D	3rd Amendment (Re-submission)	TWM	AW	AL	05/2024
E	5th Amendment	TWM	AW	AL	12/2024
E	5th Amendment (Re-submission)	TWM	AW	AL	02/2025
F	8th Amendment	LKM	AW	AL	05/2025
G	9th Amendment	LKM	AW	AL	08/2025
G	9th Amendment (Re-submission)	TWM	AW	AL	10/2025
H	10th Amendment	TWM	AW	AL	12/2025
I	11th Amendment	TWM	AW	AL	2/2026

Type II works
The works shown on these plans are Type II works (Building Amendment) in respect of which consent is applied for the purpose of Fast Track consent application under regulation 33 of the Building (Administration) Regulations.

RONALD LU & PARTNERS

呂元祥建築師事務所

Check all measurements on site. Do not scale off drawings.
This drawing is to be read in conjunction with the specification and any discrepancies are to be immediately reported to the Architect.
This drawing remains the copyright property of the Architect and is not to be reproduced in whole or part without permission of the Architect.

Project Title :
PROPOSED DEVELOPMENT
AT BAILEY STREET
& WING KWONG STREET
TO KWA WAN, KOWLOON

Drawing Title :
ELEVATION 7 & 8
(TOWER 1)

Drawn By	TWM	Date	08/2025
Checked By	AW	Date	08/2025
Approved By	AL	Date	08/2025
Project No.	21163KL	Issue Date	08/2025

File Path :
I:\Bim Proj 2\a2021\21KL Kiln Dev\1.0 Proj Info\2DWG\BASE\DGF 1\7+8 elevation1.test.dwg\Plt\21KL_GBP_B.stb

Scale 1:200 By CAD

Drawing Number : A/GBP/26

Revision Number : I

Drawing Purpose

Buildings Department
Amended Plan


Digitally signed by LEUNG Kit Man Andy
APVA (BOIS)
16 March 2026

Received on
16 March 2026

Plan Approved
(Digitally Signed)
TSOI Lap-san, Lapson
Senior Building Surveyor
for BUILDING AUTHORITY
17 March 2026


Note: This plan has been processed on a curtailed check basis under the centralized processing system as promulgated in PNAP ADM-19. The duties of the authorized person, registered structural engineer and/or registered geotechnical engineer concerned as specified under section 4(3)(b) and the provision of section 14(2)(c) of the Buildings Ordinance are of particular relevance in this regard.

TOWER 1

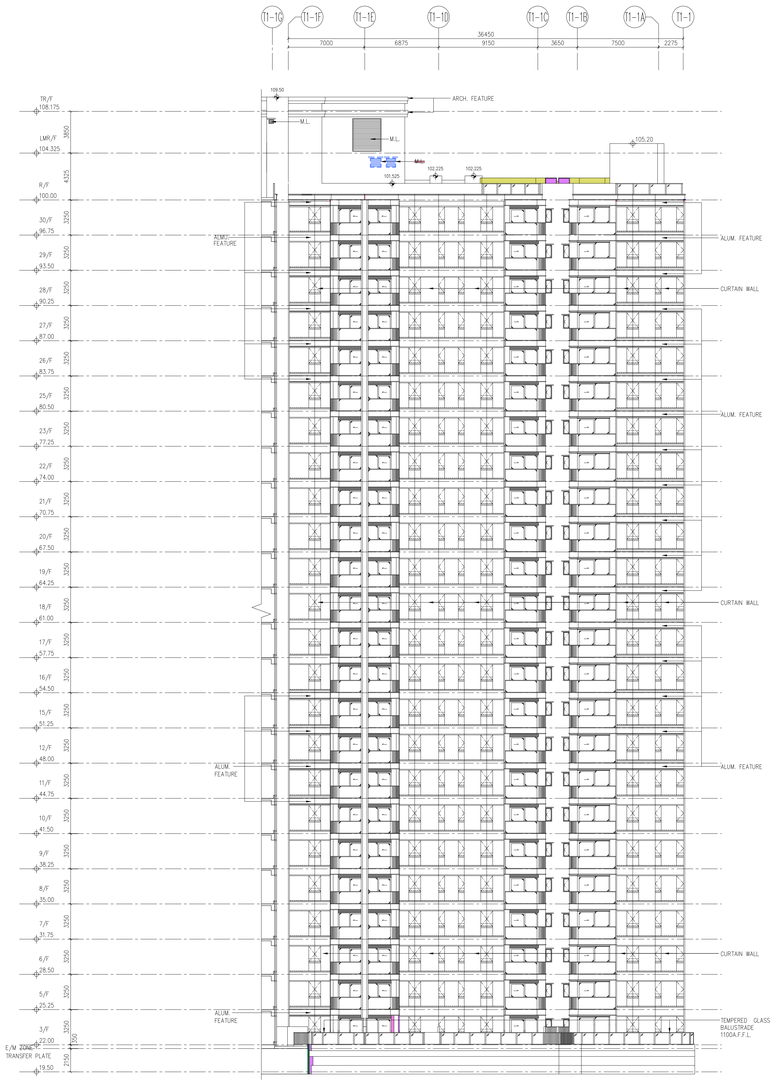


17 ELEVATION

TOWER 2

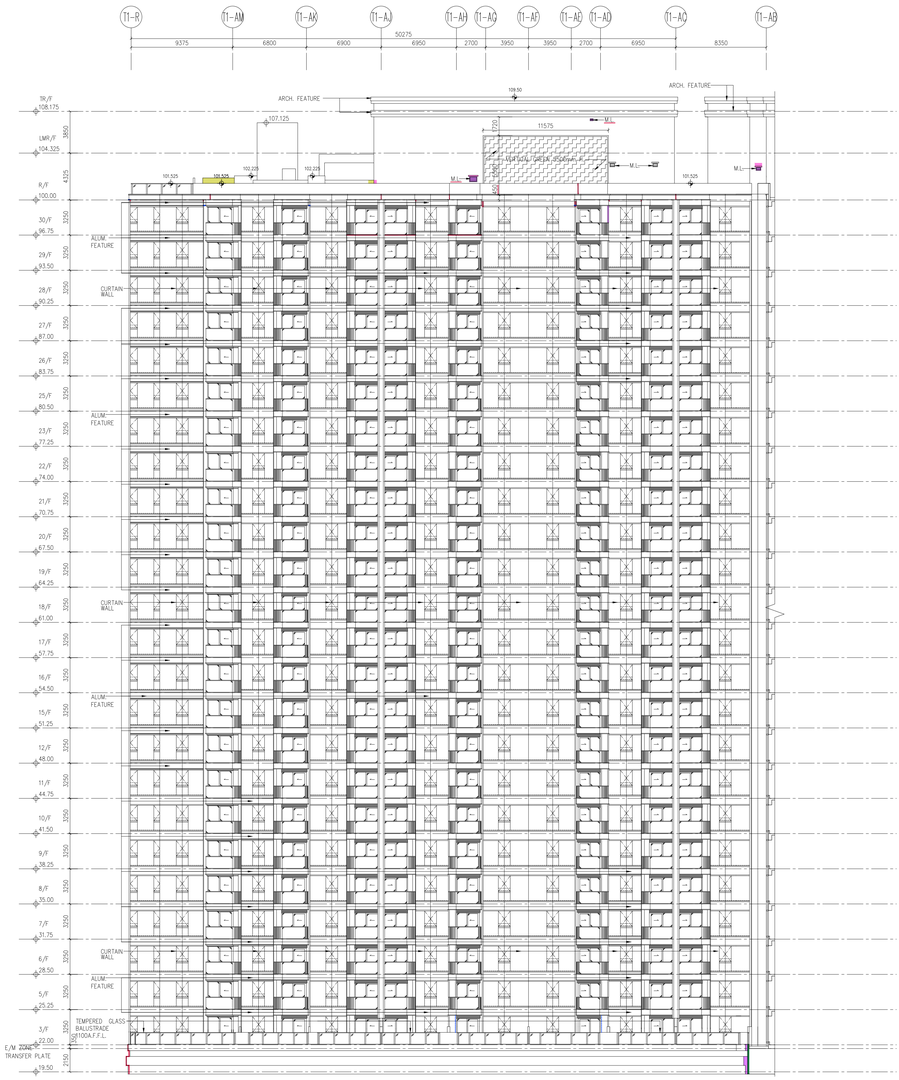

18 ELEVATION

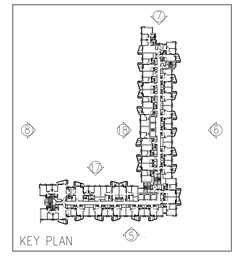

KEY PLAN

B.D. Ref :					
BD 2/4024/21					
BIM Ref :	-	-			
F.S.D. Ref :	-	-			
D.L.O. Ref :	-	-			

Rev.	Description	Drawn	Checked	Approved	Date
-	3rd Amendment	WAC	AW	AL	04/2024
A	5th Amendment	TWM	AW	AL	12/2024
A	5th Amendment (Re-submission)	TWM	AW	AL	02/2025
B	8th Amendment	LKM	AW	AL	05/2025
C	9th Amendment	LKM	AW	AL	08/2025
C	9th Amendment (Re-submission)	TWM	AW	AL	10/2025
D	10th Amendment	TWM	AW	AL	12/2025
E	11th Amendment	TWM	AW	AL	2/2026

Type II works
The works shown on these plans are Type II works (Building Amendment) in respect of which consent is applied for the purpose of Fast Track consent application under regulation 33 of the Building (Administration) Regulations.

RONALD LU & PARTNERS

呂元祥建築師事務所

Check all measurements on site. Do not scale off drawings.
Any discrepancies are to be read in conjunction with the Specification and any discrepancies are to be immediately reported to the Architect.
This drawing remains the copyright property of the Architect and is not to be reproduced in whole or in part without permission of the Architect.

Project Title :
PROPOSED DEVELOPMENT
AT BAILEY STREET
& WING KWONG STREET
TO KWA WAN, KOWLOON

Drawing Title :
ELEVATION 17 & 18
(TOWER 1 & TOWER 2)

Drawn By	TWM	Date	08/2025
Checked By	AW	Date	08/2025
Approved By	AL	Date	08/2025
Project No.	21163KL	Issue Date	08/2025

File Path : T:\Job 3Prj_Jan2021\21163_Bailey Street & Wing Kwong Street\DWG\BD\02\BD\2F 17-18\elevation1 Rev.E.dwg

Scale	1:200	By	CAD
Drawing Number :	A/GBP/26.1	Revision Number :	E

Drawing Purpose

Buildings Department
Amended Plan


Digitally signed by LEUNG Ka Man Andy
APUA | BOBS
16 March 2026

Received on
16 March 2026

Plan Approved
(Digitally Signed)
TSOI Lap-san, Lapson
Senior Building Surveyor
for BUILDING AUTHORITY
17 March 2026


Note: This plan has been processed on a curtailed check basis under the centralized processing system as promulgated in PNAP ADM-19. The duties of the authorized person, registered structural engineer and/or registered geotechnical engineer concerned as specified under section 4(3)(b) and the provision of section 14(2)(c) of the Buildings Ordinance are of particular relevance in this regard.

TOWER 3

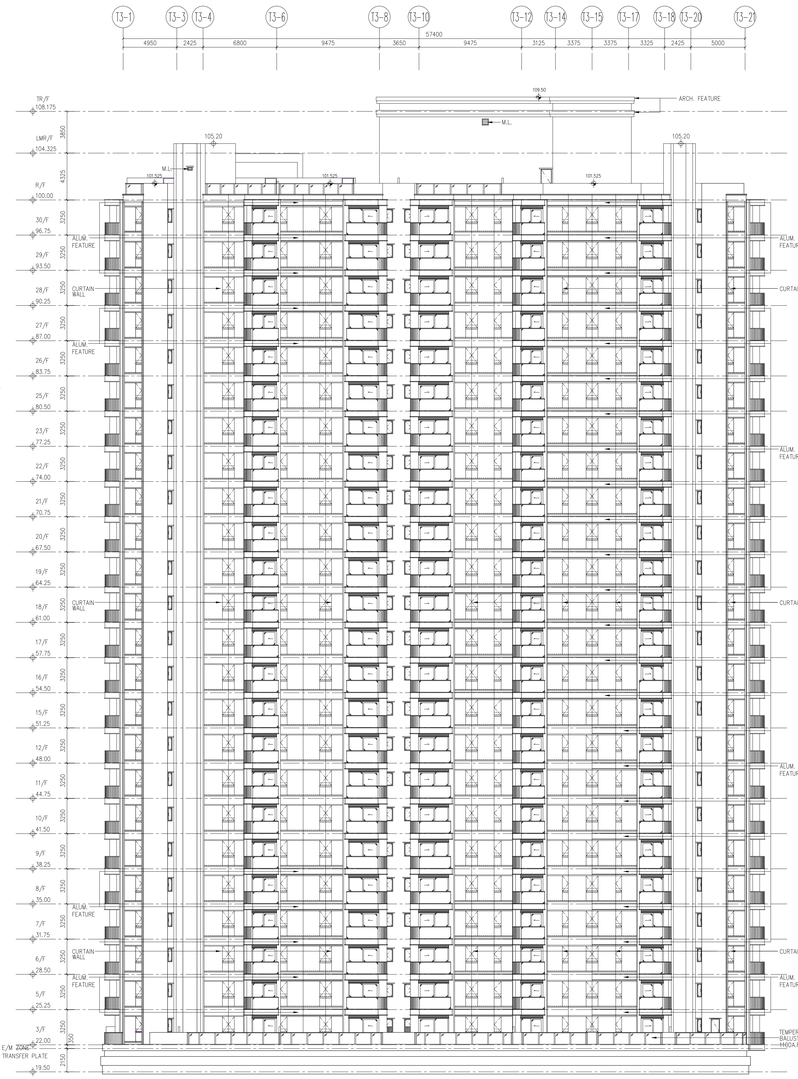


9 ELEVATION

TOWER 3

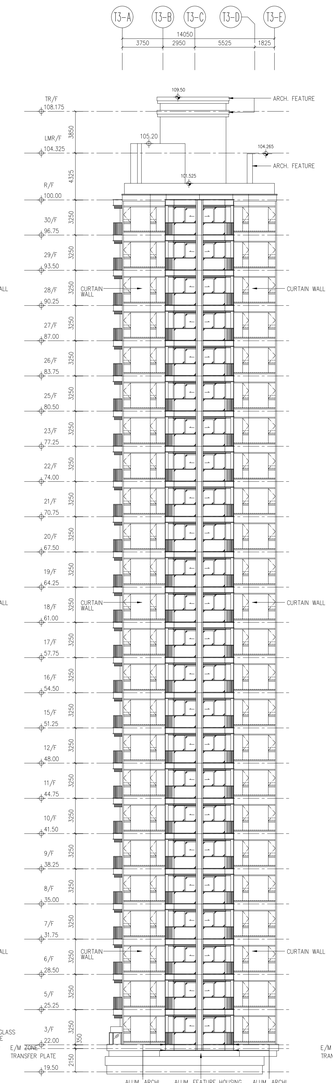


10 ELEVATION

TOWER 3

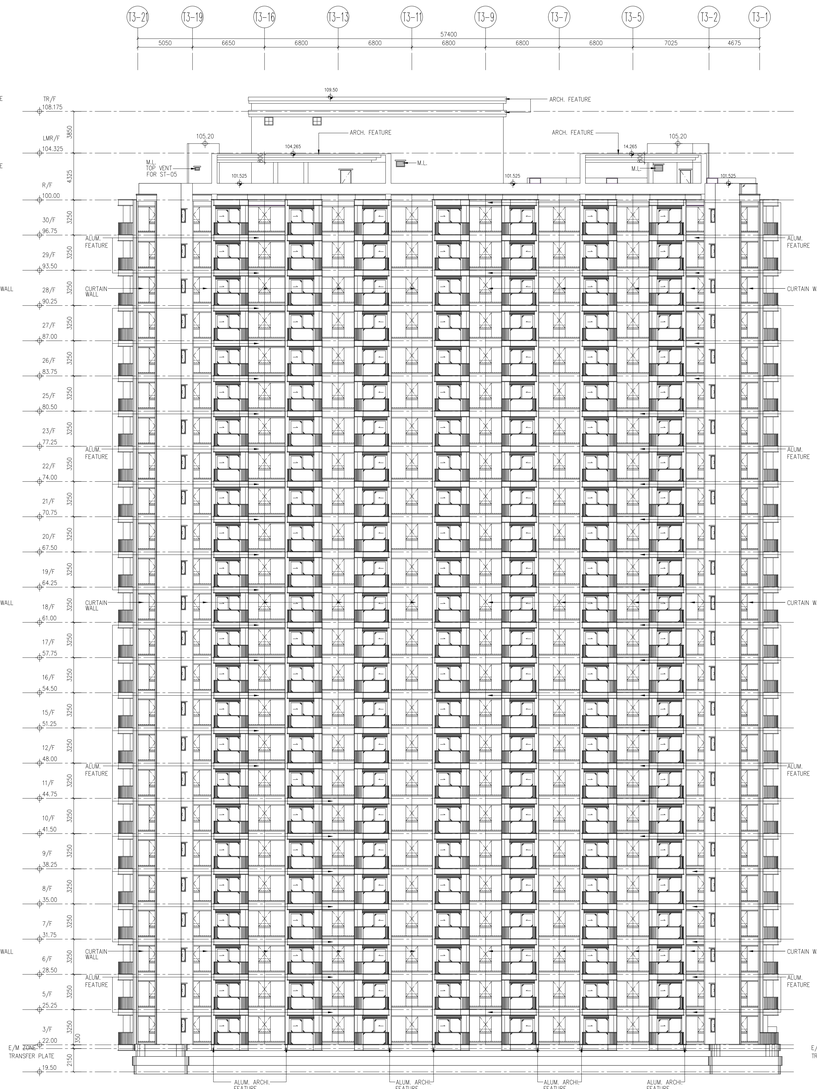


11 ELEVATION

TOWER 3

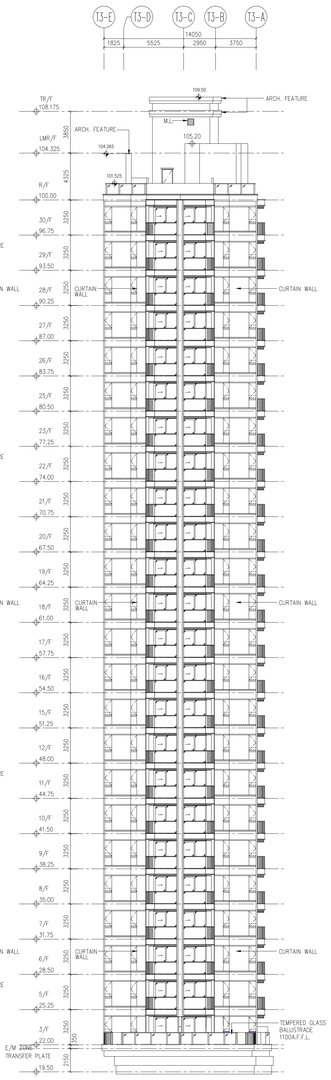

12 ELEVATION

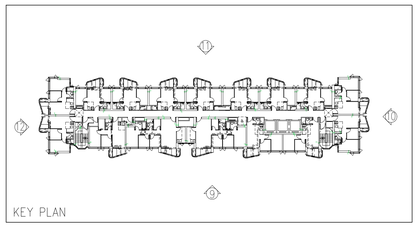

B.D. Ref : 80 2/4024/21

BIM Ref : - -

F.S.D. Ref : - -

D.L.O. Ref : - -

Rev.	Description	Drawn	Checked	Approved	Date
-	1st Submission	WY	AW	AL	07/2022
A	2nd Submission	WY	AW	AL	11/2022
B	1st Amendment	TWM	AW	AL	04/2023
C	2nd Amendment	TWM	AW	AL	12/2023
D	3rd Amendment	TWM	AW	AL	04/2024
D	3rd Amendment (Re-submission)	TWM	AW	AL	05/2024
E	5th Amendment	TWM	AW	AL	12/2024
E	5th Amendment (Re-submission)	TWM	AW	AL	02/2025
F	8th Amendment	LKM	AW	AL	05/2025
G	9th Amendment	LKM	AW	AL	08/2025
G	9th Amendment (Re-submission)	TWM	AW	AL	10/2025
H	10th Amendment	TWM	AW	AL	12/2025
I	11th Amendment	TWM	AW	AL	02/2026
J	12th Amendment	TWM	AW	AL	05/2026

Type II works
The works shown on these plans are Type II works (Building Amendment) in respect of which consent is applied for the purpose of Fast Track consent application under regulation 33 of the Building (Administration) Regulations.

RONALD LU & PARTNERS

呂元祥建築師事務所

Check all dimensions on site. Do not scale off drawing.
Use dimensions only as read or derived from the specification and any discrepancies are to be immediately reported to the Architect.
This drawing remains the copyright property of the Architect and is not to be reproduced in whole or in part without permission of the Architect.

Project Title :
PROPOSED DEVELOPMENT
AT BAILEY STREET
& WING KWONG STREET
TO KWA WAN, KOWLOON

Drawing Title :
ELEVATION 9, 10, 11 & 12
(TOWER 2)

Drawn By	TWM	Date	08/2025
Checked By	AW	Date	08/2025
Approved By	AL	Date	08/2025
Project No.	21163KL	Issue Date	08/2025

File Path :
S:\Bailey, &Wing, Street\2021\21163KL Bailey Street & Wing Kwong Street\DWG\WORKING\BD\02\BP 1P.dwg

Scale 1:200 By CAD

Drawing Number : A/GBP/27

Revision Number : J

Drawing Purpose
Buildings Department
Amended Plan

Digitally signed by LEUNG Ka Man Andy
APVA 80/85
27 May 2026

Received on
27 May 2026

Plan Approved
(Digitally Signed)
TSOI Lap-san, Lapson
Senior Building Surveyor
for BUILDING AUTHORITY
02 June 2026

Note: This plan has been processed on a curtailed check basis under the centralized processing system as promulgated in PNAP ADM-19. The duties of the authorized person, registered structural engineer and/or registered geotechnical engineer concerned as specified under section 4(3)(b) and the provision of section 14(2)(c) of the Buildings Ordinance are of particular relevance in this regard.


B.D. Ref. : 80 2/4024/21

BIM Ref. : - --


F.S.D. Ref. : - --

D.L.O. Ref. : - --

Rev.	Description	Drawn	Checked	Approved	Date
-	1st Submission	WY	AW	AL	07/2022
A	2nd Submission	WY	AW	AL	11/2022
B	1st Amendment	TWM	AW	AL	04/2023
C	2nd Amendment	TWM	AW	AL	12/2023
D	3rd Amendment	TWM	AW	AL	04/2024
D	3rd Amendment (Re-submission)	TWM	AW	AL	05/2024
E	5th Amendment	TWM	AW	AL	12/2024
E	5th Amendment (Re-submission)	TWM	AW	AL	02/2025
F	8th Amendment	LKM	AW	AL	05/2025
G	9th Amendment	LKM	AW	AL	08/2025
G	9th Amendment (Re-submission)	TWM	AW	AL	10/2025
H	10th Amendment	TWM	AW	AL	12/2025
I	11th Amendment	TWM	AW	AL	02/2026
J	12th Amendment	TWM	AW	AL	05/2026
K	13th Amendment	TWM	AW	AL	06/2026

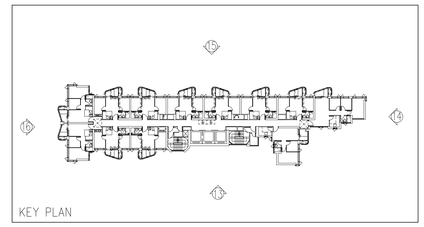


TOWER 5

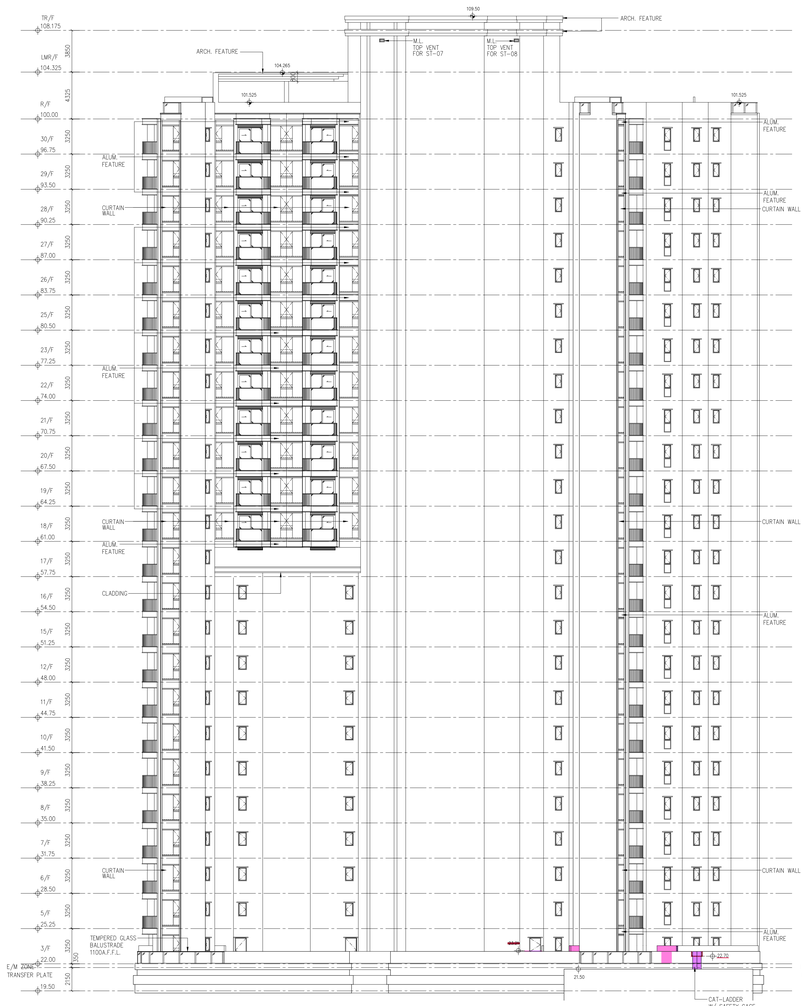


13 ELEVATION

TOWER 5

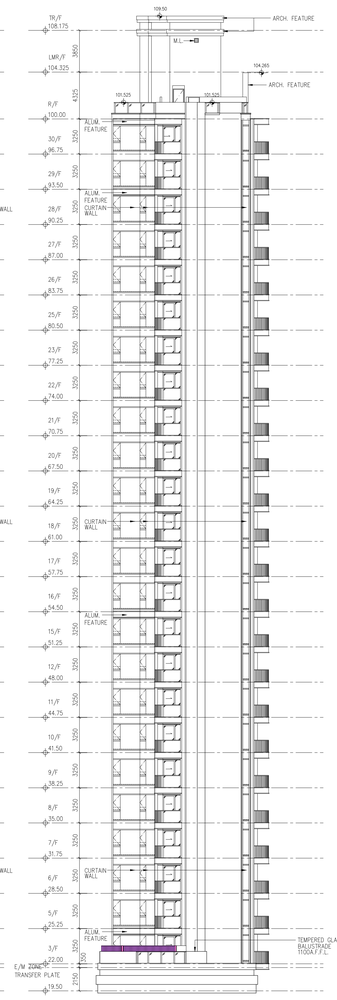


14 ELEVATION

TOWER 5

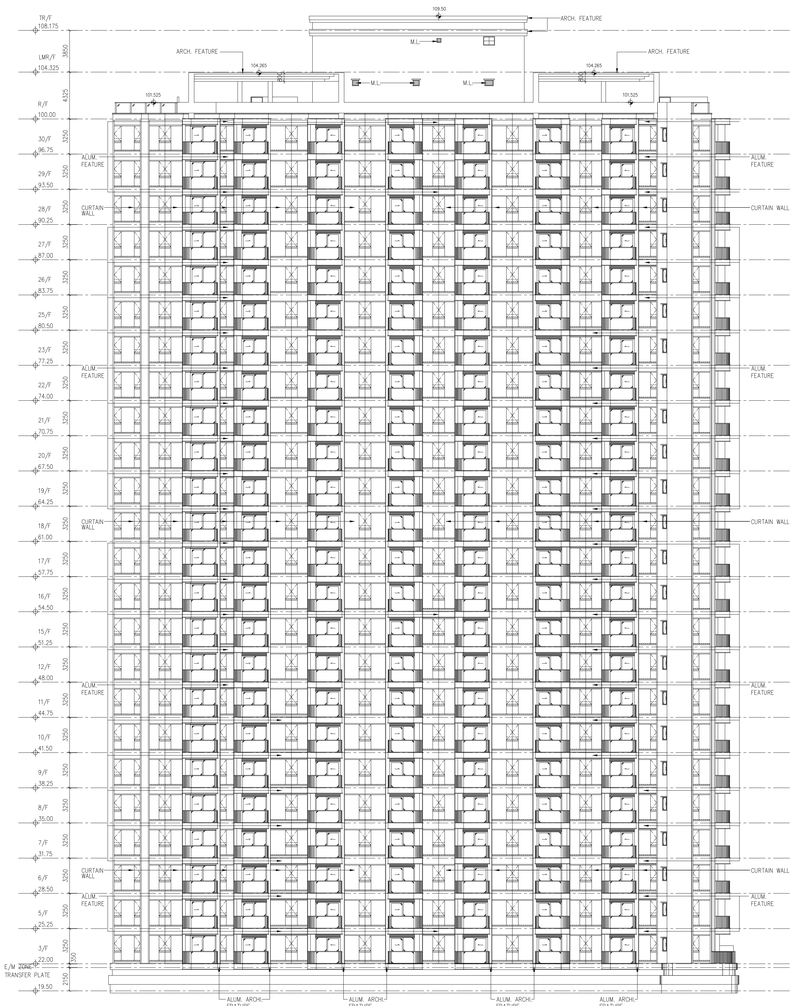

15 ELEVATION

TOWER 5

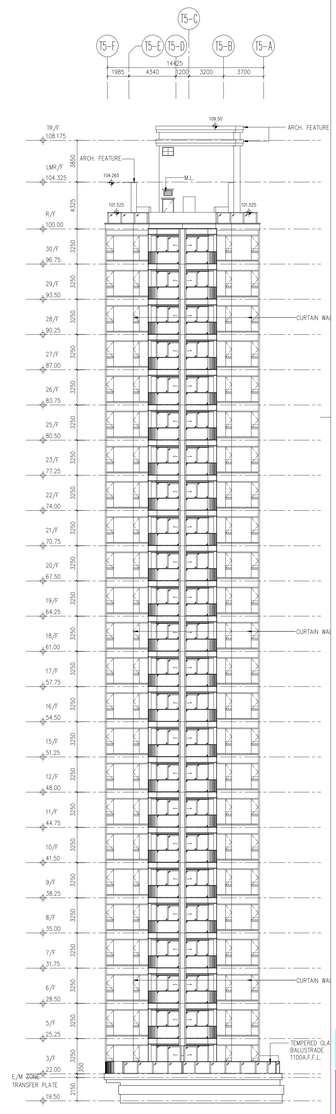

16 ELEVATION

Type II works
The works shown on these plans are Type II works (Building Amendment) in respect of which consent is applied for the purpose of Fast Track consent application under regulation 33 of the Building (Administration) Regulations.

RONALD LU & PARTNERS

呂元祥建築師事務所

Check all measurements on site. Do not scale off drawings.
Any discrepancies are to be read in conjunction with the specification and any discrepancies are to be immediately reported to the Architect.
This drawing remains the copyright property of the Architect and is not to be reproduced in whole or in part without permission of the Architect.

Project Title :
PROPOSED DEVELOPMENT
AT BAILEY STREET
& WING KWONG STREET
TO KWA WAN, KOWLOON

Drawing Title :
ELEVATION 13, 14, 15 & 16
(TOWER 3)

Drawn By	TWM	Date	08/2025
Checked By	AW	Date	08/2025
Approved By	AL	Date	08/2025
Project No.	21163KL	Issue Date	08/2025

File Path :
Scale 1:200 By CAD

Drawing Number : A/GBP/28
Revision Number : K


Drawing Purpose
Buildings Department
Amended Plan

Digitally signed by WONG Chi Kin Kenneth
APAL/ 19/95
08 July 2026


Received on
08 July 2026

Plan Approved
(Digitally Signed)
TSOI Lap-sam, Lapson
Senior Building Surveyor
for BUILDING AUTHORITY
08 July 2026


Note: This plan has been processed on a curtailed check basis under the centralized processing system as promulgated in PNAP ADM-19. The duties of the authorized person, registered structural engineer and/or registered geotechnical engineer concerned as specified under section 4(3)(b) and the provision of section 14(2)(c) of the Buildings Ordinance are of particular relevance in this regard.

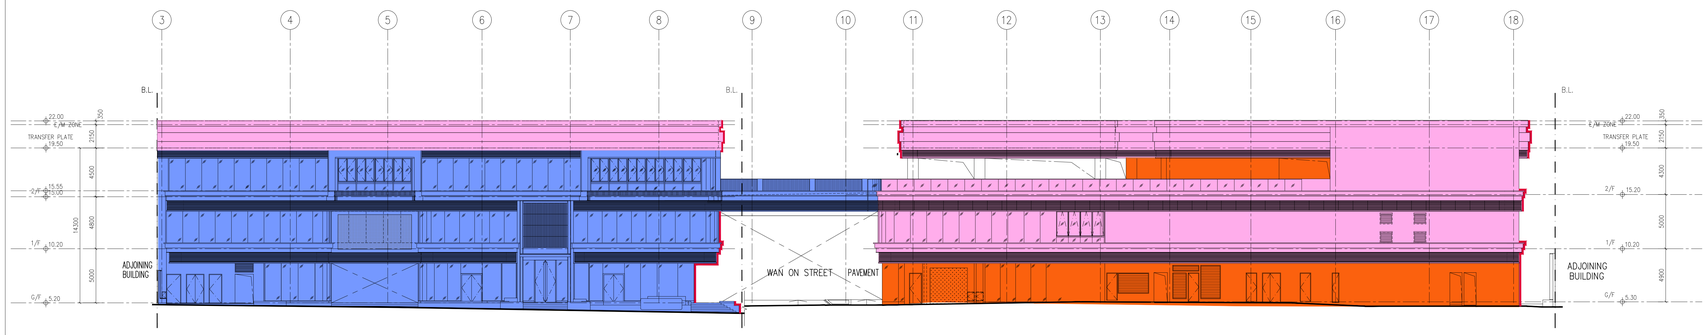

E1 ELEVATION

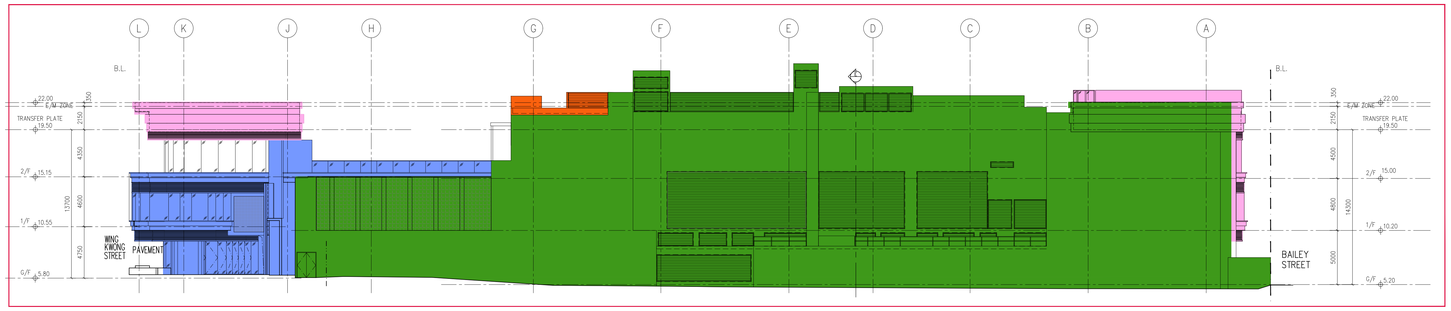


E2 ELEVATION

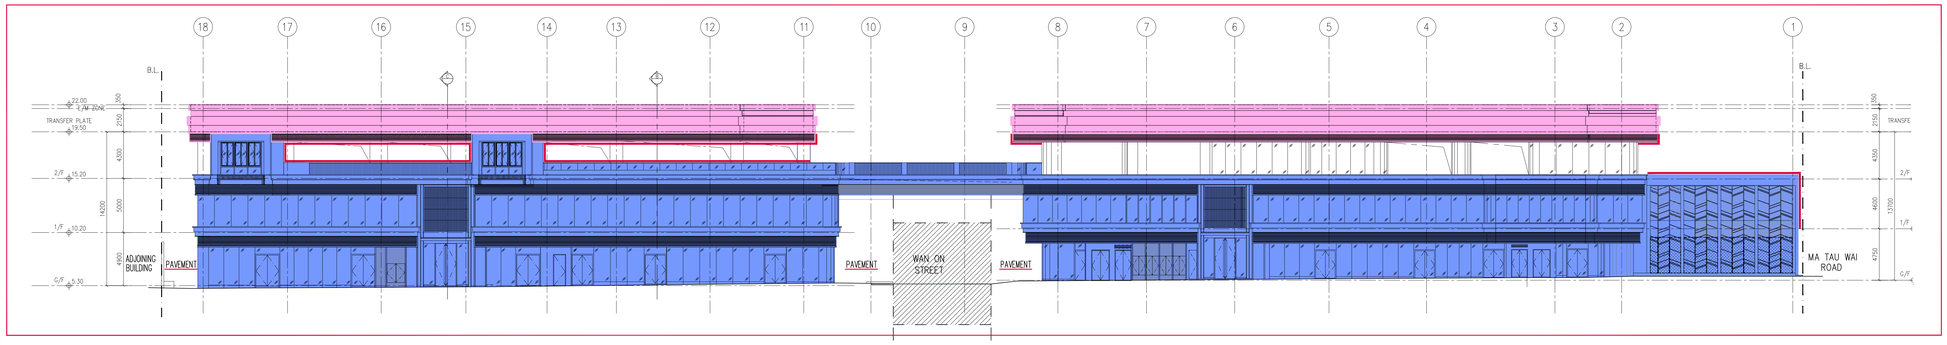

E3 ELEVATION



E4 ELEVATION

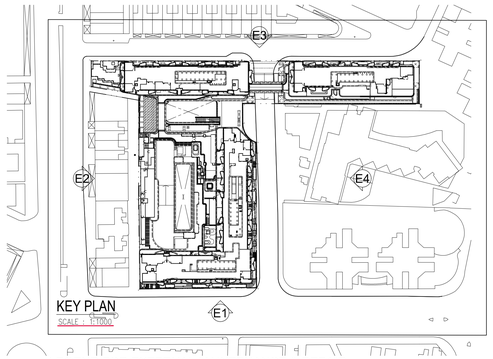

KEY PLAN
SCALE : 1:1000

LEGEND FOR EXTERNAL MAINTENANCE & REPAIR :

- SYSTEM A : SUSPENDED WORKING PLATFORM ON TOP ROOF
- SYSTEM B : POWER-OPERATED ELEVATED WORK PLATFORM ON GROUND FLOOR
- DIRECT ACCESS ON ADJOINING FLOOR BY TEMPORARY SCAFFOLDING
- TEMPORARY SCAFFOLDING

B.D. Ref : BD 2/4024/21

BIM Ref : - --

F.S.D. Ref : - --

D.L.O. Ref : - --

Rev.	Description	Drawn	Checked	Approved	Date
-	1st Submission	TWM	AW	AL	03/2024
A	1st Amendment	TWM	AW	AL	12/2024
A	1st Amendment (Re-submission)	TWM	AW	AL	02/2025
B	11th Amendment	TWM	AW	AL	2/2026

Type II works
The works shown on these plans are Type II works (Building Amendment) in respect of which consent is applied for the purpose of Fast Track consent application under regulation 33 of the Building (Administration) Regulations.

RONALD LU & PARTNERS

呂元祥建築師事務所

Check all measurements on site. Do not scale off drawings.
Any discrepancies between drawings and site conditions and any discrepancies are to be immediately reported to the Architect.
This drawing remains the copyright property of the Architect and is not to be reproduced in whole or in part without permission of the Architect.

Project Title :
PROPOSED DEVELOPMENT AT BAILEY STREET & WING KWONG STREET TO KWA WAN, KOWLOON

Drawing Title :
PODIUM ELEVATION (1) (ACCESS FOR EXTERNAL MAINTENANCE)

Drawn By	TWM	Date	05/2025
Checked By	AW	Date	05/2025
Approved By	AL	Date	05/2025
Project No.	21163KL	Issue Date	05/2025

File Path :
I:\Job 3Ps\ 2a\21\2100_Bailey Street & Wing Kwong Street\WORKING\EXE\EXP_1\Tsoi's\revised_ tsoi's revised\R27_BEP4.4(E-1).dwg

Scale 1:200 By CAD

Drawing Number : A/AEM/11

Revision Number : B

Drawing Purpose
Buildings Department
Amended Plan

Digitally signed by LEUNG Kit Man Andy
APUN 86085
16 March 2026


Received on
16 March 2026

Plan Approved
(Digitally Signed)
TSOI Lap-san, Lapson
Senior Building Surveyor
for BUILDING AUTHORITY
17 March 2026

Note: This plan has been processed on a curtailed check basis under the centralized processing system as promulgated in PNAP ADM-19. The duties of the authorized person, registered structural engineer and/or registered geotechnical engineer concerned as specified under section 4(3)(b) and the provision of section 14(2)(c) of the Buildings Ordinance are of particular relevance in this regard.


LEGEND FOR EXTERNAL MAINTENANCE & REPAIR :

- SYSTEM A : SUSPENDED WORKING PLATFORM ON TOP ROOF
- SYSTEM B : POWER-OPERATED ELEVATED WORK PLATFORM ON GROUND FLOOR
- DIRECT ACCESS ON ADJOINING FLOOR BY TEMPORARY SCAFFOLDING
- VISUAL INSPECTION BY GONDOLA MAINTENANCE & REPAIR BY TEMPORARY SCAFFOLDING
- TEMPORARY SCAFFOLDING
- RESTRAINT SOCKET FOR SUSPENDED WORKING PLATFORM (STRUCTURAL DETAIL UNDER SEPARATE SUBMISSION)

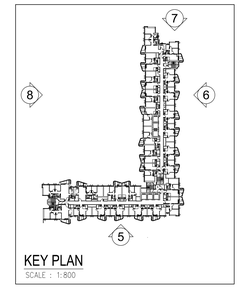


KEY PLAN
SCALE : 1:800

TOWER 1

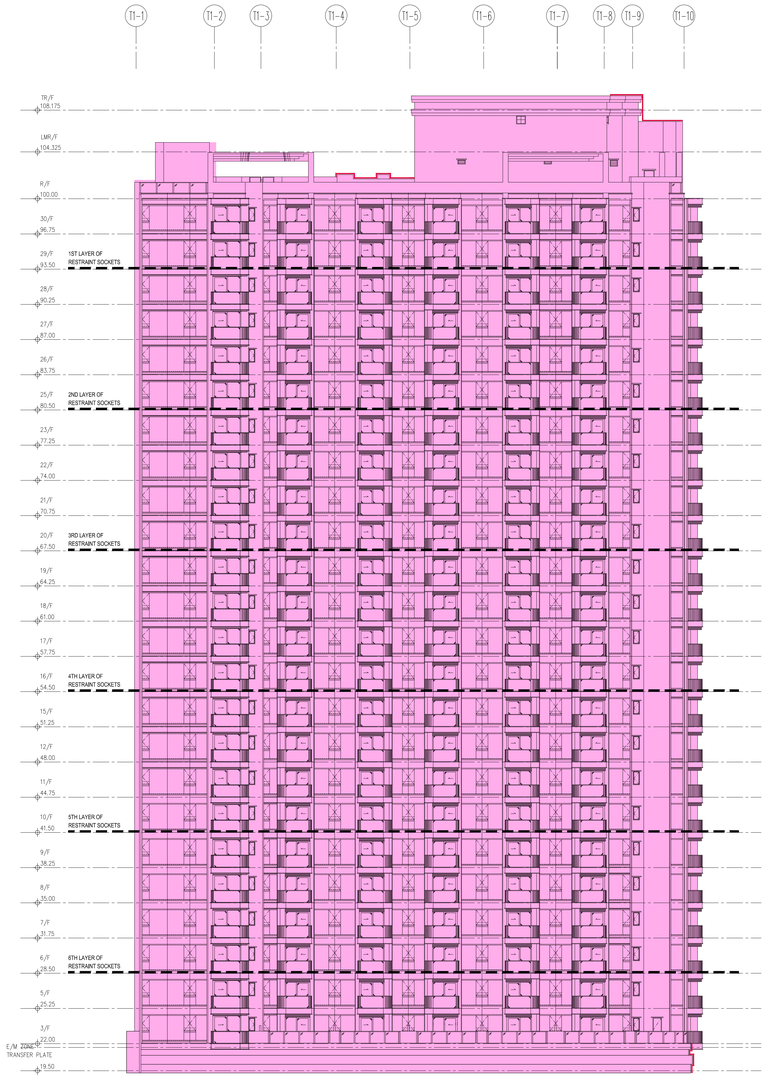

5 ELEVATION

TOWER 1 & TOWER 2

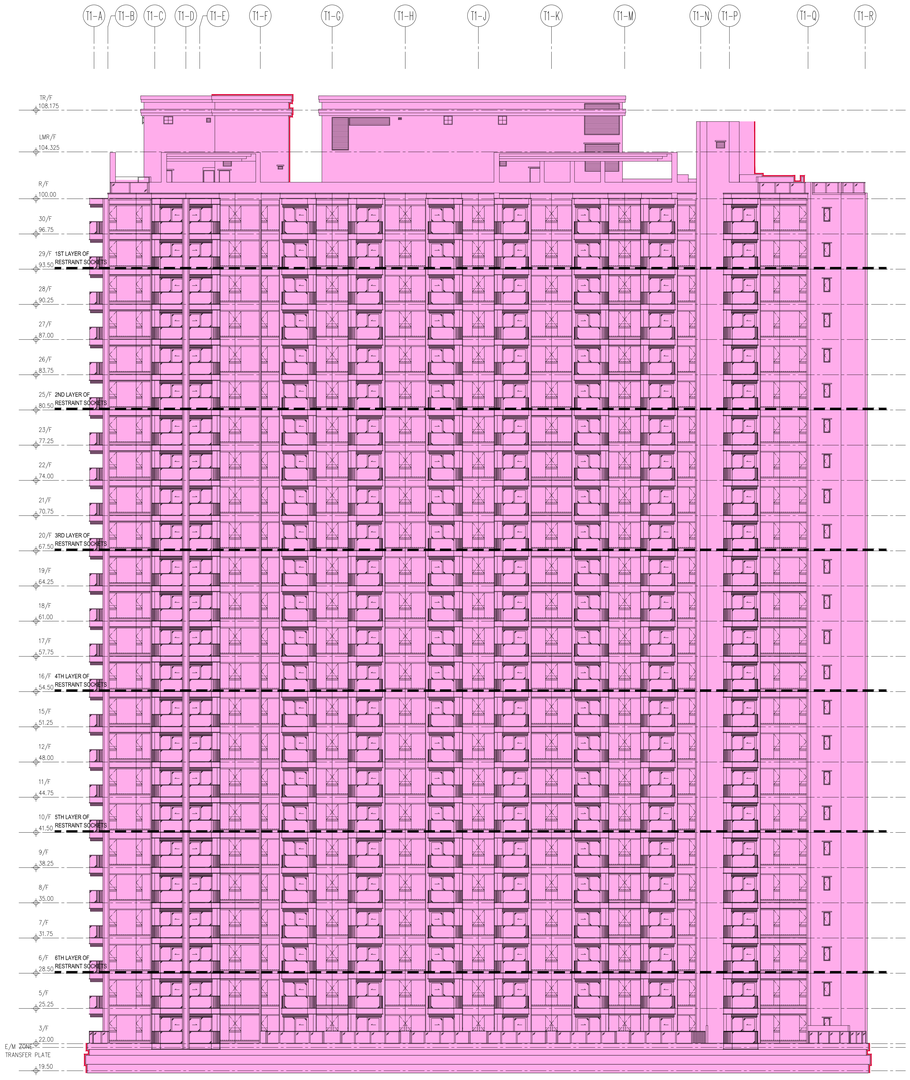

6 ELEVATION

B.D. Ref : BD 2/4024/21

BIM Ref : - ---

F.S.D. Ref : - ---

D.L.O. Ref : - ---

Rev.	Description	Drawn	Checked	Approved	Date
-	1st Submission	TWM	AW	AL	03/2024
A	1st Amendment	TWM	AW	AL	12/2024
A	1st Amendment (Re-submission)	TWM	AW	AL	02/2025
B	11th Amendment	TWM	AW	AL	2/2026

Type II works
The works shown on these plans are Type II works (Building Amendment) in respect of which consent is applied for the purpose of Fast Track consent application under regulation 33 of the Building (Administration) Regulations.

RONALD LU & PARTNERS

呂元祥建築師事務所

Check all measurements on site. Do not scale off drawings.
This drawing is to be read in conjunction with the specification and any discrepancies are to be immediately reported to the Architect.
This drawing remains the copyright property of the Architect and is not to be reproduced in part or whole without permission of the Architect.

Project Title :
PROPOSED DEVELOPMENT AT BAILEY STREET & WING KWONG STREET TO KWA WAN, KOWLOON

Drawing Title :
TOWER 1 & TOWER 2 - ELEVATION (1) (ACCESS FOR EXTERNAL MAINTENANCE)

Drawn By	TWM	Date	05/2025
Checked By	AW	Date	05/2025
Approved By	AL	Date	05/2025
Project No.	21163KL	Issue Date	05/2025

File Path : T:\Job 21_Jobs\21163_Bailey Street\Working Drawings\BIM\RVT\21163BDP 1-7-Submitted\ 2nd Amend\BLD 1&2 - ELEVATION (1) (ACCESS FOR EXTERNAL MAINTENANCE) 2nd Amend.rvt

Scale 1:200 By CAD

Drawing Number : A/AEM/12

Revision Number : B

Drawing Purpose

Buildings Department
Amended Plan

Digitally signed by LEUNG Ka Man, Andy
on behalf of APUN 80093
16 March 2026


Received on
16 March 2026

Plan Approved
(Digitally Signed)
TSOI Lap-san, Lapson
Senior Building Surveyor
for BUILDING AUTHORITY
17 March 2026

Note: This plan has been processed on a curtailed check basis under the centralized processing system as promulgated in PNAP ADM-19. The duties of the authorized person, registered structural engineer and/or registered geotechnical engineer concerned as specified under section 4(3)(b) and the provision of section 14(2)(c) of the Buildings Ordinance are of particular relevance in this regard.


LEGEND FOR EXTERNAL MAINTENANCE & REPAIR :

- SYSTEM A : SUSPENDED WORKING PLATFORM ON TOP ROOF
- SYSTEM B : POWER-OPERATED ELEVATED WORK PLATFORM ON GROUND FLOOR
- DIRECT ACCESS ON ADJOINING FLOOR BY TEMPORARY SCAFFOLDING
- VISUAL INSPECTION BY GONDOLA MAINTENANCE & REPAIR BY TEMPORARY SCAFFOLDING
- TEMPORARY SCAFFOLDING
- RESTRAINT SOCKET FOR SUSPENDED WORKING PLATFORM (STRUCTURAL DETAIL UNDER SEPARATE SUBMISSION)

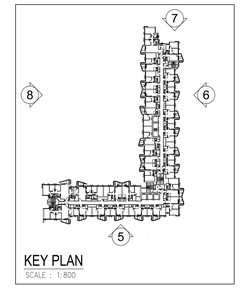

KEY PLAN
SCALE : 1:800

TOWER 1 & TOWER 2

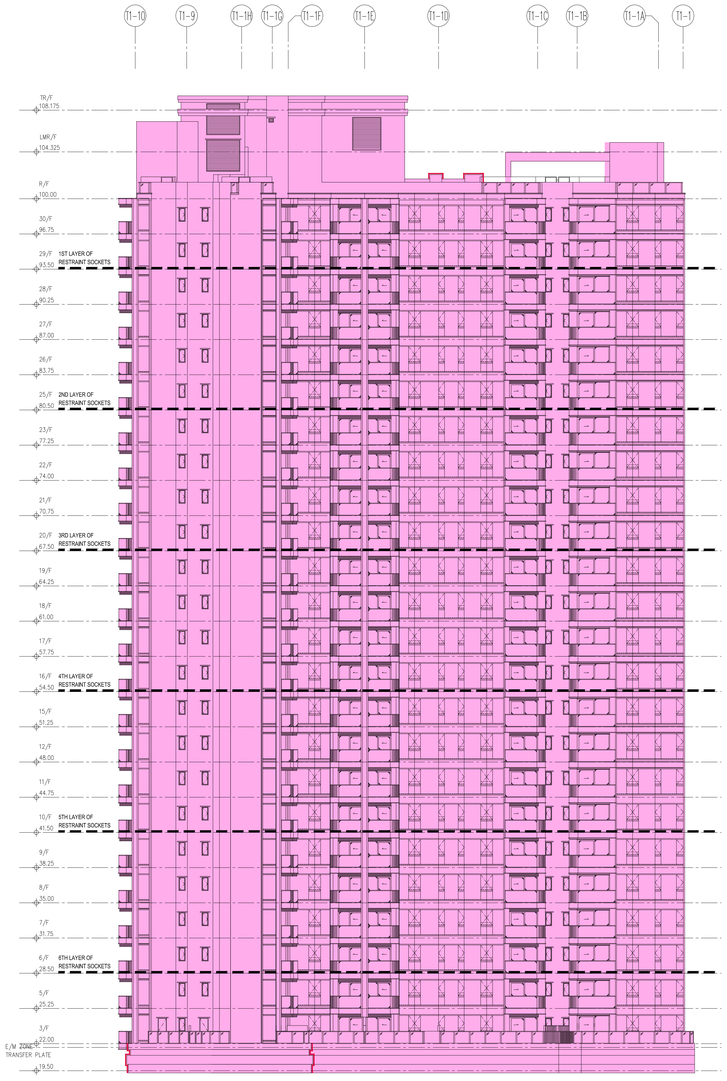

7 ELEVATION

TOWER 1 & TOWER 2



8 ELEVATION

B.D. Ref :	BD 2/4024/21
BIM Ref :	- ---
F.S.D. Ref :	- ---
D.L.O. Ref :	- ---

Rev.	Description	Drawn	Checked	Approved	Date
-	1st Submission	TWM	AW	AL	03/2024
A	1st Amendment	TWM	AW	AL	12/2024
A	1st Amendment (Re-submission)	TWM	AW	AL	02/2025
B	11th Amendment	TWM	AW	AL	2/2026

Type II works
The works shown on these plans are Type II works (Building Amendment) in respect of which consent is applied for the purpose of Fast Track consent application under regulation 33 of the Building (Administration) Regulations.

RONALD LU & PARTNERS

呂元祥建築師事務所

Check all measurements on site. Do not scale off drawings.
This drawing is to be read in conjunction with the specification and any discrepancies are to be immediately reported to the Architect.
This drawing is copyright of Ronald Lu & Partners and the like and is not to be reproduced in whole or in part without permission of the Architect.

Project Title :
PROPOSED DEVELOPMENT
AT BAILEY STREET
& WING KWONG STREET
TO KWA WAN, KOWLOON

Drawing Title :
TOWER 1 & TOWER 2 - ELEVATION (2)
(ACCESS FOR EXTERNAL MAINTENANCE)

Drawn By	TWM	Date	05/2025
Checked By	AW	Date	05/2025
Approved By	AL	Date	05/2025
Project No.	21163KL	Issue Date	05/2025

File Path :
J:\Job (Pj's_Jobs)\21\21163_Sale Dept & Wp\Apply Dev\DWG\03.BD\DP - 5 Fast-track_1st Amend\R2\7_8BW_ELEVATION.dwg

Scale 1:200 By CAD

Drawing Number : A/AEM/13
Revision Number : B

Drawing Purpose
Buildings Department
Amended Plan

Digitally signed by LEUNG Kit Man Andy
APPLI.BUWS
16 March 2026


Received on
16 March 2026

Plan Approved
(Digitally Signed)
TSOI Lap-san, Lapson
Senior Building Surveyor
for BUILDING AUTHORITY
17 March 2026

Note: This plan has been processed on a curtailed check basis under the centralized processing system as promulgated in PNAP ADM-15. The duties of the authorized person, registered structural engineer and/or registered geotechnical engineer concerned as specified under section 4(3)(b) and the provision of section 14(2)(c) of the Buildings Ordinance are of particular relevance in this regard.

LEGEND FOR EXTERNAL MAINTENANCE & REPAIR :


- SYSTEM A : SUSPENDED WORKING PLATFORM ON TOP ROOF
- SYSTEM B : POWER-OPERATED ELEVATED WORK PLATFORM ON GROUND FLOOR
- DIRECT ACCESS ON ADJOINING FLOOR BY TEMPORARY SCAFFOLDING
- VISUAL INSPECTION BY GONDOLA MAINTENANCE & REPAIR BY TEMPORARY SCAFFOLDING
- TEMPORARY SCAFFOLDING
- RESTRAINT SOCKET FOR SUSPENDED WORKING PLATFORM (STRUCTURAL DETAIL UNDER SEPARATE SUBMISSION)

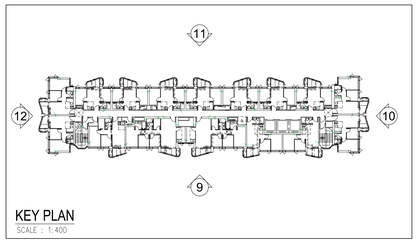

KEY PLAN


SCALE : 1:400

TOWER 3

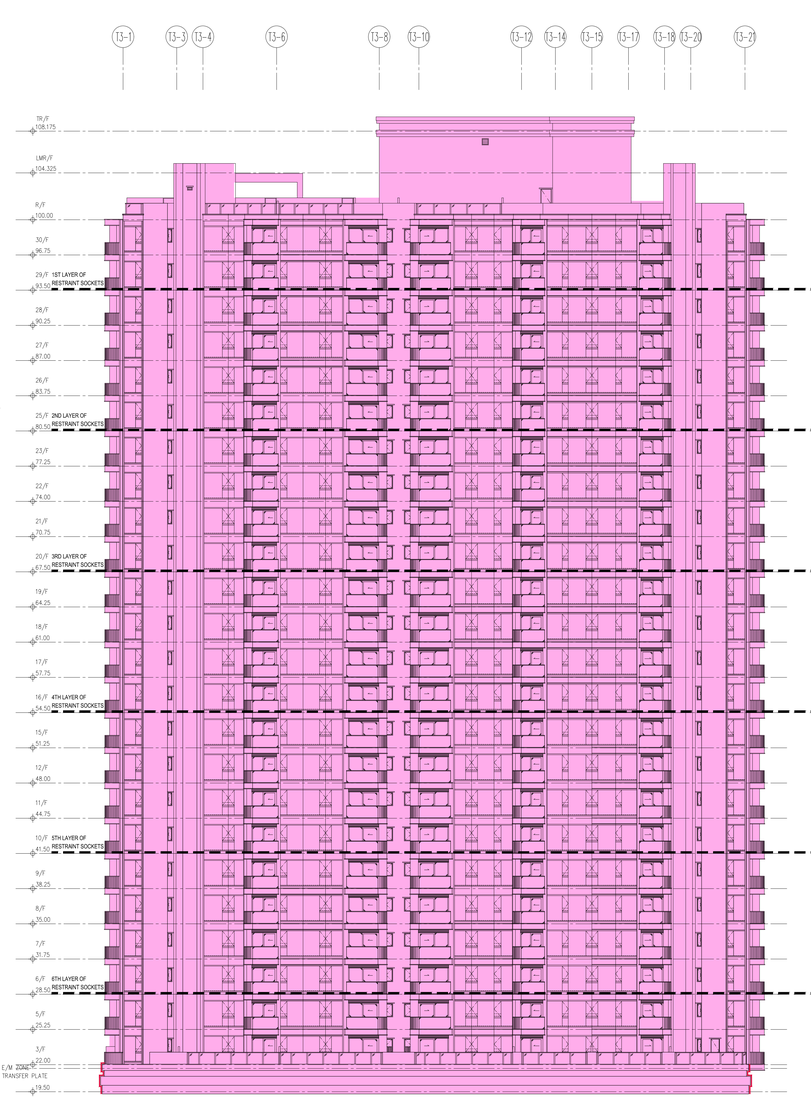


9 ELEVATION

TOWER 3

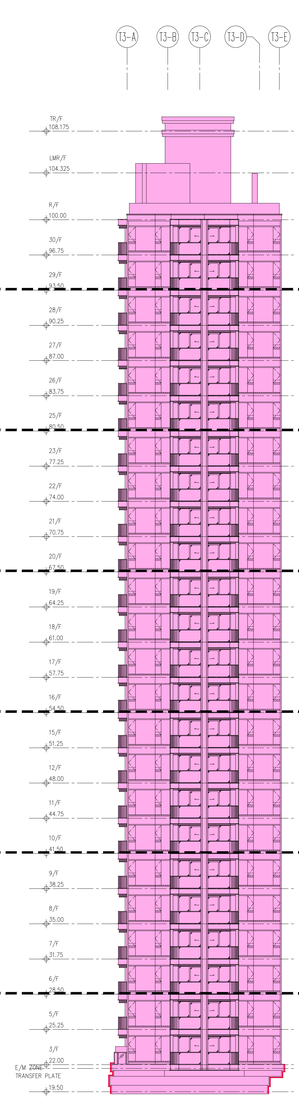


10 ELEVATION

TOWER 3

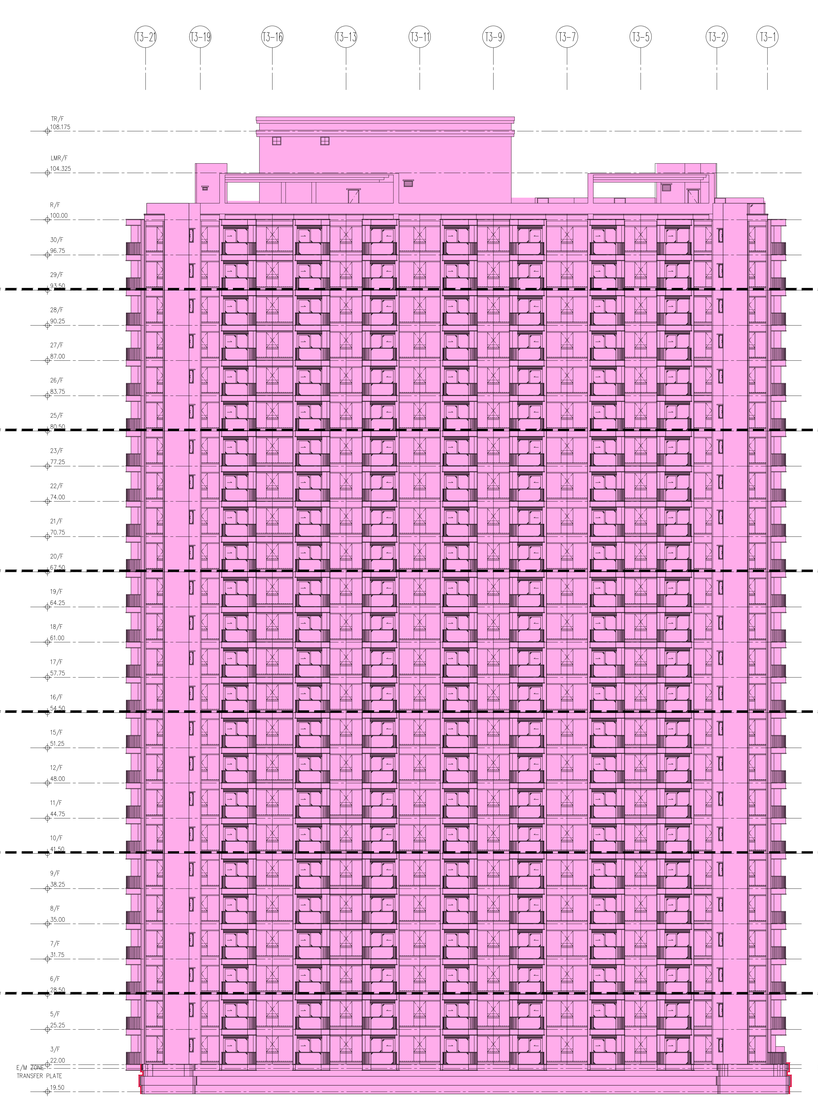

11 ELEVATION

TOWER 3

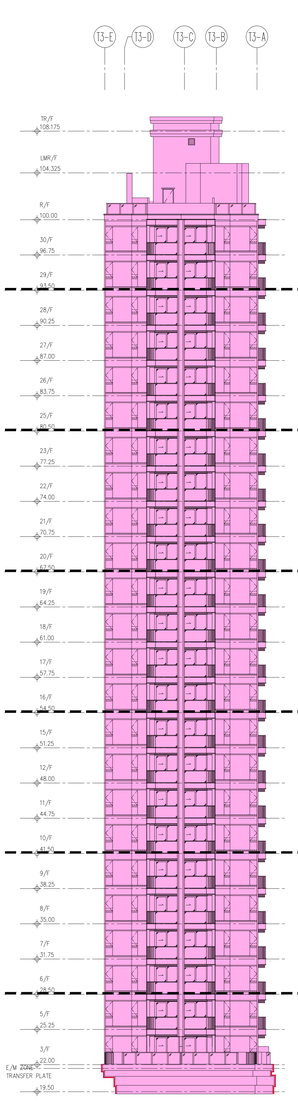

12 ELEVATION

B.D. Ref : BD 2/4024/21

BIM Ref : - ---

F.S.D. Ref : - ---

D.L.O. Ref : - ---

Rev.	Description	Drawn	Checked	Approved	Date
---	1st Submission	TWM	AW	AL	03/2024
A	1st Amendment	TWM	AW	AL	12/2024
A	1st Amendment (Re-submission)	TWM	AW	AL	02/2025
B	11th Amendment	TWM	AW	AL	2/2026

Type II works

The works shown on these plans are Type II works (Building Amendment) in respect of which consent is applied for the purpose of Fast Track consent application under regulation 33 of the Building (Administration) Regulations.

RONALD LU & PARTNERS

呂元祥建築師事務所

Check all measurements on site. Do not scale off drawings.
This drawing is to be read in conjunction with the specification and any discrepancies are to be immediately reported to the Architect.
This drawing is copyright and may not be reproduced, lent or hired out or not to be reproduced in whole or in part without permission of the Architect.

Project Title :

PROPOSED DEVELOPMENT AT BAILEY STREET & WING KWONG STREET TO KWA WAN, KOWLOON

Drawing Title :

TOWER 3 - ELEVATION (ACCESS FOR EXTERNAL MAINTENANCE)

Drawn By	TWM	Date	05/2025
Checked By	AW	Date	05/2025
Approved By	AL	Date	05/2025
Project No.	21163KL	Issue Date	05/2025

File Path :

C:\Bob.Ph's Job\21X\01KL Sale Site\1 Working Files\DWG\ELEVATION\T3 Elevations\T3_ELEVATION_ACCESS FOR EXTERNAL MAINTENANCE_B.dwg

Scale 1:200 By CAD

Drawing Number : A/AEM/14

Revision Number : B

Drawing Purpose

Buildings Department
Amended Plan

Digitally signed by LEUNG Kit Man Andy
APPLIMARE
16 March 2026

Received on 16 March 2026


Plan Approved

(Digitally Signed)
TSOI Lap-san, Lapson
Senior Building Surveyor
for BUILDING AUTHORITY
17 March 2026

Note: This plan has been processed on a curtailed check basis under the centralized processing system as promulgated in PNAP ADM-19. The duties of the authorized person, registered structural engineer and/or registered geotechnical engineer concerned as specified under section 4(3)(b) and the provision of section 14(2)(c) of the Buildings Ordinance are of particular relevance in this regard.

LEGEND FOR EXTERNAL MAINTENANCE & REPAIR :


- SYSTEM A : SUSPENDED WORKING PLATFORM ON TOP ROOF
- SYSTEM B : POWER-OPERATED ELEVATED WORK PLATFORM ON GROUND FLOOR
- DIRECT ACCESS ON ADJOINING FLOOR BY TEMPORARY SCAFFOLDING
- VISUAL INSPECTION BY GONDOLA MAINTENANCE & REPAIR BY TEMPORARY SCAFFOLDING
- TEMPORARY SCAFFOLDING
- RESTRAINT SOCKET FOR SUSPENDED WORKING PLATFORM (STRUCTURAL DETAIL UNDER SEPARATE SUBMISSION)
- FALL ARREST ANCHOR

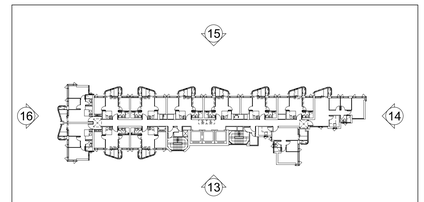

KEY PLAN


SCALE : 1:400

TOWER 5

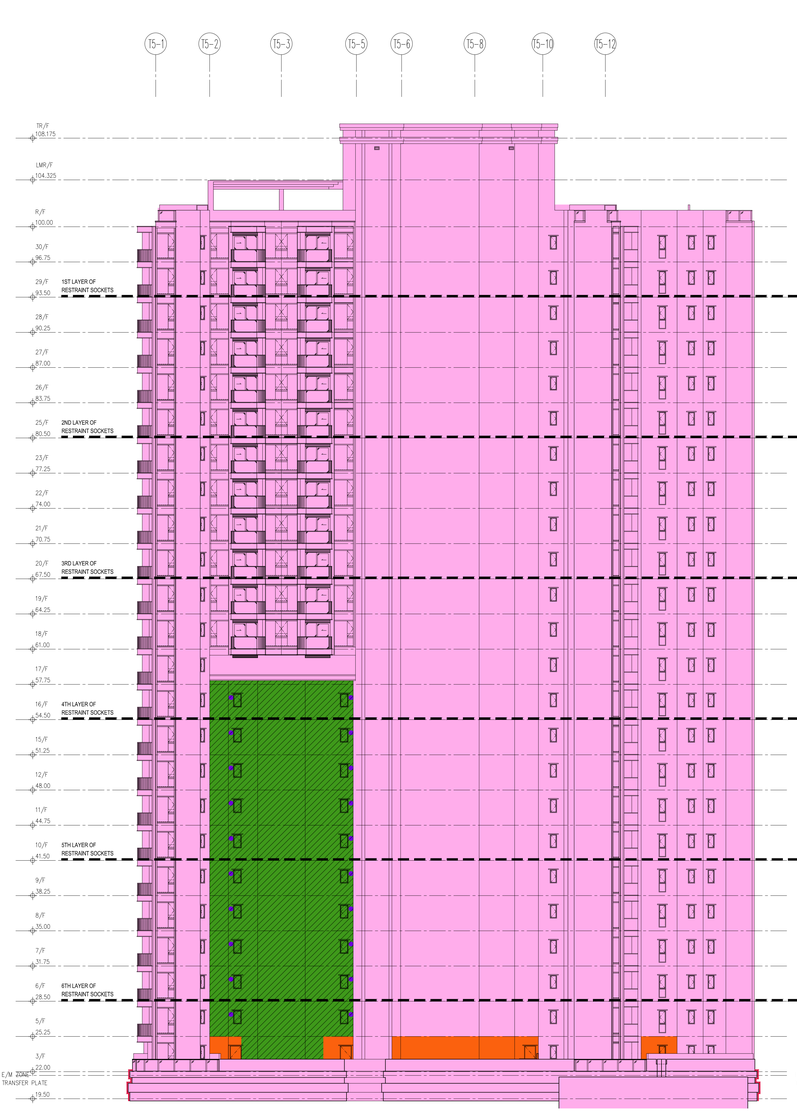


13 ELEVATION

TOWER 5

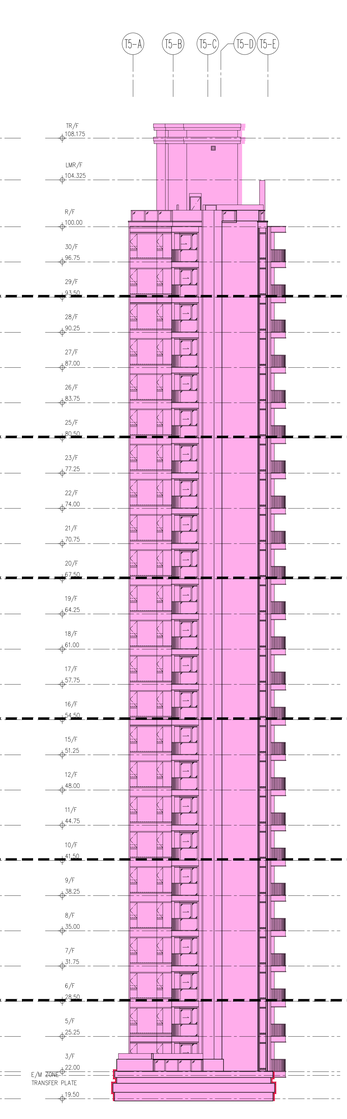


14 ELEVATION

TOWER 5

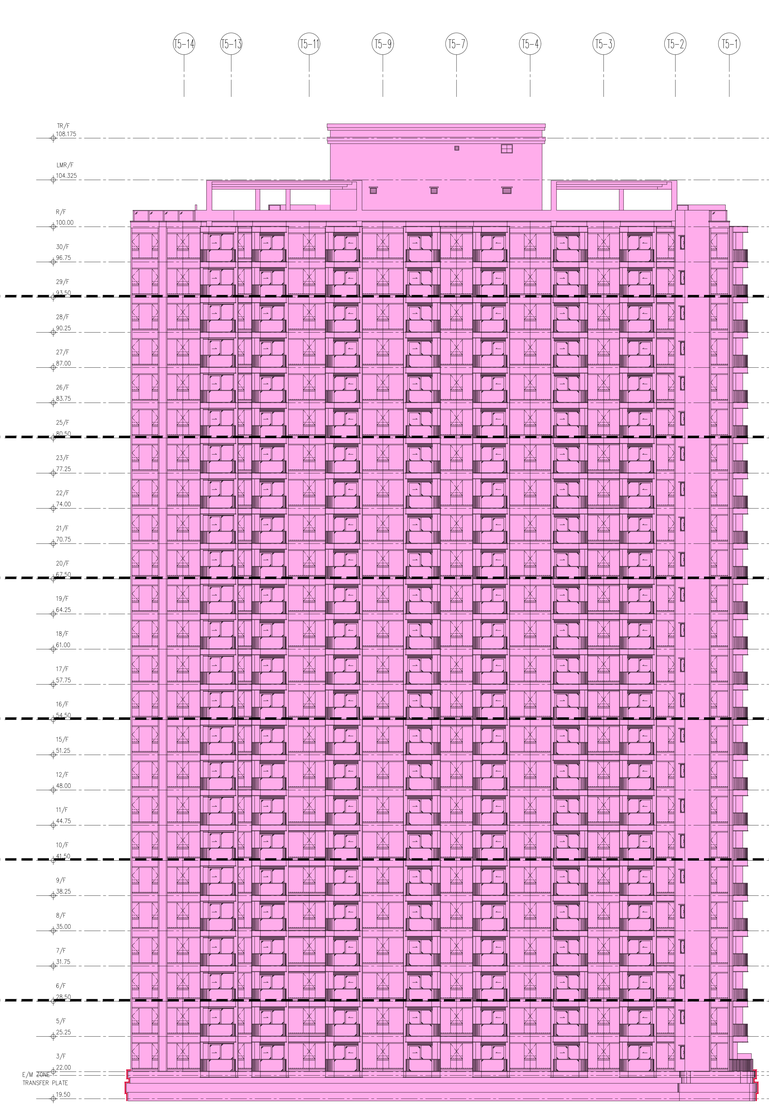

15 ELEVATION

TOWER 5

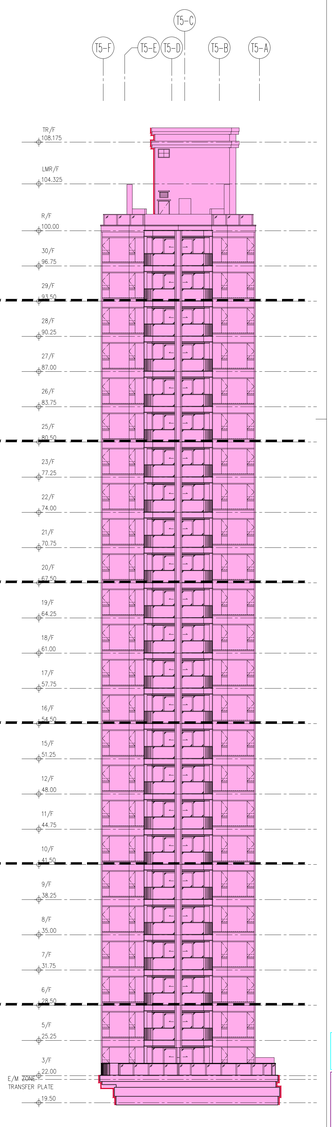

16 ELEVATION

B.D. Ref : BD 2/4024/21

BIM Ref : - ---

F.S.D. Ref : - ---

D.L.O. Ref : - ---

Rev.	Description	Drawn	Checked	Approved	Date
--	1st Submission	TWM	AW	AL	03/2024
A	1st Amendment	TWM	AW	AL	12/2024
A	1st Amendment (Re-submission)	TWM	AW	AL	02/2025
B	11th Amendment	TWM	AW	AL	2/2026

Type II works

The works shown on these plans are Type II works (Building Amendment) in respect of which consent is applied for the purpose of Fast Track consent application under regulation 33 of the Building (Administration) Regulations.

RONALD LU & PARTNERS

呂元祥建築師事務所

Check all measurements on site. Do not scale off drawings.
This drawing is to be read in conjunction with the specification and any discrepancies are to be immediately reported to the Architect.
The copyright of this drawing is vested in the Architect and is not to be reproduced in whole or in part without permission of the Architect.

Project Title :
PROPOSED DEVELOPMENT AT BAILEY STREET & WING KWONG STREET TO KWA WAN, KOWLOON

Drawing Title :
TOWER 5 - ELEVATION (ACCESS FOR EXTERNAL MAINTENANCE)

Drawn By	TWM	Date	05/2025
Checked By	AW	Date	05/2025
Approved By	AL	Date	05/2025
Project No.	21163KL	Issue Date	05/2025

File Path :
I:\Bob (Pc_Jobs)\21163L Sale Dwg\Working Dwg\DWG\BD\EXP_1\Tuning\ext_maint\ext(B)21_BBN 4D1.1.Dwg

Scale 1:200 By CAD

Drawing Number : A/AEM/15

Revision Number : B

Drawing Purpose

Buildings Department
Amended Plan

Digitally signed by LEUNG Ka Man Andy
APVA (BIM)
16 March 2026

Received on
16 March 2026

Plan Approved
(Digitally Signed)
TSOI Lap-san, Lapson
Senior Building Surveyor
for BUILDING AUTHORITY
17 March 2026

Note: This plan has been processed on a curtailed check basis under the centralized processing system as promulgated in PNAP ADM-19. The duties of the authorized person, registered structural engineer and/or registered geotechnical engineer concerned as specified under section 4(3)(b) and the provision of section 14(2)(c) of the Buildings Ordinance are of particular relevance in this regard.