SMOKE VENT CALCULATION (NOT FOR FSD APPROVAL) :

(COMPARTMENT (B3–1) + (B2–1))
AREA REFER DWG. NO. A/GBP/35)

NO.	SIZE	TOTAL
VB3–1	1.000 X 2.180 = 2.180 s.m.	17.788 s.m.
VB3–2	1.000 X 1.455 = 1.455 s.m.	
VB3–3	1.100 X 1.600 = 1.760 s.m.	
VB3–4	5.300 X 1.025 = 5.433 s.m.	
VB3–5	1.200 X 2.250 = 2.700 s.m.	
VB3–6	2.130 X 1.000 = 2.130 s.m.	
VB3–7	2.130 X 1.000 = 2.130 s.m.	

SMOKE VENT AREA CALCULATION :

COMPARTMENT FLOOR AREA = 3533.489 m²
SMOKE OUTLET AREA REQ. = 3533.489 x 0.5% = 17.667 m²
SMOKE OUTLET AREA PROV. = 17.788 m² > 17.667 m²

NOTES:

ALL SMOKE VENT ENCLOSURE TO BE –/240/240 FRR

CAR PARK SPACE (2.5mx5.0mx2.4m HEADROOM)		PROVIDE			
				M–EV	EV
RESIDENTIAL	R01 – R102	102	122 Nos.	31#	71
VISITOR	V01 – V20*	20##		6#	14
MOTOR CYCLE PARKING SPACE (1.0mx2.4mx2.4m HEADROOM)					
RESIDENTIAL	RM01 – RM13	13 Nos.			

# (NOT LESS THAN 30% OF THE PARKING SPACES PROVIDED)
## (CARPARK NO. V18, V19 & V20 PROVIDED AT BASEMENT 2 CARPARK)
* V01 – V20 SHALL BE DESIGNATED AS "COMMON AREA" IN DEED OF MUTUAL COVENANT "DMC" OR SUB–DEED OF MUTUAL COVENANT "SUB–DMC" (IF ANY)

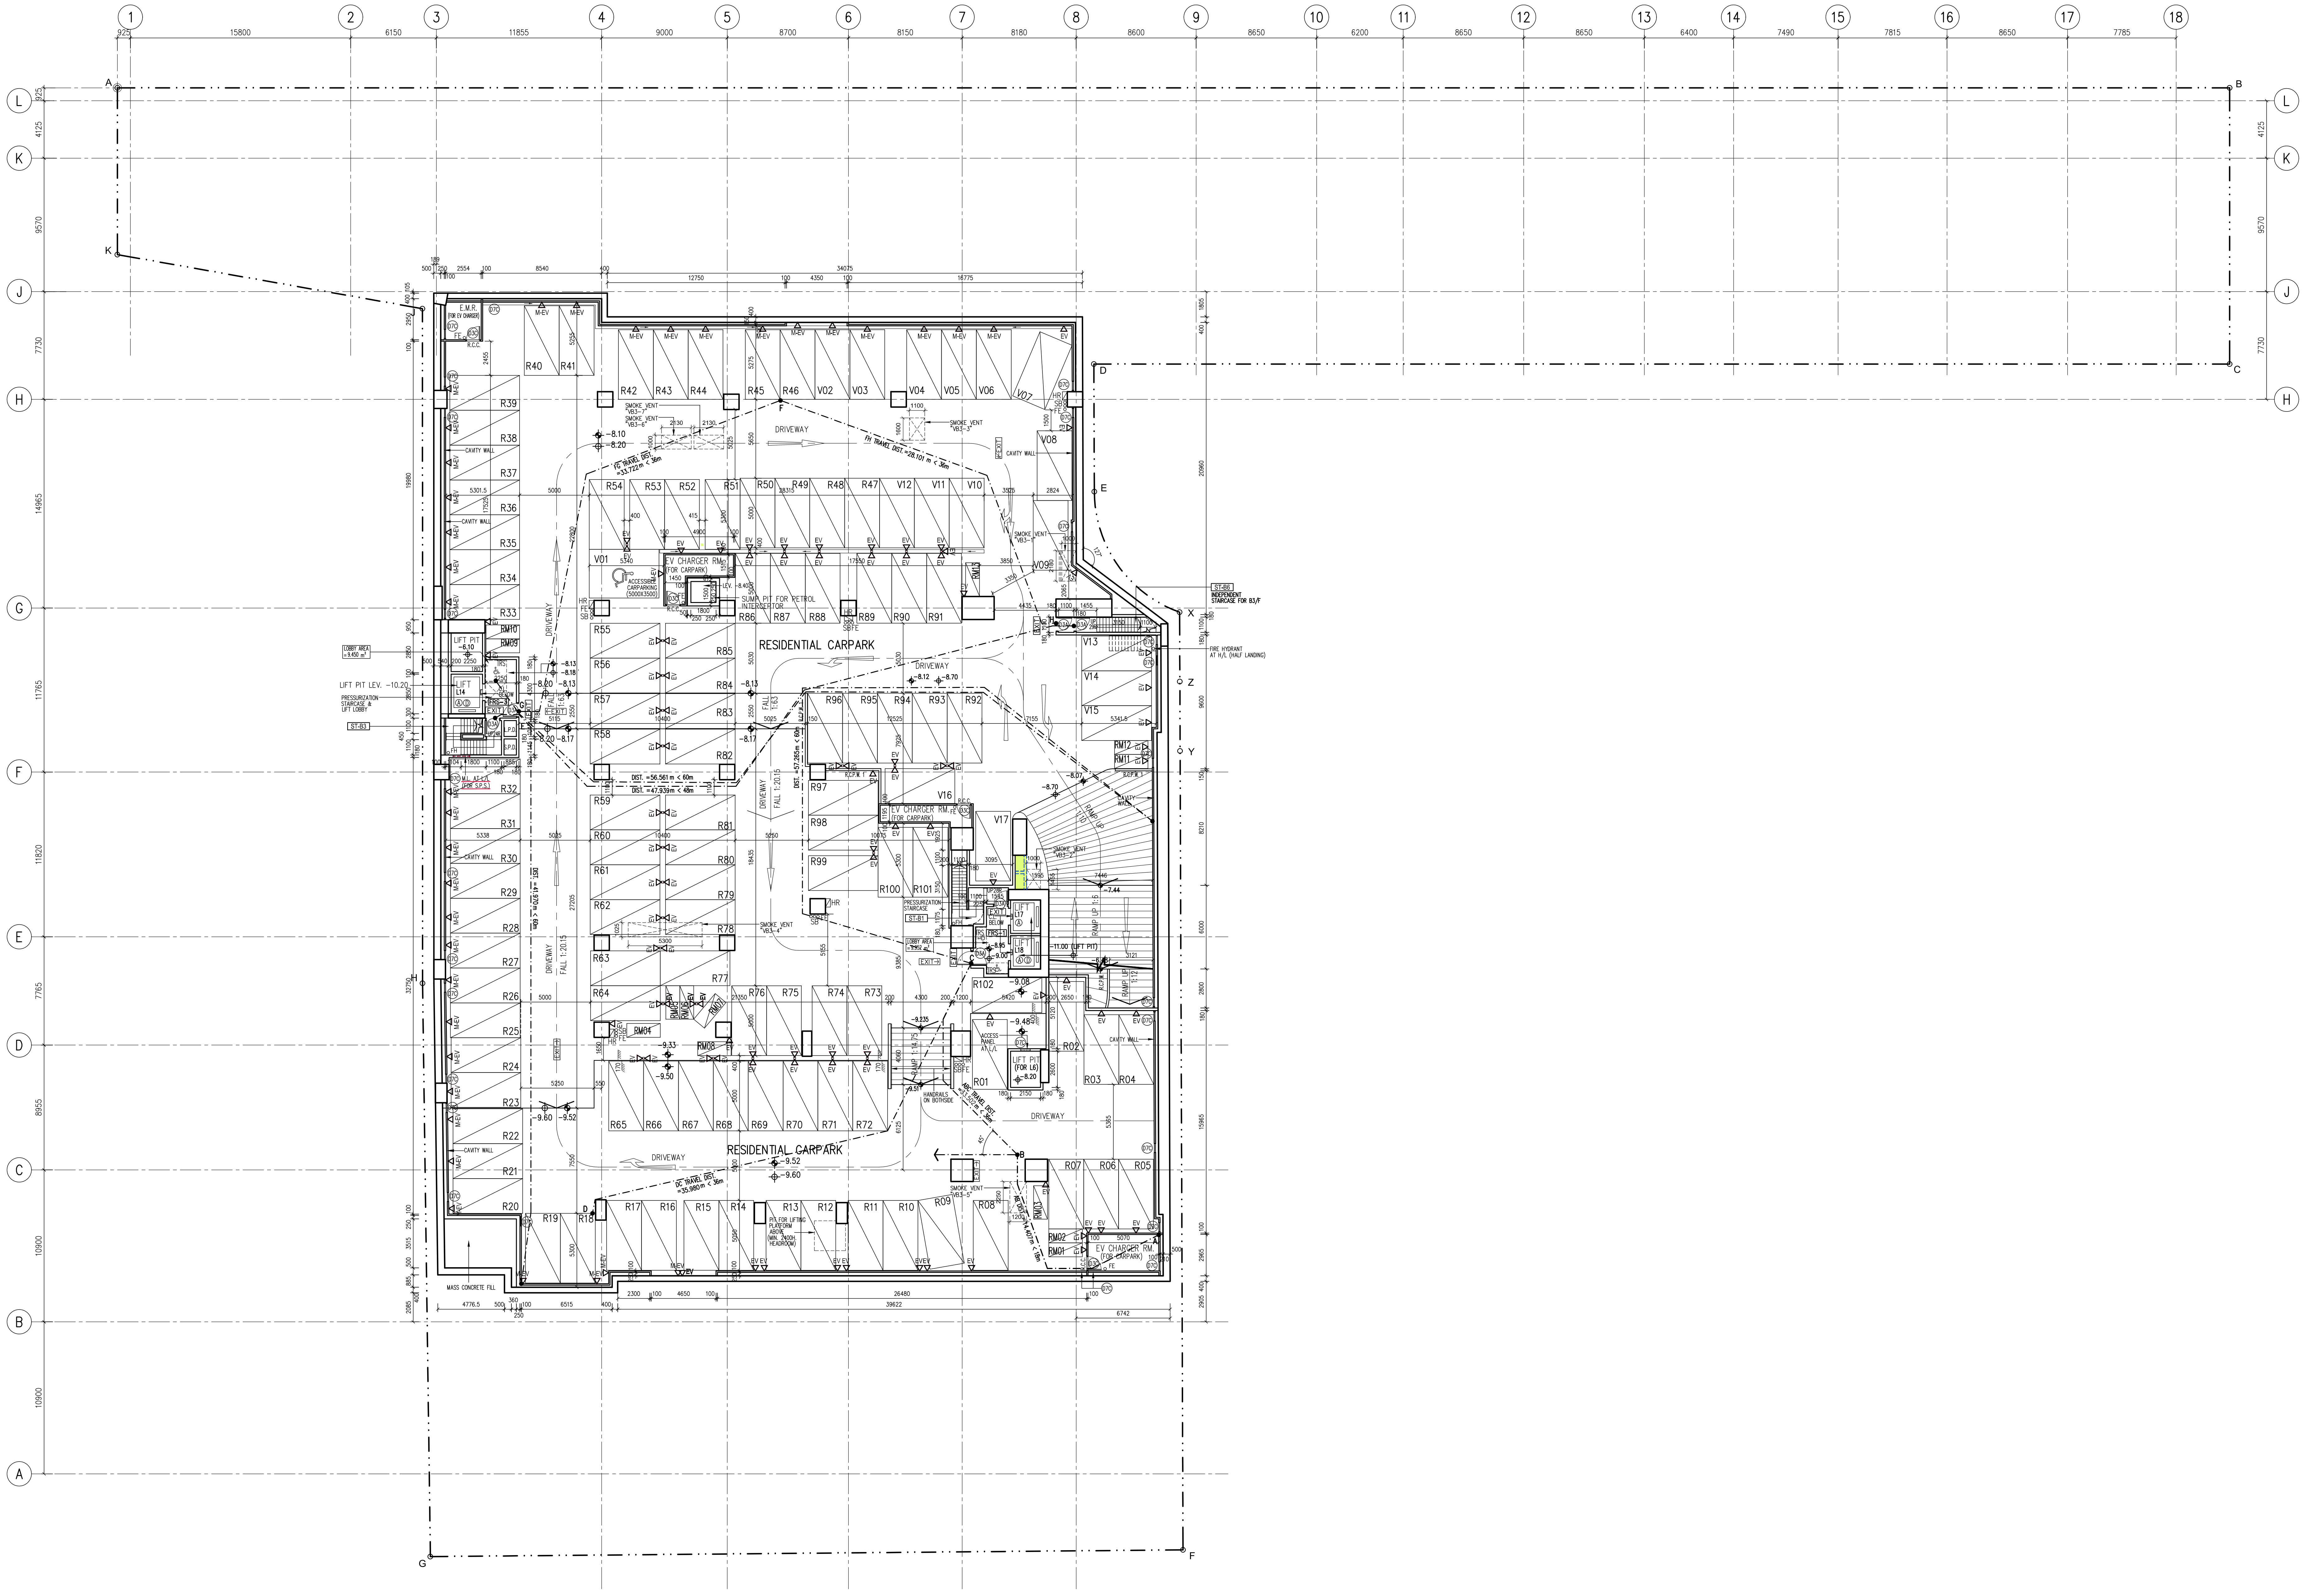
RESIDENTIAL CARPARK
RESIDENTIAL CARPARK
DRIVEWAY
E.M.R.
EV CHARGER RM. FOR CARPARK
LIFT PIT
SMOKE VENT
CAVITY WALL
MASS CONCRETE FILL
INDEPENDENT STAIRCASE FOR B2/F
FIRE HYDRANT AT H/L (HALF LANDING)
LIFT PIT LEV. –10.20
PRESSURIZATION STAIRCASE & LIFT LOBBY
SUMP PIT FOR PETROL INTERCEPTOR
1
2
3
4
5
6
7
8
9
10
11
12
13
14
15
16
17
18
L
K
J
H
G
F
E
D
C
B
A

BASEMENT 3 FLOOR PLAN

LEGEND :

△ EV	CARPARKING SPACES & MOTORCYCLE PARKING SPACES TO BE PROVIDED AND INSTALLED CHARGING FACILITIES FOR ELECTRIC VEHICLES
△ M-EV	CARPARKING SPACES TO BE PROVIDE AND INSTALL ELECTRIC VEHICLE MEDIUM CHARGER

B.D. Ref : BD 2/4024/21
BIM Ref : - --
F.S.D. Ref : - --
D.L.O. Ref : - --

Rev.	Description	Drawn	Checked	Approved	Date
-	1st Submission	WY	AW	AL	07/2022
A	2nd Submission	WY	AW	AL	11/2022
B	1st Amendment	TWM	AW	AL	04/2023
C	2nd Amendment	TWM	AW	AL	12/2023
D	3rd Amendment	TWM	AW	AL	04/2024
D	3rd Amendment (Re-submission)	TWM	AW	AL	05/2024
E	5th Amendment	TWM	AW	AL	12/2024
E	5th Amendment (Re-submission)	TWM	AW	AL	02/2025
F	8th Amendment	TWM	AW	AL	05/2025
G	9th Amendment	TWM	AW	AL	08/2025
G	9th Amendment (Re-submission)	TWM	AW	AL	10/2025
G	9th Amendment	TWM	AW	AL	10/2025
H	11th Amendment	TWM	AW	AL	2/2026

Type II works
The works shown on these plans are Type II works (Building Amendment) in respect of which consent is applied for the purpose of Fast Track consent application under regulation 33 of the Building (Administration) Regulations.

RONALD LU & PARTNERS
呂元祥建築師事務所

Project Title :
PROPOSED DEVELOPMENT
AT BAILEY STREET
& WING KWONG STREET
TO KWA WAN, KOWLOON

Drawing Title :
BASEMENT 3 FLOOR PLAN

Drawn By	TWM	Date	08/2025
Checked By	AW	Date	08/2025
Approved By	AL	Date	08/2025
Project No.	21163KL	Issue Date	08/2025

File Path :
U:\Studio_B\Proj_Data\2021\21163KL_Bailey Street & Wing Kwong Street\DRAWING\SUB\BD\GBP_13 (Final Amendment)_Hand Amend\PLOT\A_GBP_03.dwg

Scale 1:200 By CAD

Drawing Number : A/GBP/03
Revision Number : H

Drawing Purpose
Buildings Department
Amended Plan

Digitally signed by
LEUNG Kit Man Andy
AP(A) 80/85
16 March 2026

Received on
16 March 2026

Plan Approved
(Digitally Signed)
TSOI Lap-san, Lapson
Senior Building Surveyor
for BUILDING AUTHORITY
17 March 2026

Note: This plan has been processed on a curtailed check basis under the centralized processing system as promulgated in PNAP ADM-19. The duties of the authorized person, registered structural engineer and/or registered geotechnical engineer concerned as specified under section 4(3)(b) and the provision of section 14(2)(c) of the Buildings Ordinance are of particular relevance in this regard.

SMOKE VENT CALCULATION (NOT FOR FSD APPROVAL) :

(COMPARTMENT (B2-3) + (B1-1))
AREA REFER DWG. NO. A/GBP/35)

NO.	SIZE	TOTAL
VB2-1	2.130 X 1.100 = 2.343 s.m.	23.628
VB2-2	2.535 X 1.000 = 2.535 s.m.	
VB2-3	2.000 X 1.000 = 2.000 s.m.	
VB2-4	4.000 X 1.000 = 4.000 s.m.	
VB2-5	4.000 X 1.000 = 4.000 s.m.	
VB2-6	3.650 X 1.000 = 3.650 s.m.	
VB2-7	1.000 X 1.000 = 1.000 s.m.	
VB2-8	1.000 X 1.000 = 1.000 s.m.	
VB2-9	1.000 X 1.000 = 1.000 s.m.	
VB2-10	2.100 X 1.000 = 2.100 s.m.	

COMPARTMENT FLOOR AREA = 4693.743 m^2
SMOKE OUTLET AREA REQ. = 4693.743 x 0.5% = 23.469 m^2
SMOKE OUTLET AREA PROV. = 23.628 m^2 > 23.469 m^2

(COMPARTMENT (B2-2)
AREA REFER DWG. NO. A/GBP/35)
NOTE : DYNAMIC SMOKE EXTRACTION TO BE PROVIDED.

NO.	SIZE	TOTAL
VB2-11	1.000 X 1.000 = 1.000 s.m.	2
VB2-12	1.000 X 1.000 = 1.000 s.m.	

FIRE COMPARTMENT VOLUME = 3773.697 m^3
SMOKE OUTLET Nos. REQ. = 3773.697 / 3500 = 1.078
SMOKE OUTLET Nos. PROV. = 2 Nos.

NOTES:

ALL SMOKE VENT ENCLOSURE TO BE -/240/240 FRR
ALL S.E.S. A.D. WITHIN THE SAME COMPARTMENT.

PUBLIC PARKING SPACE (2.5mx5.0mx2.4m HEADROOM)		PROVIDE		
			M-EV	EV
	P001 - P100	100* Nos.	30#	70
PUBLIC MOTOR CYCLE PARKING SPACE (1.0mx2.4mx2.4m HEADROOM)				
	PM01 - PM20	20 Nos.	6#	14

* (INCLUDED 2 NOS. ACCESSIBLE PARKING SPACE CARPARK WHICH SHALL BE DESIGNATED AS "COMMON AREA" IN DEED OF MUTUAL COVENANT "DMC" OR SUB-DEED OF MUTUAL COVENANT "SUB-DMC" (IF ANY)

# (NOT LESS THAN 30% OF THE PARKING SPACES PROVIDED)

RETAIL CAR PARK SPACE (2.5mx5.0mx2.4m HEADROOM)		PROVIDE		
			M-EV	EV
	C201 - C246	46* Nos.	14#	32
LOADING/UNLOADING ** (7mx3.5mx3.6m HEADROOM)				
RESIDENTIAL	LG01 - LG04	4 Nos.		
NON-INDUSTRIAL	LG05 - LG11	7 Nos.		

* (INCLUDED 2 NOS. ACCESSIBLE PARKING SPACE CARPARK WHICH SHALL BE DESIGNATED AS "COMMON AREA" IN DEED OF MUTUAL COVENANT "DMC" OR SUB-DEED OF MUTUAL COVENANT "SUB-DMC" (IF ANY)

# (NOT LESS THAN 30% OF THE PARKING SPACES PROVIDED)

** LOADING/UN-LOADING SPACE WHICH SHALL BE DESIGNATED AS "COMMON AREA" IN DEED OF MUTUAL COVENANT "DMC" OR SUB-DEED OF MUTUAL CONVENT "SUB-DMC" (IF ANY)

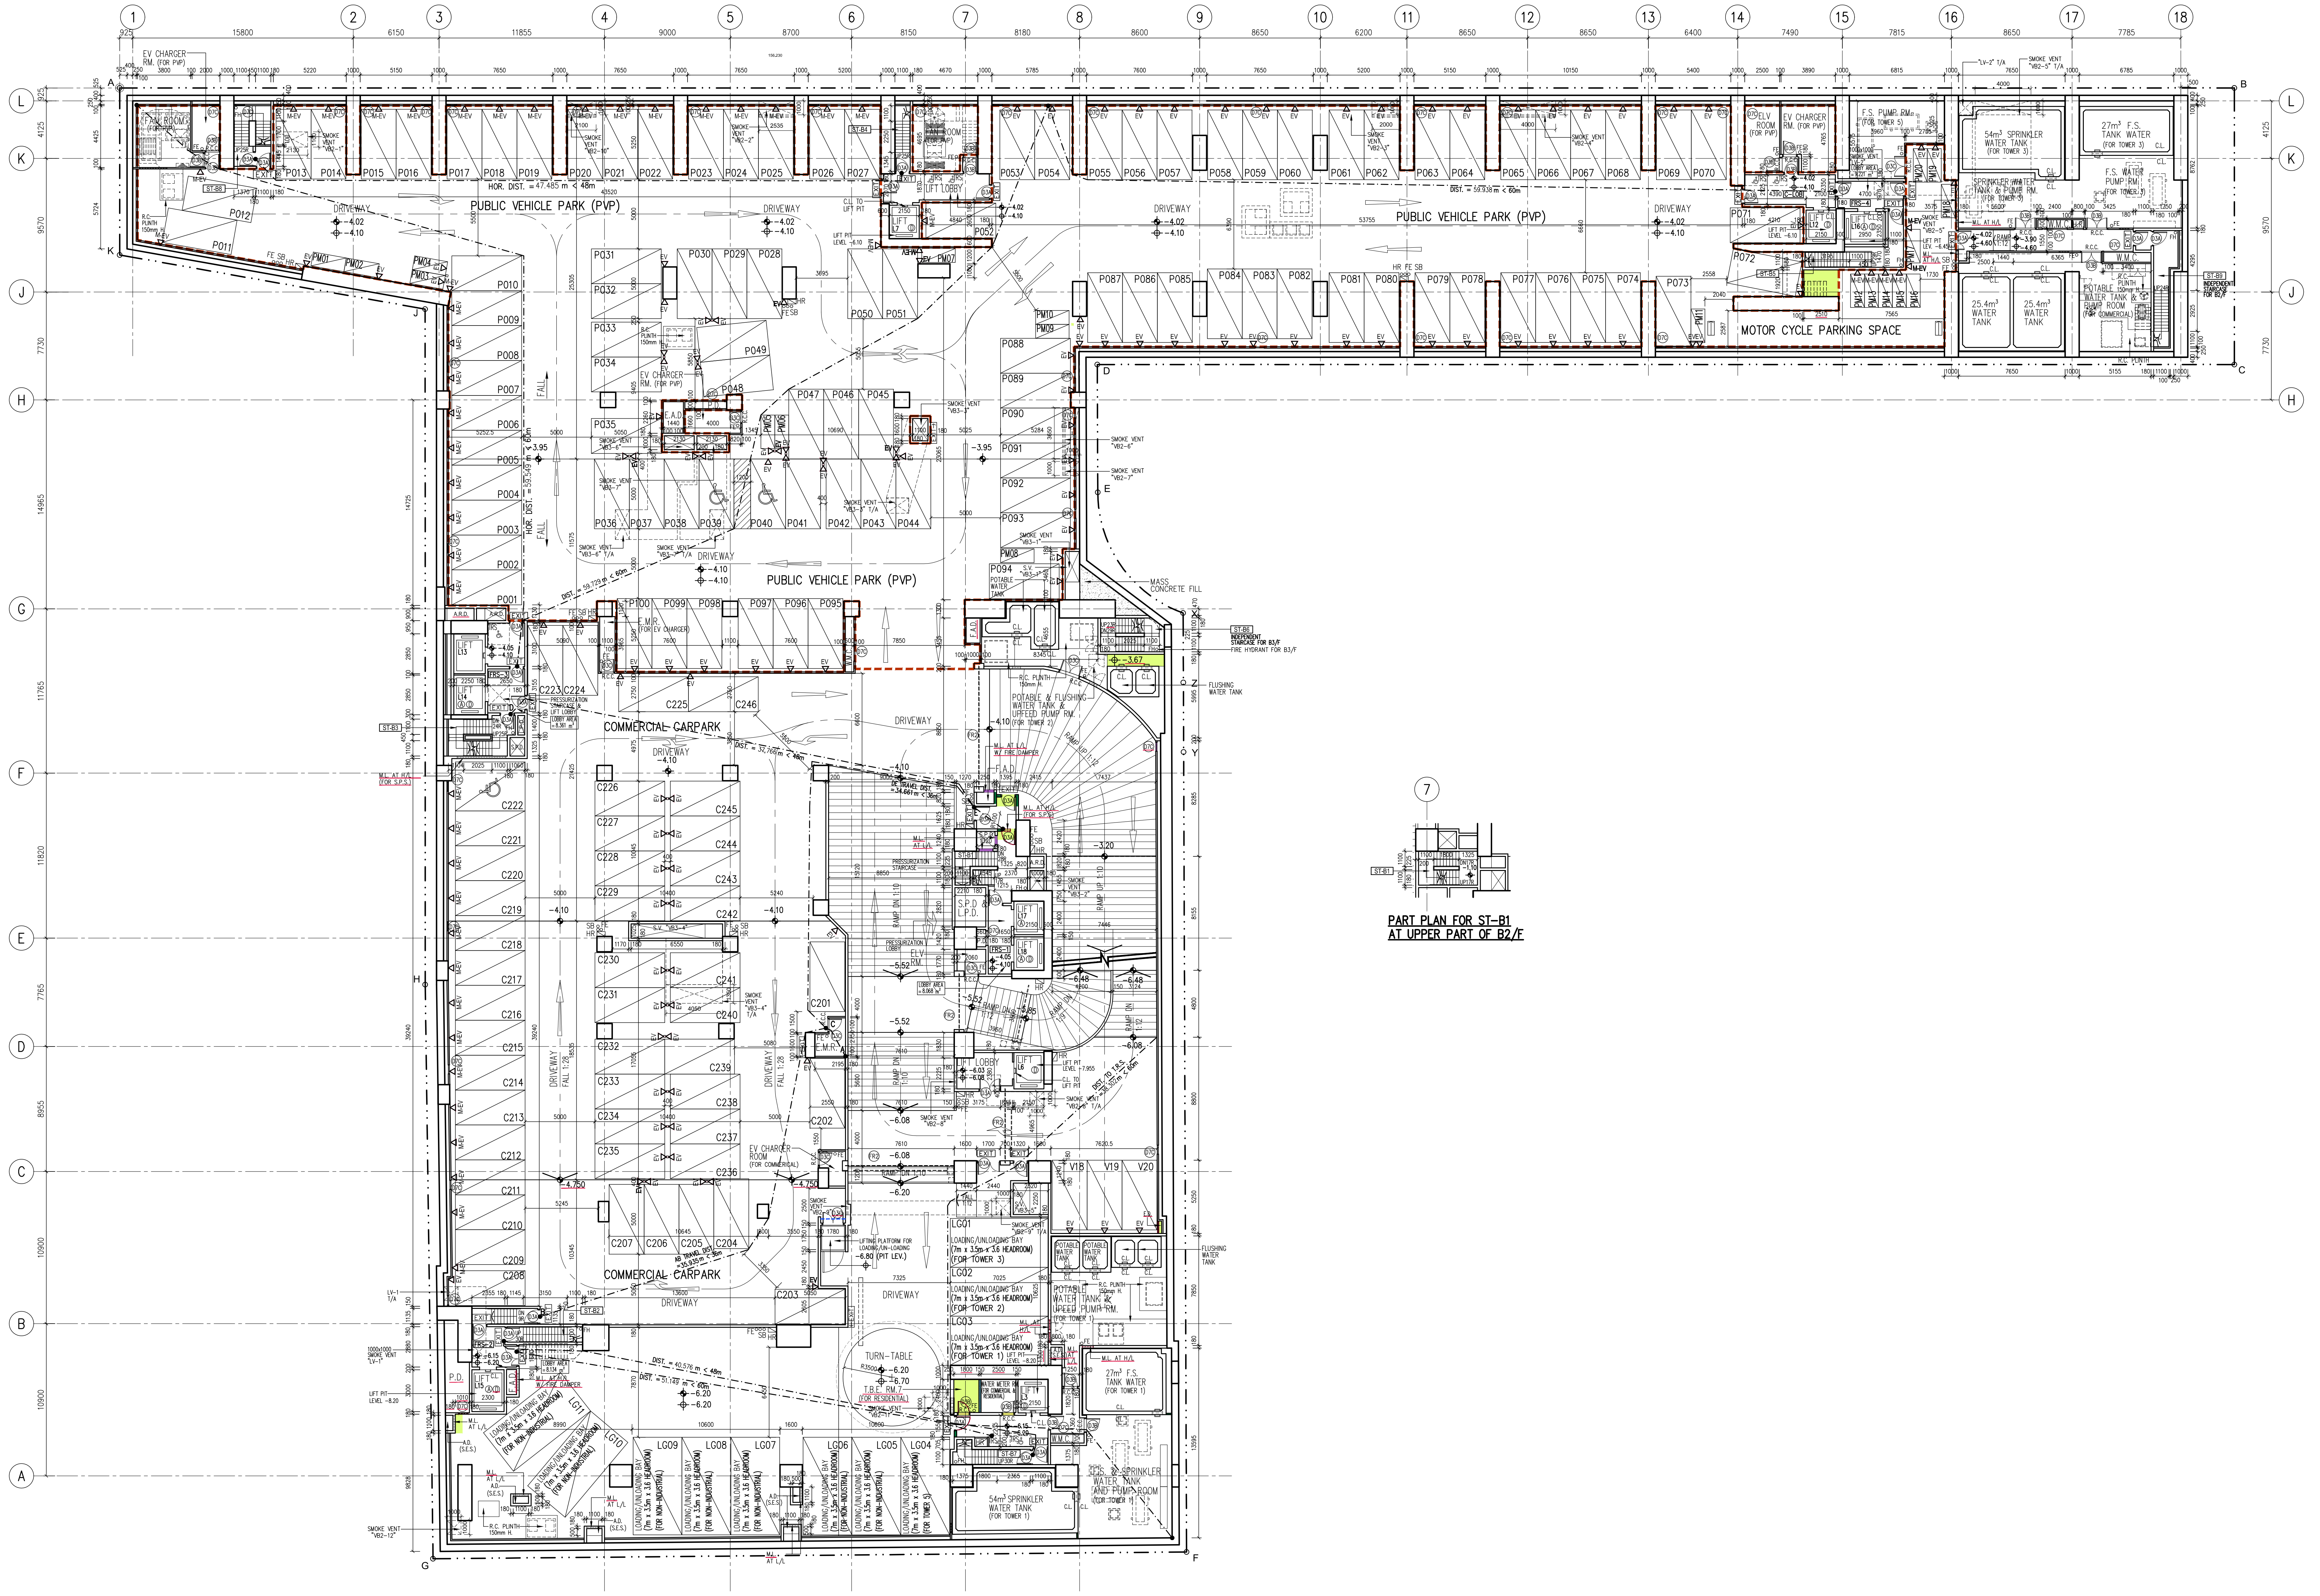

BASEMENT 2 FLOOR PLAN

PART PLAN FOR ST-B1
AT UPPER PART OF B2/F

LEGEND :

△ EV	CARPARKING SPACES & MOTORCYCLE PARKING SPACES TO BE PROVIDED AND INSTALLED CHARGING FACILITIES FOR ELECTRIC VEHICLES
△ M-EV	CARPARKING SPACES TO BE PROVIDE AND INSTALL ELECTRIC VEHICLE MEDIUM CHARGER
▬ ▬ ▬	EXTENT OF "PUBLIC VEHICLE PARK"
PVP	PUBLIC VEHICLE PARK

B.D. Ref : BD 2/4024/21
BIM Ref : - --
F.S.D. Ref : - --
D.L.O. Ref : - --

Rev.	Description	Drawn	Checked	Approved	Date
-	1st Submission	WY	AW	AL	07/2022
A	2nd Submission	WY	AW	AL	11/2022
B	1st Amendment	TWM	AW	AL	04/2023
C	2nd Amendment	TWM	AW	AL	12/2023
D	3rd Amendment	TWM	AW	AL	04/2024
D	3rd Amendment (Re-submission)	TWM	AW	AL	05/2024
E	5th Amendment	TWM	AW	AL	12/2024
E	5th Amendment (Re-submission)	TWM	AW	AL	02/2025
F	7th Amendment	LKM	AW	AL	03/2025
G	8th Amendment	TWM	AW	AL	05/2025
H	9th Amendment	TWM	AW	AL	08/2025
H	9th Amendment (Re-submission)	TWM	AW	AL	10/2025
I	11th Amendment	TWM	AW	AL	2/2026

Type II works
The works shown on these plans are Type II works (Building Amendment) in respect of which consent is applied for the purpose of Fast Track consent application under regulation 33 of the Building (Administration) Regulations.

RONALD LU & PARTNERS

呂元祥建築師事務所

Project Title :
PROPOSED DEVELOPMENT
AT BAILEY STREET
& WING KWONG STREET
TO KWA WAN, KOWLOON

Drawing Title :
BASEMENT 2 FLOOR PLAN

Drawn By TWM Date 08/2025
Checked By AW Date 08/2025
Approved By AL Date 08/2025
Project No. 21163KL Issue Date 08/2025
File Path : U:\Studio_B\Proj_Data\2021\21163KL_Bailey Street & Wing Kwong Street\DRAWING\SUB\BD\GBP_13 (Final Amendment)_Hand Amend\PLOT\A_GBP_04.dwg
Scale 1:200 By CAD
Drawing Number : A/GBP/04
Revision Number : I

Drawing Purpose
Buildings Department
Amended Plan

Digitally signed by
LEUNG Kit Man Andy
AP(A) 80/85
16 March 2026

Received on
16 March 2026

Plan Approved
(Digitally Signed)
TSOI Lap-san, Lapson
Senior Building Surveyor
for BUILDING AUTHORITY
17 March 2026

Note: This plan has been processed on a curtailed check basis under the centralized processing system as promulgated in PNAP ADM-19. The duties of the authorized person, registered structural engineer and/or registered geotechnical engineer concerned as specified under section 4(3)(b) and the provision of section 14(2)(c) of the Buildings Ordinance are of particular relevance in this regard.

SMOKE VENT CALCULATION (NOT FOR FSD APPROVAL):

(COMPARTMENT (B1–4))
AREA REFER DWG. NO. A/GBP/35)
NOTE : DYNAMIC SMOKE EXTRACTION TO BE PROVIDED.

NO.	SIZE	TOTAL
VB1–1	1.000 X 1.000 = 1.000 s.m.	4
VB1–2	1.000 X 1.000 = 1.000 s.m.	
VB1–3	1.000 X 1.000 = 1.000 s.m.	
VB1–4	1.000 X 1.000 = 1.000 s.m.	

SMOKE VENT AREA CALCULATION :

FIRE COMPARTMENT VOLUME = 11185.375 m³
SMOKE OUTLET Nos. REQ. = 11185.375 / 3500 = 3.196
SMOKE OUTLET Nos. PROV. = 4 Nos.

(COMPARTMENT (B2–4) + (B1–6) + (G–9) + (B1–2))
AREA REFER DWG. NO. A/GBP/35)

NO.	SIZE	TOTAL
VB1–11	1.000 X 2.150 = 2.150 s.m.	9.050
VB1–12	1.900 X 1.000 = 1.900 s.m.	
VB1–13	1.000 X 1.000 = 1.000 s.m.	
VB1–14	1.000 X 1.500 = 1.500 s.m.	
VB1–15	1.000 X 1.000 = 1.000 s.m.	
VB1–16	1.000 X 1.500 = 1.500 s.m.	

SMOKE VENT AREA CALCULATION :

COMPARTMENT FLOOR AREA = 1699.560 m²
SMOKE OUTLET AREA REQ. = 1699.560 x 0.5% = 8.498 m²
SMOKE OUTLET AREA PROV. = 9.050 m² > 8.498 m²

(COMPARTMENT (B1–3))
AREA REFER DWG. NO. A/GBP/35)
NOTE : DYNAMIC SMOKE EXTRACTION TO BE PROVIDED.

NO.	SIZE	TOTAL
VB1–21	1.000 X 1.000 = 1.000 s.m.	2
VB1–22	1.000 X 1.000 = 1.000 s.m.	

SMOKE VENT AREA CALCULATION :

FIRE COMPARTMENT VOLUME = 3716.416 m³
SMOKE OUTLET Nos. REQ. = 3716.416 / 3500 = 1.062
SMOKE OUTLET Nos. PROV. = 2 Nos.

(COMPARTMENT (B1–5)
AREA REFER DWG. NO. A/GBP/35)

NO.	SIZE	TOTAL
VB1–31	4.000 X 1.000 = 4.000 s.m.	5.595 s.m.
VB1–32	1.595 X 1.000 = 1.595 s.m.	

SMOKE VENT AREA CALCULATION :

COMPARTMENT FLOOR AREA = 1086.560 m²
SMOKE OUTLET AREA REQ. = 1086.560 x 0.5% = 5.433 m²
SMOKE OUTLET AREA PROV. = 5.595 m² > 5.433 m²

NOTES:
ALL SMOKE VENT ENCLOSURE TO BE –/240/240 FRR
ALL S.E.S. A.D. WITHIN THE SAME COMPARTMENT.

COMMERCIAL CAR PARKING SPACE (2.5mx5.0mx2.4m HEADROOM)			M–EV	EV
	C101 – C112	12 Nos.	4 #	8
COMMERCIAL MOTOR CYCLE PARKING SPACE (1.0mx2.4mx2.4m HEADROOM)				
	CM01 – CM06	6 Nos.	–	6
LOADING/UN–LOADING ** (11mx3.5mx4.7m HEADROOM) / (7mx3.5mx3.6m HEADROOM)				
NON–INDUSTRIAL	HG01 – HG06	6 Nos.	–	
NON–INDUSTRIAL	LG012	1 Nos.	–	

(NOT LESS THAN 30% OF THE PARKING SPACES PROVIDED)

** LOADING/UN–LOADING SPACE WHICH SHALL BE DESIGNATED AS "COMMON AREA" IN DEED OF MUTUAL COVENANT "DMC" OR SUB–DEED OF MUTUAL CONVENT "SUB–DMC" (IF ANY)

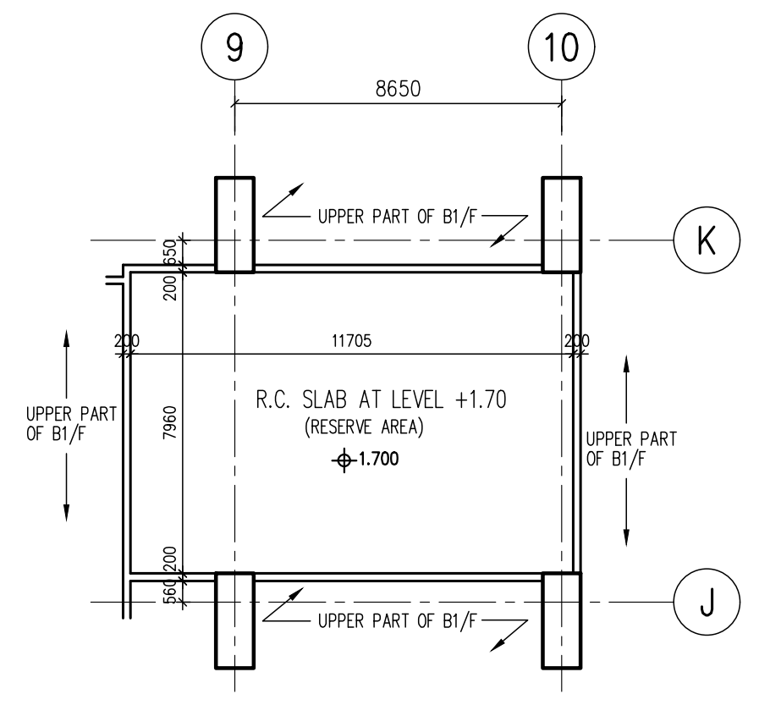

9
10
8650
K
J
UPPER PART OF B1/F
R.C. SLAB AT LEVEL +1.70 (RESERVE AREA)
+1.700
11705
7960

PART PLAN FOR RC SLAB
AT LEVEL +1.70 & +0.80

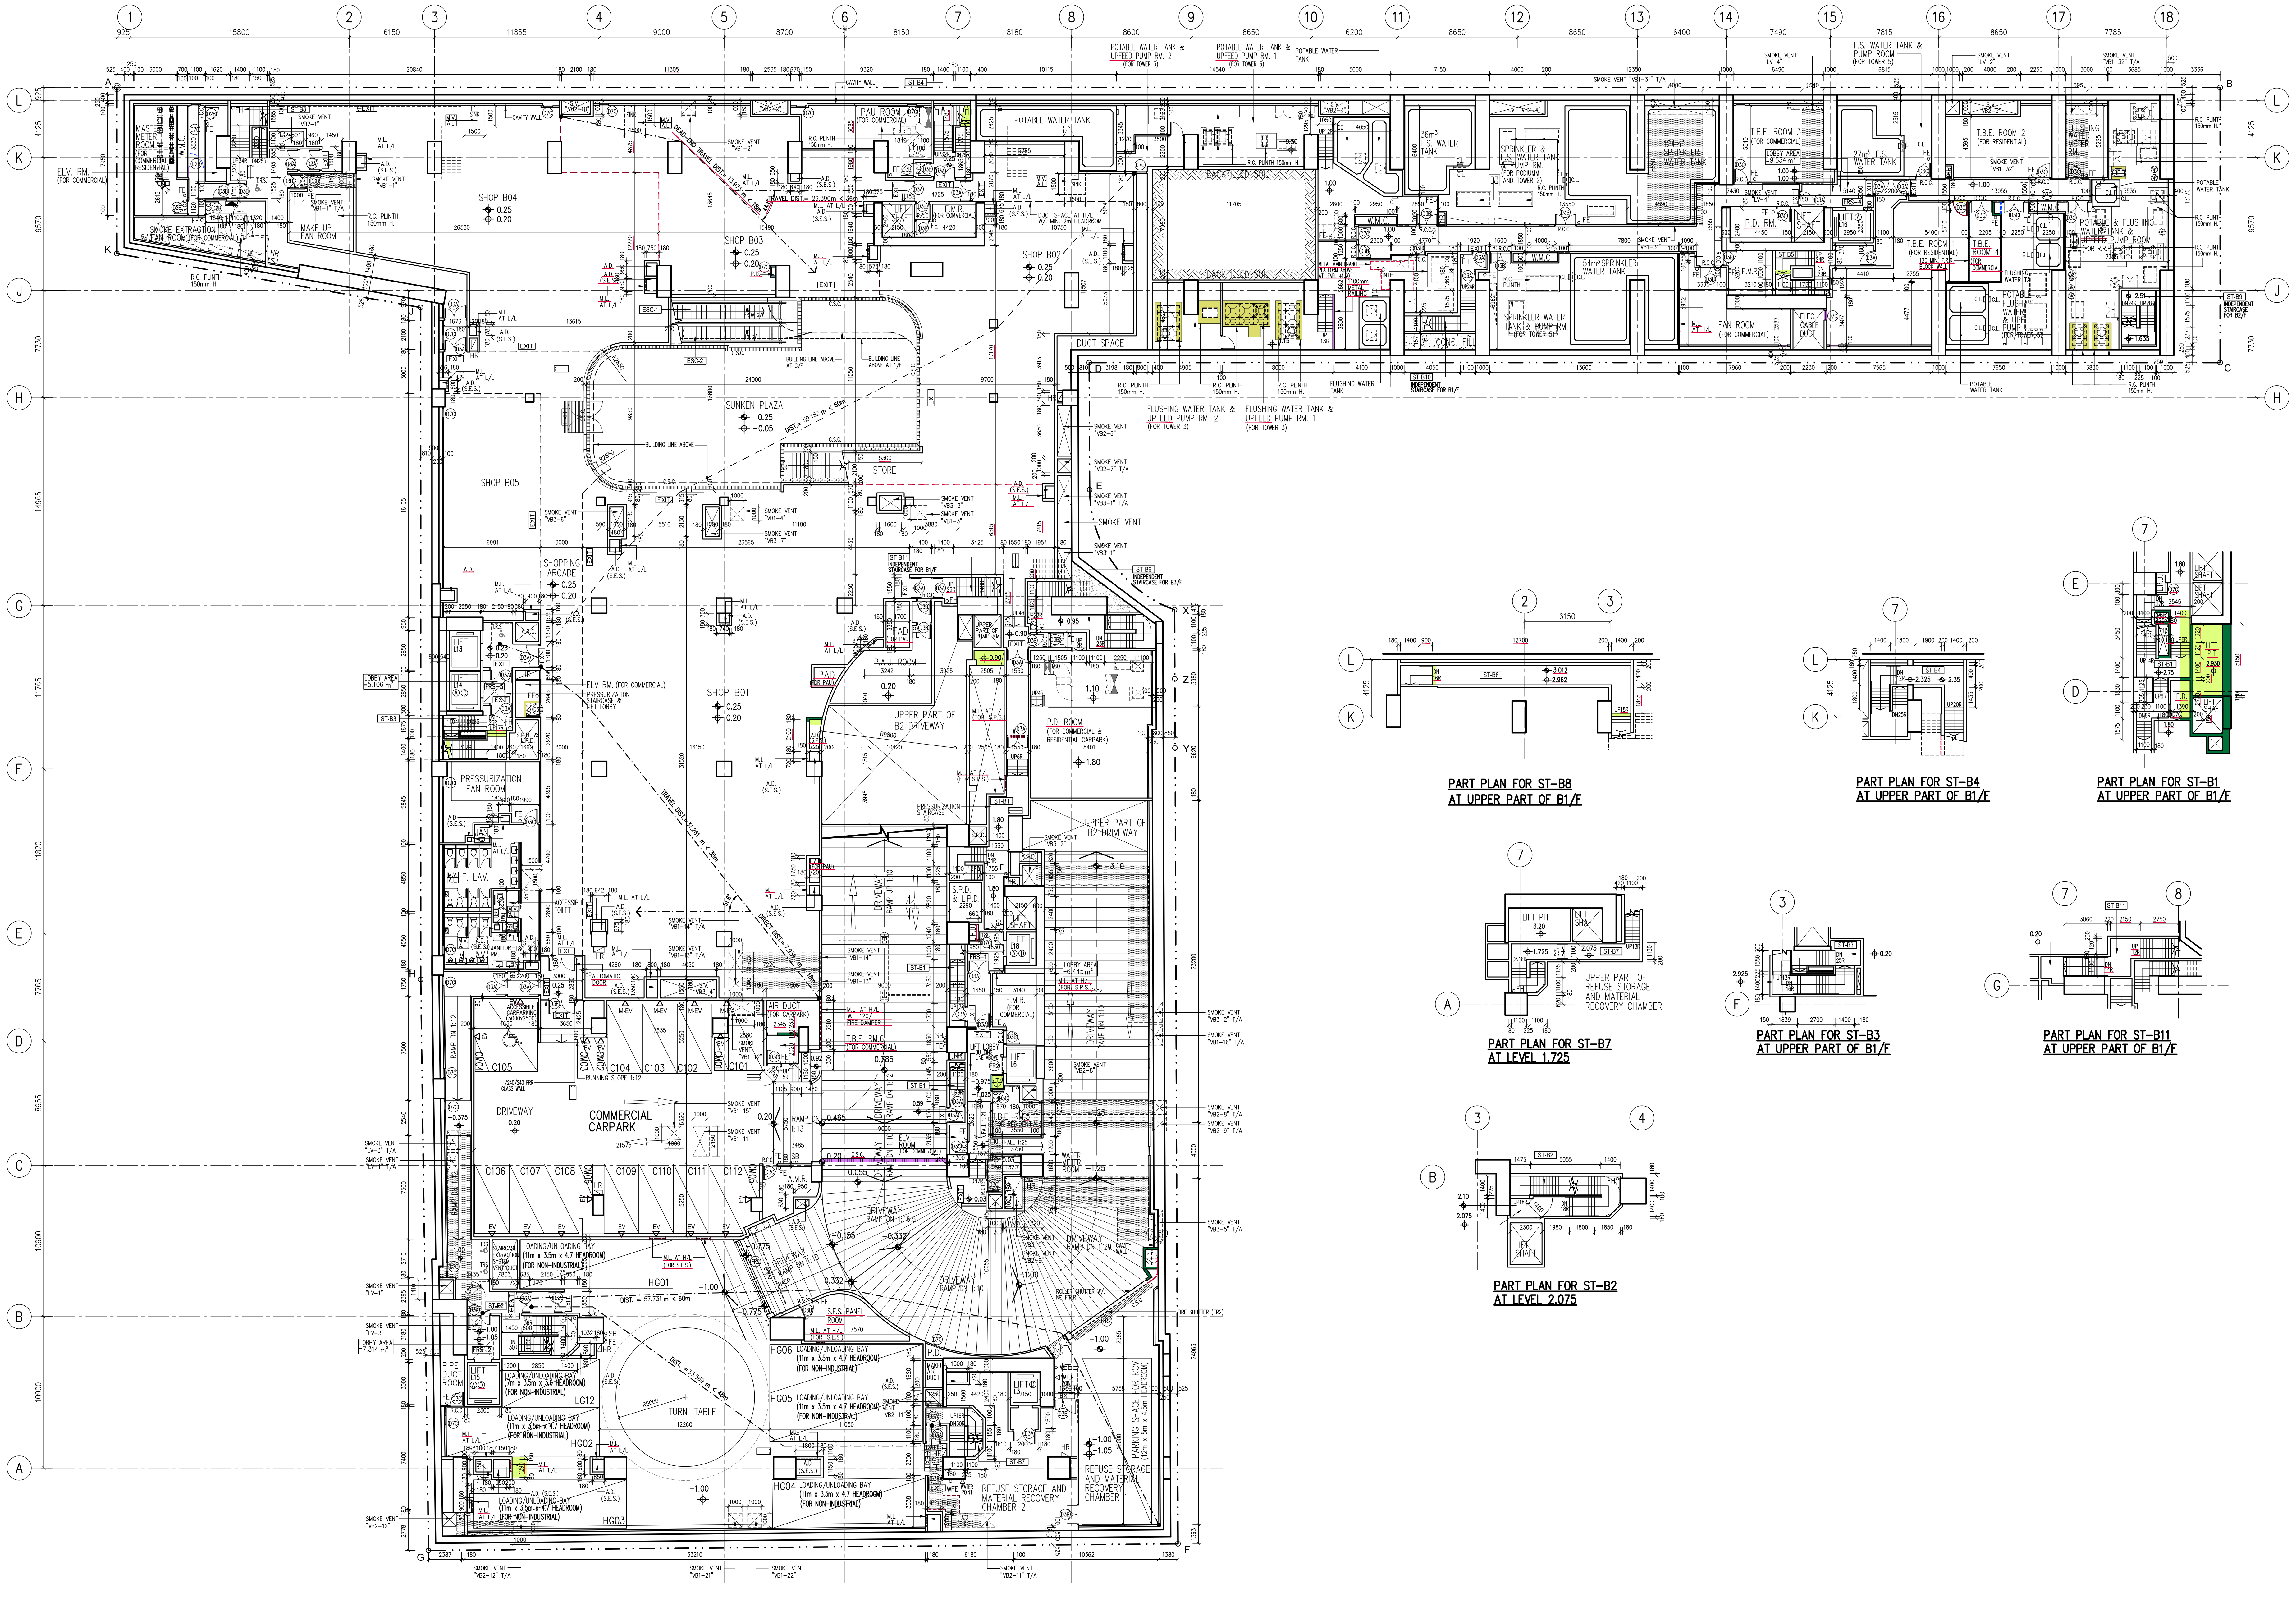

1
2
3
4
5
6
7
8
9
10
11
12
13
14
15
16
17
18
L
K
J
H
G
F
E
D
C
B
A
15800
6150
11855
9000
8700
8150
8180
8600
8650
6200
8650
8650
6400
7490
7815
8650
7785
ELV. RM. (FOR COMMERCIAL)
SHOP B04
SHOP B03
SHOP B02
SHOP B05
SHOP B01
SUNKEN PLAZA
SHOPPING ARCADE
STORE
DUCT SPACE
POTABLE WATER TANK
F.S. WATER TANK
SPRINKLER WATER TANK
T.B.E. ROOM
P.D. RM.
FAN ROOM
P.A.U. ROOM
PRESSURIZATION FAN ROOM
P.D. ROOM
UPPER PART OF B2 DRIVEWAY
DRIVEWAY
COMMERCIAL CARPARK
C101
C102
C103
C104
C105
C106
C107
C108
C109
C110
C111
C112
HG01
HG02
HG03
HG04
HG05
HG06
LG12
TURN–TABLE
REFUSE STORAGE AND MATERIAL RECOVERY CHAMBER 1
REFUSE STORAGE AND MATERIAL RECOVERY CHAMBER 2
FLUSHING WATER TANK & UPFEED PUMP RM. 1
FLUSHING WATER TANK & UPFEED PUMP RM. 2
POTABLE WATER TANK & UPFEED PUMP RM. 1
POTABLE WATER TANK & UPFEED PUMP RM. 2
SMOKE VENT "VB1–21"
SMOKE VENT "VB1–22"
SMOKE VENT "VB2–11" T/A
33210
6180

BASEMENT 1 FLOOR PLAN

2
3
6150
L
K

PART PLAN FOR ST–B8
AT UPPER PART OF B1/F

7
L
K

PART PLAN FOR ST–B4
AT UPPER PART OF B1/F

7
E
D

PART PLAN FOR ST–B1
AT UPPER PART OF B1/F

7
A
LIFT PIT
UPPER PART OF REFUSE STORAGE AND MATERIAL RECOVERY CHAMBER

PART PLAN FOR ST–B7
AT LEVEL 1.725

3
F

PART PLAN FOR ST–B3
AT UPPER PART OF B1/F

7
8
G

PART PLAN FOR ST–B11
AT UPPER PART OF B1/F

3
4
B

PART PLAN FOR ST–B2
AT LEVEL 2.075

LEGEND

▨ P – PINK HATCHED BLACK (UNDER LEASE)

△ EV CARPARKING SPACES & MOTORCYCLE PARKING SPACES TO BE PROVIDED AND INSTALLED CHARGING FACILITIES FOR ELECTRIC VEHICLES

△ M–EV CARPARKING SPACES TO BE PROVIDE AND INSTALL ELECTRIC VEHICLE MEDIUM CHARGER

B.D. Ref : BD 2/4024/21
BIM Ref : - --
F.S.D. Ref : - --
D.L.O. Ref : - --

Rev.	Description	Drawn	Checked	Approved	Date
-	1st Submission	WY	AW	AL	07/2022
A	2nd Submission	WY	AW	AL	11/2022
B	1st Amendment	TWM	AW	AL	04/2023
C	2nd Amendment	TWM	AW	AL	12/2023
D	3rd Amendment	TWM	AW	AL	04/2024
D	3rd Amendment (Re-submission)	TWM	AW	AL	05/2024
E	5th Amendment	TWM	AW	AL	12/2024
E	5th Amendment (Re-submission)	TWM	AW	AL	02/2025
F	8th Amendment	TWM	AW	AL	05/2025
G	9th Amendment	TWM	AW	AL	08/2025
G	9th Amendment (Re-submission)	TWM	AW	AL	10/2025
H	11th Amendment	TWM	AW	AL	2/2026

Type II works
The works shown on these plans are Type II works (Building Amendment) in respect of which consent is applied for the purpose of Fast Track consent application under regulation 33 of the Building (Administration) Regulations.

RONALD LU & PARTNERS
呂元祥建築師事務所

Project Title :
PROPOSED DEVELOPMENT
AT BAILEY STREET
& WING KWONG STREET
TO KWA WAN, KOWLOON

Drawing Title :
BASEMENT 1 FLOOR PLAN

Drawn By	TWM	Date	08/2025
Checked By	AW	Date	08/2025
Approved By	AL	Date	08/2025
Project No.	21163KL	Issue Date	08/2025

File Path :
U:\Studio_B\Proj_Data\2021\21163KL_Bailey Street & Wing Kwong Street\DRAWING\SUB\BD\GBP_13 (Final Amendment)_Hand Amend\PLOT\A_GBP_05.dwg

Scale 1:200 By CAD

Drawing Number : A/GBP/05
Revision Number : H

Drawing Purpose
Buildings Department
Amended Plan

Digitally signed by
LEUNG Kit Man Andy
AP(A) 80/85
16 March 2026

Received on
16 March 2026

Plan Approved
(Digitally Signed)
TSOI Lap-san, Lapson
Senior Building Surveyor
for BUILDING AUTHORITY
17 March 2026

Note: This plan has been processed on a curtailed check basis under the centralized processing system as promulgated in PNAP ADM-19. The duties of the authorized person, registered structural engineer and/or registered geotechnical engineer concerned as specified under section 4(3)(b) and the provision of section 14(2)(c) of the Buildings Ordinance are of particular relevance in this regard.

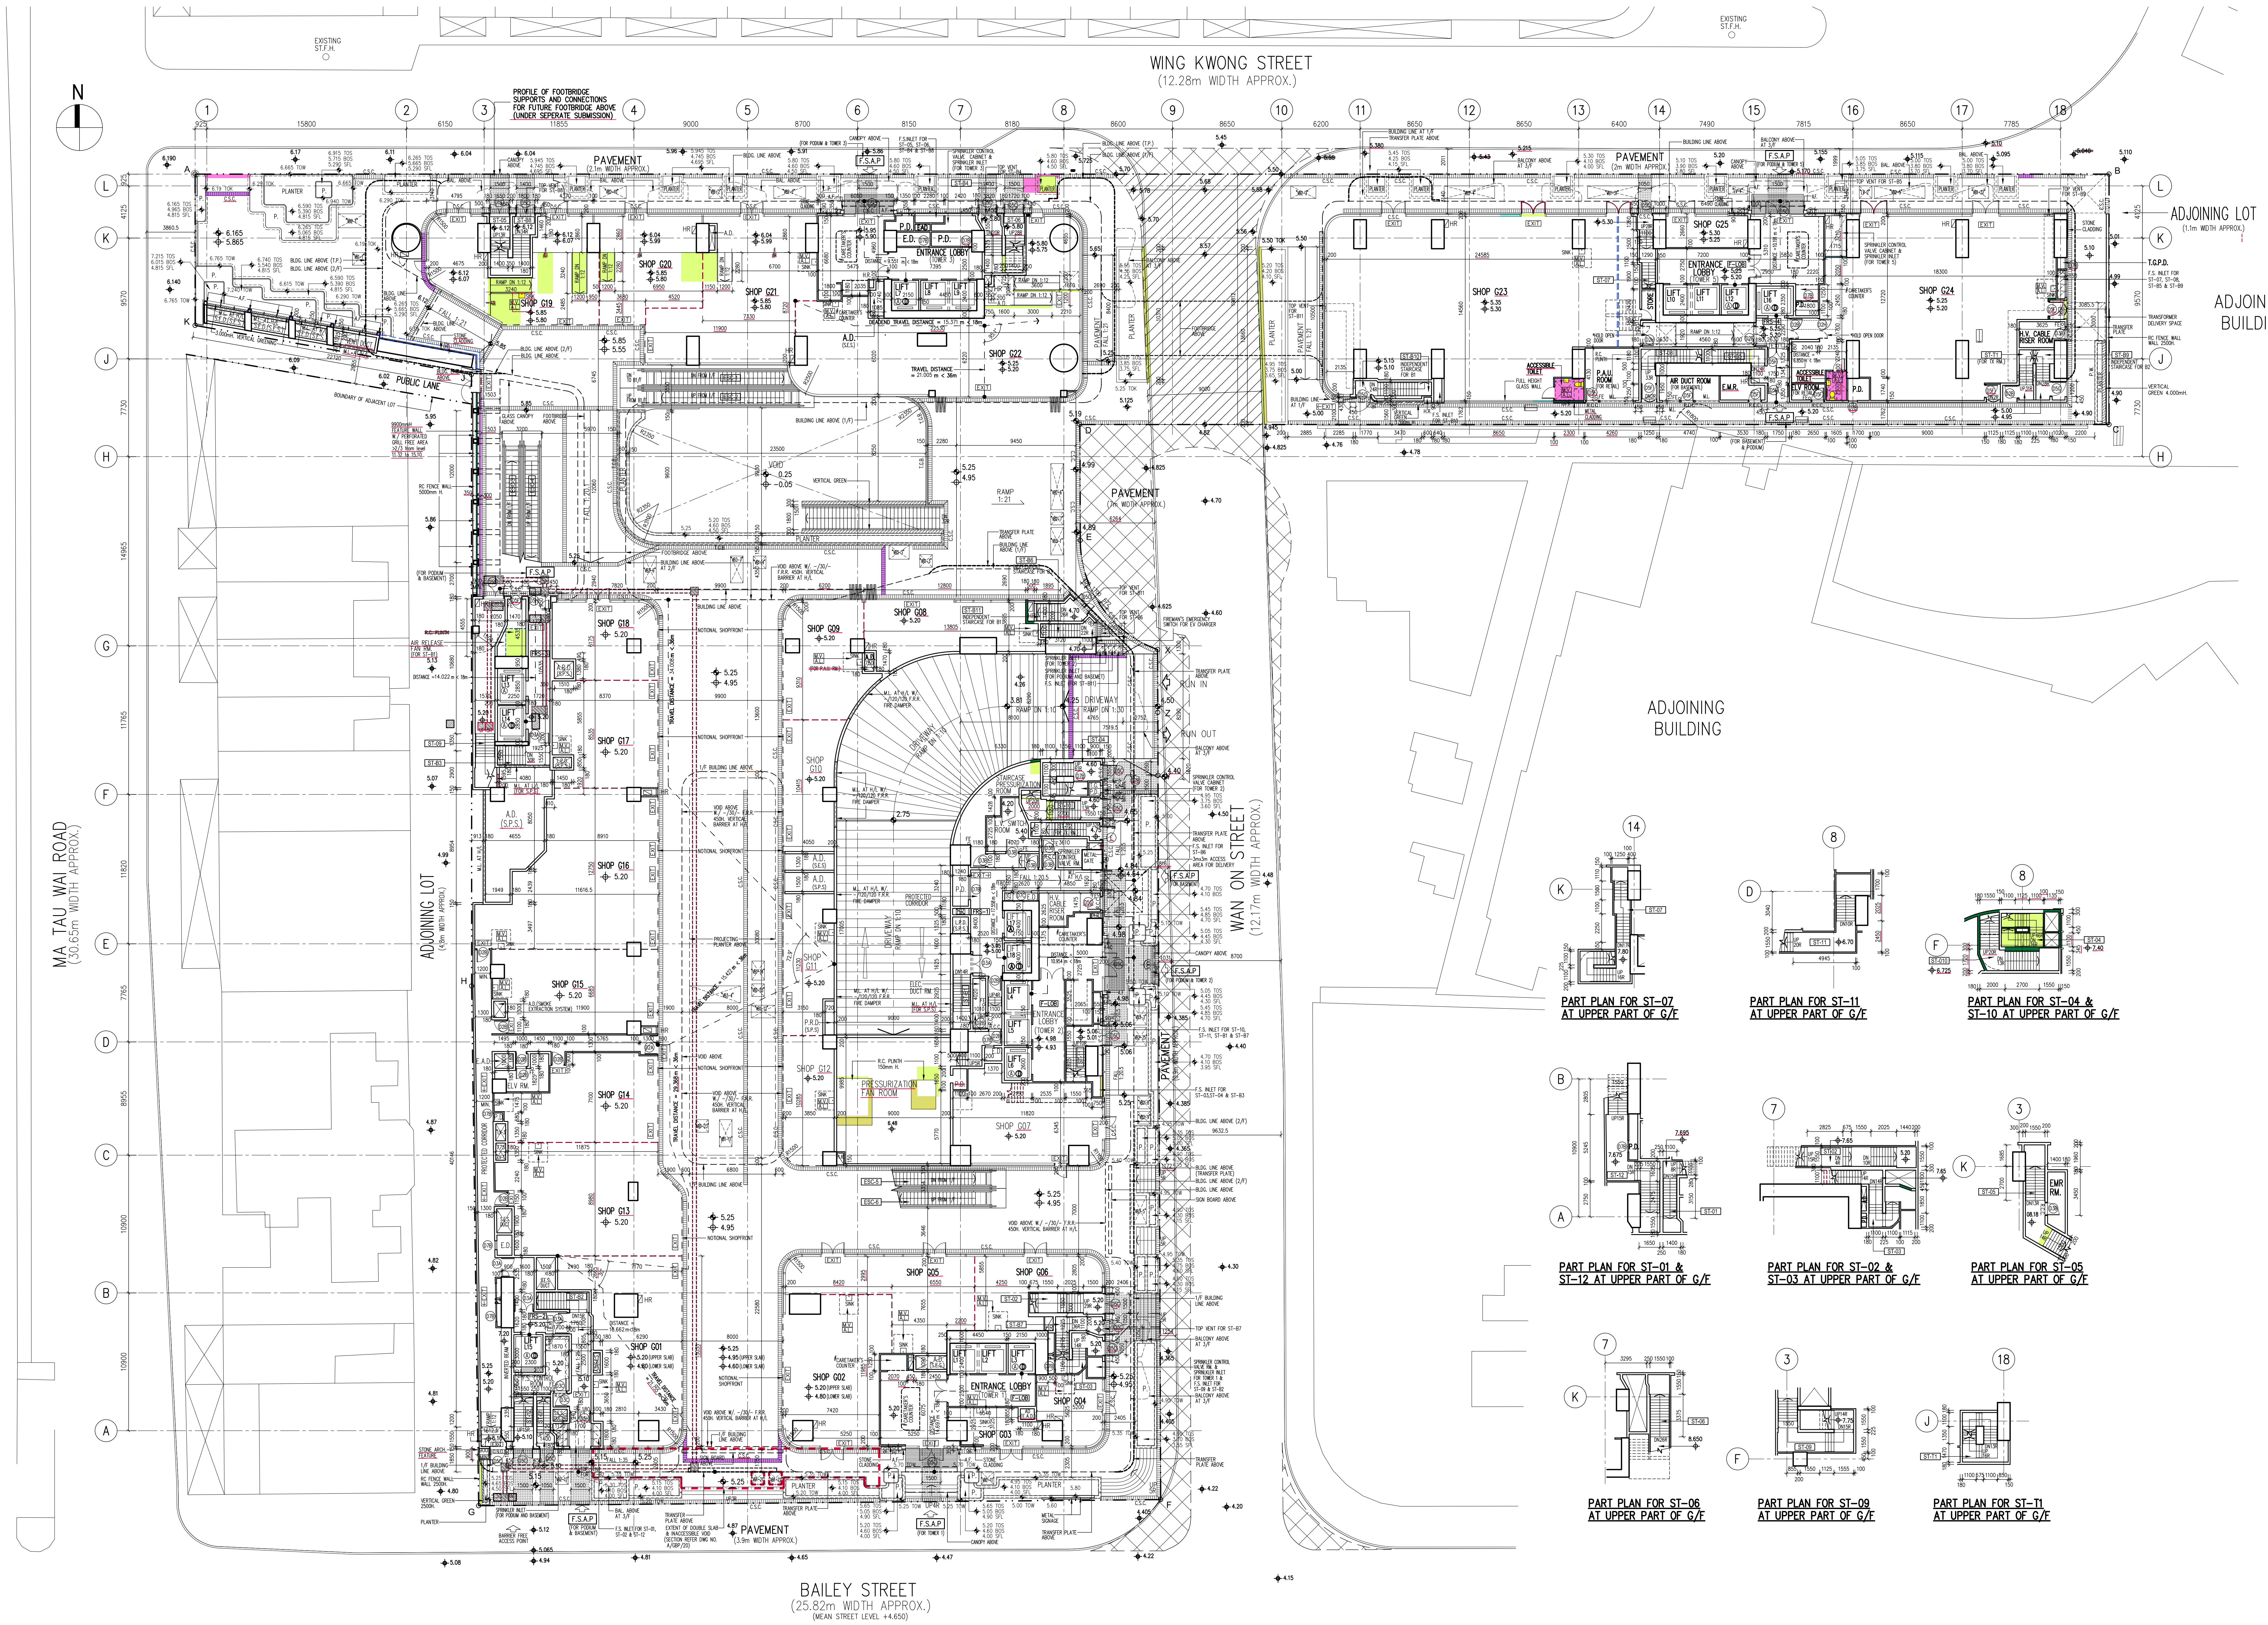
N
WING KWONG STREET
(12.28m WIDTH APPROX.)
EXISTING ST.F.H.
PROFILE OF FOOTBRIDGE SUPPORTS AND CONNECTIONS FOR FUTURE FOOTBRIDGE ABOVE (UNDER SEPERATE SUBMISSION)
PAVEMENT
PUBLIC LANE
ADJOINING LOT
ADJOINING BUILDING
MA TAU WAI ROAD
(30.63m WIDTH APPROX.)
ADJOINING LOT (4.9m WIDTH APPROX.)
WAN ON STREET
(12.17m WIDTH APPROX.)
SHOP G01
SHOP G02
SHOP G03
SHOP G04
SHOP G05
SHOP G06
SHOP G07
SHOP G08
SHOP G09
SHOP G10
SHOP G11
SHOP G12
SHOP G13
SHOP G14
SHOP G15
SHOP G16
SHOP G17
SHOP G18
SHOP G19
SHOP G20
SHOP G21
SHOP G22
SHOP G23
SHOP G24
SHOP G25
ENTRANCE LOBBY
DRIVEWAY
F.S.A.P
PART PLAN FOR ST-07 AT UPPER PART OF G/F
PART PLAN FOR ST-11 AT UPPER PART OF G/F
PART PLAN FOR ST-04 & ST-10 AT UPPER PART OF G/F
PART PLAN FOR ST-01 & ST-12 AT UPPER PART OF G/F
PART PLAN FOR ST-02 & ST-03 AT UPPER PART OF G/F
PART PLAN FOR ST-05 AT UPPER PART OF G/F
PART PLAN FOR ST-06 AT UPPER PART OF G/F
PART PLAN FOR ST-09 AT UPPER PART OF G/F
PART PLAN FOR ST-T1 AT UPPER PART OF G/F
PAVEMENT (3.9m WIDTH APPROX.)

BAILEY STREET
(25.82m WIDTH APPROX.)
(MEAN STREET LEVEL +4.650)

GROUND FLOOR PLAN

LEGEND (UNDER LEASE)

▨	P – PINK HATCHED BLACK
⊠	G – GREEN
⁘	COVERED LANDSCAPED AREA

LEGEND

▒	EXIT ROUTE OF REQUIRED STAIRCASE / COVERED PASSAGE OF F.S.A.P.	▨	TACTILE POSITIONAL TILE/BLOCKS
------	TACTILE DIRECTIONAL TILE/BLOCKS	▨	TACTILE WARNING TILE/BLOCKS

NOTE :

# ROOM SHALL BE DESIGNATED AS "COMMON AREA" IN DEED OF MUTUAL COVENANT "DMC"

* HOLD OPEN DOOR DEVICE SHALL COMPLY TO CLAUSE B13.8 OF COP FOR FIRE SAFETY IN BUILDINGS AND TO THE SATISFACTION OF THE DIRECTOR OF FIRE SERVICES.

EXISTING ST.F.H.

B.D. Ref : BD 2/4024/21
BIM Ref : - --
F.S.D. Ref : - --
D.L.O. Ref : - --

Rev.	Description	Drawn	Checked	Approved	Date
-	1st Submission	WY	AW	AL	07/2022
A	2nd Submission	WY	AW	AL	11/2022
B	1st Amendment	TWM	AW	AL	04/2023
C	2nd Amendment	TWM	AW	AL	12/2023
D	3rd Amendment	TWM	AW	AL	04/2024
D	3rd Amendment (Re-submission)	TWM	AW	AL	05/2024
E	5th Amendment	TWM	AW	AL	12/2024
E	5th Amendment (Re-submission)	TWM	AW	AL	02/2025
F	8th Amendment	TWM	AW	AL	05/2025
G	9th Amendment	TWM	AW	AL	08/2025
G	9th Amendment (Re-submission)	TWM	AW	AL	10/2025
H	10th Amendment	TWM	AW	AL	12/2025
I	11th Amendment	TWM	AW	AL	02/2026

Type II works
The works shown on these plans are Type II works (Building Amendment) in respect of which consent is applied for the purpose of Fast Track consent application under regulation 33 of the Building (Administration) Regulations.

RONALD LU & PARTNERS
呂元祥建築師事務所

Project Title :
PROPOSED DEVELOPMENT
AT BAILEY STREET
& WING KWONG STREET
TO KWA WAN, KOWLOON

Drawing Title :
GROUND FLOOR PLAN

Drawn By	TWM	Date	08/2025
Checked By	AW	Date	08/2025
Approved By	AL	Date	08/2025
Project No.	21163KL	Issue Date	08/2025

File Path : U:\Studio_B\Proj_Data\2021\21163KL_Bailey Street & Wing Kwong Street\DRAWING\SUB\BD\GBP_13 (Final Amendment)_Hand Amend\PLOT\A_GBP_06.dwg
Scale 1:200 By CAD
Drawing Number : A/GBP/06
Revision Number : I

Drawing Purpose
Buildings Department
Amended Plan

Digitally signed by
LEUNG Kit Man Andy
AP(A) 80/85
16 March 2026

Received on
16 March 2026

Plan Approved
(Digitally Signed)
TSOI Lap-san, Lapson
Senior Building Surveyor
for BUILDING AUTHORITY
17 March 2026

Note: This plan has been processed on a curtailed check basis under the centralized processing system as promulgated in PNAP ADM-19. The duties of the authorized person, registered structural engineer and/or registered geotechnical engineer concerned as specified under section 4(3)(b) and the provision of section 14(2)(c) of the Buildings Ordinance are of particular relevance in this regard.

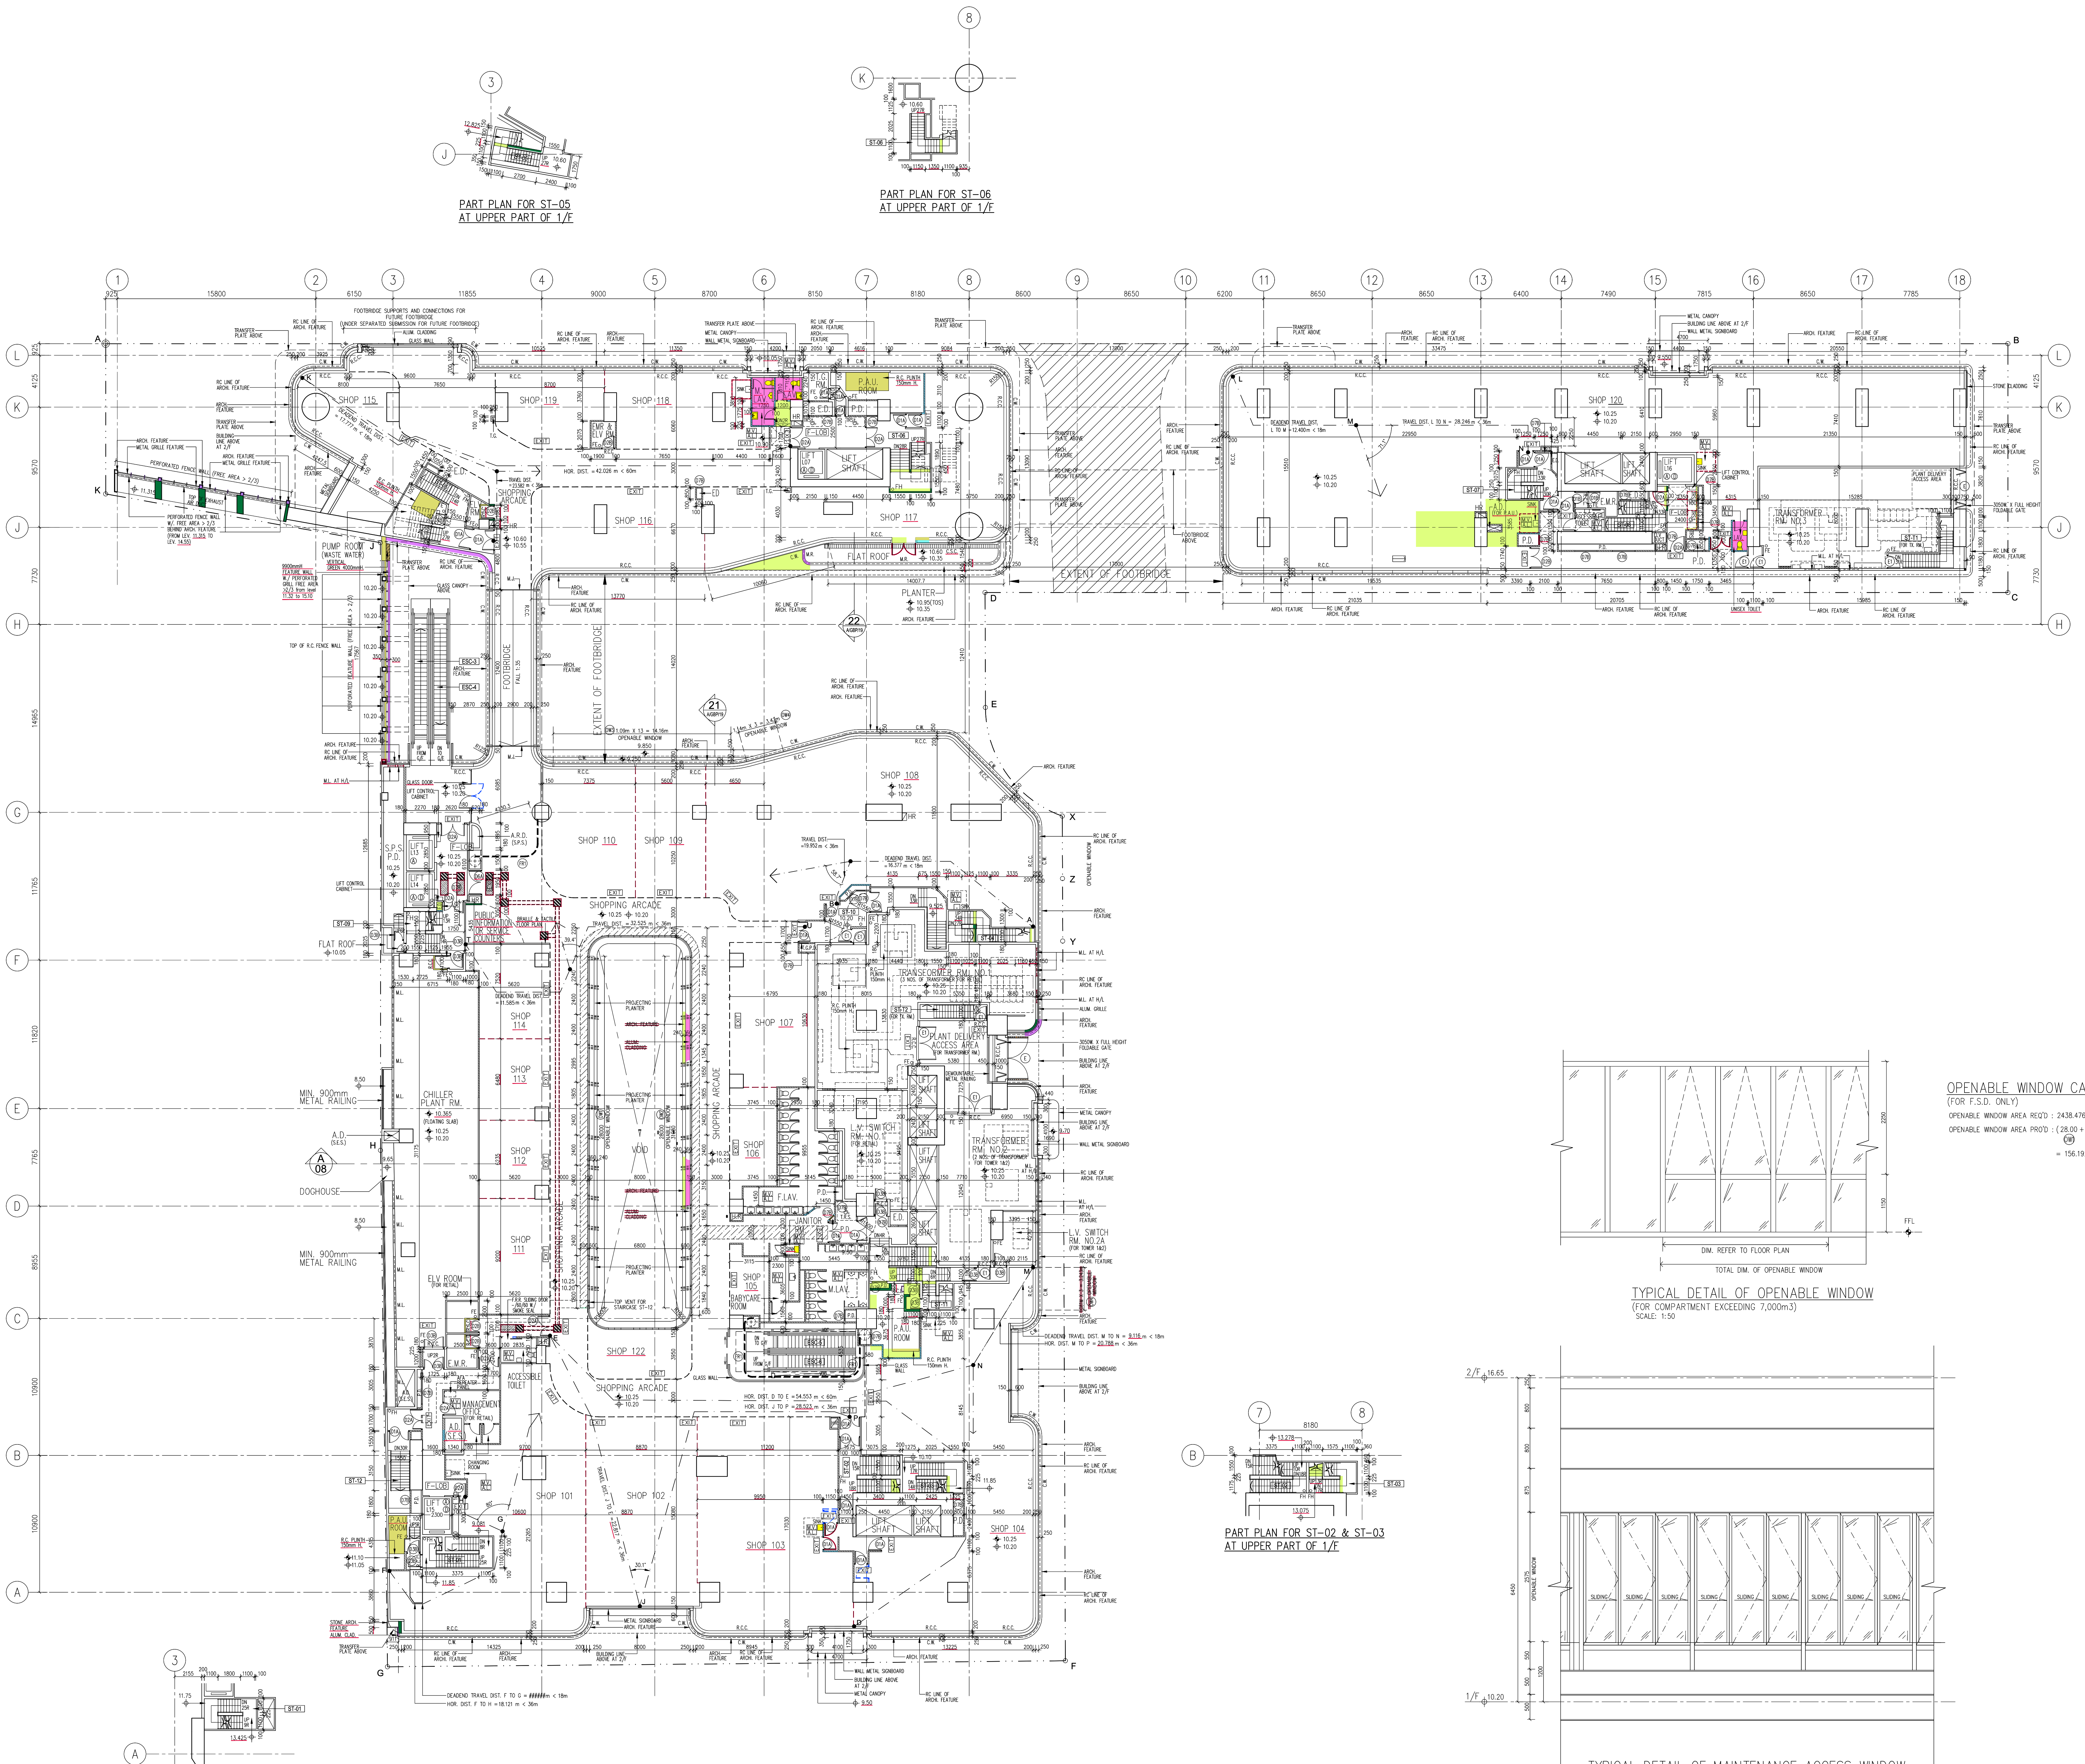
SHOP 115
SHOP 119
SHOP 118
SHOP 116
SHOP 117
SHOP 120
SHOP 108
SHOP 110
SHOP 109
SHOP 107
SHOP 106
SHOP 105
SHOP 114
SHOP 113
SHOP 112
SHOP 111
SHOP 122
SHOP 101
SHOP 102
SHOP 103
SHOP 104
SHOPPING ARCADE
PUMP ROOM (WASTE WATER)
FLAT ROOF
PLANTER
EXTENT OF FOOTBRIDGE
CHILLER PLANT RM.
DOGHOUSE
MIN. 900mm METAL RAILING
ELV ROOM
TRANSFORMER RM. NO.1
TRANSFORMER RM. NO.2
TRANSFORMER RM. NO.3
L.V. SWITCH RM. NO.2A
LIFT SHAFT
VOID
OPENABLE WINDOW
OW1
OW2
OW3
OW4
1
2
3
4
5
6
7
8
9
10
11
12
13
14
15
16
17
18
L
K
J
H
G
F
E
D
C
B
A
TYPICAL DETAIL OF OPENABLE WINDOW
DIM. REFER TO FLOOR PLAN
TOTAL DIM. OF OPENABLE WINDOW
FFL
2250
1150
16.65
10.20
SLIDING

PART PLAN FOR ST-05
AT UPPER PART OF 1/F

PART PLAN FOR ST-06
AT UPPER PART OF 1/F

PART PLAN FOR ST-02 & ST-03
AT UPPER PART OF 1/F

PART PLAN FOR ST-02
AT UPPER PART OF 1/F

TYPICAL DETAIL OF OPENABLE WINDOW
(FOR COMPARTMENT EXCEEDING 7,000m3)
SCALE: 1:50

TYPICAL DETAIL OF MAINTENANCE ACCESS WINDOW
ABOVE PROJECTING PLANTER
SCALE: 1:50

OPENABLE WINDOW CALCULATION

(FOR F.S.D. ONLY)

OPENABLE WINDOW AREA REQ'D : $2438.476 \times 0.0625 = 152.405$ s.m.

OPENABLE WINDOW AREA PRO'D : $(\underset{OW1}{28.00} + \underset{OW2}{28.00}) \times 2.575 \times 0.85 + (\underset{OW3}{14.16} + \underset{OW4}{3.42}) \times 2.25 \times 0.85$

$= 156.192$ s.m. > 152.405 s.m. (REQUIRED)

1ST FLOOR PLAN

LEGEND

- ▨ P – PINK HATCHED BLACK (UNDER LEASE)
- ▨ TACTILE POSITIONAL TILE/BLOCKS
- - - - TACTILE DIRECTIONAL TILE/BLOCKS
- ▨ TACTILE WARNING TILE/BLOCKS

B.D. Ref : BD 2/4024/21

BIM Ref : - --

F.S.D. Ref : - --

D.L.O. Ref : - --

Rev.	Description	Drawn	Checked	Approved	Date
-	1st Submission	WY	AW	AL	07/2022
A	2nd Submission	WY	AW	AL	11/2022
B	1st Amendment	TWM	AW	AL	04/2023
C	2nd Amendment	TWM	AW	AL	12/2023
D	3rd Amendment	TWM	AW	AL	04/2024
D	3rd Amendment (Re-submission)	TWM	AW	AL	05/2024
E	5th Amendment	TWM	AW	AL	12/2024
E	5th Amendment (Re-submission)	TWM	AW	AL	02/2025
F	8th Amendment	TWM	AW	AL	05/2025
G	9th Amendment	TWM	AW	AL	08/2025
G	9th Amendment (Re-submission)	TWM	AW	AL	10/2025
H	10th Amendment	TWM	AW	AL	12/2025
I	11th Amendment	TWM	AW	AL	02/2026

Type II works
The works shown on these plans are Type II works (Building Amendment) in respect of which consent is applied for the purpose of Fast Track consent application under regulation 33 of the Building (Administration) Regulations.

RONALD LU & PARTNERS
呂元祥建築師事務所

Project Title :
PROPOSED DEVELOPMENT
AT BAILEY STREET
& WING KWONG STREET
TO KWA WAN, KOWLOON

Drawing Title :
1ST FLOOR PLAN

Drawn By	TWM	Date	08/2025
Checked By	AW	Date	08/2025
Approved By	AL	Date	08/2025
Project No.	21163KL	Issue Date	08/2025

File Path :
U:\Studio_B\Proj_Data\2021\21163KL_Bailey Street & Wing Kwong Street\DRAWING\SUB\BD\GBP_13 (Final Amendment)_Hand Amend\PLOT\A_GBP_07.dwg

Scale 1:200 By CAD

Drawing Number : A/GBP/07
Revision Number : I

Drawing Purpose
Buildings Department
Amended Plan

Digitally signed by
LEUNG Kit Man Andy
AP(A) 80/85
16 March 2026

Received on
16 March 2026

Plan Approved
(Digitally Signed)
TSOI Lap-san, Lapson
Senior Building Surveyor
for BUILDING AUTHORITY
17 March 2026

Note: This plan has been processed on a curtailed check basis under the centralized processing system as promulgated in PNAP ADM-19. The duties of the authorized person, registered structural engineer and/or registered geotechnical engineer concerned as specified under section 4(3)(b) and the provision of section 14(2)(c) of the Buildings Ordinance are of particular relevance in this regard.

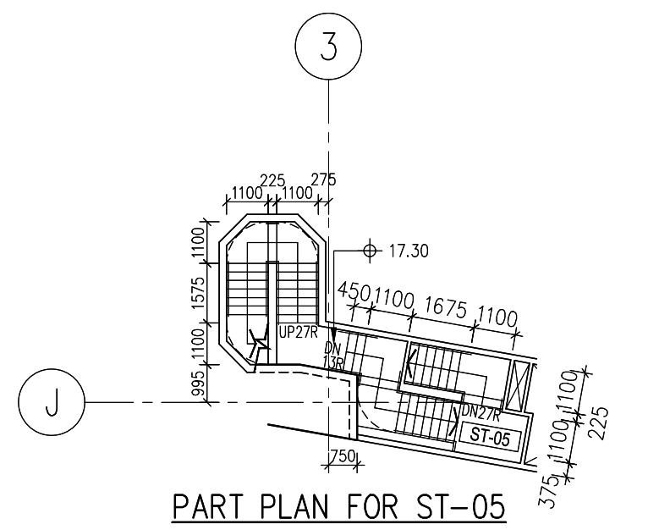
PART PLAN FOR ST-05
AT UPPER PART OF 2/F

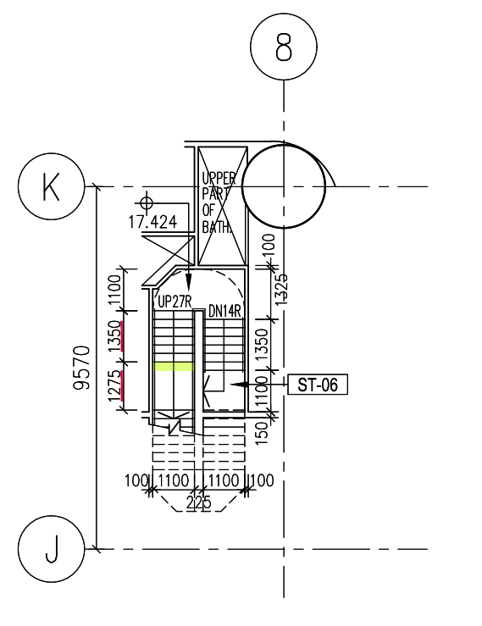
PART PLAN FOR ST-06
AT LEVEL +17.424

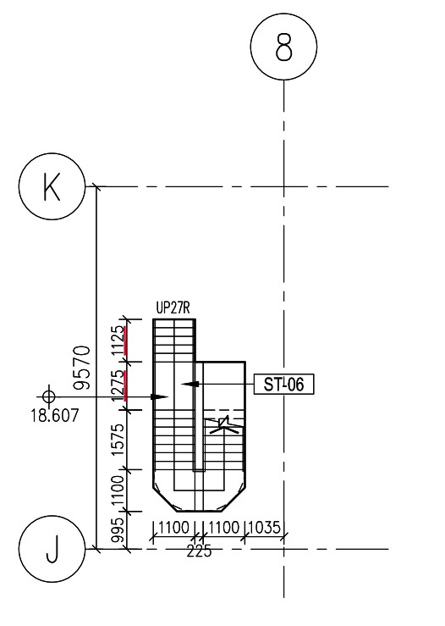
PART PLAN FOR ST-06
AT UPPER PART OF 2/F

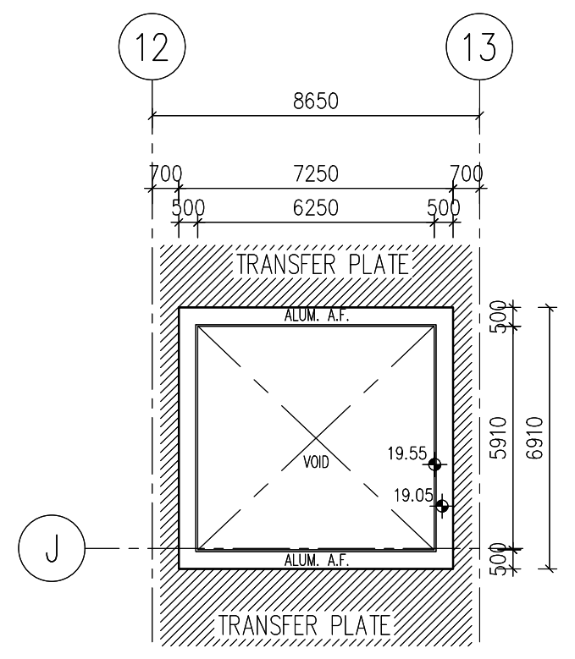

TRANSFER PLATE
TRANSFER PLATE

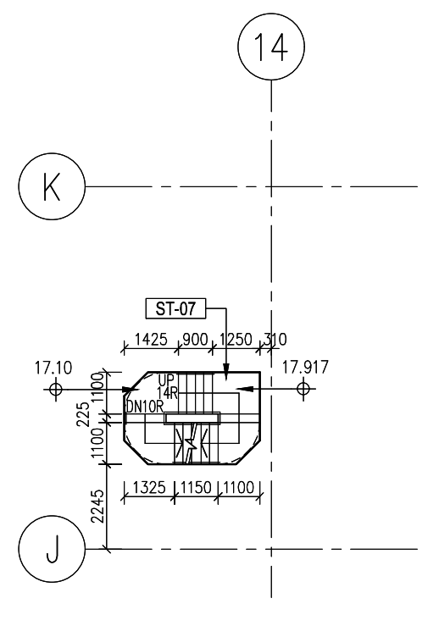
PART PLAN FOR ST-07
AT LEVEL +17.10

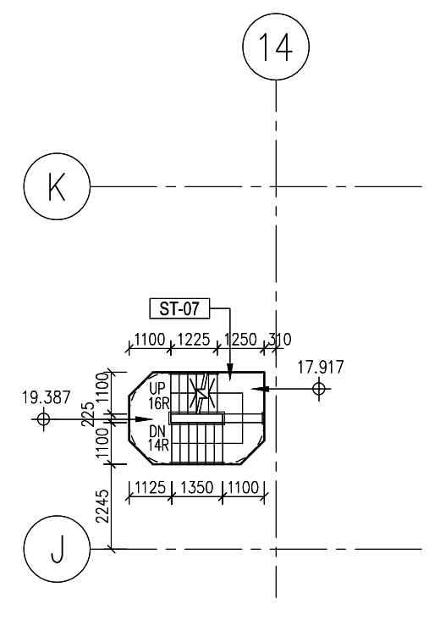
PART PLAN FOR ST-07
AT UPPER PART OF 2/F

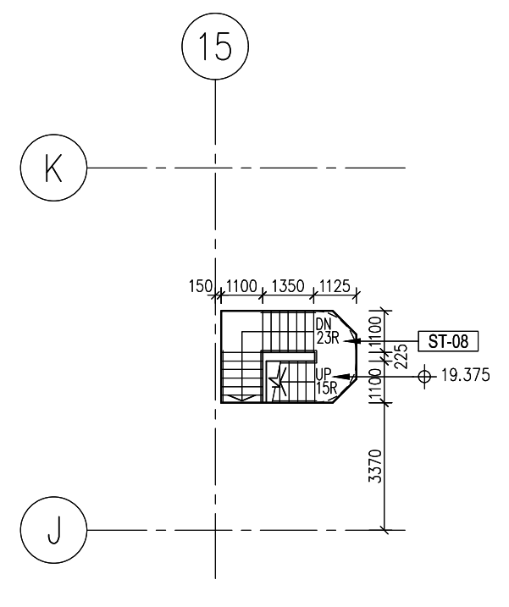
PART PLAN FOR ST-08
AT UPPER PART OF 2/F

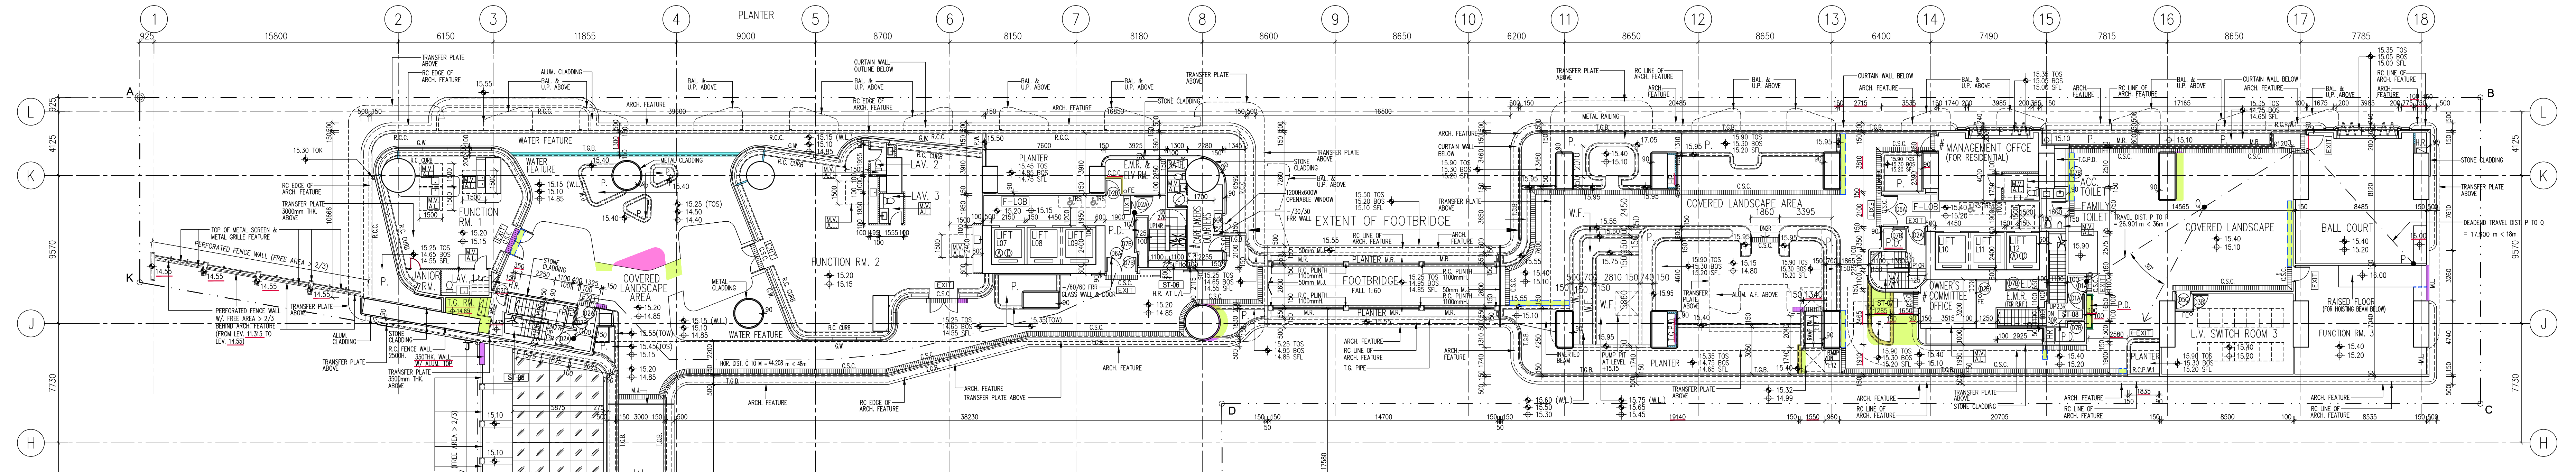
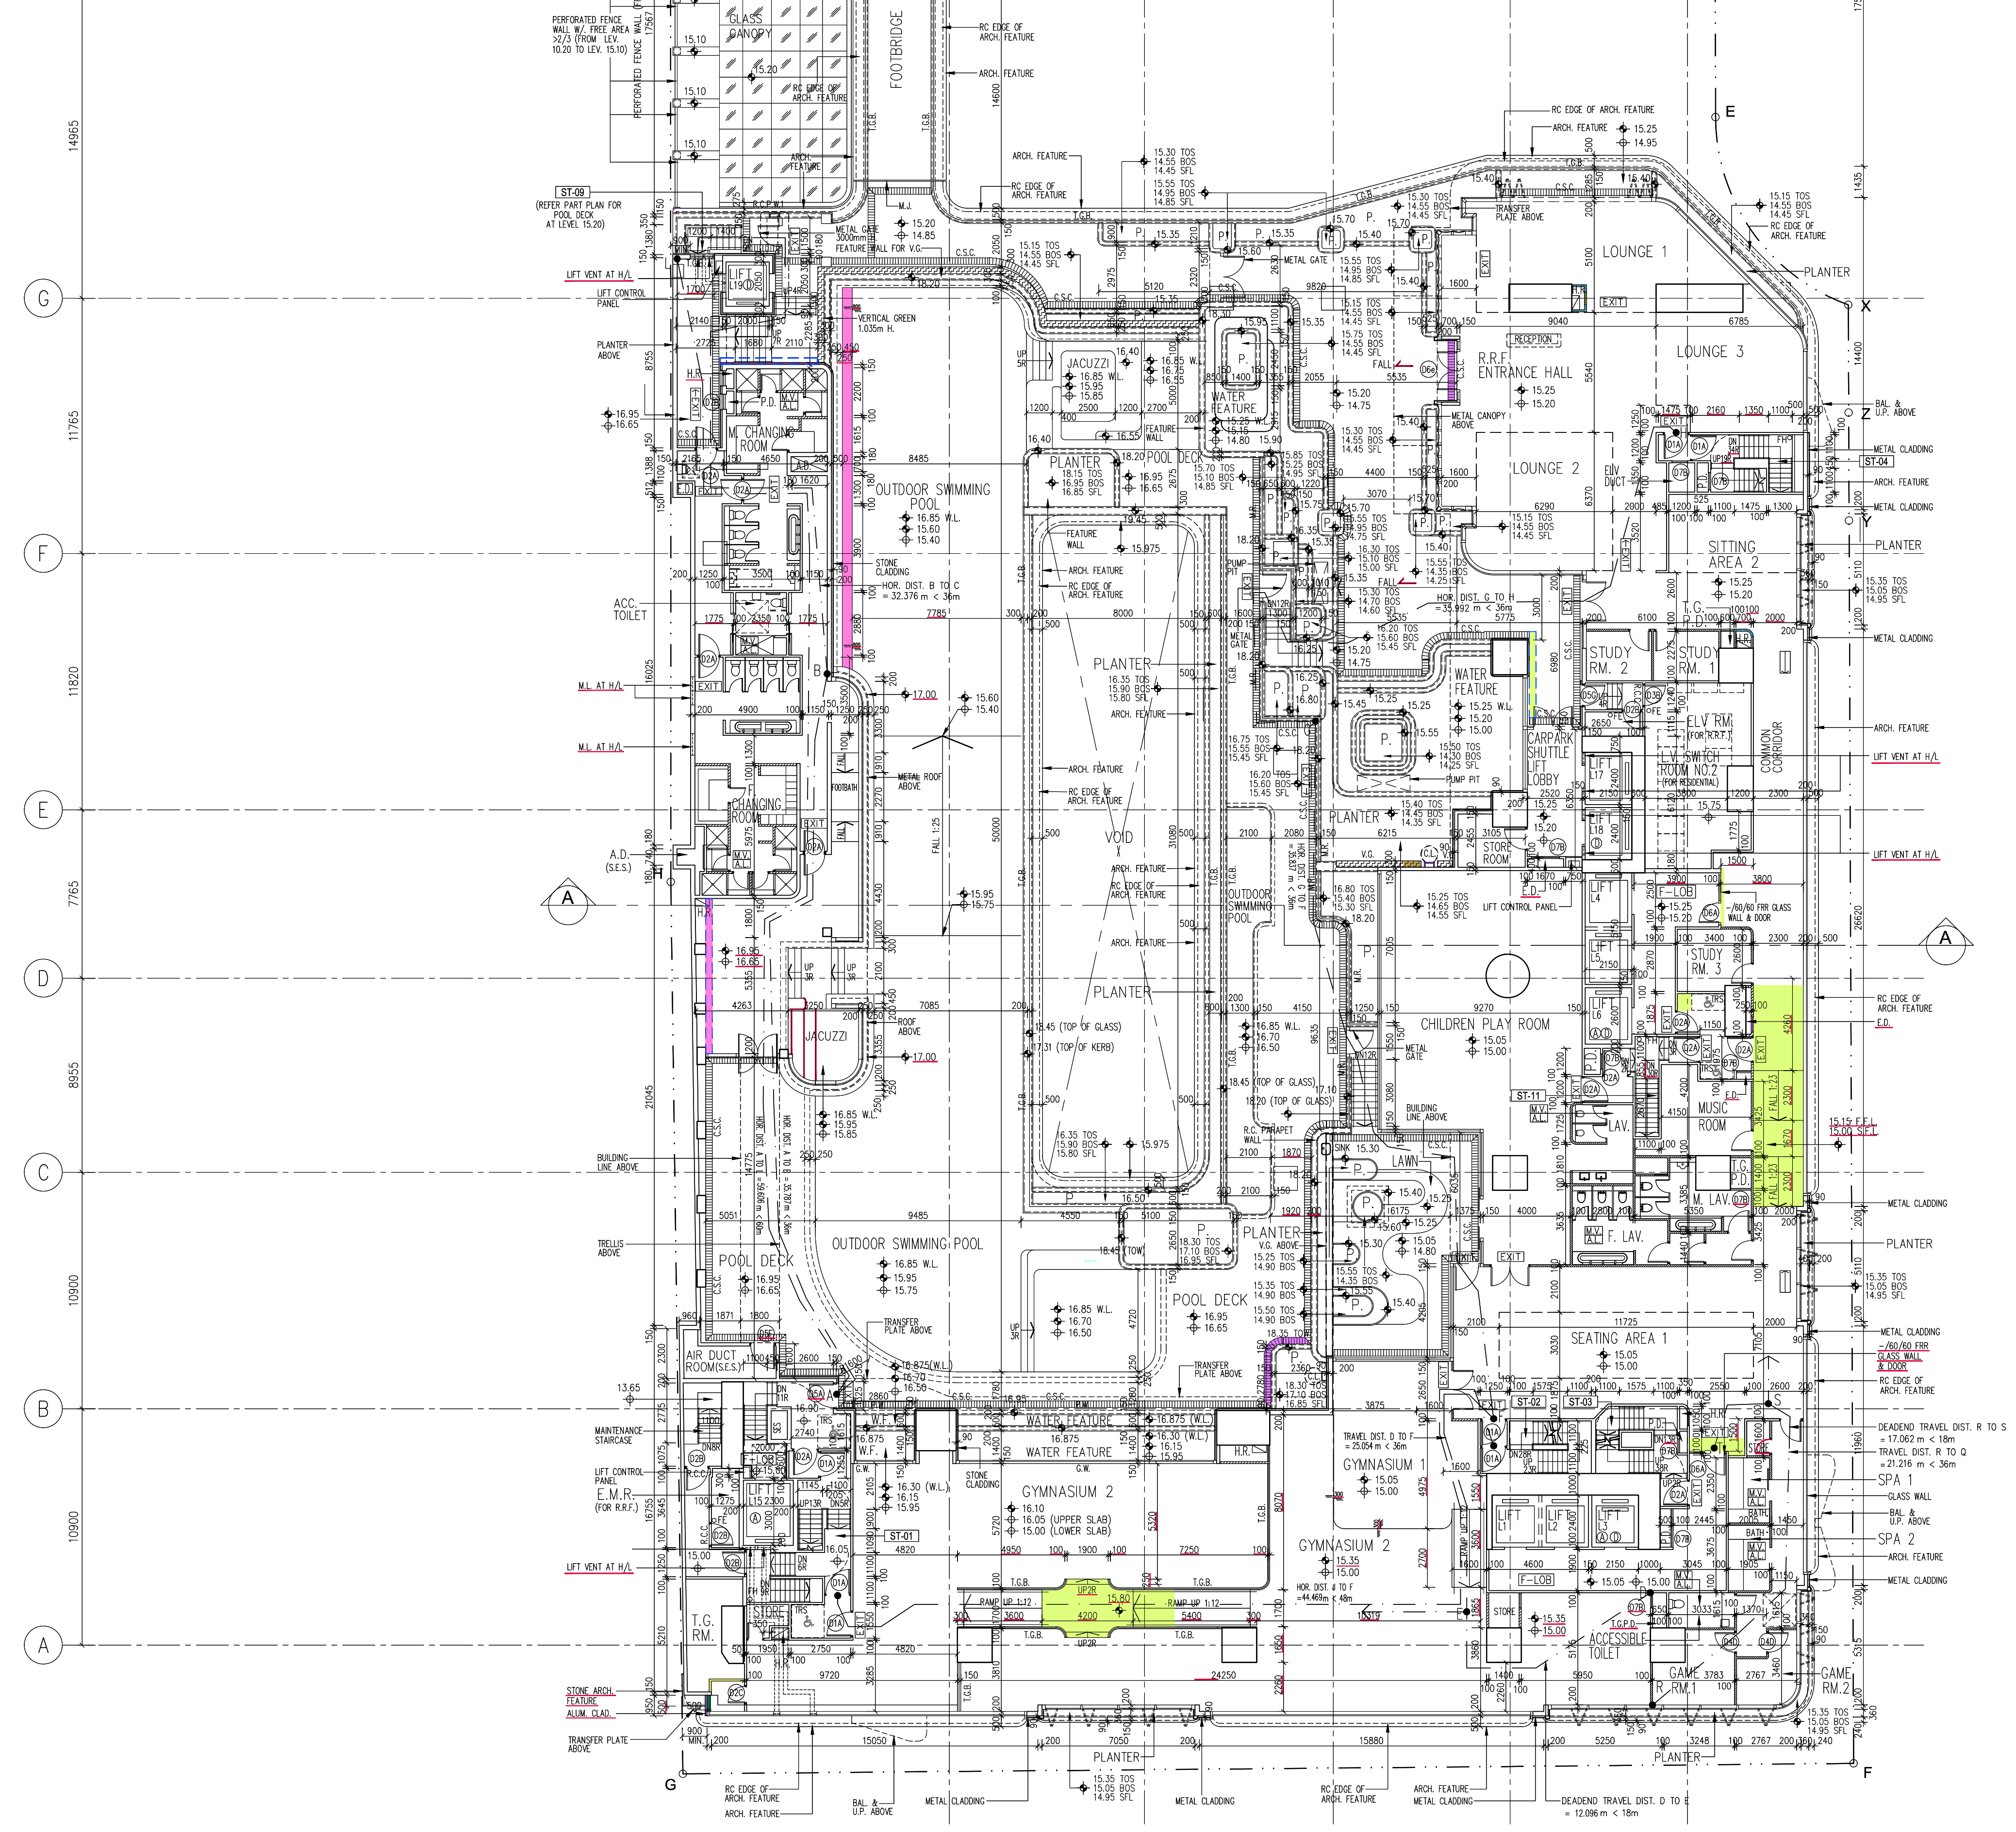

FUNCTION RM. 1
FUNCTION RM. 2
COVERED LANDSCAPE AREA
EXTENT OF FOOTBRIDGE
FOOTBRIDGE
MANAGEMENT OFFICE (FOR RESIDENTIAL)
BALL COURT
FUNCTION RM. 3
L.V. SWITCH ROOM 3
OUTDOOR SWIMMING POOL
LOUNGE 1
LOUNGE 2
LOUNGE 3
R.R.F. ENTRANCE HALL
SITTING AREA 2
STUDY RM. 1
STUDY RM. 2
CHILDREN PLAY ROOM
MUSIC ROOM
POOL DECK
SEATING AREA 1
GYMNASIUM 1
GYMNASIUM 2
SPA 1
SPA 2
ACCESSIBLE TOILET
GAME RM. 2
PLANTER

2ND FLOOR PLAN

LEGEND

▨ COVERED LANDSCAPED AREA

NOTE :

ROOM SHALL BE DESIGNATED AS "COMMON AREA"
IN DEED OF MUTUAL COVENANT "DMC"

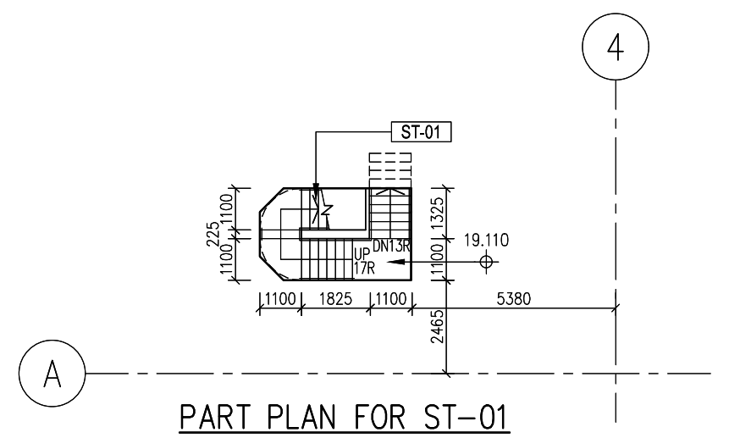
PART PLAN FOR ST-01
AT UPPER PART OF 2/F

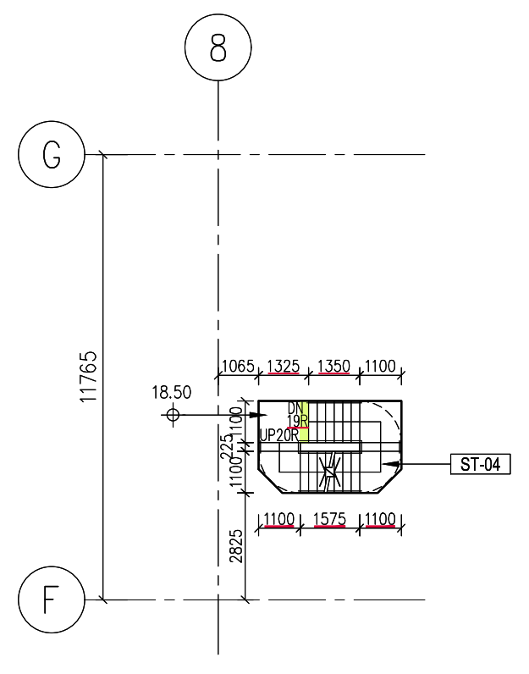
PART PLAN FOR ST-04
AT UPPER PART OF 2/F

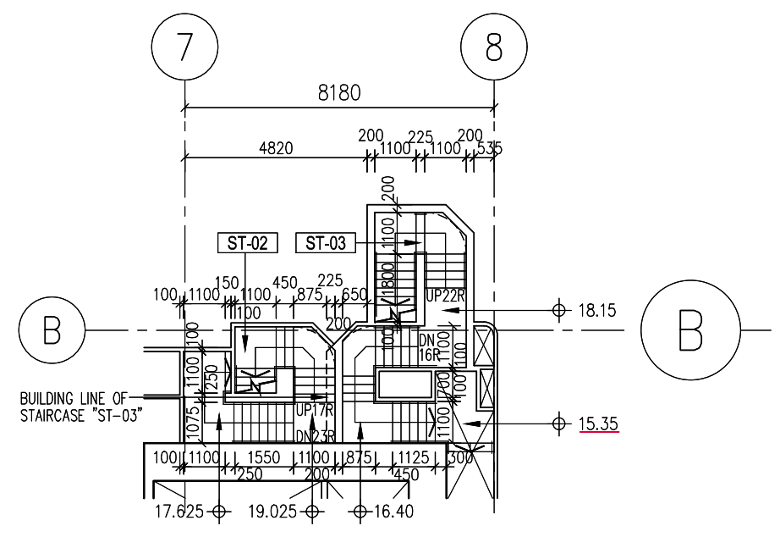
PART PLAN FOR ST-02 & ST-03
AT UPPER PART OF 2/F

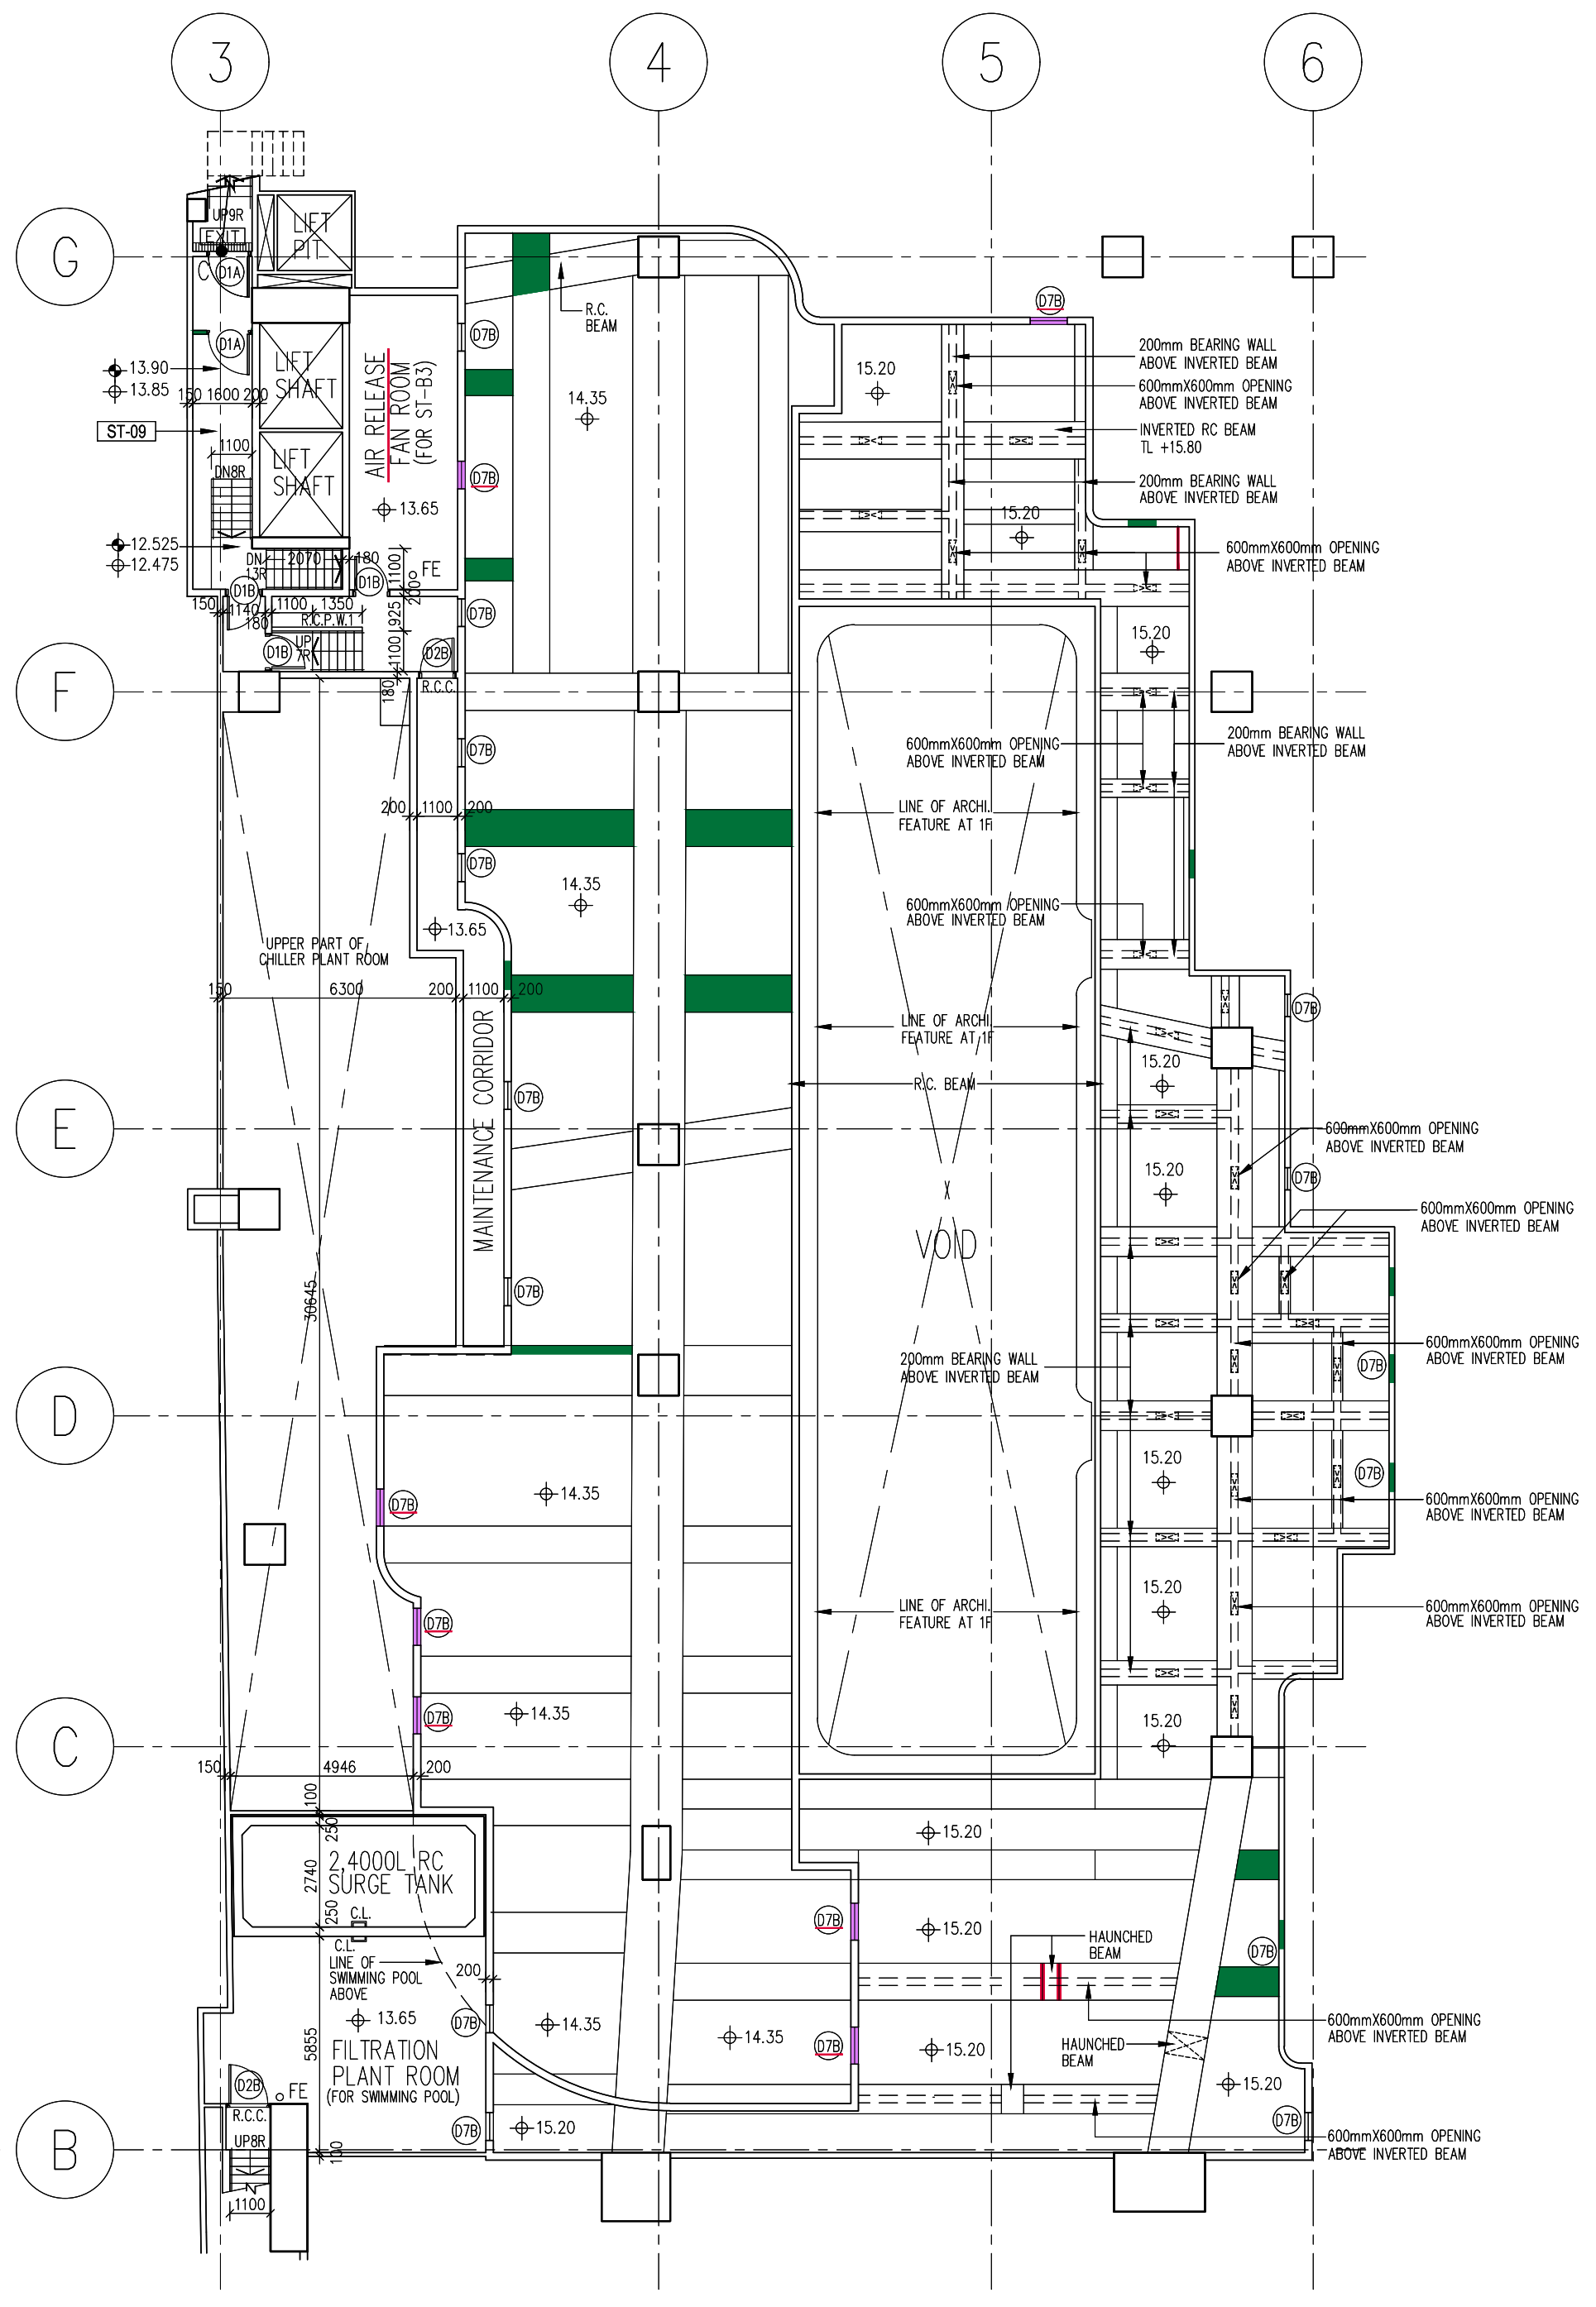
PART PLAN FOR POOL DECK
AT LEVEL 15.20

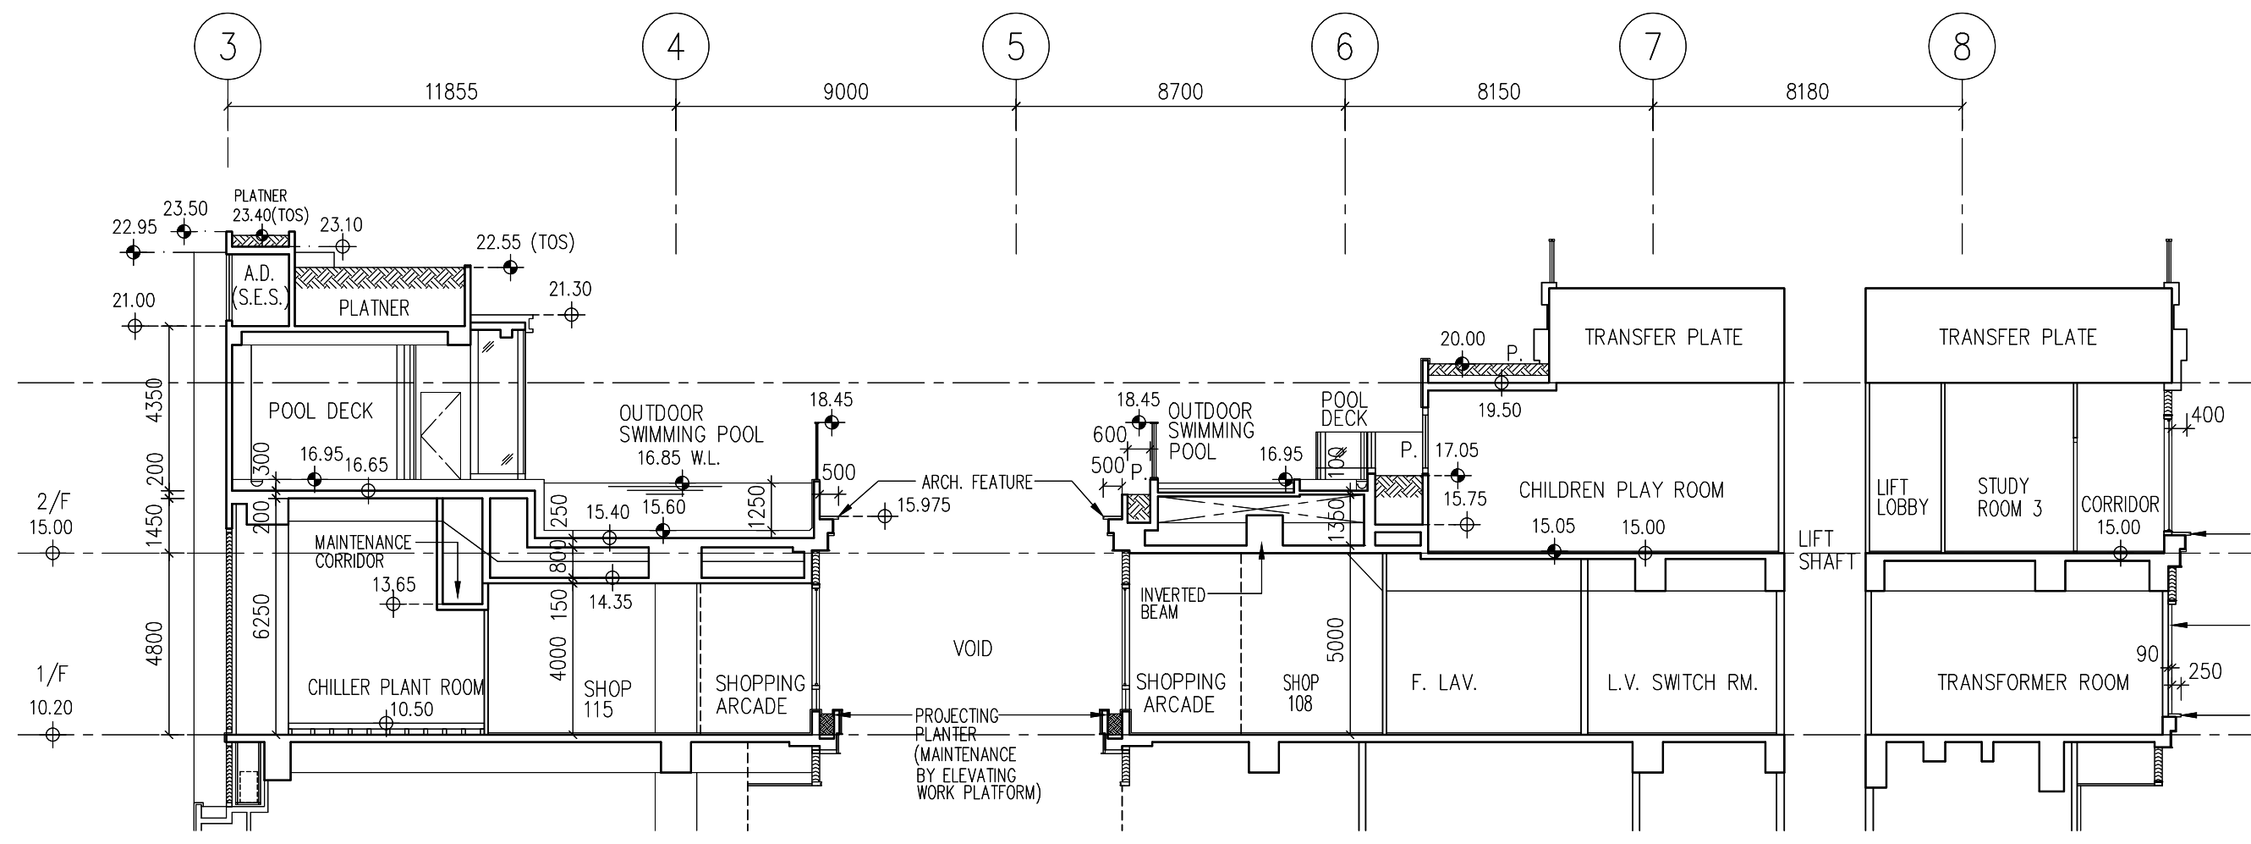
PART SECTION A

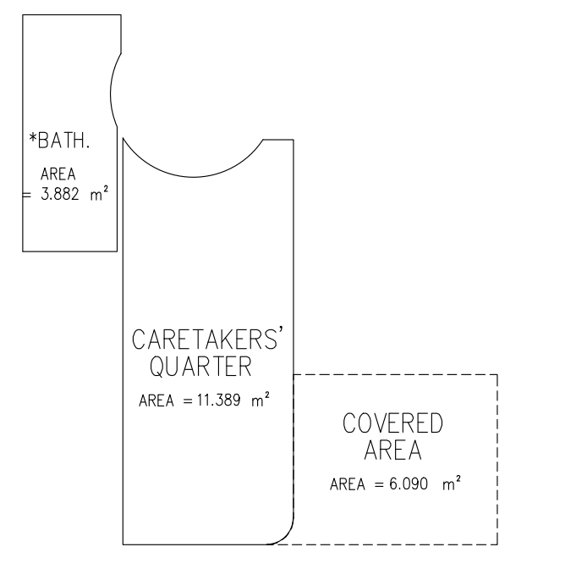

*BATH.
AREA = 3.882 m²
CARETAKERS' QUARTER
AREA = 11.389 m²
COVERED AREA
AREA = 6.090 m²

CARETAKERS' QUARTER AREA

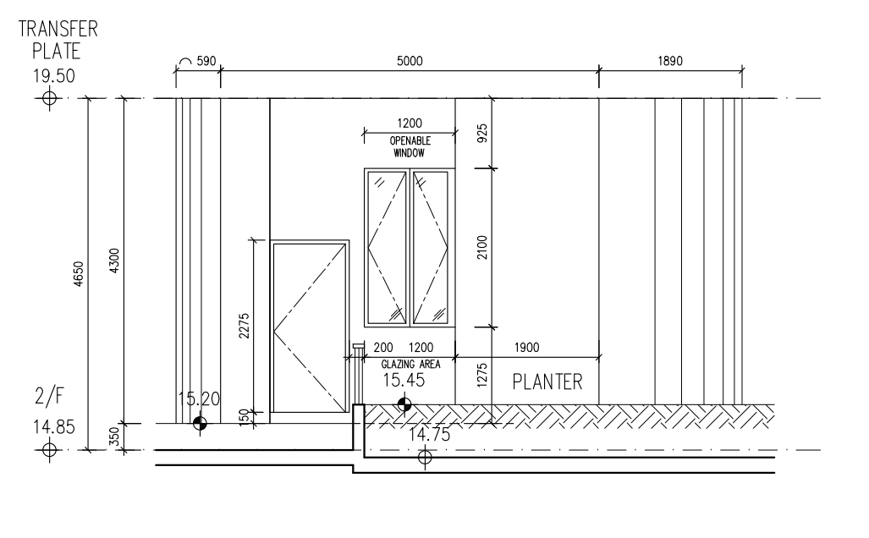

TRANSFER PLATE
19.50
2/F
14.85
590
5000
1890
1200
OPENABLE WINDOW
925
2100
4650
4300
2275
200
1200
1900
GLAZING AREA
15.45
15.20
PLANTER
1275
150
350
14.75

FLOOR AREA = 11.389 s.m. + 6.090 s.m.
= 17.479 s.m.

WINDOW AREA REQ'D = 17.479 / 10 = 1.748 s.m.
WINDOW AREA PROV'D = 1.200 x 2.100 x 0.70
= 1.764 s.m. > 1.748 s.m. (REQUIRED)

OPENABLE WINDOW AREA REQ'D = 17.479 /16 + 3.882 / 10 = 1.481 s.m.
OPENABLE WINDOW AREA PROV'D = 1.200 x 2.100 x 0.70
= 1.764 s.m. >1.481 s.m. (REQUIRED)

B.D. Ref : BD 2/4024/21
BIM Ref : - --
F.S.D. Ref : - --
D.L.O. Ref : - --

Rev.	Description	Drawn	Checked	Approved	Date
-	1st Submission	WY	AW	AL	07/2022
A	2nd Submission	WY	AW	AL	11/2022
B	1st Amendment	TWM	AW	AL	04/2023
C	2nd Amendment	TWM	AW	AL	12/2023
D	3rd Amendment	TWM	AW	AL	04/2024
D	3rd Amendment (Re-submission)	TWM	AW	AL	05/2024
E	5th Amendment	TWM	AW	AL	12/2024
E	5th Amendment (Re-submission)	TWM	AW	AL	02/2025
F	8th Amendment	TWM	AW	AL	05/2025
G	9th Amendment	TWM	AW	AL	08/2025
G	9th Amendment (Re-submission)	TWM	AW	AL	10/2025
H	10th Amendment	TWM	AW	AL	12/2025
I	11th Amendment	TWM	AW	AL	02/2026

Type II works
The works shown on these plans are Type II works (Building Amendment) in respect of which consent is applied for the purpose of Fast Track consent application under regulation 33 of the Building (Administration) Regulations.

RONALD LU & PARTNERS
呂 元 祥 建 築 師 事 務 所

Project Title :
PROPOSED DEVELOPMENT
AT BAILEY STREET
& WING KWONG STREET
TO KWA WAN, KOWLOON

Drawing Title :
2ND FLOOR PLAN

Drawn By	TWM	Date	08/2025
Checked By	AW	Date	08/2025
Approved By	AL	Date	08/2025
Project No.	21163KL	Issue Date	08/2025

File Path :
U:\Studio_B\Proj_Data\2021\21163KL_Bailey Street & Wing Kwong Street\DRAWING\SUB\BD\GBP_13 (Final Amendment)_Hand Amend\PLOT\A_GBP_08.dwg

Scale 1:200 By CAD

Drawing Number : A/GBP/08
Revision Number : I

Drawing Purpose
Buildings Department
Amended Plan

Digitally signed by
LEUNG Kit Man Andy
AP(A) 80/85
16 March 2026

Received on
16 March 2026

Plan Approved
(Digitally Signed)
TSOI Lap-san, Lapson
Senior Building Surveyor
for BUILDING AUTHORITY
17 March 2026

Note: This plan has been processed on a curtailed check basis under the centralized processing system as promulgated in PNAP ADM-19. The duties of the authorized person, registered structural engineer and/or registered geotechnical engineer concerned as specified under section 4(3)(b) and the provision of section 14(2)(c) of the Buildings Ordinance are of particular relevance in this regard.

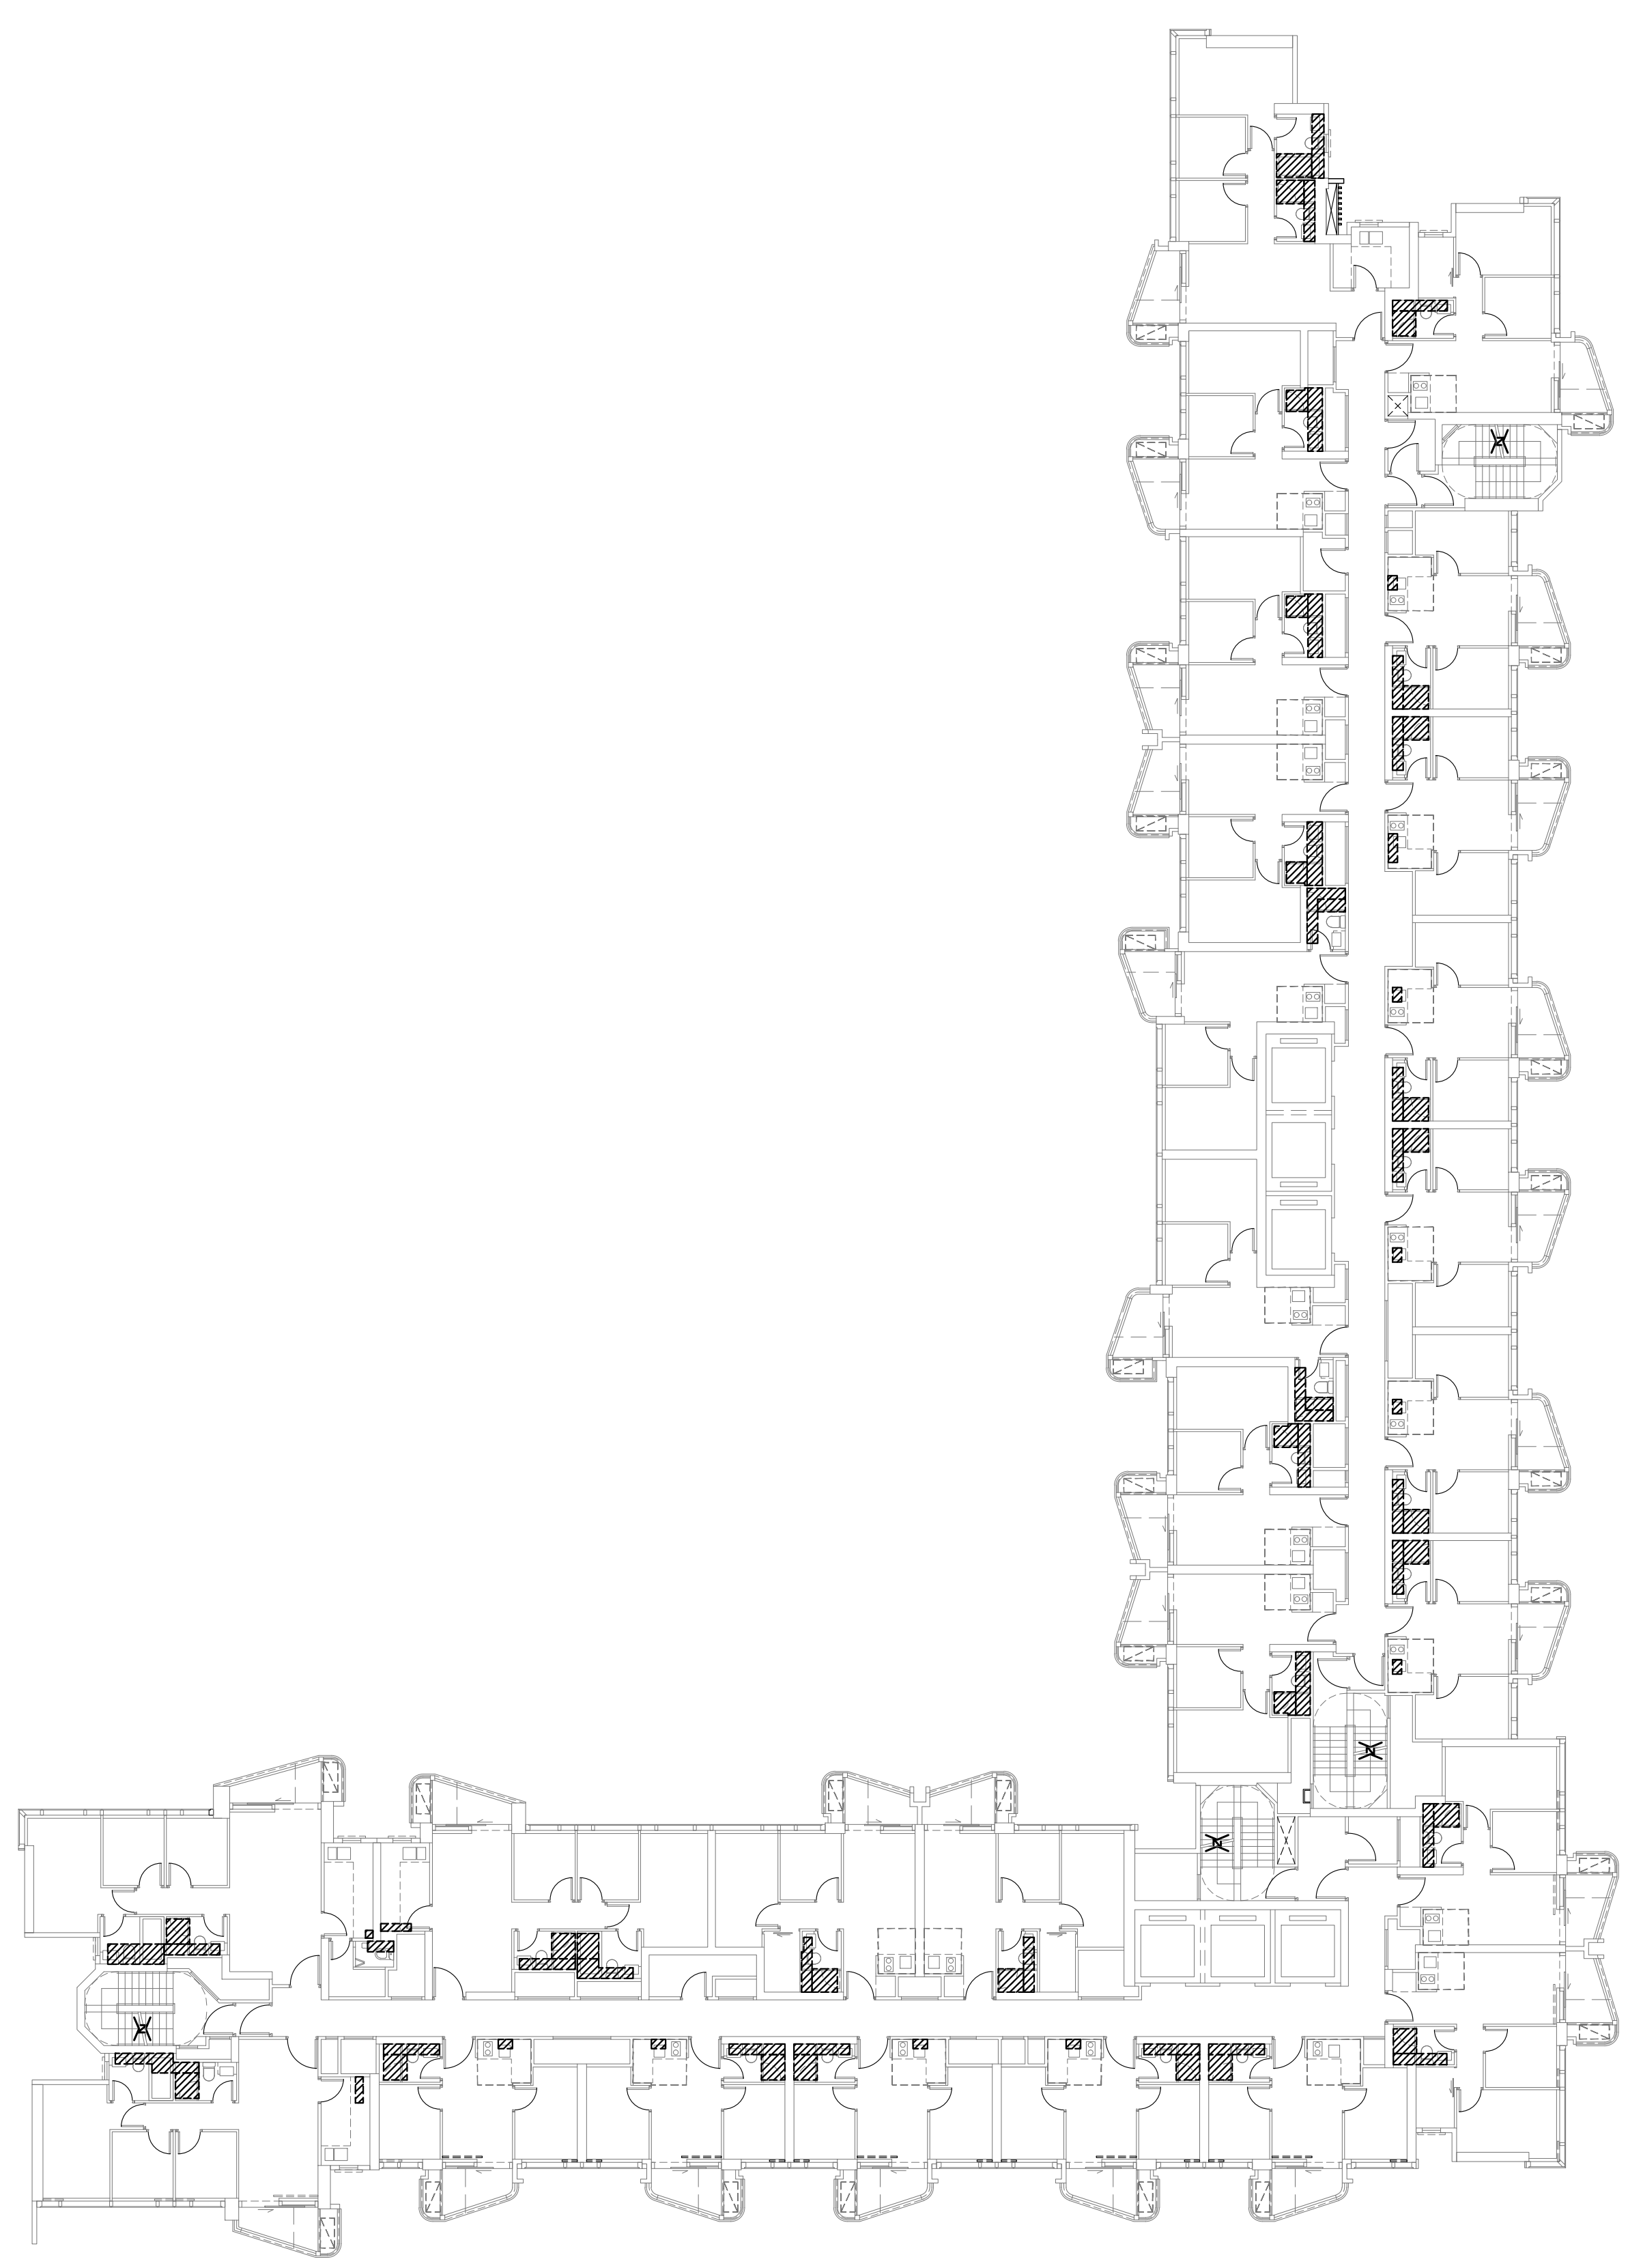

DIAGRAM OF SUNKEN SLAB EXTENT (5th TO 30th FLOOR)

SCALE 1:200

LEGEND:

▨ SUNKEN SLAB

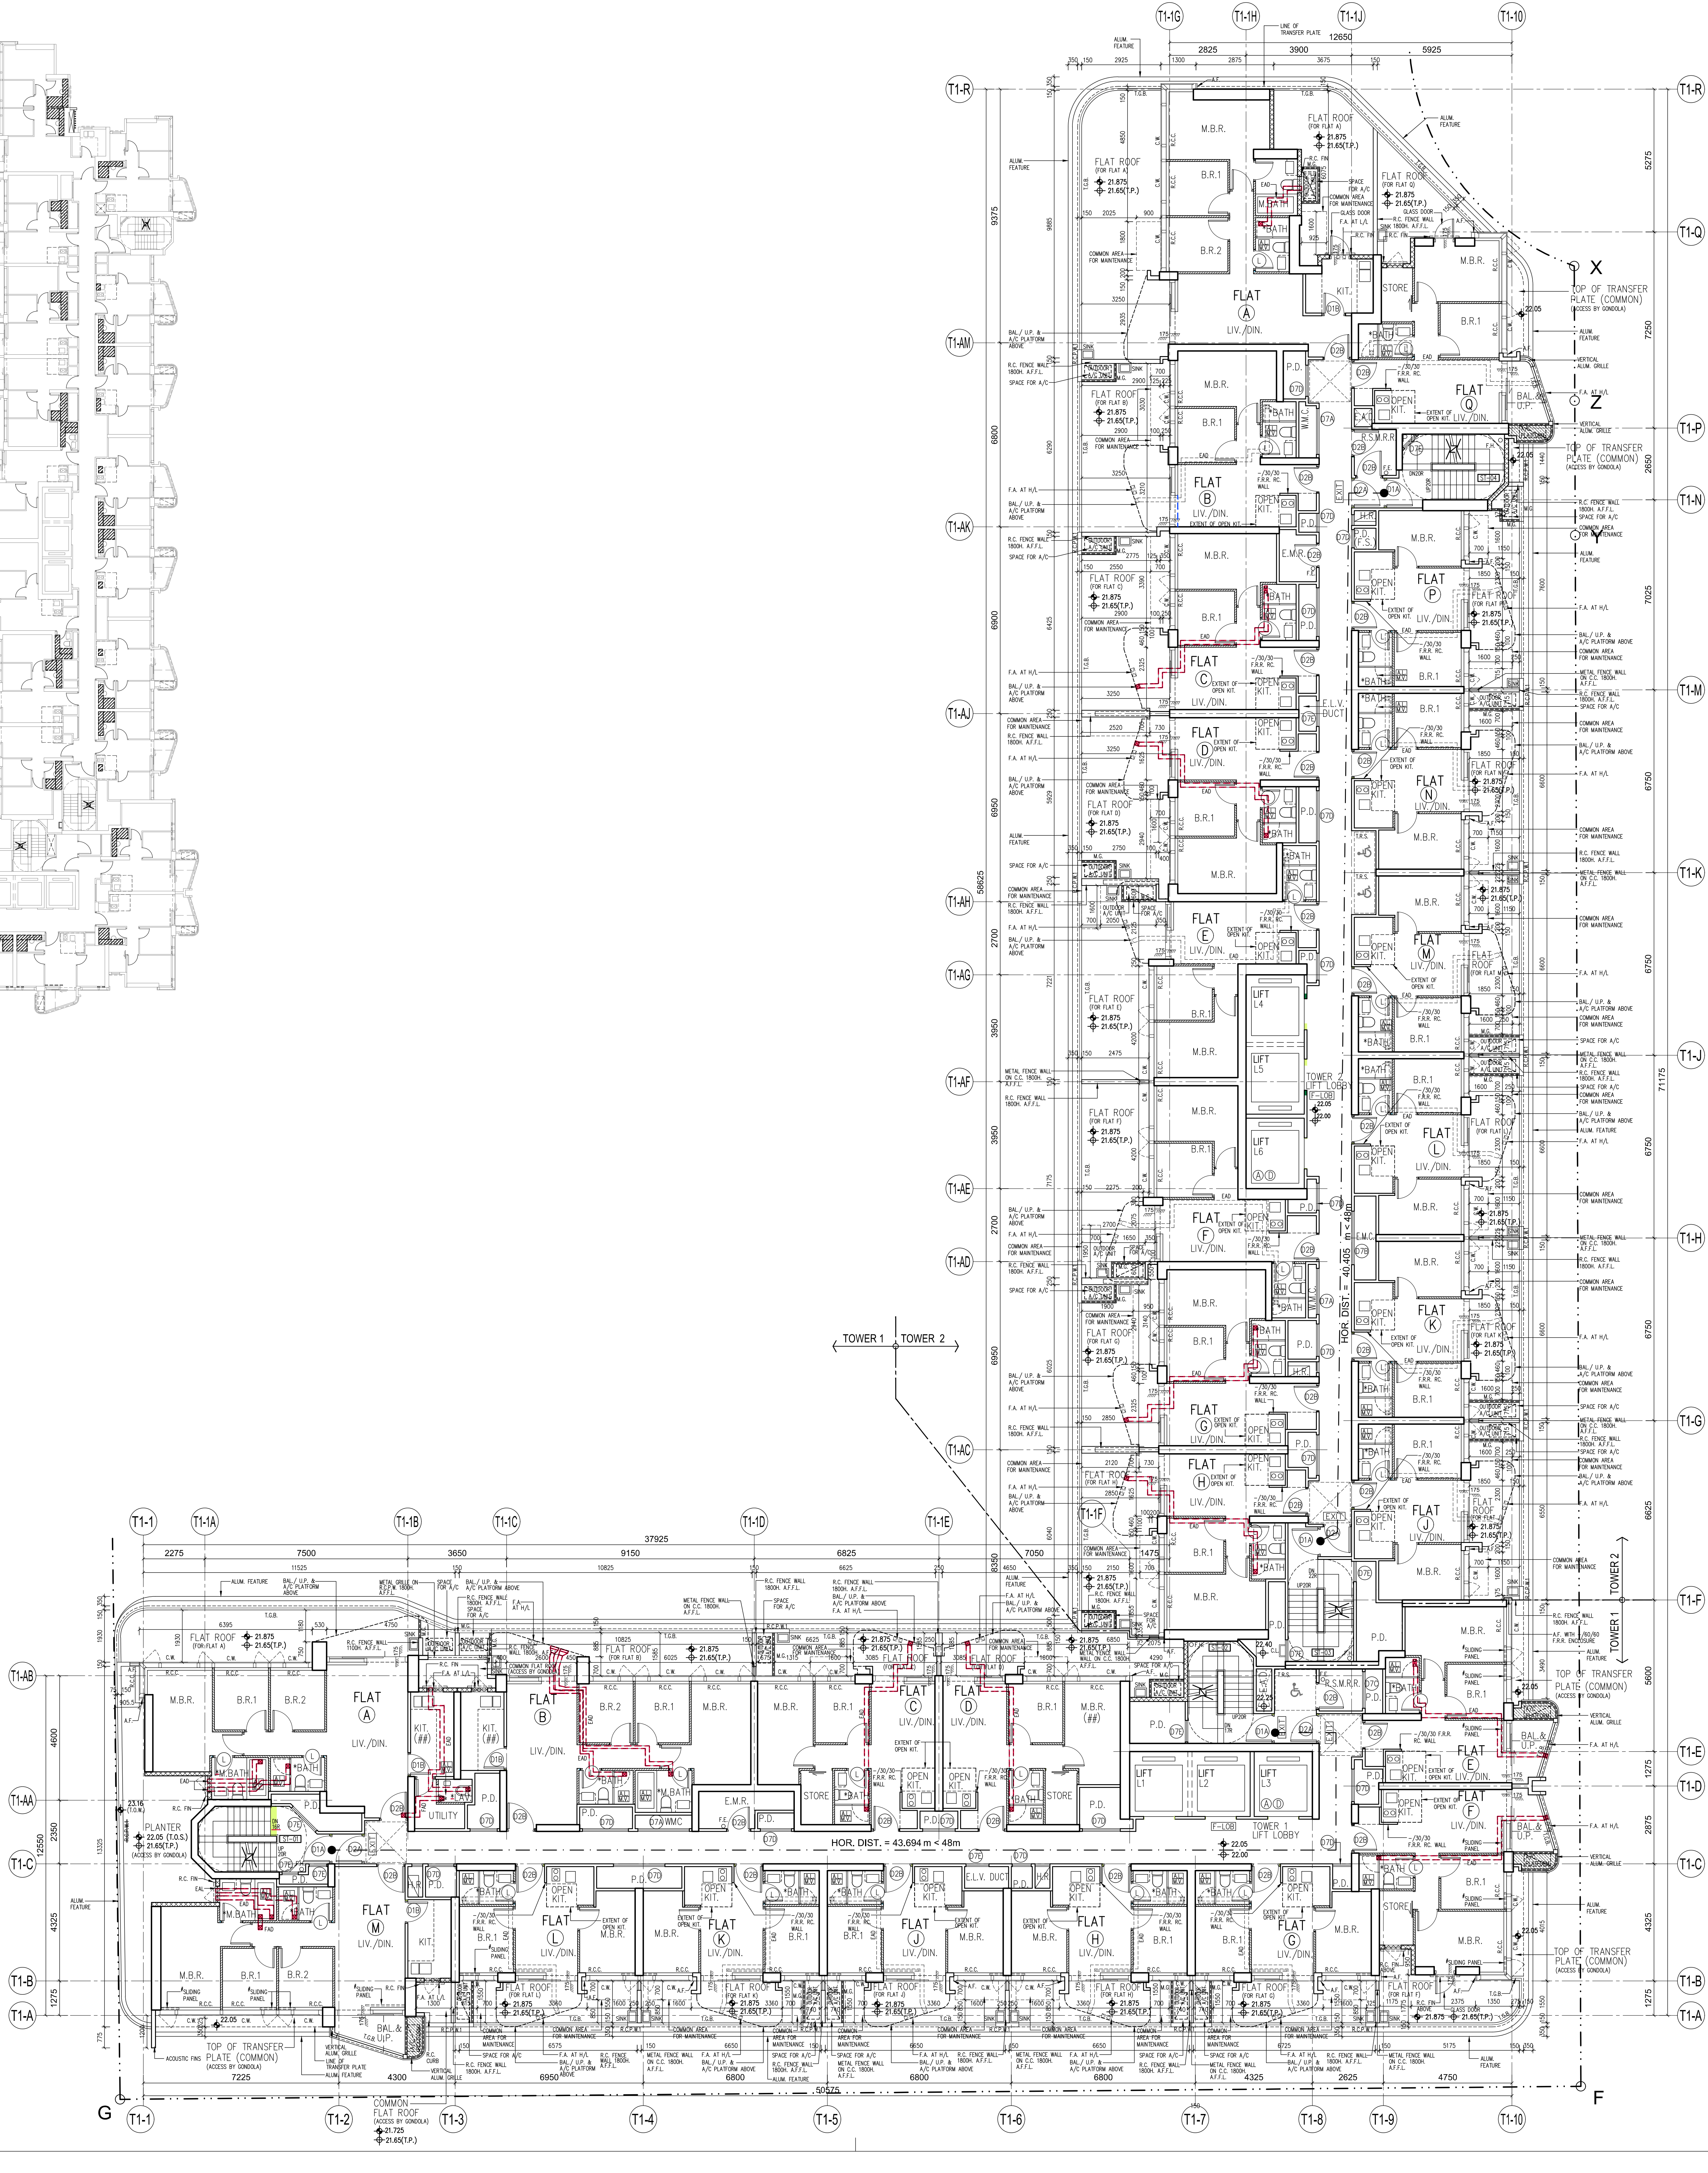
TOWER 1
TOWER 2
FLAT A
FLAT B
FLAT C
FLAT D
FLAT E
FLAT F
FLAT G
FLAT H
FLAT J
FLAT K
FLAT L
FLAT M
FLAT N
FLAT P
FLAT Q
M.B.R.
B.R.1
B.R.2
LIV./DIN.
KIT.
BATH
FLAT ROOF
TOWER 1 LIFT LOBBY
TOWER 2 LIFT LOBBY
LIFT L1
LIFT L2
LIFT L3
LIFT L4
LIFT L5
LIFT L6
HOR. DIST. = 43.694m < 48m
TOP OF TRANSFER PLATE (COMMON)
COMMON FLAT ROOF
PLANTER
UTILITY
STORE
E.M.R.
E.L.V. DUCT
37925
71175
X
Y
Z
G
F

3RD FLOOR PLAN – TOWER 1 & TOWER 2

NOTE:

1. MECHANICAL VENTILATION AND ARTIFICIAL LIGHTING WILL BE PROVIDED AT THE BATHROOM/ LAVATORY MARKED WITH " * " FOR OMISSION OF NATURAL LIGHTING AND VENTILATION.
2. ALL DIMENSION ARE SAME AS 5/F – 30/F, EXCEPT OTHERWISE NOTED.
3. SLIDING PANEL TO BE PROVIDED AT WHICH MARKED WITH "#" (REFER TO SLIDING PANEL SCHEDULE DWG. NO. A/GBP/11)
4. LIGHTING AND VENTILATION PROVISION TO ADOPT PERFORMANCE–BASED APPROACH FOR THE ROOM MARKED WITH (##) (REFER DWG. NO. A/GBP/10, A/GBP/10.1)
5. 5 ACH MECHANICAL VENTILATION SHALL BE PROVIDED TO KITCHENS USING UVA METHOD.

LEGEND:

▩ NON–STRUCTURAL PREFABRICATE EXTERNAL WALL (THICKNESS MAX. 150mm)

⬚ COMMON AREA FOR MAINTENANCE

▨ A/C PLATFORM

B.D. Ref : BD 2/4024/21

BIM Ref : - --

F.S.D. Ref : - --

D.L.O. Ref : - --

Rev.	Description	Drawn	Checked	Approved	Date
-	1st Submission	WY	AW	AL	07/2022
A	2nd Submission	WY	AW	AL	11/2022
B	1st Amendment	TWM	AW	AL	04/2023
C	2nd Amendment	TWM	AW	AL	12/2023
D	3rd Amendment	TWM	AW	AL	04/2024
D	3rd Amendment (Re-submission)	TWM	AW	AL	05/2024
E	5th Amendment	TWM	AW	AL	12/2024
E	5th Amendment (Re-submission)	TWM	AW	AL	02/2025
F	6th Amendment	TWM	AW	AL	02/2025
G	8th Amendment	TWM	AW	AL	05/2025
H	9th Amendment	TWM	AW	AL	08/2025
H	9th Amendment (Re-submission)	TWM	AW	AL	10/2025
I	10th Amendment	TWM	AW	AL	12/2025
J	11th Amendment	TWM	AW	AL	02/2026

Type II works
The works shown on these plans are Type II works (Building Amendment) in respect of which consent is applied for the purpose of Fast Track consent application under regulation 33 of the Building (Administration) Regulations.

RONALD LU & PARTNERS

呂 元 祥 建 築 師 事 務 所

Project Title :
PROPOSED DEVELOPMENT
AT BAILEY STREET
& WING KWONG STREET
TO KWA WAN, KOWLOON

Drawing Title :
3RD FLOOR PLAN
FOR TOWER 1 & TOWER 2

Drawn By	TWM	Date	08/2025
Checked By	AW	Date	08/2025
Approved By	AL	Date	08/2025
Project No.	21163KL	Issue Date	08/2025

File Path :
U:\Studio_B\Proj_Data\2021\21163KL_Bailey Street & Wing Kwong Street\DRAWING\SUB\BD\GBP_13 (Final Amendment)_Hand Amend\PLOT\A_GBP_11.dwg

Scale 1:100 By CAD

Drawing Number : A/GBP/11
Revision Number : J

Drawing Purpose

Buildings Department
Amended Plan

Digitally signed by
LEUNG Kit Man Andy
AP(A) 80/85
16 March 2026

Received on
16 March 2026

Plan Approved
(Digitally Signed)
TSOI Lap-san, Lapson
Senior Building Surveyor
for BUILDING AUTHORITY
17 March 2026

Note: This plan has been processed on a curtailed check basis under the centralized processing system as promulgated in PNAP ADM-19. The duties of the authorized person, registered structural engineer and/or registered geotechnical engineer concerned as specified under section 4(3)(b) and the provision of section 14(2)(c) of the Buildings Ordinance are of particular relevance in this regard.

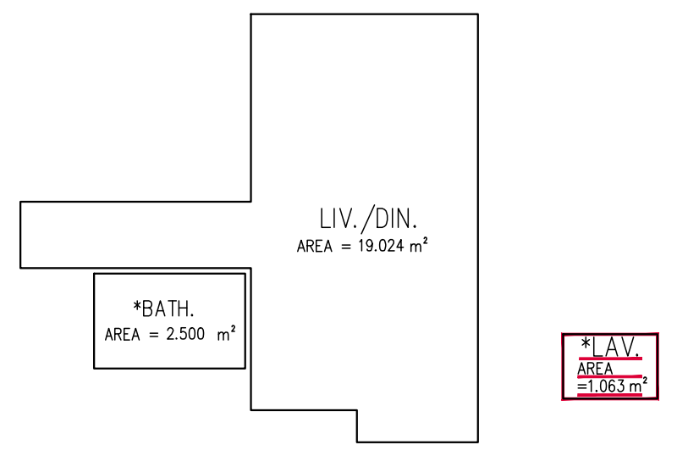
LIV./DIN.
AREA = 19.024 m²
*BATH.
AREA = 2.500 m²
*LAV.
AREA = 1.063 m²

3/F – 30/F T1-FLAT A (LIV./DIN., BATH. & LAV.) ROOM AREA

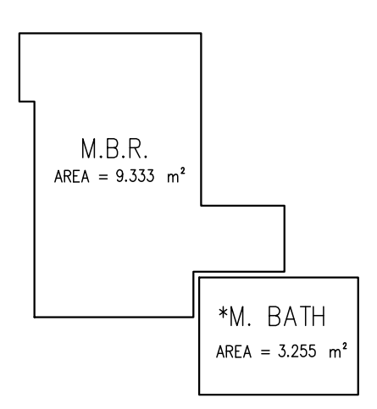
M.B.R.
AREA = 9.333 m²
*M. BATH
AREA = 3.255 m²

3/F – 30/F T1-FLAT A (M.B.R. & M. BATH) ROOM AREA

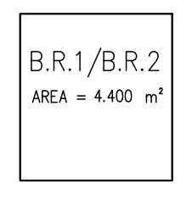
B.R.1/B.R.2
AREA = 4.400 m²

3/F – 30/F T1-FLAT A (B.R.1 & B.R.2) ROOM AREA

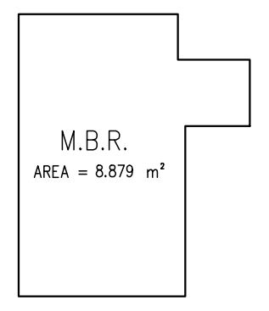
M.B.R.
AREA = 8.879 m²

3/F – 30/F T1-FLAT M (M.B.R.) ROOM AREA

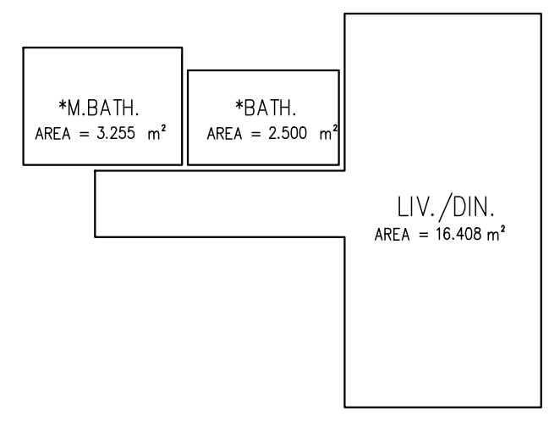
*M.BATH.
AREA = 3.255 m²
*BATH.
AREA = 2.500 m²
LIV./DIN.
AREA = 16.408 m²

3/F – 30/F T1-FLAT M (LIV./DIN., M.BATH & BATH.) ROOM AREA

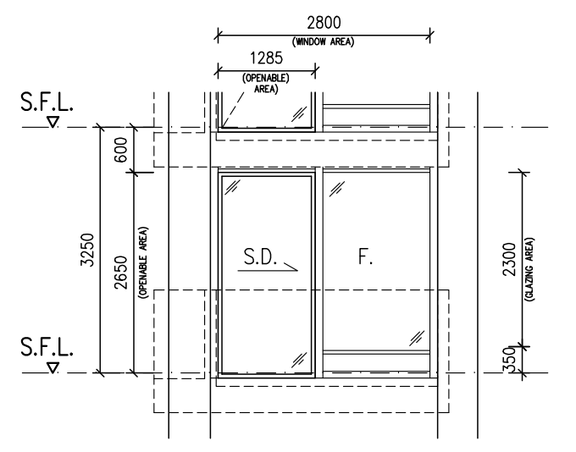
2800
S.F.L.
S.F.L.
3250
600
2650
(OPENABLE AREA)
S.D.
F.
2300
(GLAZING AREA)
350

WINDOW AREA CALCULATION
FOR T1-FLAT A (LIV./DIN., BATH. & LAV.)
(FOR T1-FLAT B TO H, J TO M (LIV./DIN. & BATH))

ROOM AREA = 19.024 s.m.

WINDOW AREA REQ'D = 19.024 / 10 = 1.902 s.m.
WINDOW AREA PROV'D = 2.800 x 2.300 x 0.70
= 4.508 s.m. > 1.902 s.m. (REQUIRED)

OPENABLE WINDOW AREA REQ'D = 19.024/16 + 2.500 / 10 + 1.063 / 10 = 1.545 s.m.
OPENABLE WINDOW AREA PROV'D = (1.285 x 2.650 x 0.70)
= 2.384 s.m. > 1.545 s.m. (REQUIRED)

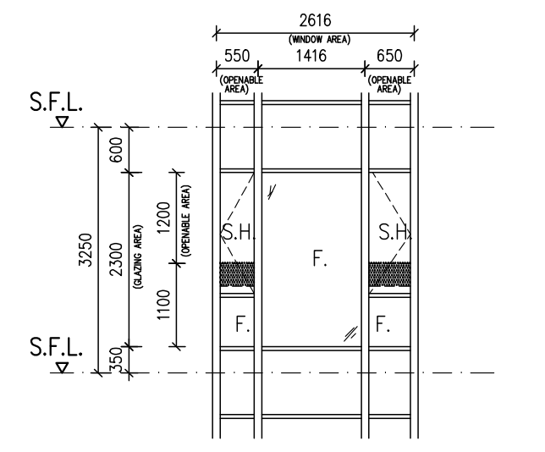
2616
550
1416
550
S.F.L.
S.F.L.
3250
600
2300
(GLAZING AREA)
1200
(OPENABLE AREA)
1100
350
S.H.
F.
S.H.
F.
F.

WINDOW AREA CALCULATION
FOR T1-FLAT A (M.B.R. & M. BATH)

ROOM AREA = 9.333 s.m.

WINDOW AREA REQ'D = 9.333 / 10 = 0.933 s.m.
WINDOW AREA PROV'D = 2.616 x 2.300 x 0.70
= 4.212 s.m. > 0.933 s.m. (REQUIRED)

OPENABLE WINDOW AREA REQ'D = 9.333 /16 + 3.255 /10 = 0.909 s.m.
OPENABLE WINDOW AREA PROV'D = (0.65 + 0.55) x 1.200 x 0.70
= 1.008 s.m. > 0.909 s.m. (REQUIRED)

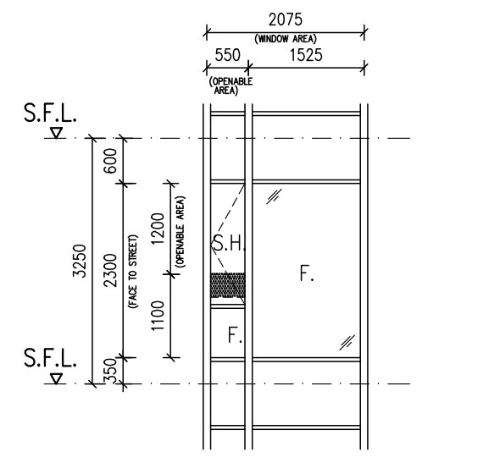
2075
550
1525
S.F.L.
S.F.L.
3250
600
2300
(FACE TO STREET)
1200
(OPENABLE AREA)
1100
350
S.H.
F.
F.

WINDOW AREA CALCULATION
FOR T1-FLAT A (B.R.1 & B.R.2)
(FOR T1-FLAT B TO H, J TO L (B.R.1 & B.R.2))

ROOM AREA = 4.400 s.m.

WINDOW AREA REQ'D = 4.400 / 10 = 0.440 s.m.
WINDOW AREA PROV'D = 2.075 x 2.300 x 0.70
= 3.341 s.m. > 0.440 s.m. (REQUIRED)

OPENABLE WINDOW AREA REQ'D = 4.400 /16 = 0.275 s.m.
OPENABLE WINDOW AREA PROV'D = 0.550 x 1.200 x 0.70
= 0.462 s.m. > 0.275 s.m. (REQUIRED)

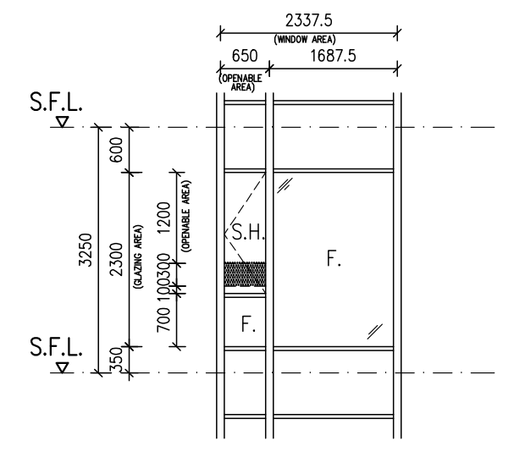
2337.5
650
1687.5
S.F.L.
S.F.L.
3250
600
2300
(GLAZING AREA)
1200
(OPENABLE AREA)
700
100
300
350
S.H.
F.
F.

WINDOW AREA CALCULATION
FOR T1-FLAT M (M.B.R.)
(FOR T1-FLAT F (M.B.R.))

ROOM AREA = 8.879 s.m.

WINDOW AREA REQ'D = 8.879 / 10 = 0.888 s.m.
WINDOW AREA PROV'D = 2.3375 x 2.300 x 0.70
= 3.763 s.m. > 0.888 s.m. (REQUIRED)

OPENABLE WINDOW AREA REQ'D = 8.879 /16 = 0.555 s.m.
OPENABLE WINDOW AREA PROV'D = 0.650 x (1.200 + 0.10) x 0.80
= 0.676 s.m. > 0.555 s.m. (REQUIRED)

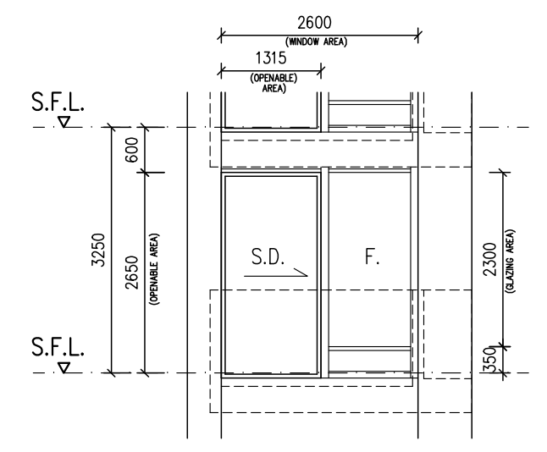
2600
1315
S.F.L.
S.F.L.
3250
600
2650
(OPENABLE AREA)
S.D.
F.
2300
(GLAZING AREA)
350

WINDOW AREA CALCULATION
FOR T1-FLAT M (LIV./DIN., M.BATH. & BATH.)

ROOM AREA = 16.408 s.m.

WINDOW AREA REQ'D = 16.408 / 10 = 1.641 s.m.
WINDOW AREA PROV'D = 2.600 x 2.300 x 0.70
= 4.186 s.m. > 1.641 s.m. (REQUIRED)

OPENABLE WINDOW AREA REQ'D = 16.408/16 + 2.500 / 10 + 3.255 / 10 = 1.601 s.m.
OPENABLE WINDOW AREA PROV'D = (1.315 x 2.650 x 0.70)
= 2.439 s.m. > 1.601 s.m. (REQUIRED)

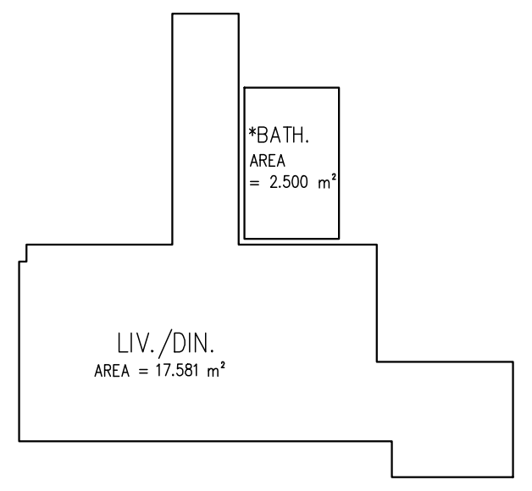
*BATH.
AREA = 2.500 m²
LIV./DIN.
AREA = 17.581 m²

3/F – 30/F T2-FLAT A (LIV./DIN. & BATH.) ROOM AREA

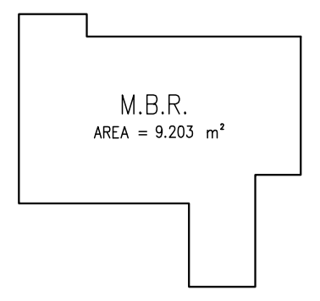
M.B.R.
AREA = 9.203 m²

3/F – 30/F T2-FLAT A (M.B.R.) ROOM AREA

B.R.1
AREA = 4.950 m²

3/F – 30/F T2-FLAT J (B.R.1) ROOM AREA

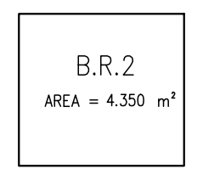
B.R.2
AREA = 4.350 m²

3/F – 30/F T2-FLAT A (B.R.2) ROOM AREA

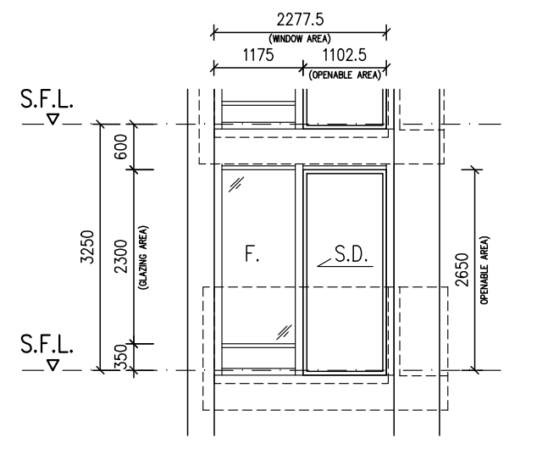
2277.5
1175
1102.5
S.F.L.
S.F.L.
3250
600
2300
(GLAZING AREA)
350
F.
S.D.
2650
(OPENABLE AREA)

WINDOW AREA CALCULATION
FOR T2-FLAT A (LIV./DIN. & BATH.)
(FOR T2-FLAT B TO H, J TO N, P & Q (LIV./DIN. & BATH))

ROOM AREA = 17.581 s.m.

WINDOW AREA REQ'D = 17.581 / 10 = 1.758 s.m.
WINDOW AREA PROV'D = 2.2775 x 2.300 x 0.70
= 3.667 s.m. > 1.758 s.m. (REQUIRED)

OPENABLE WINDOW AREA REQ'D = 17.581 /16 + 2.500 / 10 = 1.349 s.m.
OPENABLE WINDOW AREA PROV'D = (1.1025 x 2.650 x 0.70)
= 2.045 s.m. > 1.349 s.m. (REQUIRED)

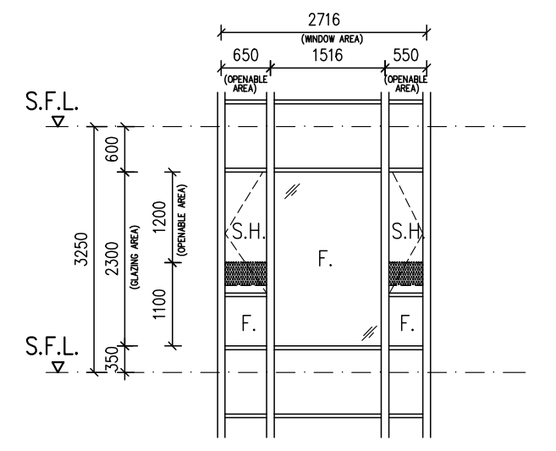
2716
650
1516
550
S.F.L.
S.F.L.
3250
600
2300
(GLAZING AREA)
1200
(OPENABLE AREA)
1100
350
S.H.
F.
S.H.
F.
F.

WINDOW AREA CALCULATION
FOR T2-FLAT A (M.B.R.)

ROOM AREA = 9.203 s.m.

WINDOW AREA REQ'D = 9.203 / 10 = 0.920 s.m.
WINDOW AREA PROV'D = 2.716 x 2.300 x 0.70
= 4.373 s.m. > 0.920 s.m. (REQUIRED)

OPENABLE WINDOW AREA REQ'D = 9.203 /16 = 0.575 s.m.
OPENABLE WINDOW AREA PROV'D = (0.65 + 0.55) x 1.200 x 0.70
= 1.008 s.m. > 0.575 s.m. (REQUIRED)

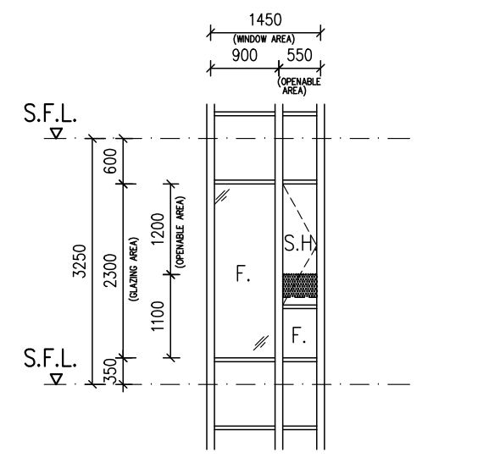
1450
900
550
S.F.L.
S.F.L.
3250
600
2300
(GLAZING AREA)
1200
(OPENABLE AREA)
1100
350
F.
S.H.
F.

WINDOW AREA CALCULATION
FOR T2-FLAT J (B.R.1)
(FOR T2-FLAT B TO D, G, H, K TO N & P (B.R.1))

ROOM AREA = 4.950 s.m.

WINDOW AREA REQ'D = 4.950 / 10 = 0.495 s.m.
WINDOW AREA PROV'D = 1.450 x 2.300 x 0.70
= 2.335 s.m. > 0.495 s.m. (REQUIRED)

OPENABLE WINDOW AREA REQ'D = 4.950 /16 = 0.309 s.m.
OPENABLE WINDOW AREA PROV'D = 0.550 x 1.200 x 0.70
= 0.462 s.m. > 0.309 s.m. (REQUIRED)

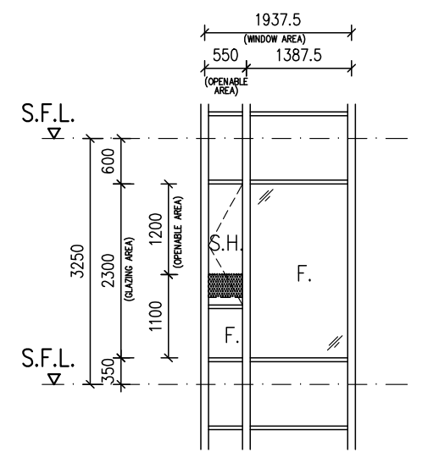
1937.5
550
1387.5
S.F.L.
S.F.L.
3250
600
2300
(GLAZING AREA)
1200
(OPENABLE AREA)
1100
350
S.H.
F.
F.

WINDOW AREA CALCULATION
FOR T2-FLAT A (B.R.2)
(FOR T2-FLAT A, E, F, J & Q (B.R.1))
(FOR T2-FLAT B TO H, K TO N, P & Q (M.B.R.))

ROOM AREA = 4.350 s.m.

WINDOW AREA REQ'D = 4.350 / 10 = 0.435 s.m.
WINDOW AREA PROV'D = 1.9375 x 2.300 x 0.70
= 3.119 s.m. > 0.435 s.m. (REQUIRED)

OPENABLE WINDOW AREA REQ'D = 4.350 /16 = 0.272 s.m.
OPENABLE WINDOW AREA PROV'D = 0.550 x 1.200 x 0.70
= 0.462 s.m. > 0.272 s.m. (REQUIRED)

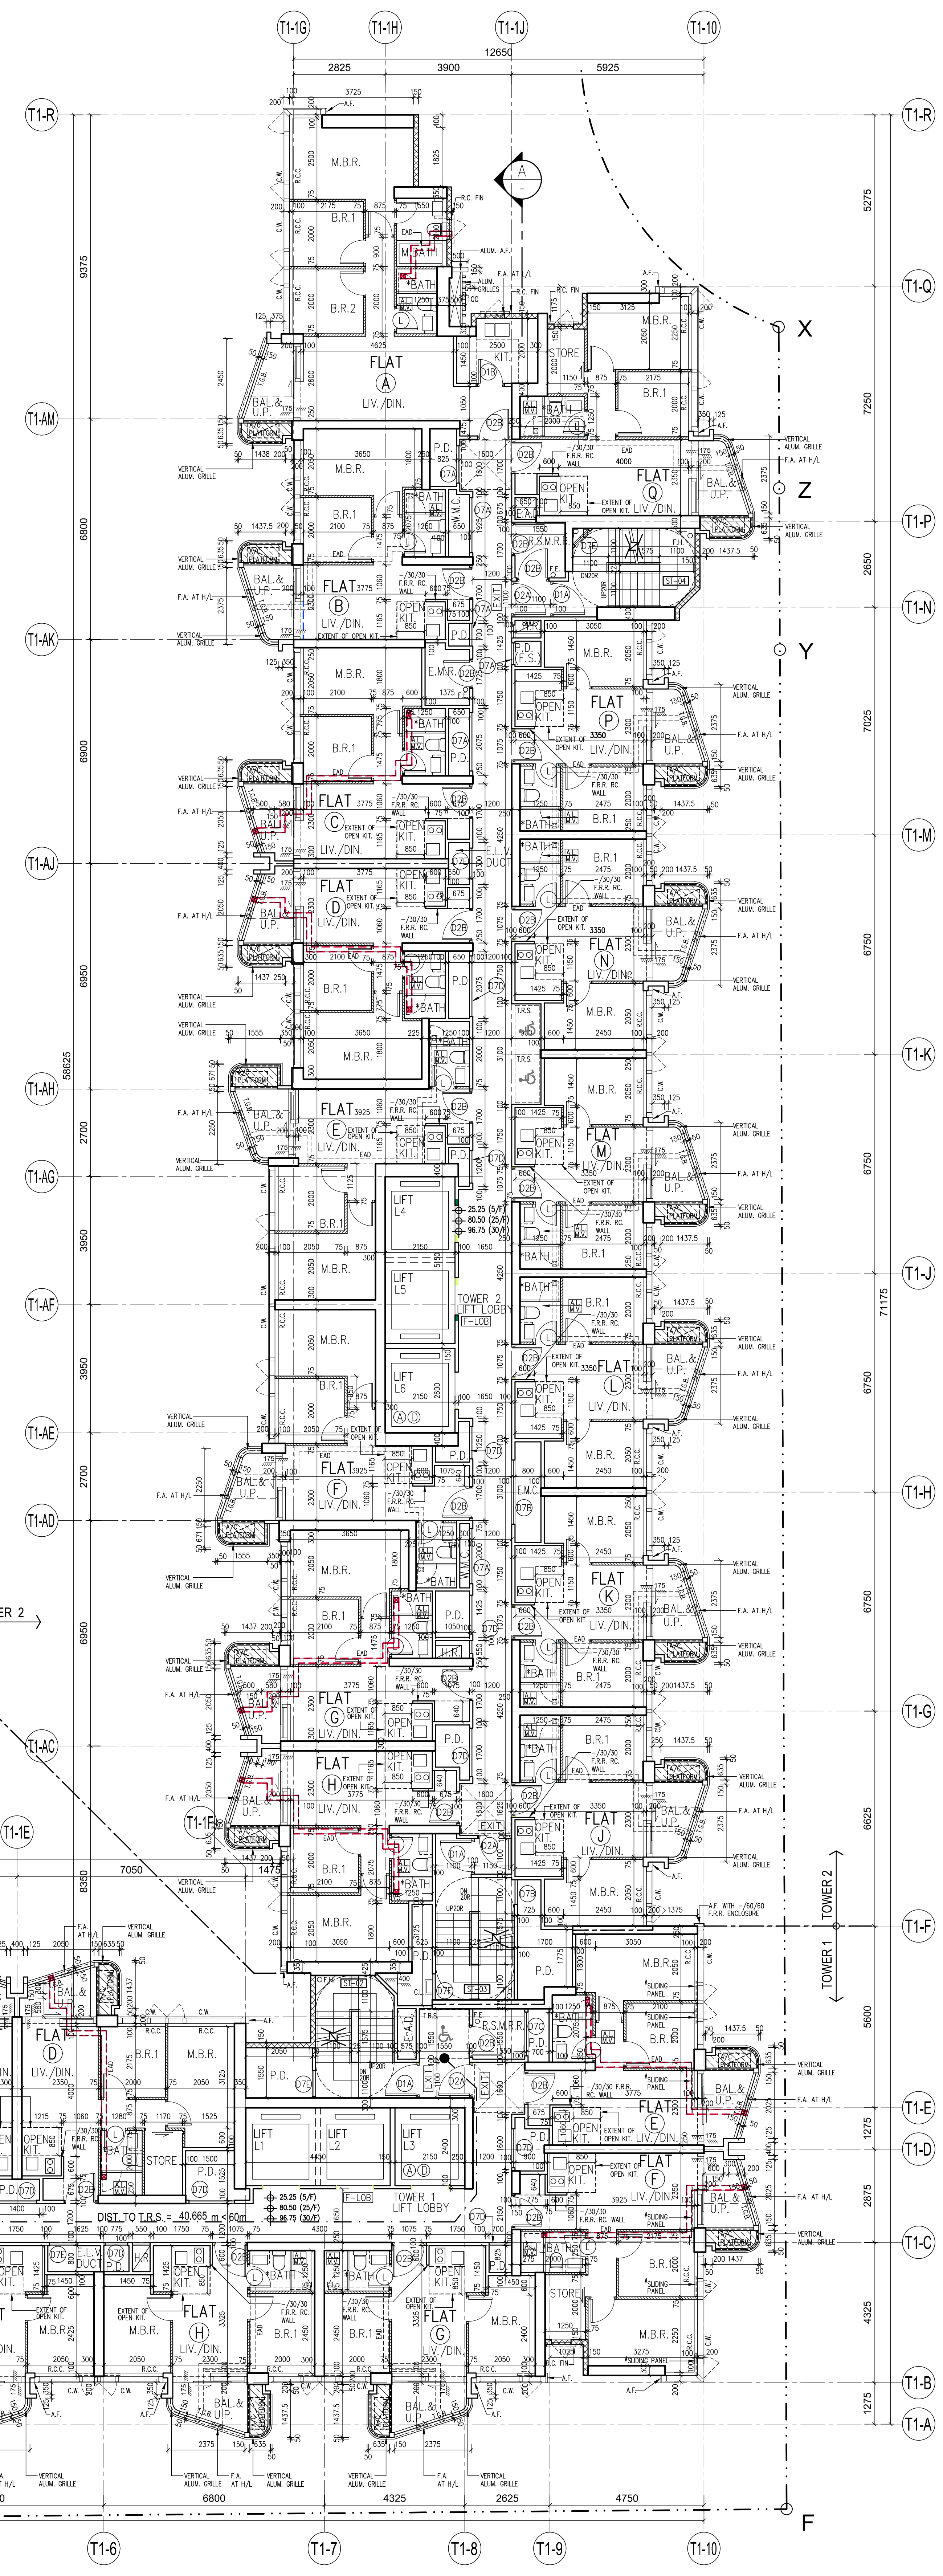
T1-1G
T1-1H
T1-1J
T1-10
2825
3900
5925
12650
T1-R
T1-Q
T1-AM
T1-P
T1-N
T1-AK
T1-M
T1-AJ
T1-L
T1-AH
T1-AG
T1-K
T1-AF
T1-J
T1-AE
T1-AD
T1-H
T1-G
T1-AC
T1-1F
T1-F
T1-E
T1-D
T1-C
T1-B
T1-A
9375
6800
6900
6950
6825
2700
3950
3950
2700
6950
6350
5275
7250
2650
7025
6750
6750
6750
6750
6625
5600
2275
2875
4325
1275
71175
FLAT A
FLAT Q
FLAT B
FLAT P
FLAT C
FLAT D
FLAT N
FLAT M
FLAT E
FLAT F
FLAT L
FLAT G
FLAT K
FLAT H
FLAT J
FLAT E
FLAT F
FLAT G
LIFT L4
LIFT L5
LIFT L6
TOWER 2 LIFT LOBBY
TOWER 1
TOWER 2
X
Y
Z
A
F
VERTICAL ALUM. GRILLE
F.A. AT H/L
LIV./DIN.
M.B.R.
B.R.1
B.R.2
KIT.
OPEN KIT.
BAL. & U.P.
P.D.
STORE
E.M.R.

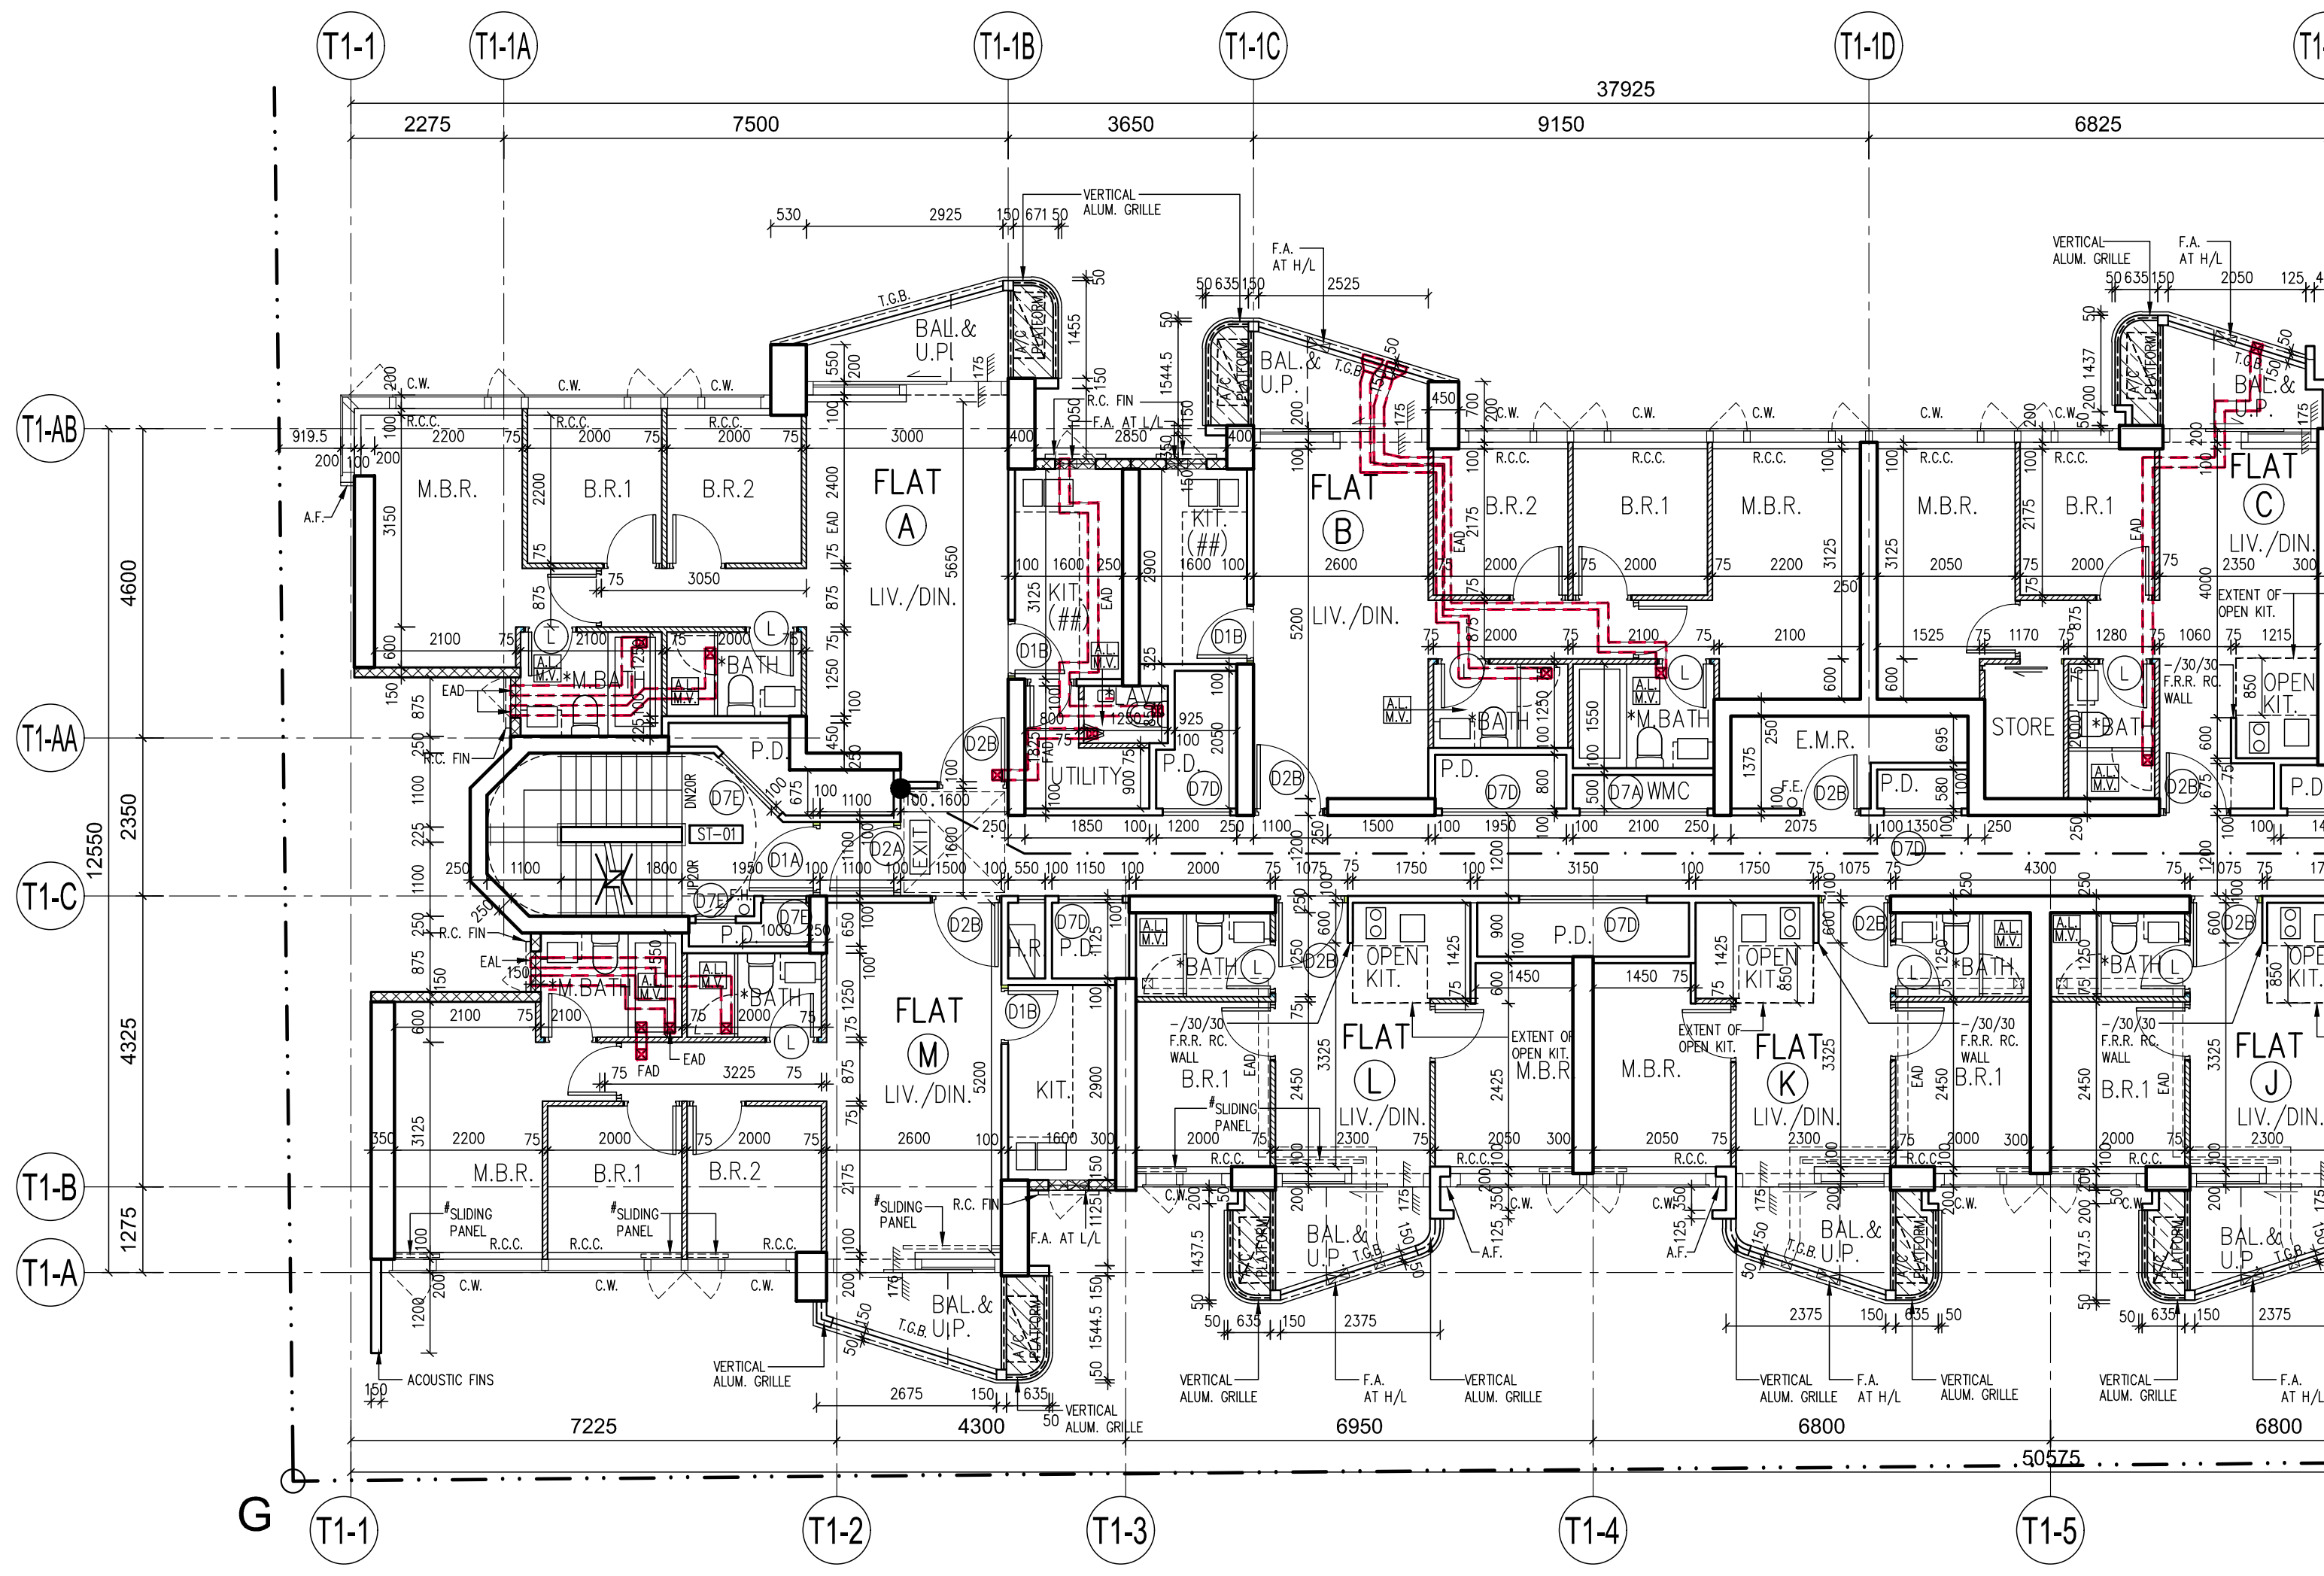
T1-1
T1-1A
T1-1B
T1-1C
T1-1D
T1-1E
37925
2275
7500
3650
9150
6825
7050
T1-AB
T1-AA
T1-C
T1-B
T1-A
4600
12550
2350
4325
1275
FLAT A
FLAT B
FLAT C
FLAT D
FLAT M
FLAT L
FLAT K
FLAT J
FLAT H
FLAT G
LIFT L1
LIFT L2
LIFT L3
TOWER 1 LIFT LOBBY
DIST. TO T.B.S. = 40.665 m
STORE
UTILITY
E.M.R.
M.B.R.
B.R.1
B.R.2
LIV./DIN.
KIT.
BAL. & U.P.
G
T1-1
T1-2
T1-3
T1-4
T1-5
T1-6
T1-7
T1-8
T1-9
T1-10
7225
4300
6950
6800
6800
6800
4325
2625
4750
50525

TOWER 1 | TOWER 2

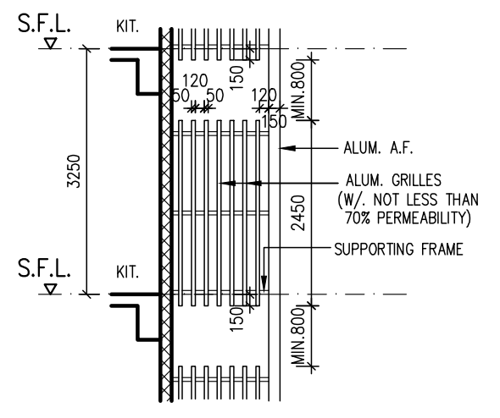
S.F.L.
S.F.L.
ALUM. AF.
ALUM. GRILLES (NOT LESS THAN 70% PERMEABILITY)
SUPPORTING FRAME

Ⓐ TYPICAL DETAIL OF ALUM. GRILLES FOR SCREENING OF EXTERNAL PIPES AT T2

5TH TO 30TH FLOOR PLAN – TOWER 1 & TOWER 2 (23 STOREYS)

NOTE:
1. MECHANICAL VENTILATION AND ARTIFICIAL LIGHTING WILL BE PROVIDED AT THE BATHROOM/ LAVATORY MARKED WITH " * " FOR OMISSION OF NATURAL LIGHTING AND VENTILATION.
2. THERE WILL BE NO 13/F, 14/F & 24/F IN THE NOMENCLATURE SYSTEM FOR NUMBERING OF FLOORS.
3. SLIDING PANEL TO BE PROVIDED AT WHICH MARKED WITH "#" (REFER TO SLIDING PANEL SCHEDULE DWG. NO. A/GBP/12)
4. LIGHTING AND VENTILATION PROVISION TO ADOPT PERFORMANCE–BASED APPROACH FOR THE ROOM MARKED WITH (##) (REFER DWG. NO. A/GBP/10, A/GBP/10.1)
5. 5 ACH MECHANICAL VENTILATION SHALL BE PROVIDED TO KITCHENS USING UVA METHOD.

LEGEND:

▨	NON–STRUCTURAL PREFABRICATE EXTERNAL WALL (THICKNESS MAX. 150mm)
⬚	COMMON AREA FOR MAINTENANCE
▧	A/C PLATFORM

SLIDING PANEL SCHEDULE

TOWER 1		
FLAT	ROOM	FLOOR
E	LIV./DIN.#2	3/F–5/F
	B.R.1#3	
	M.B.R.#3	3/F
F	LIV./DIN.#2	3/F–5/F
	B.R.1#3	3/F–6/F
	M.B.R.#3	3/F–8/F
G	LIV./DIN.#2	5/F–8/F
	M.B.R.#3	5/F–9/F
	B.R.1#3	5/F–8/F
H	LIV./DIN.#2	5/F–8/F
	M.B.R.#3	5/F–8/F
	B.R.1#3	
J	LIV./DIN.#2	5/F–8/F
	M.B.R.#3	5/F–8/F
	B.R.1#3	5/F–9/F
K	LIV./DIN.#2	5/F–9/F
	M.B.R.#3	5/F–9/F
	B.R.1#3	5/F–9/F
L	LIV./DIN.#2	5/F–10/F
	B.R.1#3	3/F–10/F
	M.B.R.#3	5/F–10/F
M	LIV./DIN.#2	3/F–12/F
	M.B.R.#3	3/F–16/F
	B.R.1#3	
	B.R.2#3	3/F–15/F

#2: ACOUSTIC DOOR
#3: ACOUSTIC WINDOW

B.D. Ref : BD 2/4024/21
BIM Ref : - --
F.S.D. Ref : - --
D.L.O. Ref : - --

Rev.	Description	Drawn	Checked	Approved	Date
-	1st Submission	WY	AW	AL	07/2022
A	2nd Submission	WY	AW	AL	11/2022
B	1st Amendment	TWM	AW	AL	04/2023
C	2nd Amendment	TWM	AW	AL	12/2023
D	3rd Amendment	TWM	AW	AL	04/2024
D	3rd Amendment (Re-submission)	TWM	AW	AL	05/2024
E	5th Amendment	TWM	AW	AL	12/2024
E	5th Amendment (Re-submission)	TWM	AW	AL	02/2025
F	8th Amendment	TWM	AW	AL	05/2025
G	9th Amendment	TWM	AW	AL	08/2025
G	9th Amendment (Re-submission)	TWM	AW	AL	10/2025
H	10th Amendment	TWM	AW	AL	12/2025
I	11th Amendment	TWM	AW	AL	02/2026

Type II works
The works shown on these plans are Type II works (Building Amendment) in respect of which consent is applied for the purpose of Fast Track consent application under regulation 33 of the Building (Administration) Regulations.

RONALD LU & PARTNERS
呂元祥建築師事務所

Project Title :
PROPOSED DEVELOPMENT
AT BAILEY STREET
& WING KWONG STREET
TO KWA WAN, KOWLOON

Drawing Title :
5TH - 30TH FLOOR PLAN
FOR TOWER 1 & TOWER 2

Drawn By	TWM	Date	08/2025
Checked By	AW	Date	08/2025
Approved By	AL	Date	08/2025
Project No.	21163KL	Issue Date	08/2025

File Path :
U:\Studio_B\Proj_Data\2021\21163KL_Bailey Street & Wing Kwong Street\DRAWING\SUB\BD\GBP_13 (Final Amendment)_Hand Amend\PLOT\A_GBP_12.dwg

Scale 1:100 By CAD

Drawing Number : A/GBP/12
Revision Number : I

Drawing Purpose
Buildings Department
Amended Plan

Digitally signed by
LEUNG Kit Man Andy
AP(A) 80/85
16 March 2026

Received on
16 March 2026

Plan Approved
(Digitally Signed)
TSOI Lap-san, Lapson
Senior Building Surveyor
for BUILDING AUTHORITY
17 March 2026

Note: This plan has been processed on a curtailed check basis under the centralized processing system as promulgated in PNAP ADM-19. The duties of the authorized person, registered structural engineer and/or registered geotechnical engineer concerned as specified under section 4(3)(b) and the provision of section 14(2)(c) of the Buildings Ordinance are of particular relevance in this regard.

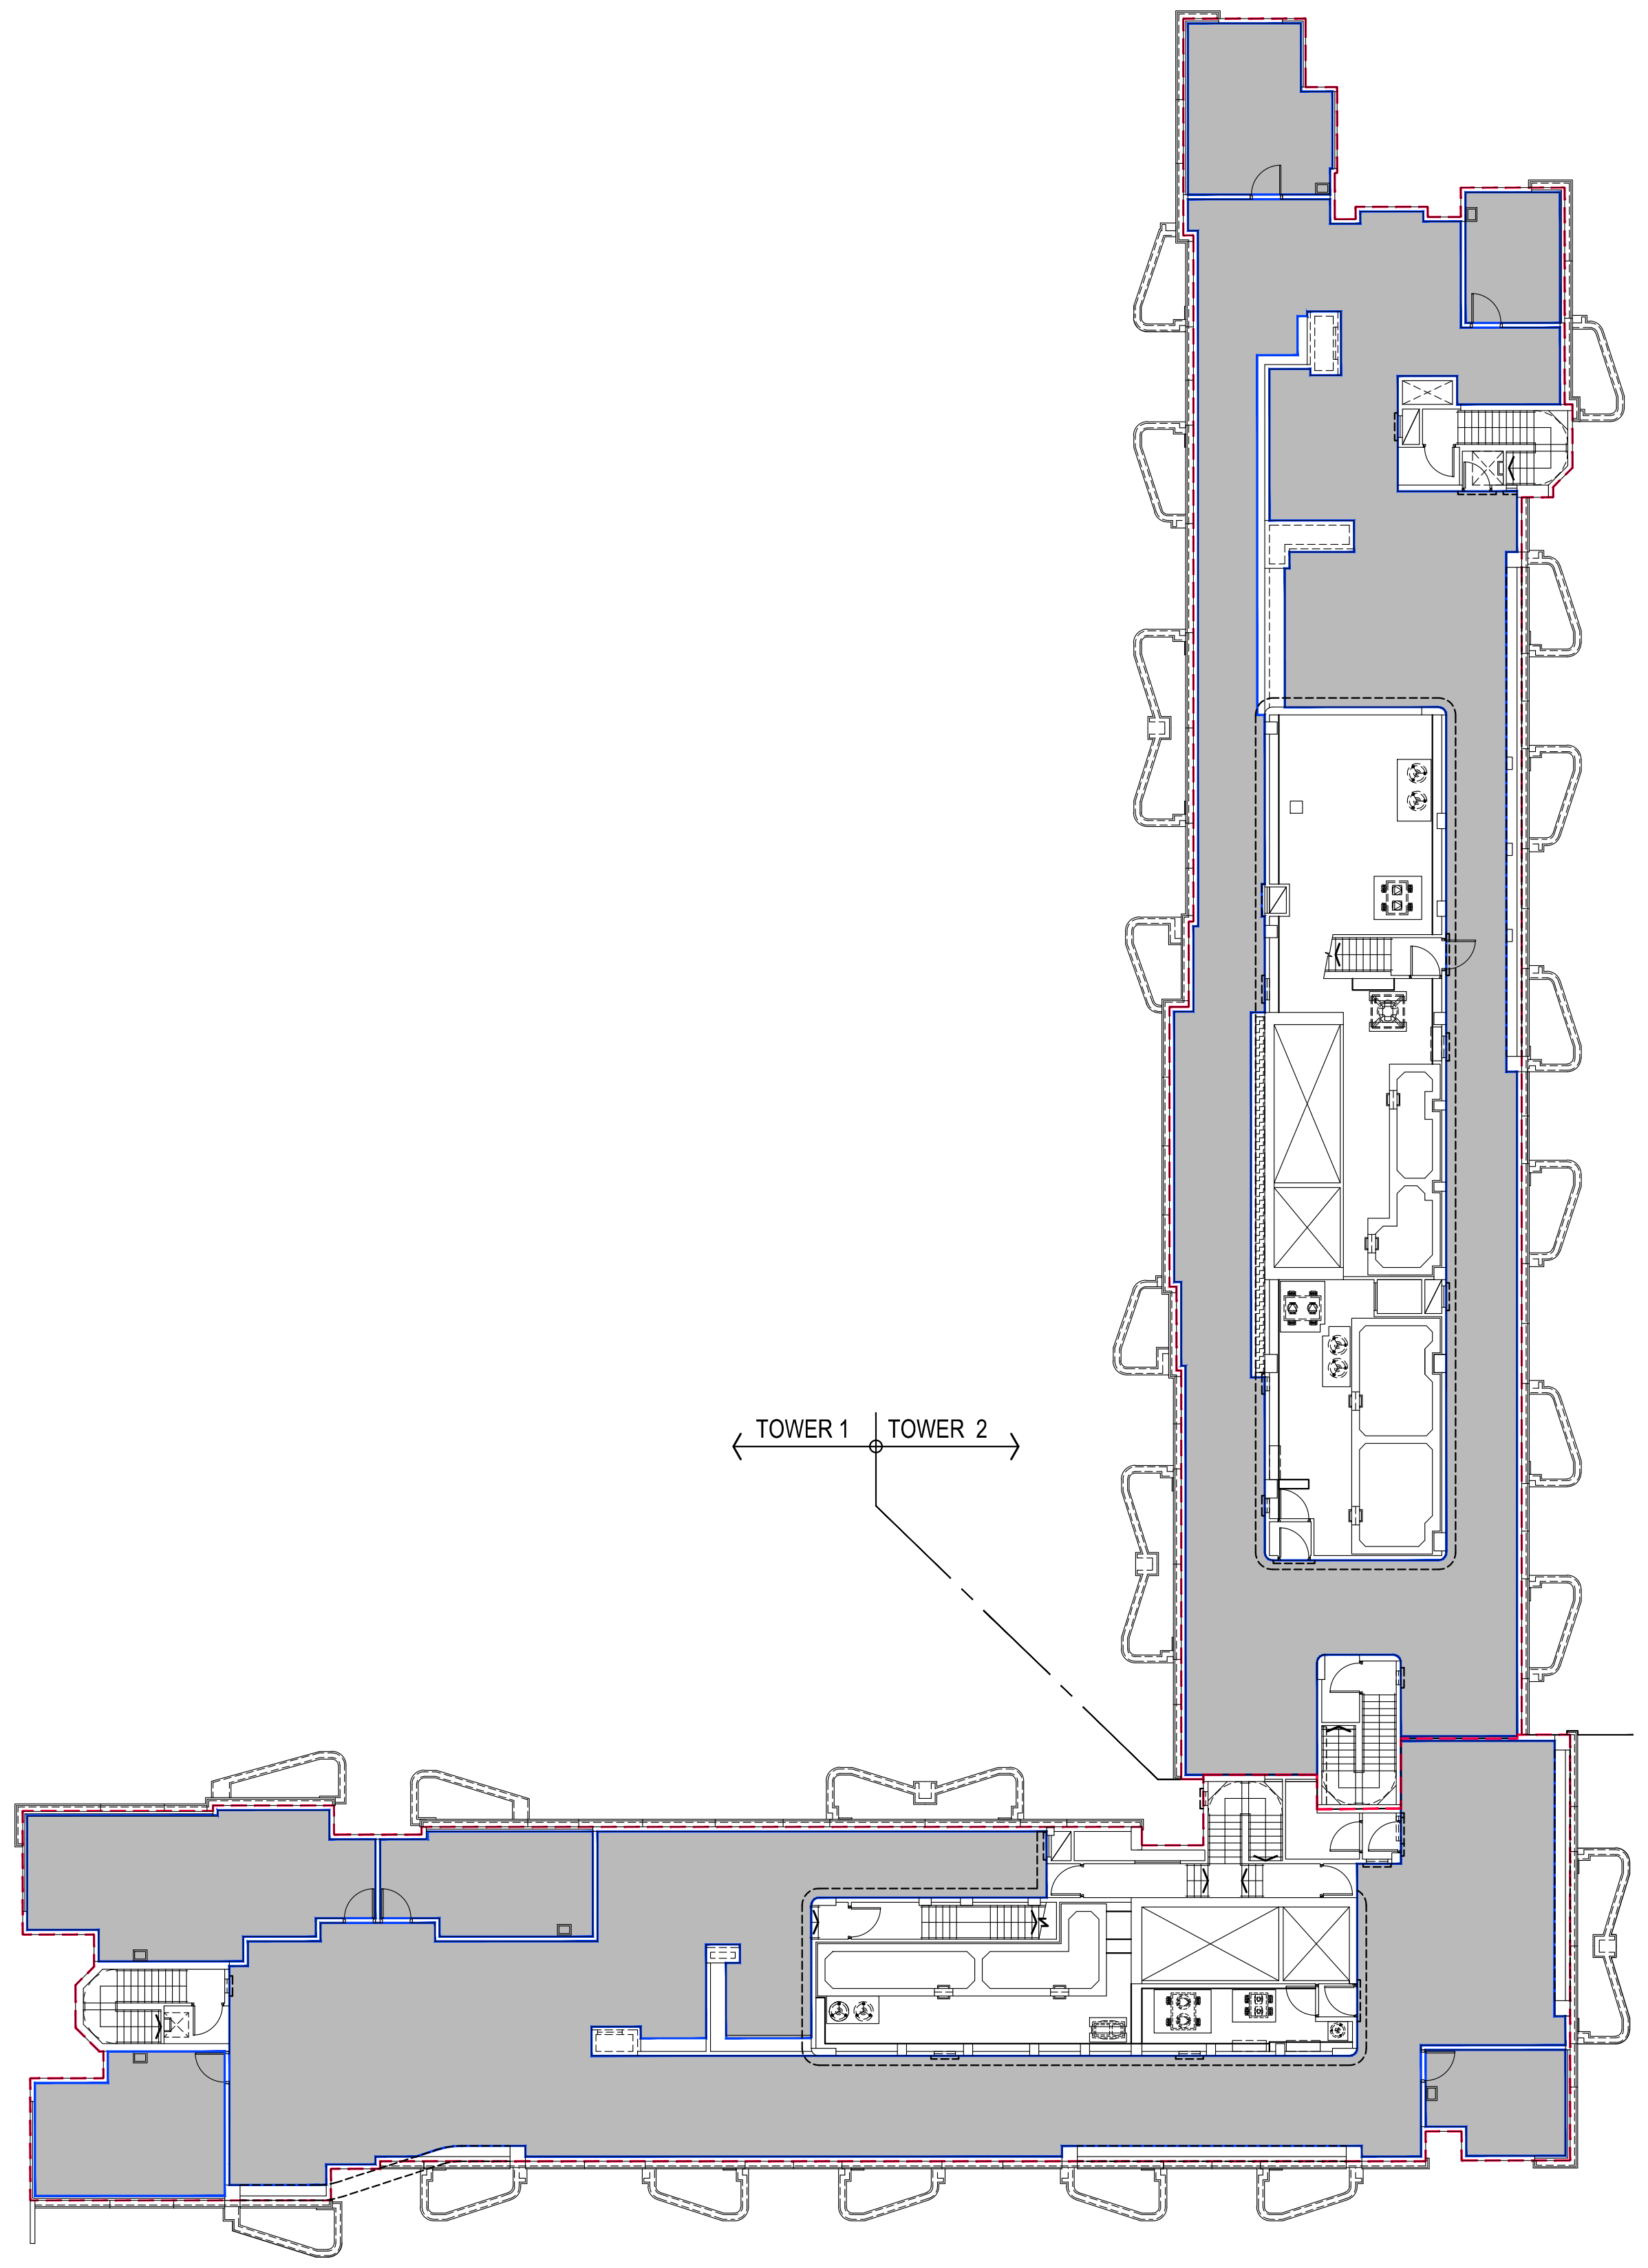
TOWER 1
TOWER 2
TOWER 1
TOWER 2

TOWER 1 & TOWER 2 ROOF FLOOR DIAGRAM

(UNDER PLANNING DEPARTMENT)
SCALE 1:200

	TOWER 1	TOWER 2
— — AREA OF ROOF	576.291 m²	600.794 m²
▨ AREA OF ROOF W/O. ROOF TOP STRUCTURE	400.750 m² (69.540 % OF ROOF AREA)	360.058 m² (59.930 % OF ROOF AREA)

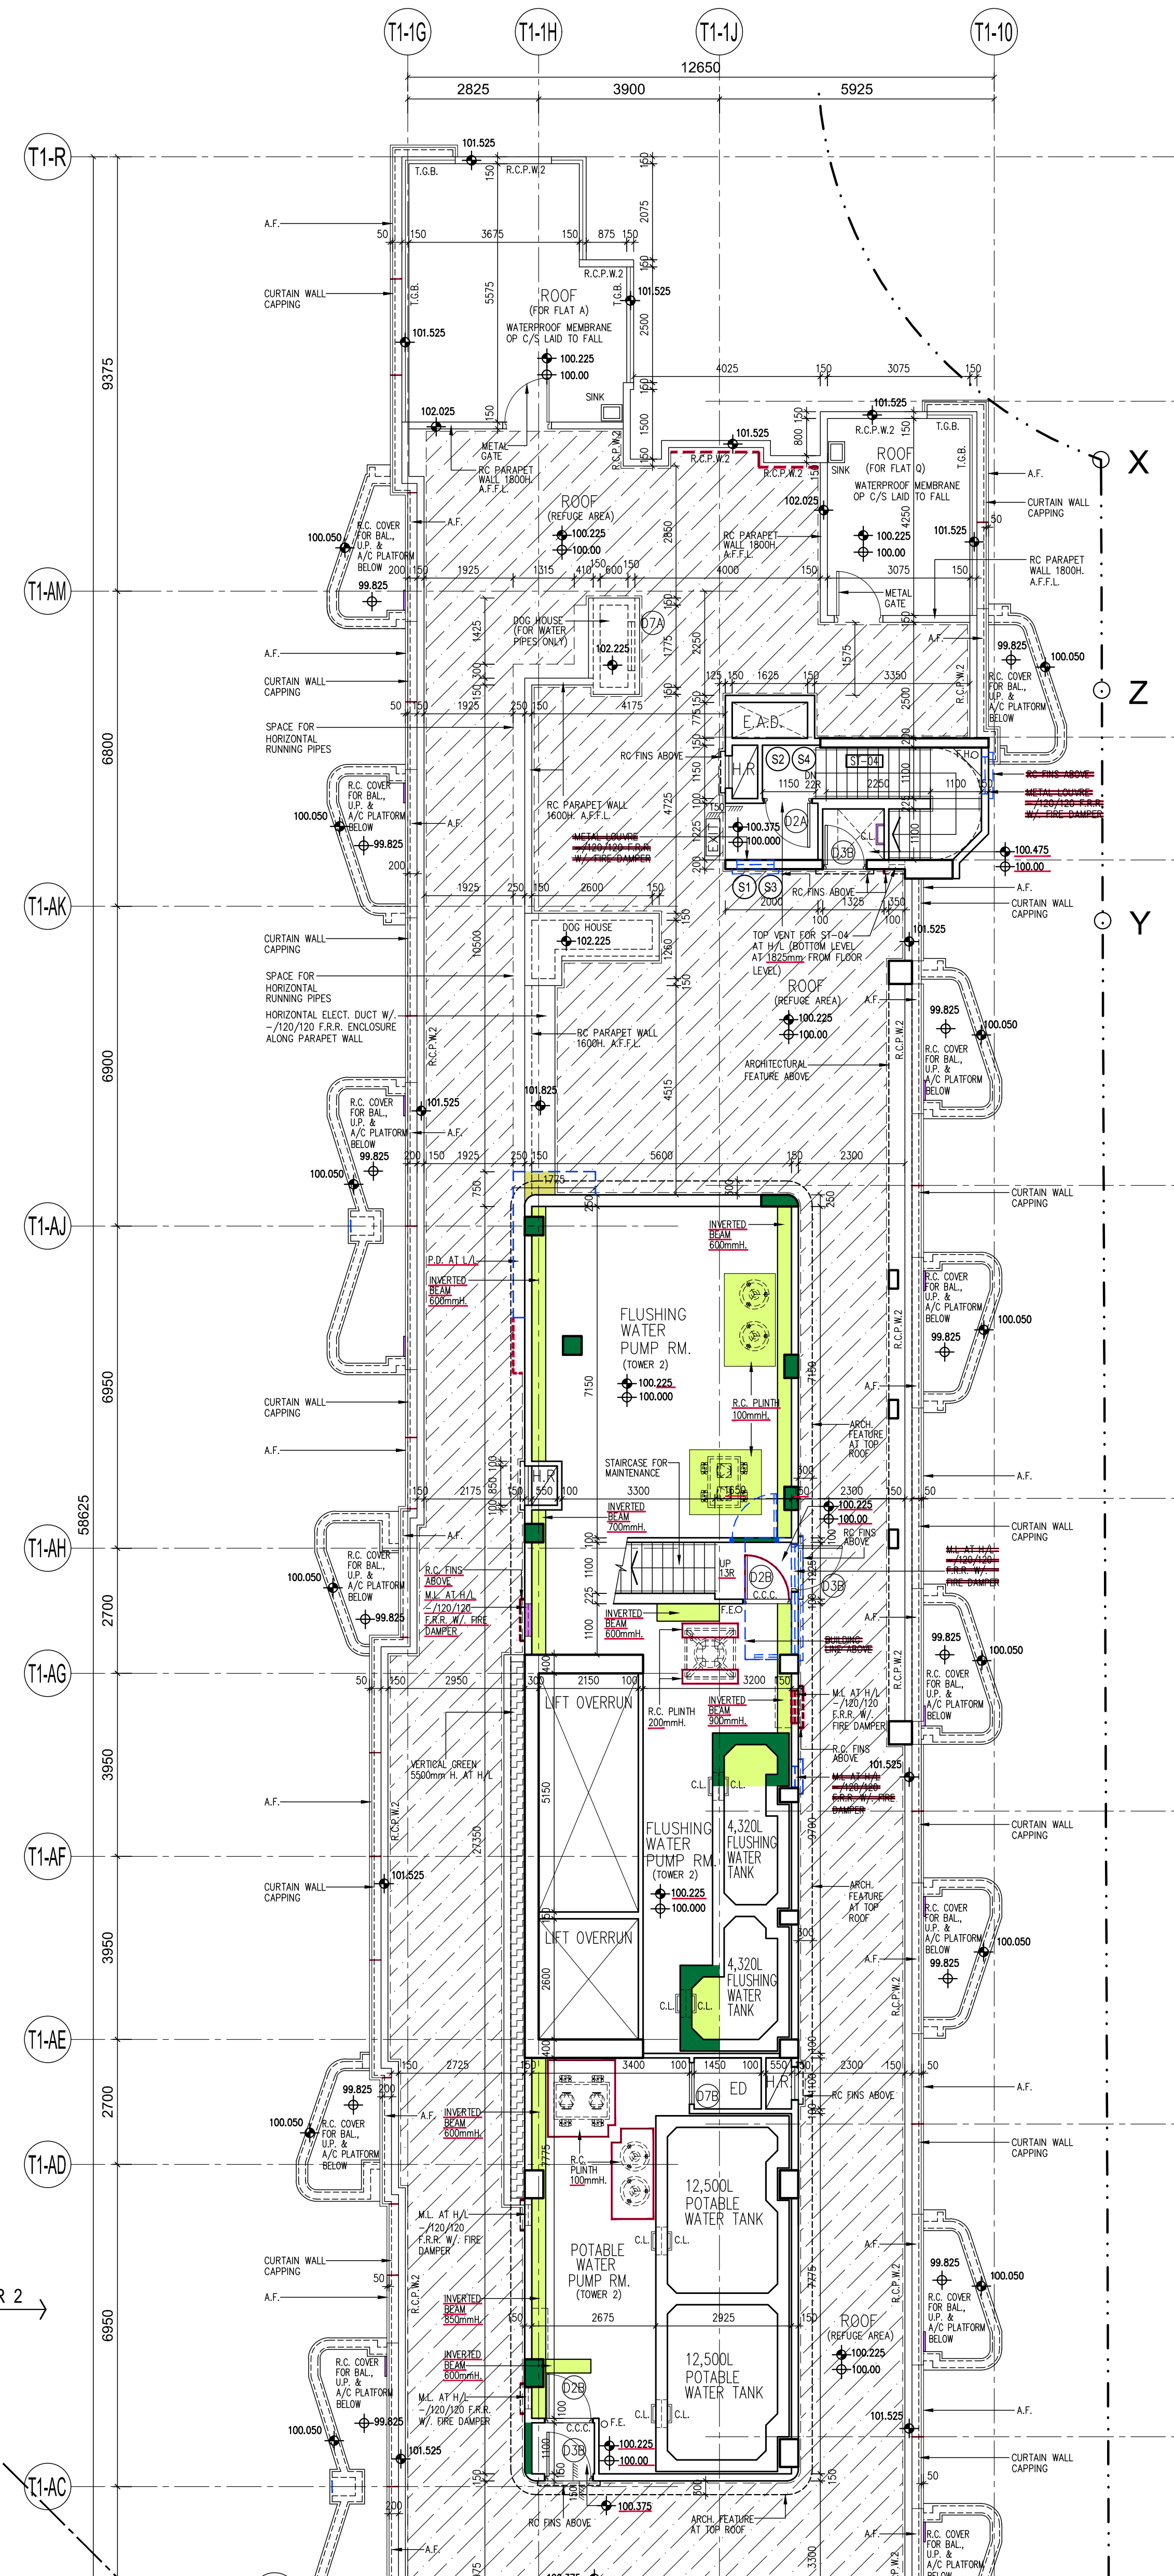
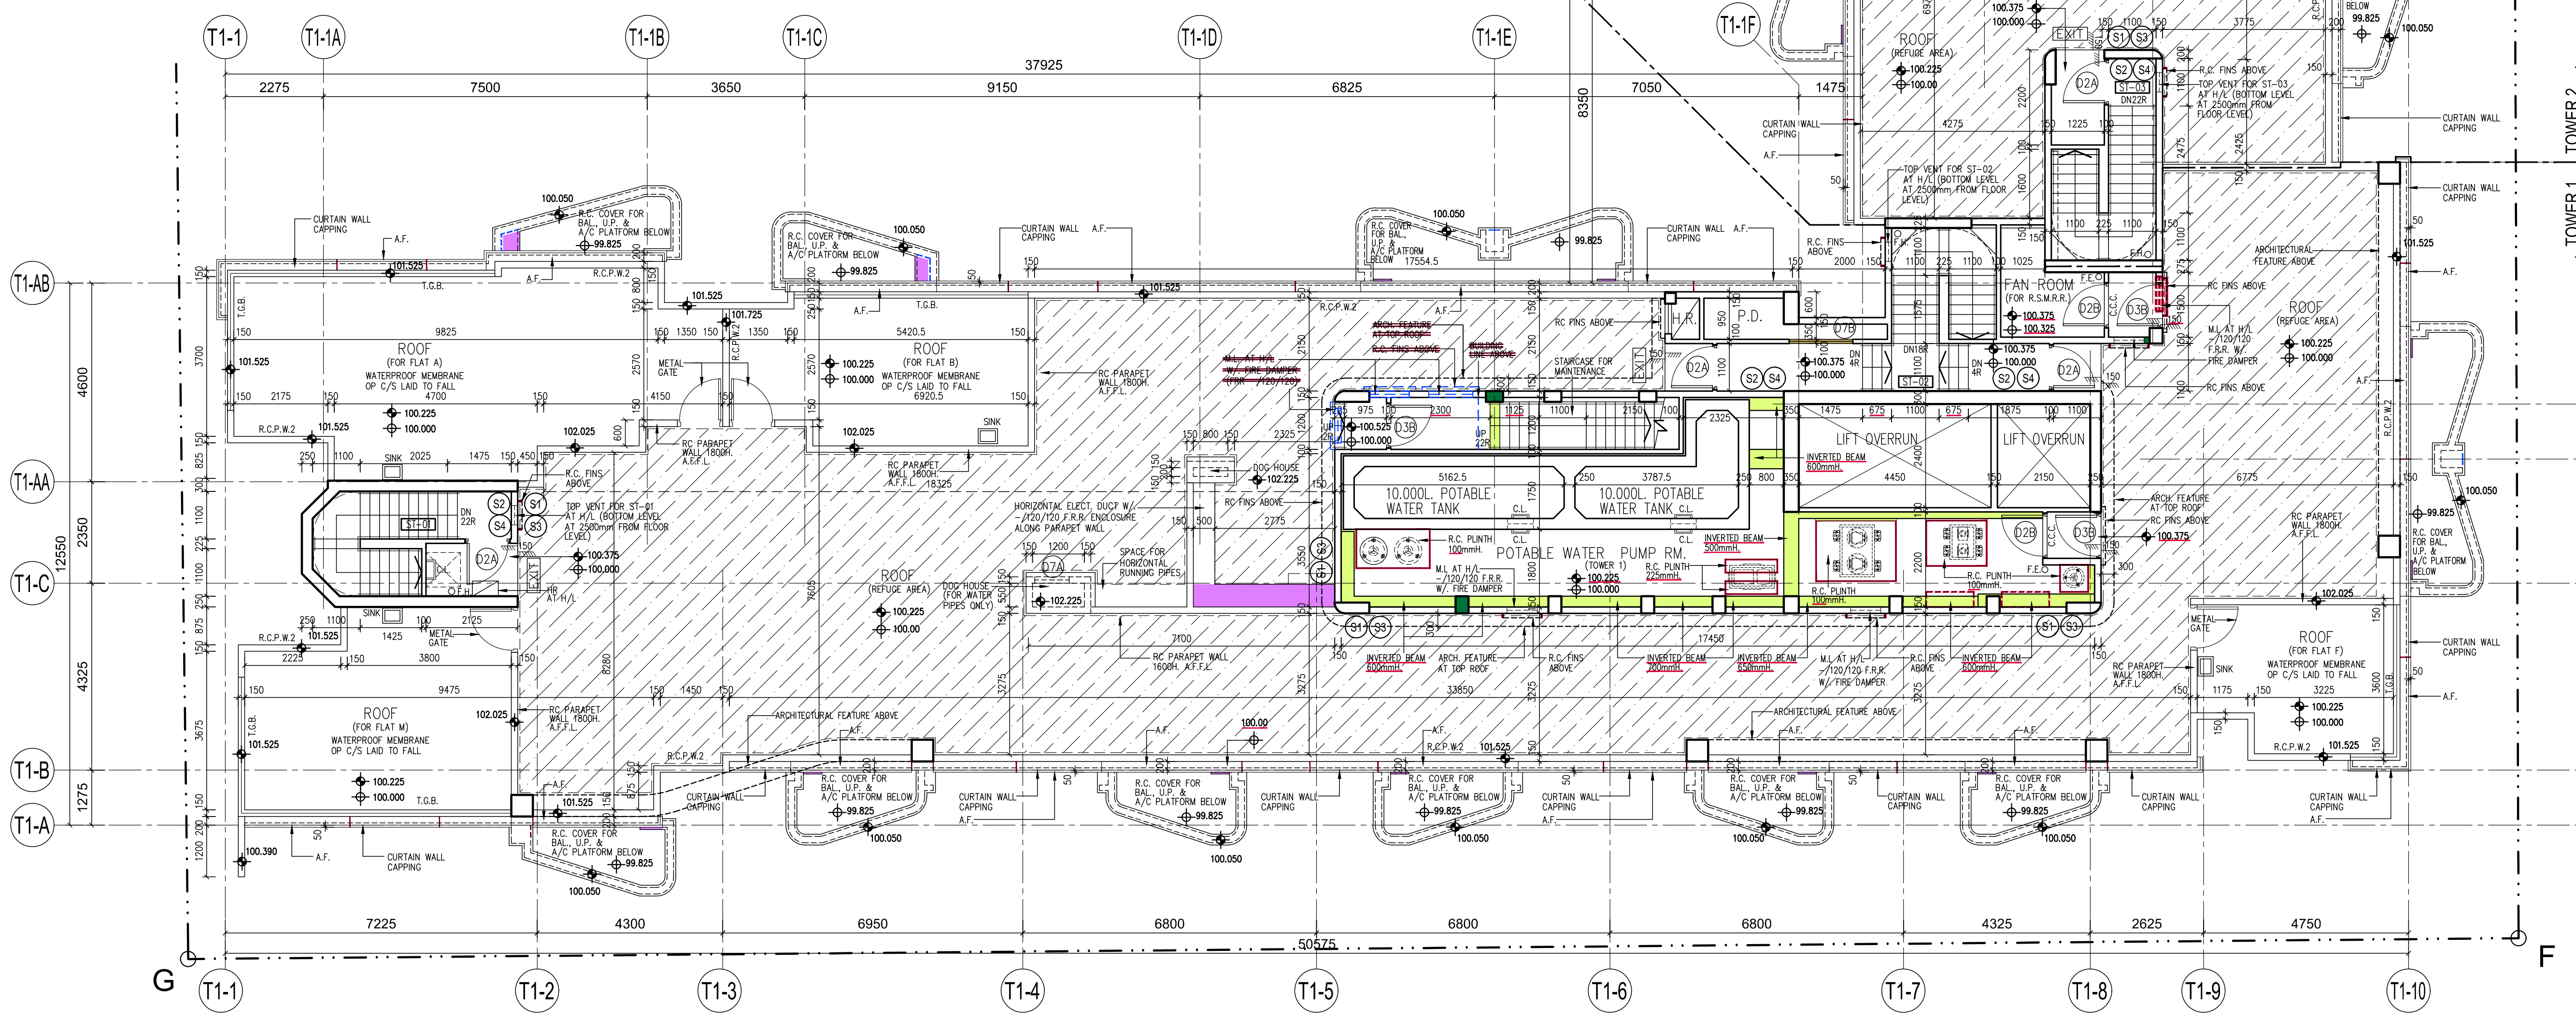
T1-1G
T1-1H
T1-1J
T1-10
T1-R
T1-Q
T1-AM
T1-P
T1-N
T1-AK
T1-M
T1-AJ
T1-K
T1-AH
T1-AG
T1-J
T1-AF
T1-H
T1-AE
T1-AD
T1-G
T1-AC
T1-1F
T1-F
T1-E
T1-D
T1-C
T1-B
T1-A
T1-AB
T1-AA
T1-1
T1-1A
T1-1B
T1-1C
T1-1D
T1-1E
T1-2
T1-3
T1-4
T1-5
T1-6
T1-7
T1-8
T1-9
X
Z
Y
F
G
12650
37925
71175
60575
ROOF
FLUSHING WATER PUMP RM. (TOWER 2)
LIFT OVERRUN
FLUSHING WATER PUMP RM. (TOWER 2)
4,320L FLUSHING WATER TANK
POTABLE WATER PUMP RM. (TOWER 2)
12,500L POTABLE WATER TANK
FAN ROOM
10,000L POTABLE WATER TANK
FLUSHING WATER PUMP RM. (TOWER 1)
TOWER 1
TOWER 2
CURTAIN WALL CAPPING
DELETE

PART PLAN AT LEVEL 102.975

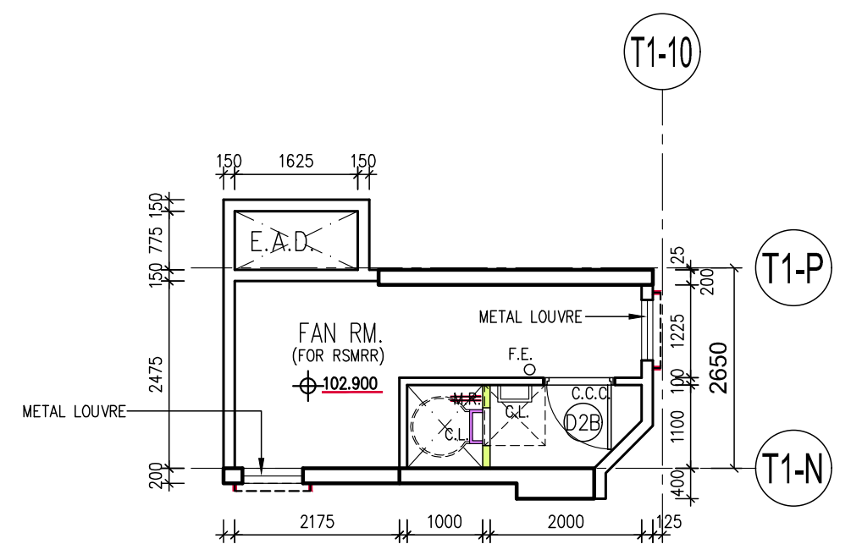
T1-10
T1-P
T1-N
E.&D.C.
FAN RM.
METAL LOUVRE

PART PLAN AT LEVEL 102.90

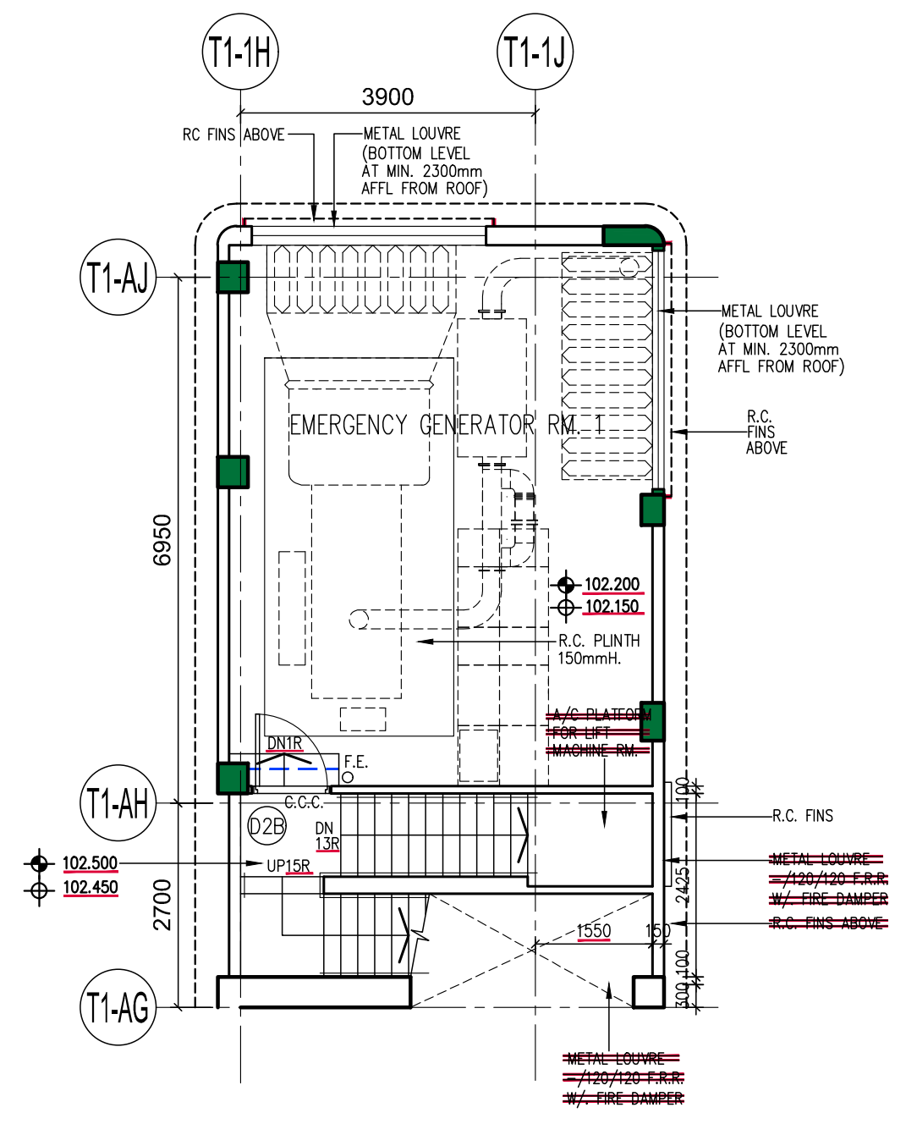
T1-1H
T1-1J
3900
T1-AJ
T1-AH
T1-AG
EMERGENCY GENERATOR RM.
METAL LOUVRE

PART PLAN AT LEVEL 102.150

ROOF PLAN – TOWER 1 & TOWER 2

LEGEND:

(S1)	REFUGE FLOOR NOTICE
(S2)	STAIR NO. SIGN
(S3)	DIRECTIONAL SIGN TO EXIT STAIRCASE
(S4)	A SIGN INDICATING THE ENTRANCE TO THE REFUGE FLOOR
▨	NET REFUGE AREA : TOWER 1 = 282.767 m², TOWER 2 = 310.287 m²

THE PERCENTAGE OF THE NET REFUGE AREA

	TOWER 1	TOWER 2
THE G.F.A. OF THE LARGEST FLOOR PLATE	561.518 m²	608.058 m²2
PERCENTAGE OF REFUGE AREA PROVIDED	282.767 / 561.518 x 100% 50.358 % > 50% (REQUIRED)	310.287 / 608.058 x 100% 51.029 % > 50% (REQUIRED)

B.D. Ref : BD 2/4024/21
BIM Ref : - --
F.S.D. Ref : - --
D.L.O. Ref : - --

Rev.	Description	Drawn	Checked	Approved	Date
-	1st Submission	WY	AW	AL	07/2022
A	2nd Submission	WY	AW	AL	11/2022
B	1st Amendment	TWM	AW	AL	04/2023
C	2nd Amendment	TWM	AW	AL	12/2023
D	3rd Amendment	TWM	AW	AL	04/2024
D	3rd Amendment	TWM	AW	AL	05/2024
	(Re-submission)				
E	5th Amendment	TWM	AW	AL	12/2024
E	5th Amendment	TWM	AW	AL	02/2025
	(Re-submission)				
F	8th Amendment	TWM	AW	AL	05/2025
G	9th Amendment	TWM	AW	AL	08/2025
G	9th Amendment	TWM	AW	AL	10/2025
	(Re-submission)				
H	10th Amendment	TWM	AW	AL	12/2025
I	11th Amendment	TWM	AW	AL	02/2026

Type II works
The works shown on these plans are Type II works (Building Amendment) in respect of which consent is applied for the purpose of Fast Track consent application under regulation 33 of the Building (Administration) Regulations.

RONALD LU
& PARTNERS

呂元祥建築師事務所

Project Title :
PROPOSED DEVELOPMENT
AT BAILEY STREET
& WING KWONG STREET
TO KWA WAN, KOWLOON

Drawing Title :
ROOF FLOOR PLAN
FOR TOWER 1 & TOWER 2

Drawn By	TWM	Date	08/2025
Checked By	AW	Date	08/2025
Approved By	AL	Date	08/2025
Project No.	21163KL	Issue Date	08/2025

File Path :
U:\Studio_B\Proj_Data\2021\21163KL_Bailey Street & Wing Kwong Street\DRAWING\SUB\BD\GBP_13 (Final Amendment)_Hand Amend\PLOT\A_GBP_13.dwg

Scale 1:100 By CAD

Drawing Number : A/GBP/13
Revision Number : I

Drawing Purpose
Buildings Department
Amended Plan

Digitally signed by
LEUNG Kit Man Andy
AP(A) 80/85
16 March 2026

Received on
16 March 2026

Plan Approved
(Digitally Signed)
TSOI Lap-san, Lapson
Senior Building Surveyor
for BUILDING AUTHORITY
17 March 2026

Note: This plan has been processed on a curtailed check basis under the centralized processing system as promulgated in PNAP ADM-19. The duties of the authorized person, registered structural engineer and/or registered geotechnical engineer concerned as specified under section 4(3)(b) and the provision of section 14(2)(c) of the Buildings Ordinance are of particular relevance in this regard.

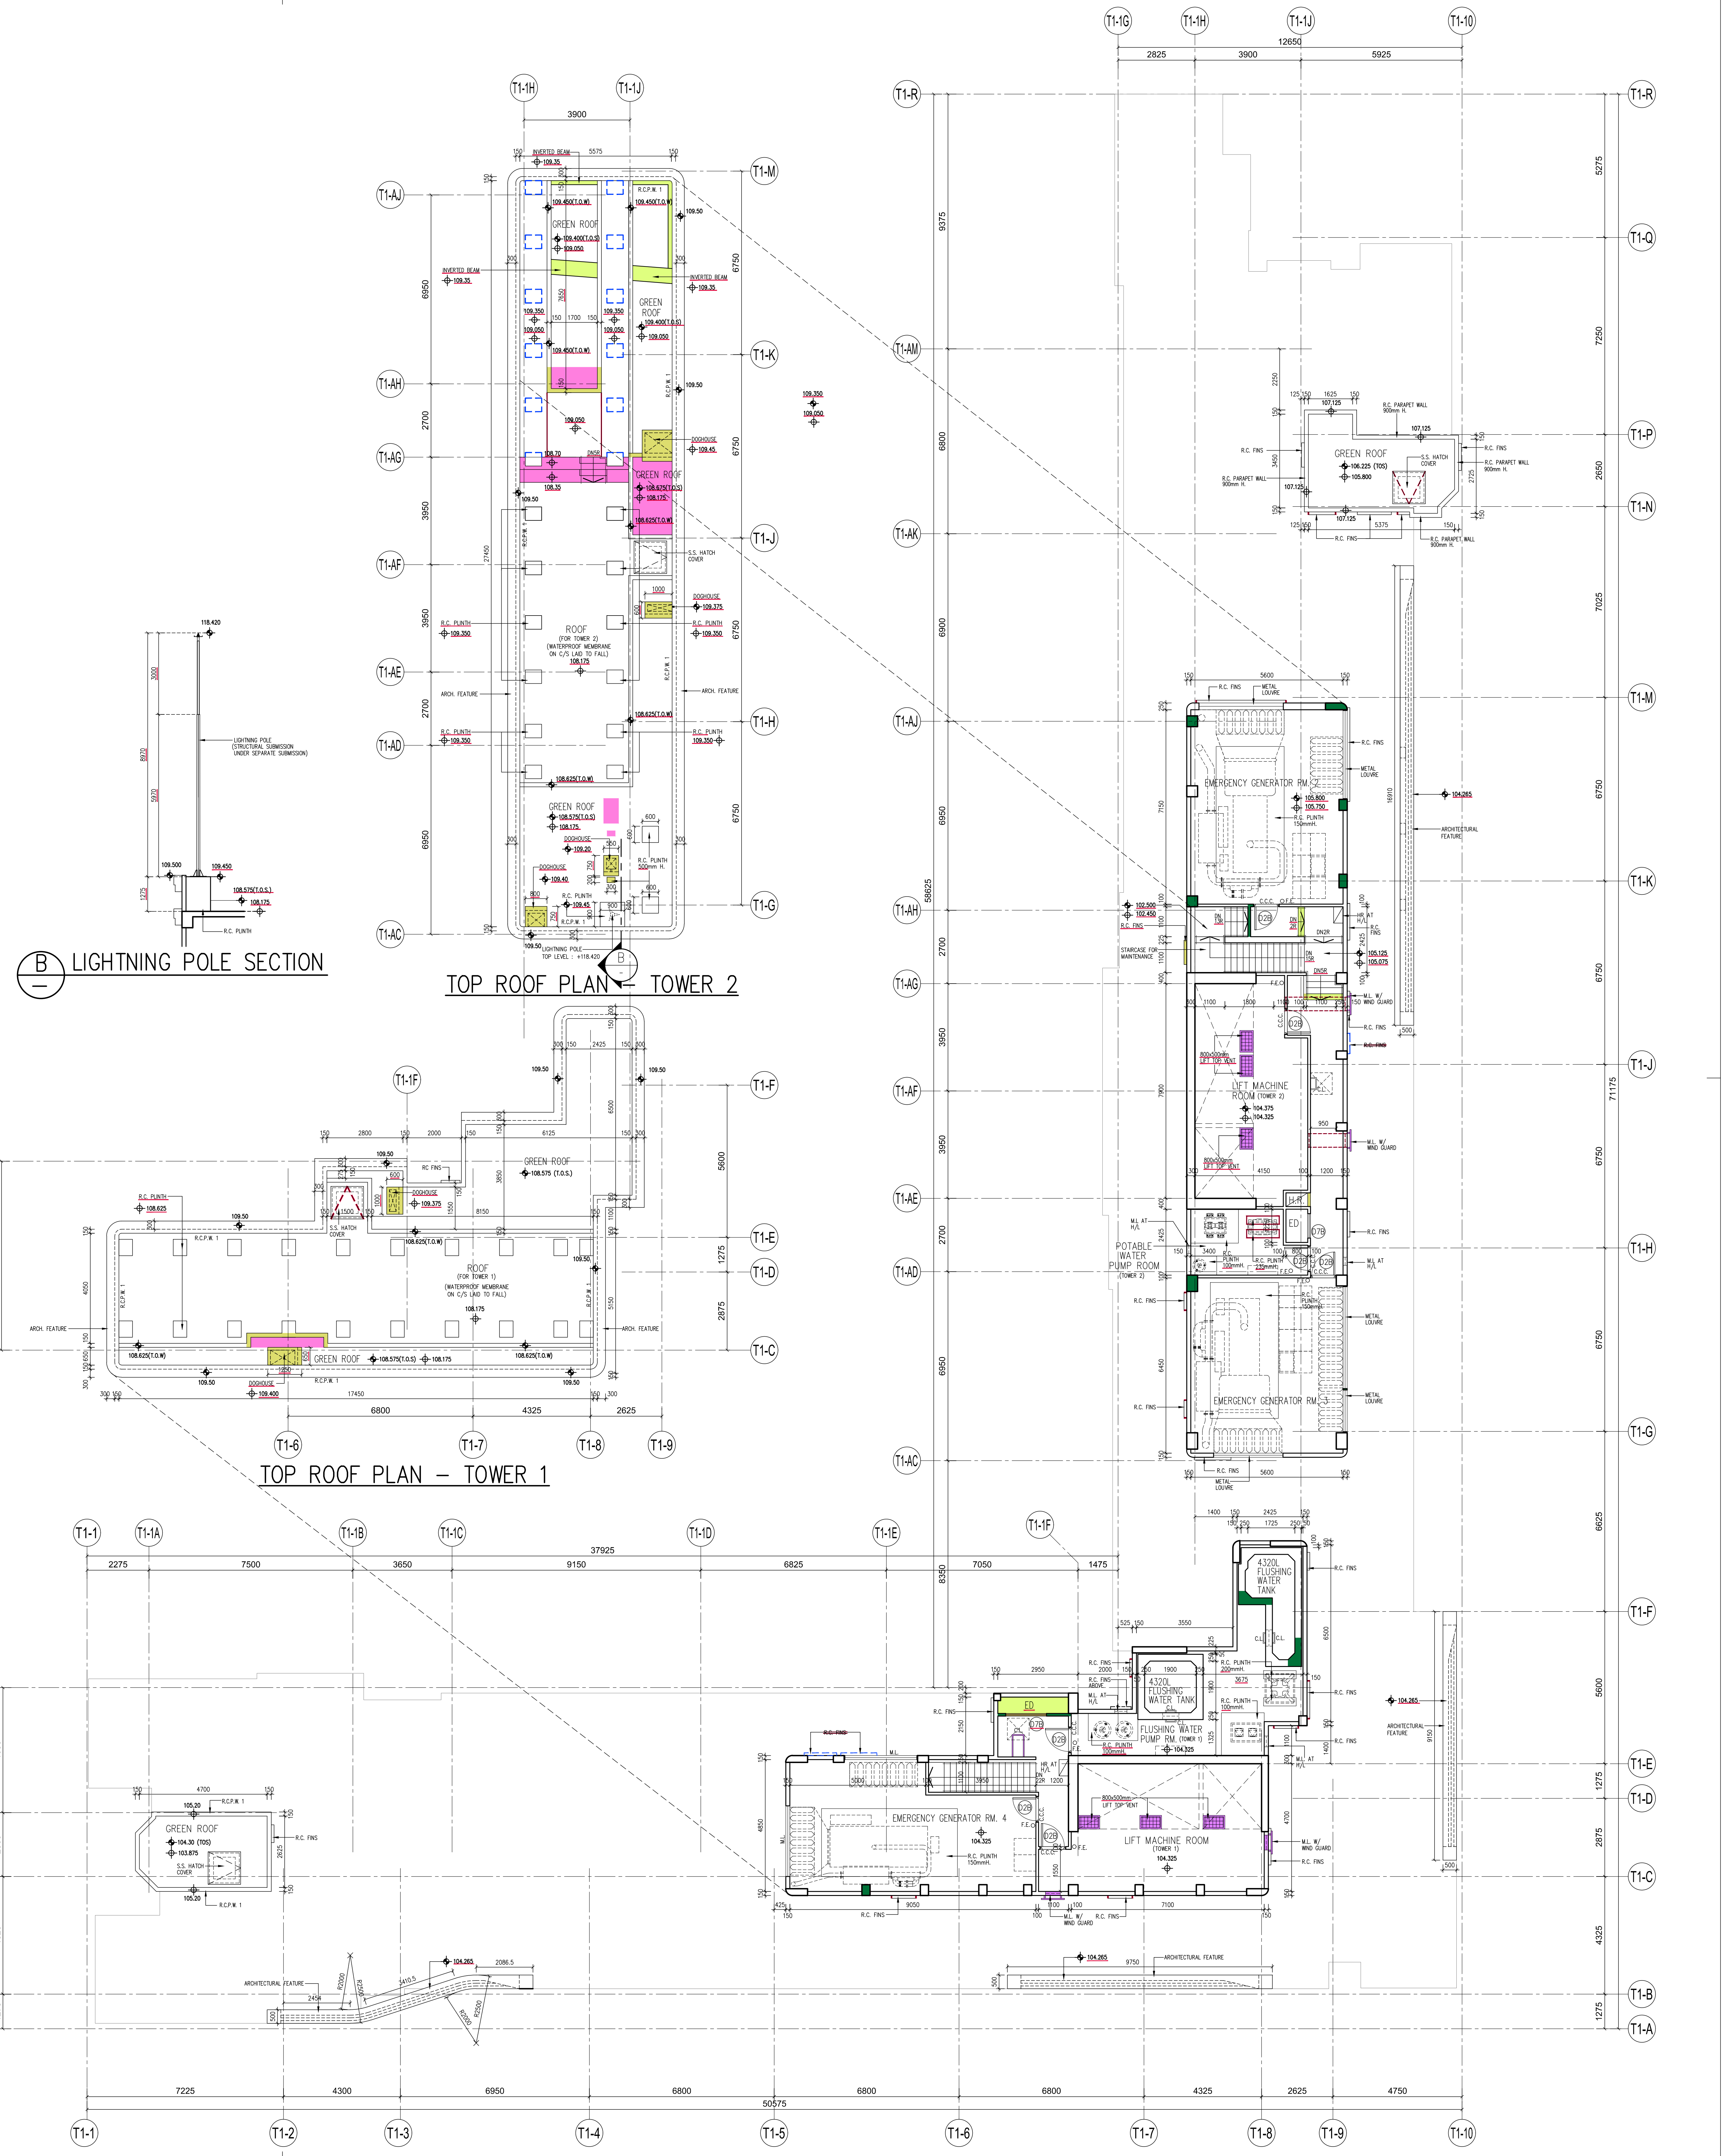

B LIGHTNING POLE SECTION
TOP ROOF PLAN – TOWER 2
TOP ROOF PLAN – TOWER 1
UPPER ROOF PLAN – TOWER 1 & TOWER 2
GREEN ROOF
ROOF (FOR TOWER 2) (WATERPROOF MEMBRANE ON C/S LAID TO FALL)
ROOF (FOR TOWER 1) (WATERPROOF MEMBRANE ON C/S LAID TO FALL)
DOGHOUSE
R.C. PLINTH
S.S. HATCH COVER
INVERTED BEAM
ARCH. FEATURE
LIGHTNING POLE (STRUCTURAL SUBMISSION UNDER SEPARATE SUBMISSION)
EMERGENCY GENERATOR RM. 3
EMERGENCY GENERATOR RM. 4
LIFT MACHINE ROOM (TOWER 2)
LIFT MACHINE ROOM (TOWER 1)
POTABLE WATER PUMP ROOM (TOWER 2)
4320L FLUSHING WATER TANK
FLUSHING WATER PUMP RM. (TOWER 1)
R.C. FINS
METAL LOUVRE
R.C. PARAPET WALL 900mm H.
ARCHITECTURAL FEATURE
STAIRCASE FOR MAINTENANCE
W.L. W/ WIND GUARD

B.D. Ref : BD 2/4024/21

BIM Ref : - --

F.S.D. Ref : - --

D.L.O. Ref : - --

Rev.	Description	Drawn	Checked	Approved	Date
-	1st Submission	WY	AW	AL	07/2022
A	2nd Submission	WY	AW	AL	11/2022
B	1st Amendment	TWM	AW	AL	04/2023
C	2nd Amendment	TWM	AW	AL	12/2023
D	3rd Amendment	TWM	AW	AL	04/2024
D	3rd Amendment (Re-submission)	TWM	AW	AL	05/2024
E	5th Amendment	TWM	AW	AL	12/2024
E	5th Amendment (Re-submission)	TWM	AW	AL	02/2025
F	8th Amendment	TWM	AW	AL	05/2025
G	9th Amendment	TWM	AW	AL	08/2025
G	9th Amendment (Re-submission)	TWM	AW	AL	10/2025
H	10th Amendment	TWM	AW	AL	12/2025
I	11th Amendment	TWM	AW	AL	02/2026

Type II works
The works shown on these plans are Type II works (Building Amendment) in respect of which consent is applied for the purpose of Fast Track consent application under regulation 33 of the Building (Administration) Regulations.

RONALD LU & PARTNERS

呂 元 祥 建 築 師 事 務 所

Project Title :
PROPOSED DEVELOPMENT
AT BAILEY STREET
& WING KWONG STREET
TO KWA WAN, KOWLOON

Drawing Title :
UPPER ROOF FLOOR PLAN
FOR TOWER 1 & TOWER 2

Drawn By	TWM	Date	08/2025
Checked By	AW	Date	08/2025
Approved By	AL	Date	08/2025
Project No.	21163KL	Issue Date	08/2025

File Path :
U:\Studio_B\Proj_Data\2021\21163KL_Bailey Street & Wing Kwong Street\DRAWING\SUB\BD\GBP_13 (Final Amendment)_Hand Amend\PLOT\A_GBP_14.dwg

Scale 1:100 By CAD

Drawing Number : A/GBP/14

Revision Number : I

Drawing Purpose

Buildings Department
Amended Plan

Digitally signed by
LEUNG Kit Man Andy
AP(A) 80/85
16 March 2026

Received on
16 March 2026

Plan Approved
(Digitally Signed)
TSOI Lap-san, Lapson
Senior Building Surveyor
for BUILDING AUTHORITY
17 March 2026

Note: This plan has been processed on a curtailed check basis under the centralized processing system as promulgated in PNAP ADM-19. The duties of the authorized person, registered structural engineer and/or registered geotechnical engineer concerned as specified under section 4(3)(b) and the provision of section 14(2)(c) of the Buildings Ordinance are of particular relevance in this regard.

SLIDING PANEL SCHEDULE

TOWER 3		
FLAT	ROOM	FLOOR
D	LIV./DIN.#2	3/F–30/F
	B.R.1#1 #3	
	M.B.R.#3	
E	LIV./DIN.#2	3/F–30/F
	B.R.1#1 #3	
	M.B.R.#3	
F	LIV./DIN.#2	10/F–30/F
	M.B.R.#3	
	B.R.1 #3	11/F–30/F
G	LIV./DIN.#2	15/F–30/F
	M.B.R.#3	17/F–26/F
	B.R.1 #3	11/F–30/F

#1 : WITH SOUND ABSORPTIVE MATERIAL
#2 : ACOUSTIC DOOR
#3 : ACOUSTIC WIDNOW

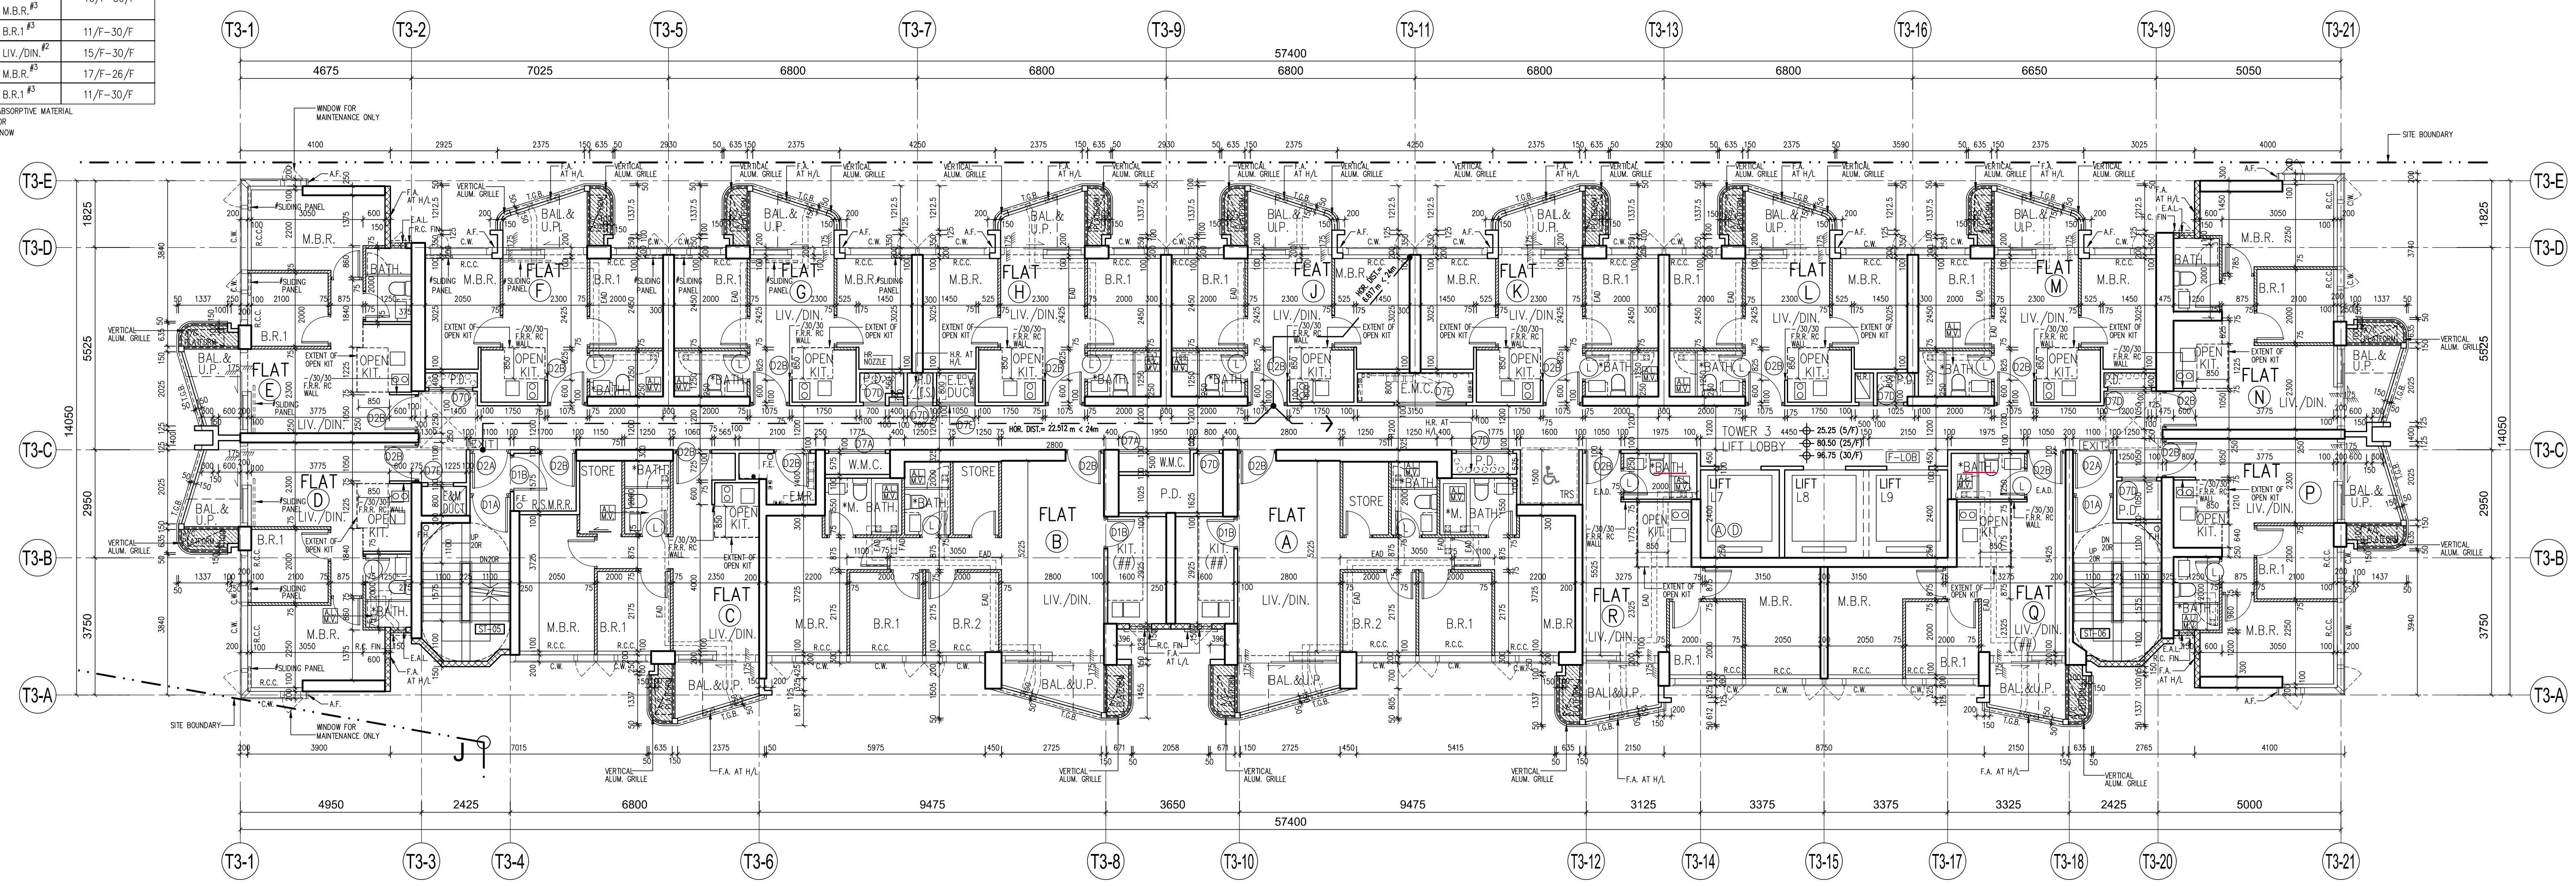
T3-1
T3-2
T3-5
T3-7
T3-9
T3-11
T3-13
T3-16
T3-19
T3-21
T3-E
T3-D
T3-C
T3-B
T3-A
T3-3
T3-4
T3-6
T3-8
T3-10
T3-12
T3-14
T3-15
T3-17
T3-18
T3-20
57400
4675
7025
6800
6800
6800
6800
6650
5050
4950
2425
6800
9475
3650
9475
3125
3375
3375
3325
2425
5000
1825
5525
2950
3750
14050
FLAT A
FLAT B
FLAT C
FLAT D
FLAT E
FLAT F
FLAT G
FLAT H
FLAT J
FLAT K
FLAT L
FLAT M
FLAT N
FLAT P
FLAT Q
FLAT R
LIV./DIN.
M.B.R.
B.R.1
B.R.2
BAL. & U.P.
OPEN KIT.
STORE
LIFT L7
LIFT L8
LIFT L9
TOWER 3 LIFT LOBBY
SITE BOUNDARY
VERTICAL ALUM. GRILLE
WINDOW FOR MAINTENANCE ONLY

5TH TO 30TH FLOOR PLAN – TOWER 3 (23 STOREYS)

NOTE:
1. MECHANICAL VENTILATION AND ARTIFICIAL LIGHTING WILL BE PROVIDED AT THE BATHROOM/ LAVATORY MARKED WITH " * " FOR OMISSION OF NATURAL LIGHTING AND VENTILATION.
2. THERE WILL BE NO 13/F, 14/F & 24/F IN THE NOMENCLATURE SYSTEM FOR NUMBERING OF FLOORS.
3. SLIDING PANEL TO BE PROVIDED AT WHICH MARKED WITH "#" (REFER TO SLIDING PANEL SCHEDULE DWG. NO. A/GBP/19)
4. LIGHTING AND VENTILATION PROVISION TO ADOPT PERFORMANCE–BASED APPROACH FOR THE ROOM MARKED WITH (##) (REFER DWG. NO. A/GBP/10)
5. 5 ACH MECHANICAL VENTILATION SHALL BE PROVIDED TO KITCHENS USING UVA METHOD.

LEGEND:

▨ A/C PLATFORM

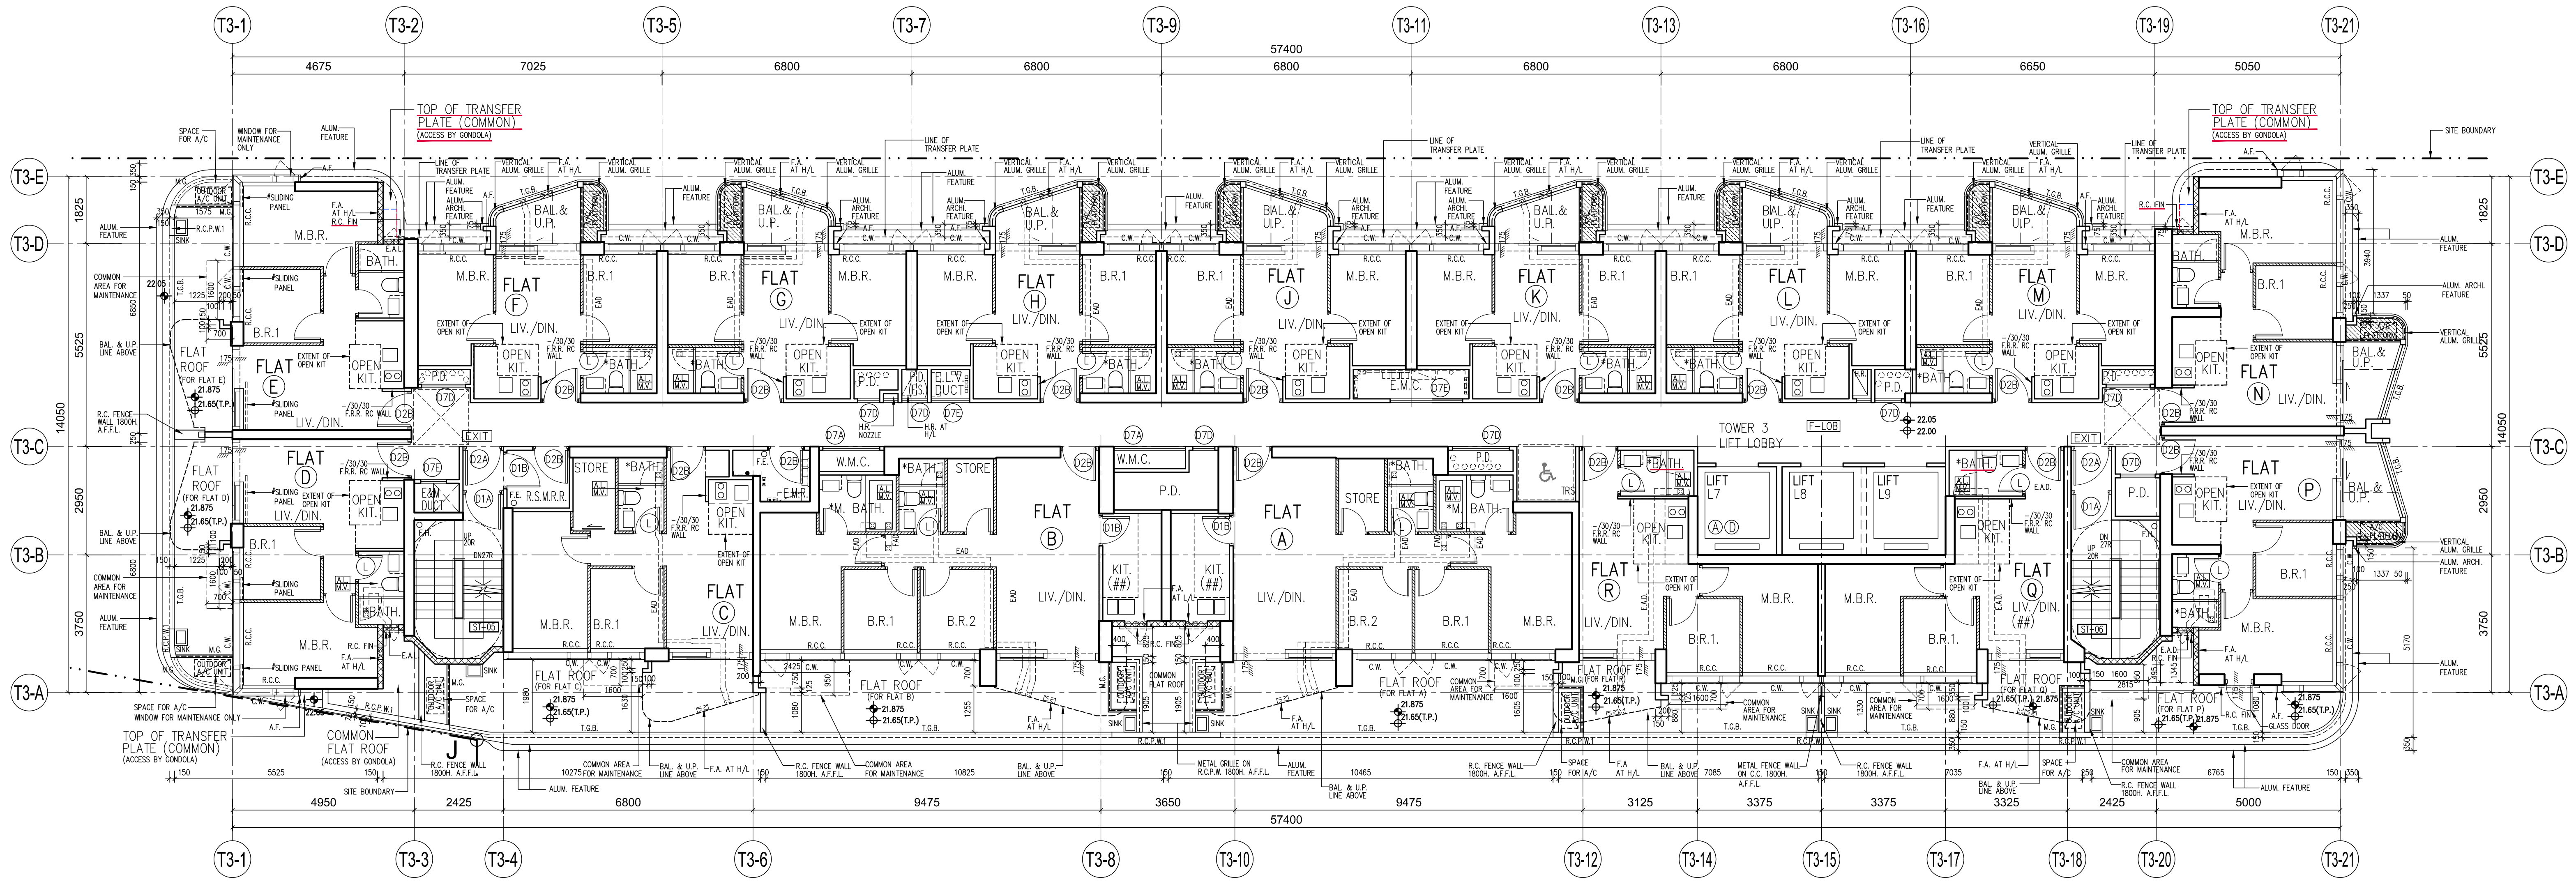
T3-1
T3-2
T3-5
T3-7
T3-9
T3-11
T3-13
T3-16
T3-19
T3-21
T3-E
T3-D
T3-C
T3-B
T3-A
T3-3
T3-4
T3-6
T3-8
T3-10
T3-12
T3-14
T3-15
T3-17
T3-18
T3-20
57400
TOP OF TRANSFER PLATE (COMMON) (ACCESS BY GONDOLA)
FLAT ROOF
COMMON FLAT ROOF
TOWER 3 LIFT LOBBY
LIFT L7
LIFT L8
LIFT L9
SITE BOUNDARY
BAL. & U.P. LINE ABOVE
R.C. FENCE WALL 1800H. A.F.F.L.
METAL GRILLE ON R.C.P.W. 1800H. A.F.F.L.
ALUM. FEATURE
SPACE FOR A/C
10825
10465

3RD FLOOR PLAN – TOWER 3

NOTE:
1. MECHANICAL VENTILATION AND ARTIFICIAL LIGHTING WILL BE PROVIDED AT THE BATHROOM/ LAVATORY MARKED WITH " * " FOR OMISSION OF NATURAL LIGHTING AND VENTILATION.
2. ALL DIMENSION ARE SAME AS 5/F – 30/F, EXCEPT OTHERWISE NOTED.
3. SLIDING PANEL TO BE PROVIDED AT WHICH MARKED WITH "#" (REFER TO SLIDING PANEL SCHEDULE DWG. NO. A/GBP/19)
4. LIGHTING AND VENTILATION PROVISION TO ADOPT PERFORMANCE–BASED APPROACH FOR THE ROOM MARKED WITH (##) (REFER DWG. NO. A/GBP/10)
5. 5 ACH MECHANICAL VENTILATION SHALL BE PROVIDED TO KITCHENS USING UVA METHOD.

LEGEND:

▨ A/C PLATFORM

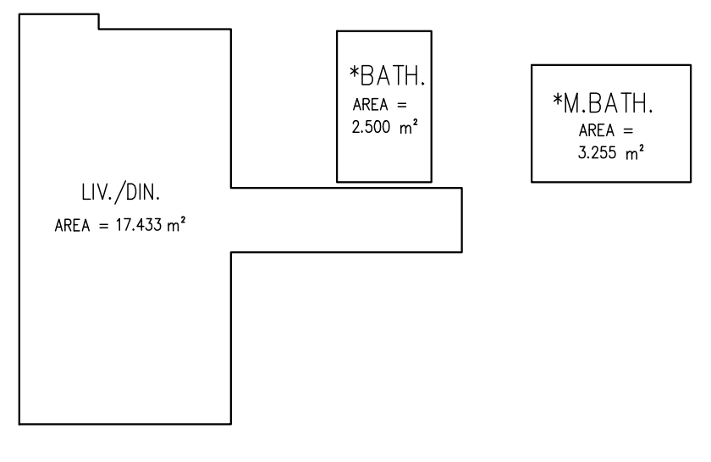
LIV./DIN.
AREA = 17.433 m²
*BATH.
AREA = 2.500 m²
*M.BATH.
AREA = 3.255 m²

3/F – 30/F FLAT A (LIV./DIN. & BATH. & M.BATH.) ROOM AREA

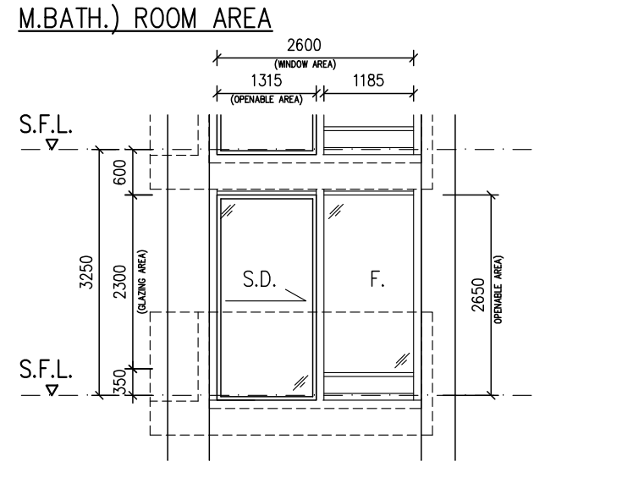
S.F.L.
S.D.
F.
3250
2300 (GLAZING AREA)
2650 (OPENABLE AREA)
350
600
2600

WINDOW AREA CALCULATION
FOR FLAT A (LIV./DIN. & BATH. & M.BATH.)
(FOR FLAT B TO H, J TO N & P (LIV./DIN. & BATH. & M.BATH.))

ROOM AREA = 17.433 s.m.

WINDOW AREA REQ'D = 17.433 / 10 = 1.743 s.m.
WINDOW AREA PROV'D = (2.600 x 2.300 x 0.70)
= 4.186 s.m. > 1.743 s.m. (REQUIRED)

OPENABLE WINDOW AREA REQ'D = 17.433 /16 + 2.500 /10 + 3.255 /10 = 1.665 s.m.
OPENABLE WINDOW AREA PROV'D = 1.315 x 2.650 x 0.70
= 2.439 s.m. > 1.665 s.m. (REQUIRED)

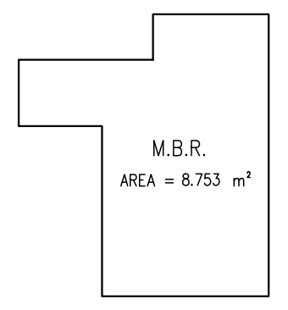
M.B.R.
AREA = 8.753 m²

3/F – 30/F FLAT A (M.B.R. & M. BATH.) ROOM AREA

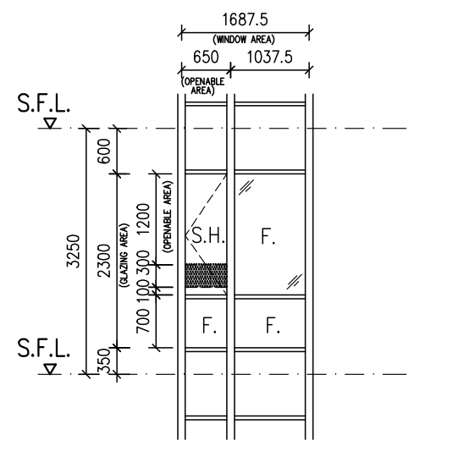
S.F.L.
S.H.
F.
3250
2300 (GLAZING AREA)
1200 (OPENABLE AREA)
1687.5
350
600

WINDOW AREA CALCULATION
FOR FLAT A (M.B.R. & M. BATH.)
(FOR FLAT B (M.B.R. & M. BATH.))

ROOM AREA = 8.753 s.m.

WINDOW AREA REQ'D = 8.753 / 10 = 0.875 s.m.
WINDOW AREA PROV'D = (1.6875 x 2.300 x 0.70)
= 2.717 s.m. > 0.875 s.m. (REQUIRED)

OPENABLE WINDOW AREA REQ'D = 8.753 /16 = 0.547 s.m.
OPENABLE WINDOW AREA PROV'D = 0.650 x (1.200 + 0.10) x 0.8
= 0.676 s.m. > 0.547 s.m. (REQUIRED)

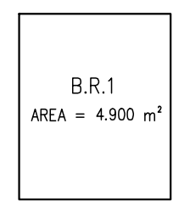
B.R.1
AREA = 4.900 m²

3/F – 30/F FLAT F (B.R.1) ROOM AREA

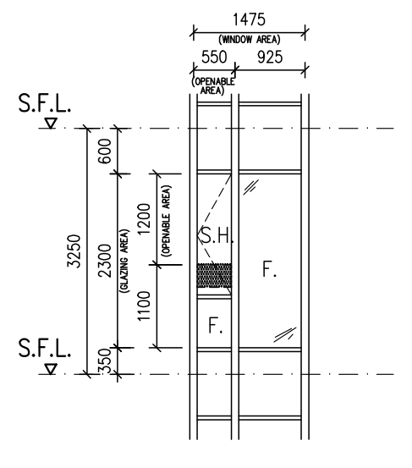
S.F.L.
S.H.
F.
3250
2300 (GLAZING AREA)
1200 (OPENABLE AREA)
1100
1475
350
600

WINDOW AREA CALCULATION
FOR FLAT F (B.R.1)
(FOR FLAT A TO E, G, H, J TO N & P (B.R.1))
(FOR FLAT A TO H, J TO N & P (M.B.R. & M. BATH.))

ROOM AREA = 4.900 s.m.

WINDOW AREA REQ'D = 4.900 / 10 = 0.490 s.m.
WINDOW AREA PROV'D = (1.475 x 2.300 x 0.70)
= 2.375 s.m. > 0.490 s.m. (REQUIRED)

OPENABLE WINDOW AREA REQ'D = 4.900 /16 = 0.306 s.m.
OPENABLE WINDOW AREA PROV'D = 0.550 x 1.200 x 0.70
= 0.462 s.m. > 0.306 s.m. (REQUIRED)

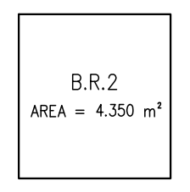
B.R.2
AREA = 4.350 m²

3/F – 30/F FLAT A (B.R.2) ROOM AREA

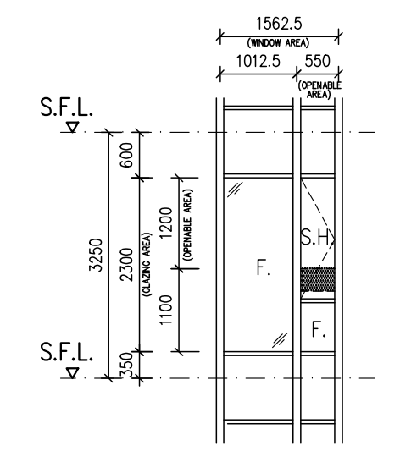
S.F.L.
S.H.
F.
3250
2300 (GLAZING AREA)
1200 (OPENABLE AREA)
1100
1562.5
350
600

WINDOW AREA CALCULATION
FOR FLAT A (B.R.2)
(FOR FLAT B (B.R.2))

ROOM AREA = 4.350 s.m.

WINDOW AREA REQ'D = 4.350 / 10 = 0.435 s.m.
WINDOW AREA PROV'D = (1.5625 x 2.300 x 0.70)
= 2.516 s.m. > 0.435 s.m. (REQUIRED)

OPENABLE WINDOW AREA REQ'D = 4.350 /16 = 0.272 s.m.
OPENABLE WINDOW AREA PROV'D = 0.550 x 1.200 x 0.70
= 0.462 s.m. > 0.272 s.m. (REQUIRED)

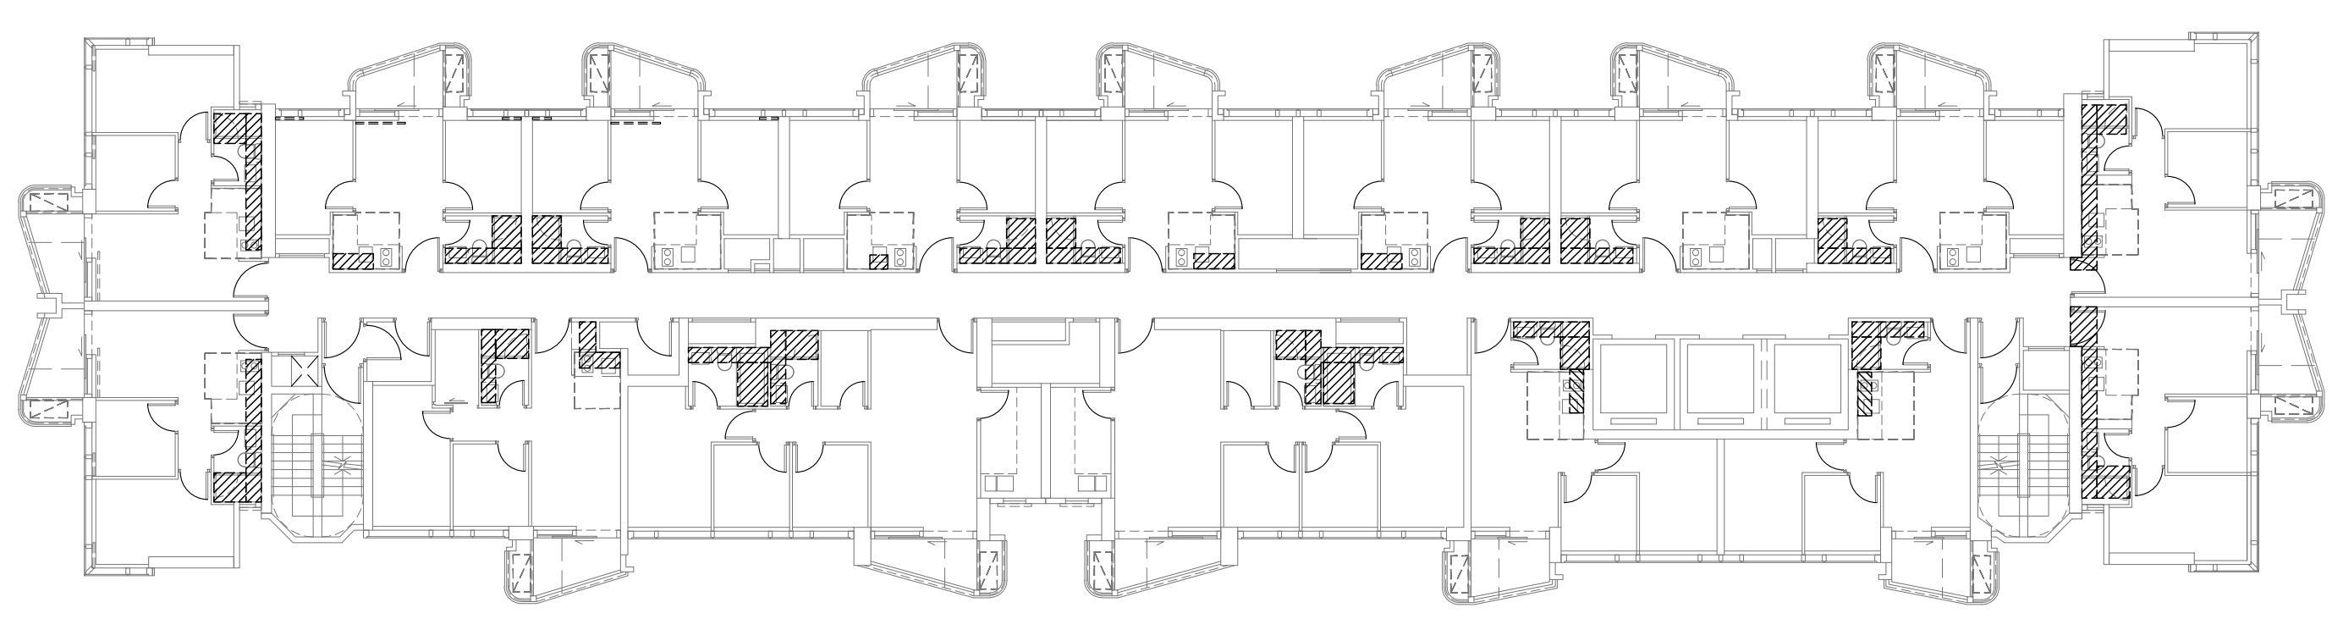

DIAGRAM OF SUNKEN SLAB EXTENT (5th TO 30th FLOOR)

SCALE 1:200

LEGEND:

▨ SUNKEN SLAB

B.D. Ref : BD 2/4024/21
BIM Ref : - --
F.S.D. Ref : - --
D.L.O. Ref : - --

Rev.	Description	Drawn	Checked	Approved	Date
-	1st Submission	WY	AW	AL	07/2022
A	2nd Submission	WY	AW	AL	11/2022
B	1st Amendment	TWM	AW	AL	04/2023
C	2nd Amendment	TWM	AW	AL	12/2023
D	3rd Amendment	TWM	AW	AL	04/2024
D	3rd Amendment (Re-submission)	TWM	AW	AL	05/2024
E	5th Amendment	TWM	AW	AL	12/2024
E	5th Amendment (Re-submission)	TWM	AW	AL	02/2025
F	6th Amendment	TWM	AW	AL	02/2025
G	8th Amendment	TWM	AW	AL	05/2025
H	9th Amendment	TWM	AW	AL	08/2025
H	9th Amendment (Re-submission)	TWM	AW	AL	10/2025
I	10th Amendment	TWM	AW	AL	12/2025
J	11th Amendment	TWM	AW	AL	02/2026
K	13th Amendment	TWM	AW	AL	06/2026

Type II works
The works shown on these plans are Type II works (Building Amendment) in respect of which consent is applied for the purpose of Fast Track consent application under regulation 33 of the Building (Administration) Regulations.

RONALD LU & PARTNERS
呂 元 祥 建 築 師 事 務 所

Project Title :
PROPOSED DEVELOPMENT
AT BAILEY STREET
& WING KWONG STREET
TO KWA WAN, KOWLOON

Drawing Title :
3RD - 30TH FLOOR PLAN
FOR TOWER 3

Drawn By	TWM	Date	08/2025
Checked By	AW	Date	08/2025
Approved By	AL	Date	08/2025
Project No.	21163KL	Issue Date	08/2025

File Path :
U:\Studio_B\Proj_Data\2021\21163KL_Bailey Street & Wing Kwong Street\DRAWING\SUB\BD\GBP_15_Hand Amend\PLOT\A_GBP_15.dwg

Scale 1:100 By CAD

Drawing Number : A/GBP/15
Revision Number : K

Drawing Purpose
Buildings Department
Amended Plan

Digitally signed by
WONG Chi Kin Kenneth
AP(A) 19/95
08 July 2026

Received on
08 July 2026

Plan Approved
(Digitally Signed)
TSOI Lap-san, Lapson
Senior Building Surveyor
for BUILDING AUTHORITY
08 July 2026

Note: This plan has been processed on a curtailed check basis under the centralized processing system as promulgated in PNAP ADM-19. The duties of the authorized person, registered structural engineer and/or registered geotechnical engineer concerned as specified under section 4(3)(b) and the provision of section 14(2)(c) of the Buildings Ordinance are of particular relevance in this regard.

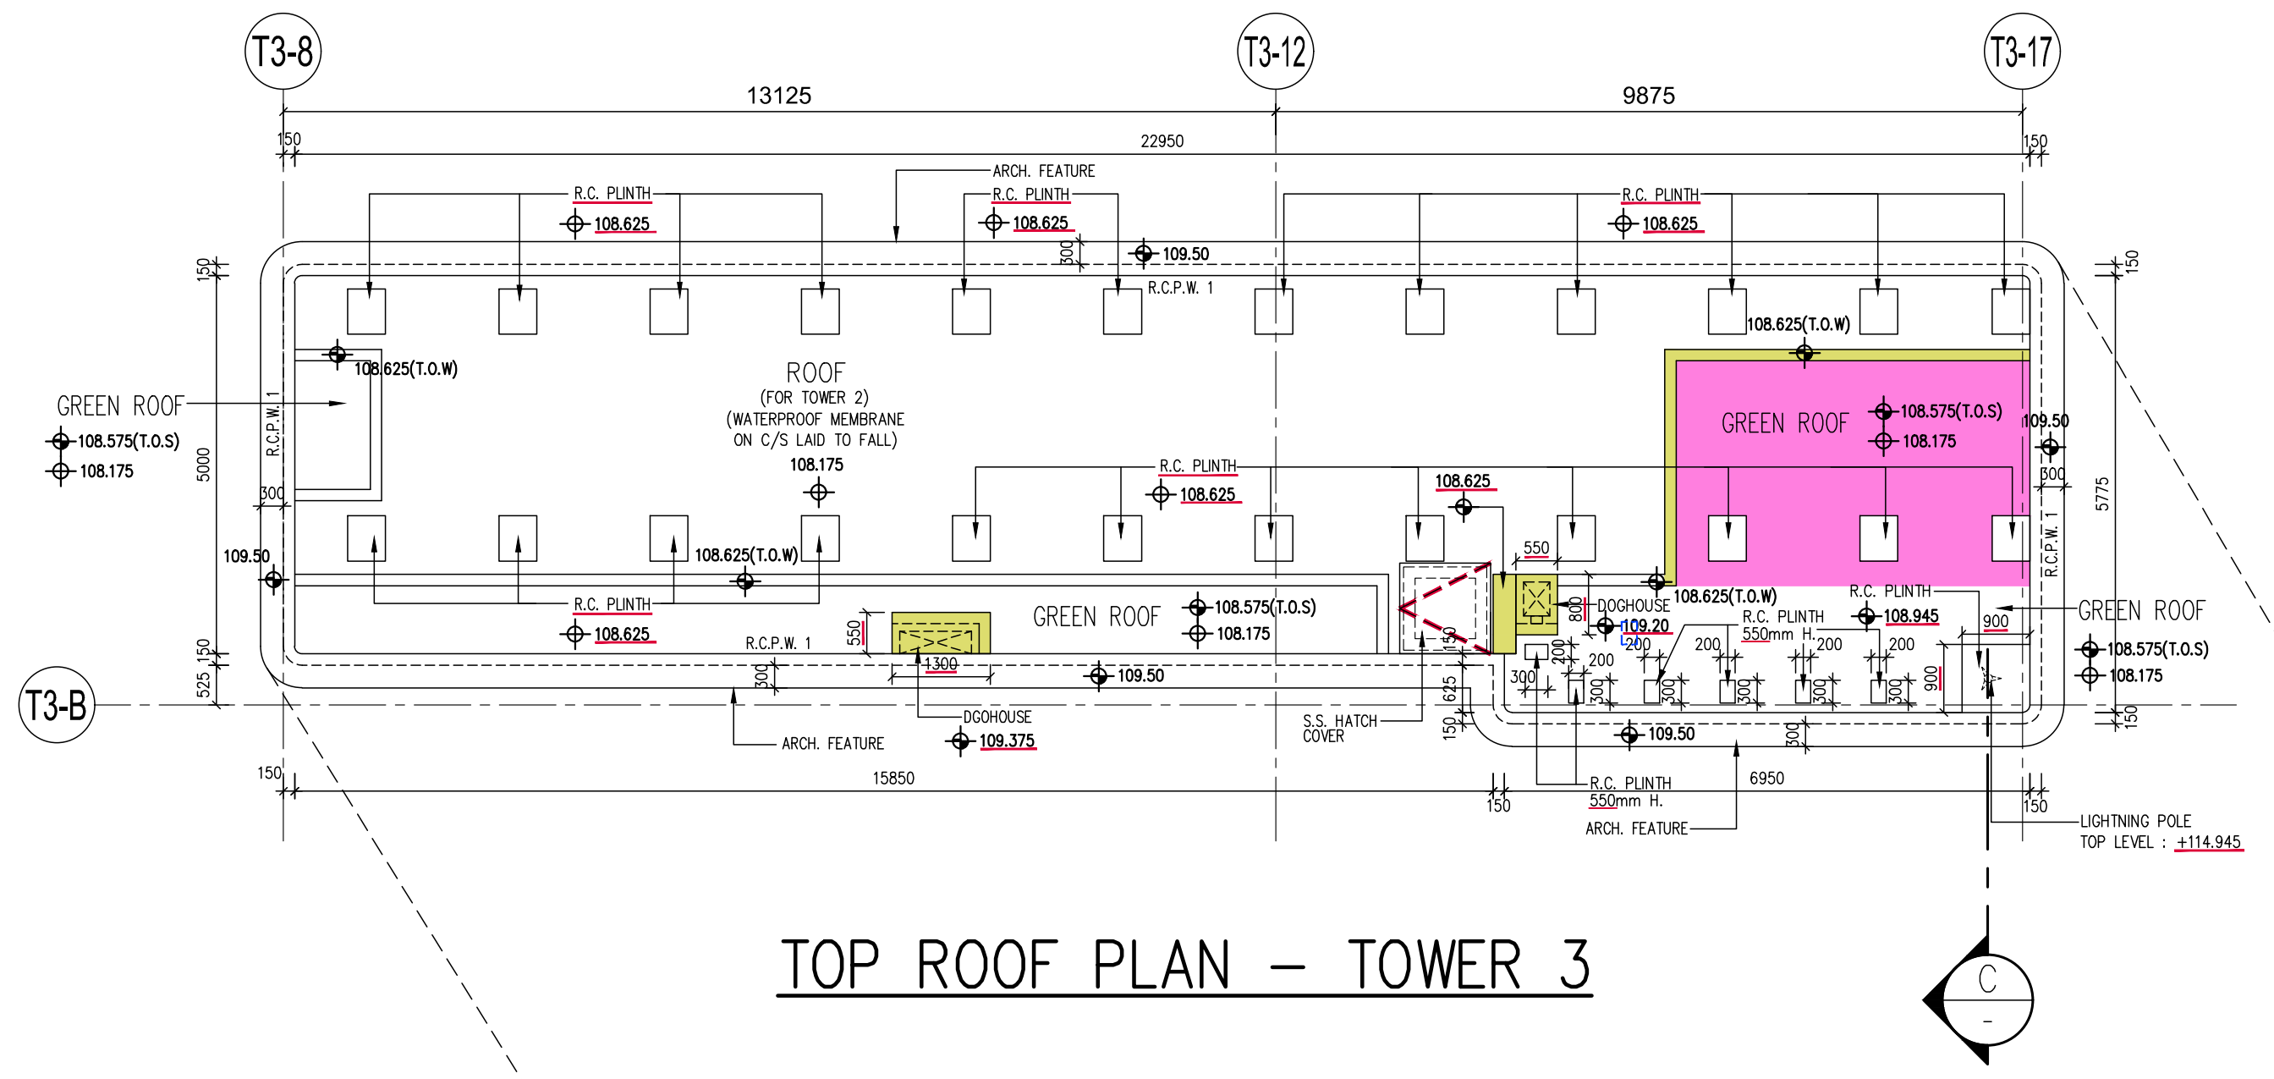
T3-8
T3-12
T3-17
T3-B
13125
9875
22900
GREEN ROOF
ROOF (FOR TOWER 3) (WATERPROOF MEMBRANE ON C/S LAID TO FALL)
GREEN ROOF
GREEN ROOF
GREEN ROOF
ARCH. FEATURE
R.C. PLINTH
LIGHTNING POLE TOP LEVEL : 114.940
C

TOP ROOF PLAN – TOWER 3

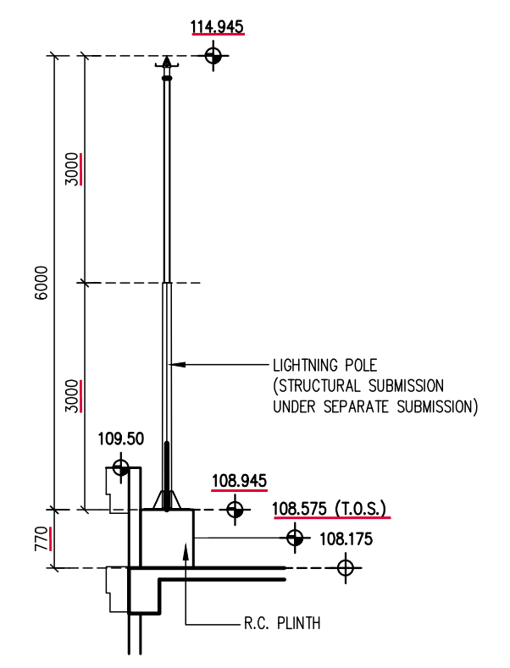
114.940
LIGHTNING POLE (STRUCTURAL SUBMISSION UNDER SEPARATE SUBMISSION)
R.C. PLINTH

C LIGHTNING POLE SECTION

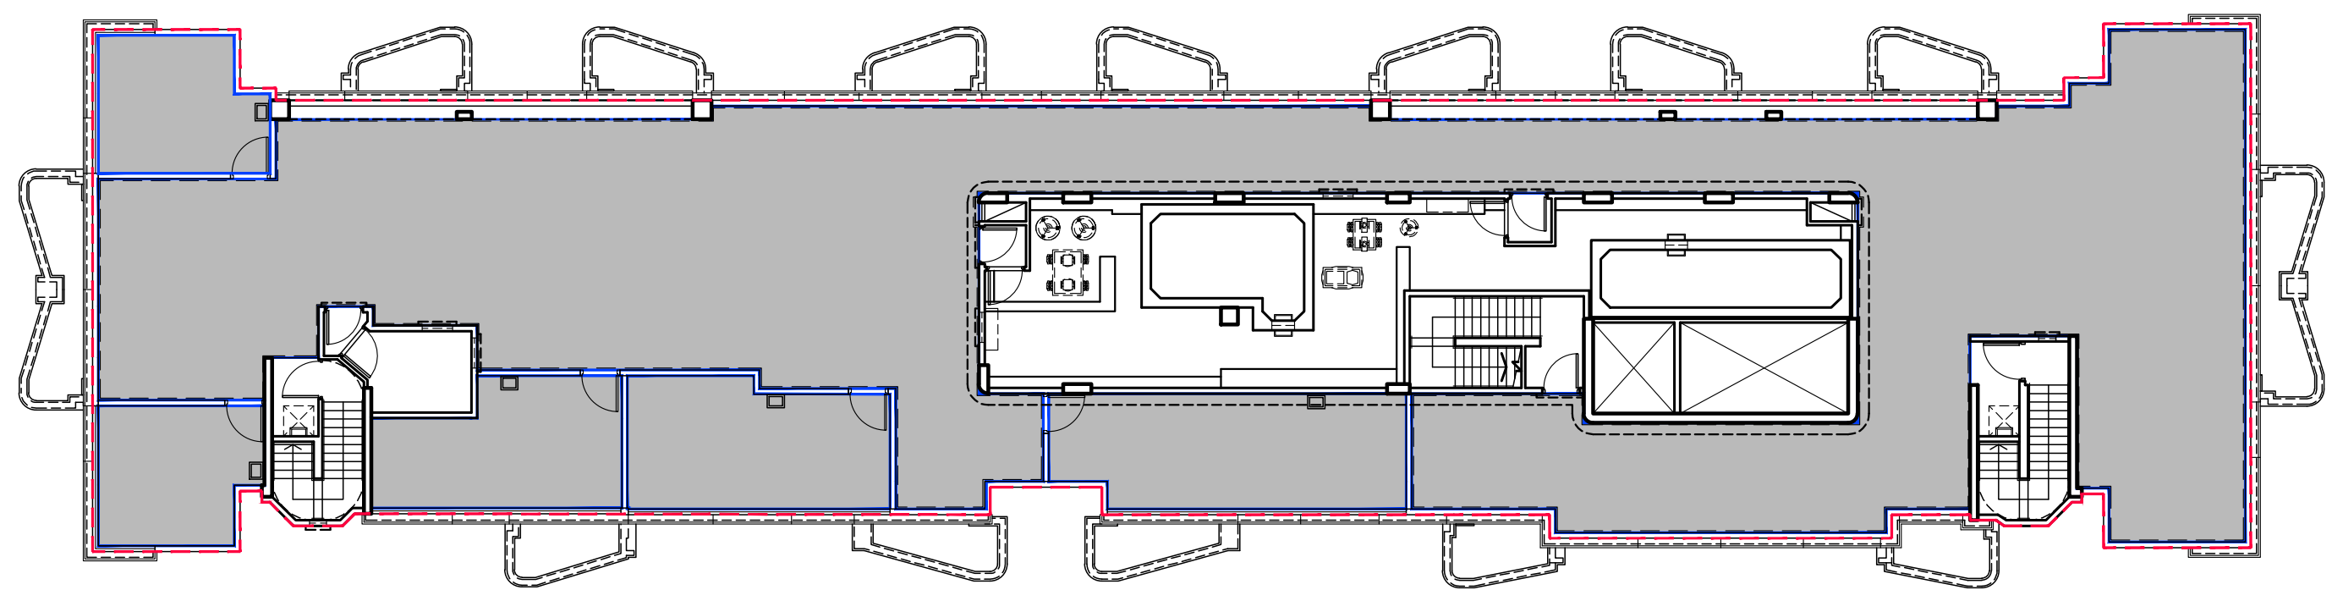

TOWER 3 ROOF FLOOR DIAGRAM

(UNDER PLANNING DEPARTMENT)
SCALE 1:200

— — AREA OF ROOF = 652.004 m²
▨ AREA OF ROOF W/O. ROOF TOP STRUCTURE = 451.783 m² (69.291 % OF ROOF AREA)

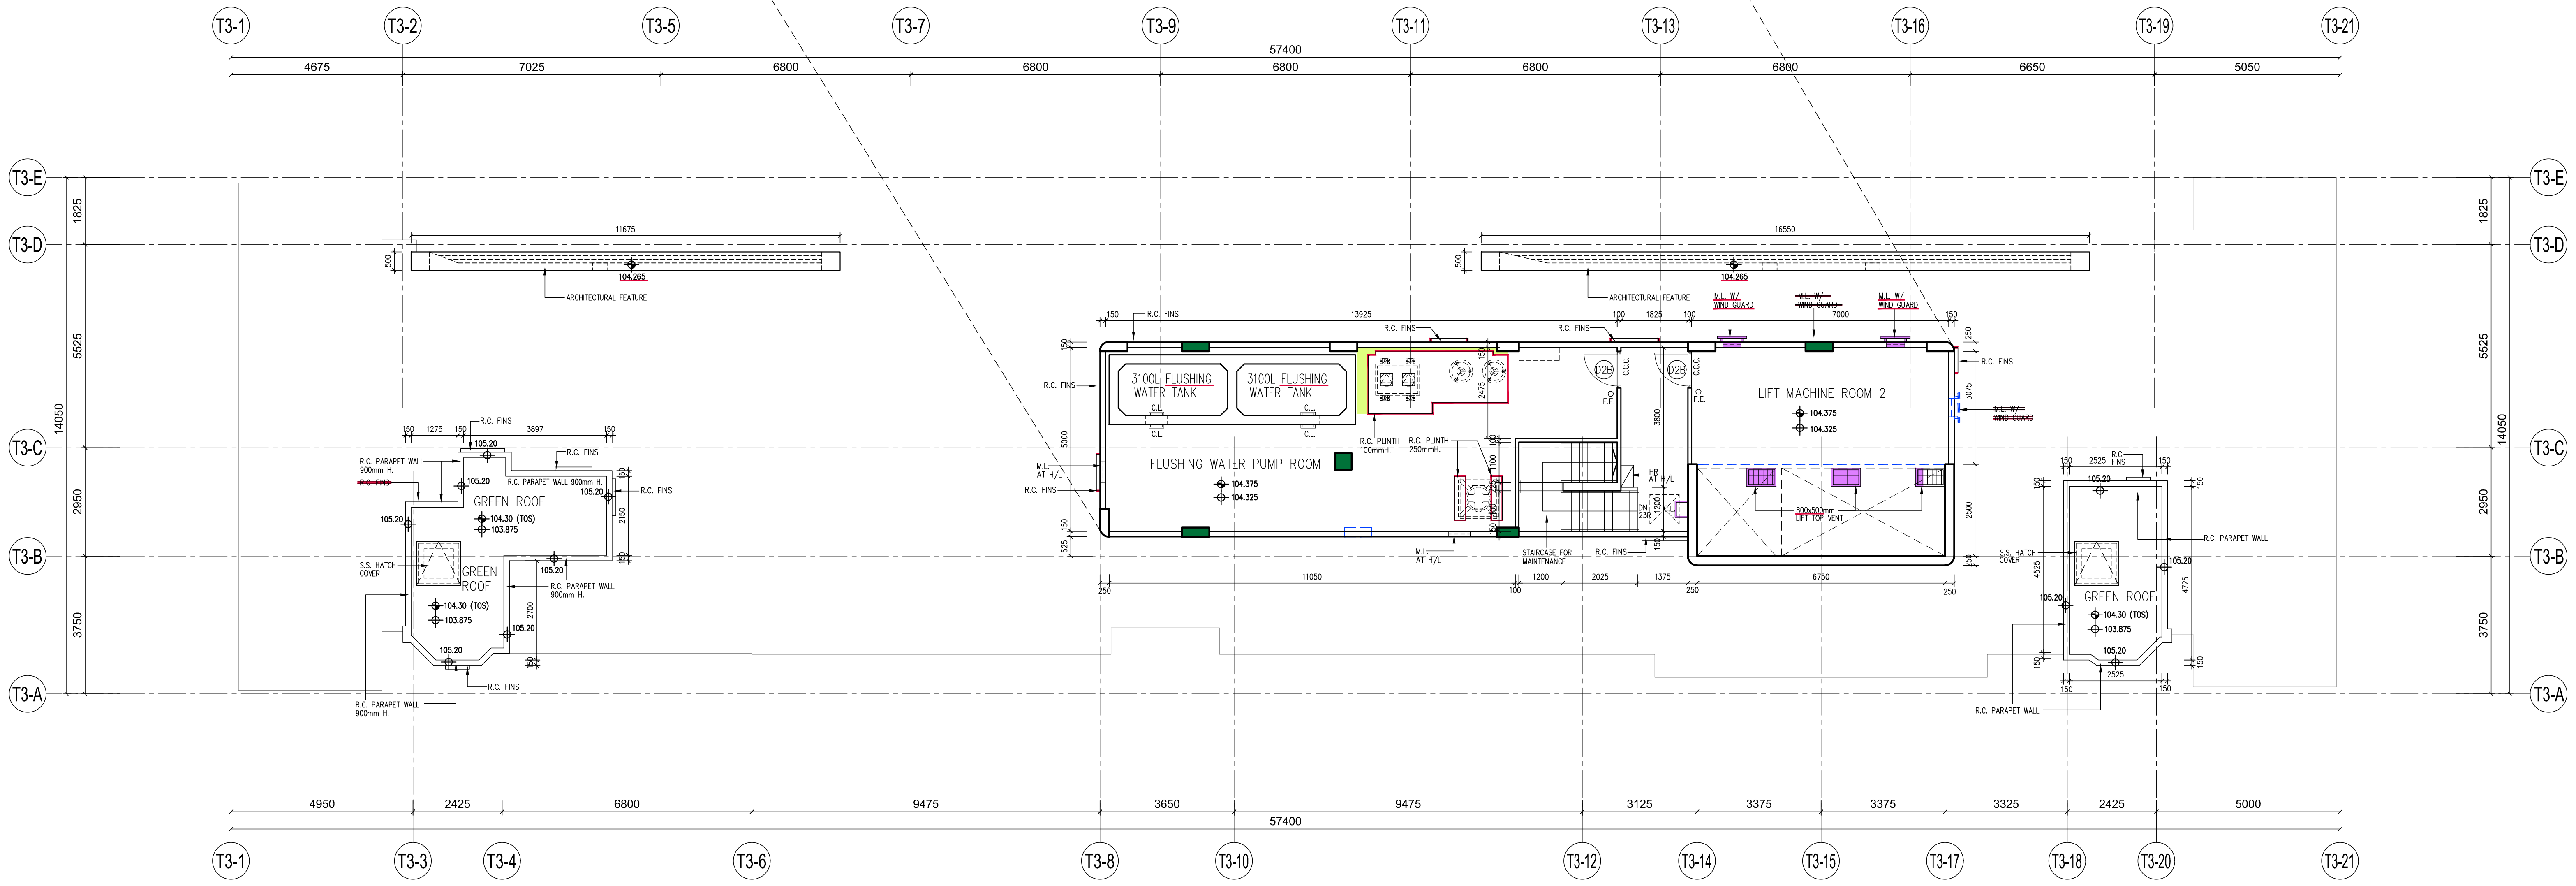
T3-1
T3-2
T3-5
T3-7
T3-9
T3-11
T3-13
T3-16
T3-19
T3-21
4675
7025
6800
6800
6800
6800
6800
6650
5050
57400
T3-E
T3-D
T3-C
T3-B
T3-A
ARCHITECTURAL FEATURE
3100L FLUSHING WATER TANK
3100L FLUSHING WATER TANK
FLUSHING WATER PUMP ROOM
LIFT MACHINE ROOM 2
GREEN ROOF
GREEN ROOF
GREEN ROOF
R.C. FINS
R.C. PARAPET WALL
4950
2425
6800
9475
3650
9475
3125
3375
3375
3325
2425
5000
T3-3
T3-4
T3-6
T3-8
T3-10
T3-12
T3-14
T3-15
T3-17
T3-18
T3-20

UPPER ROOF PLAN – TOWER 3

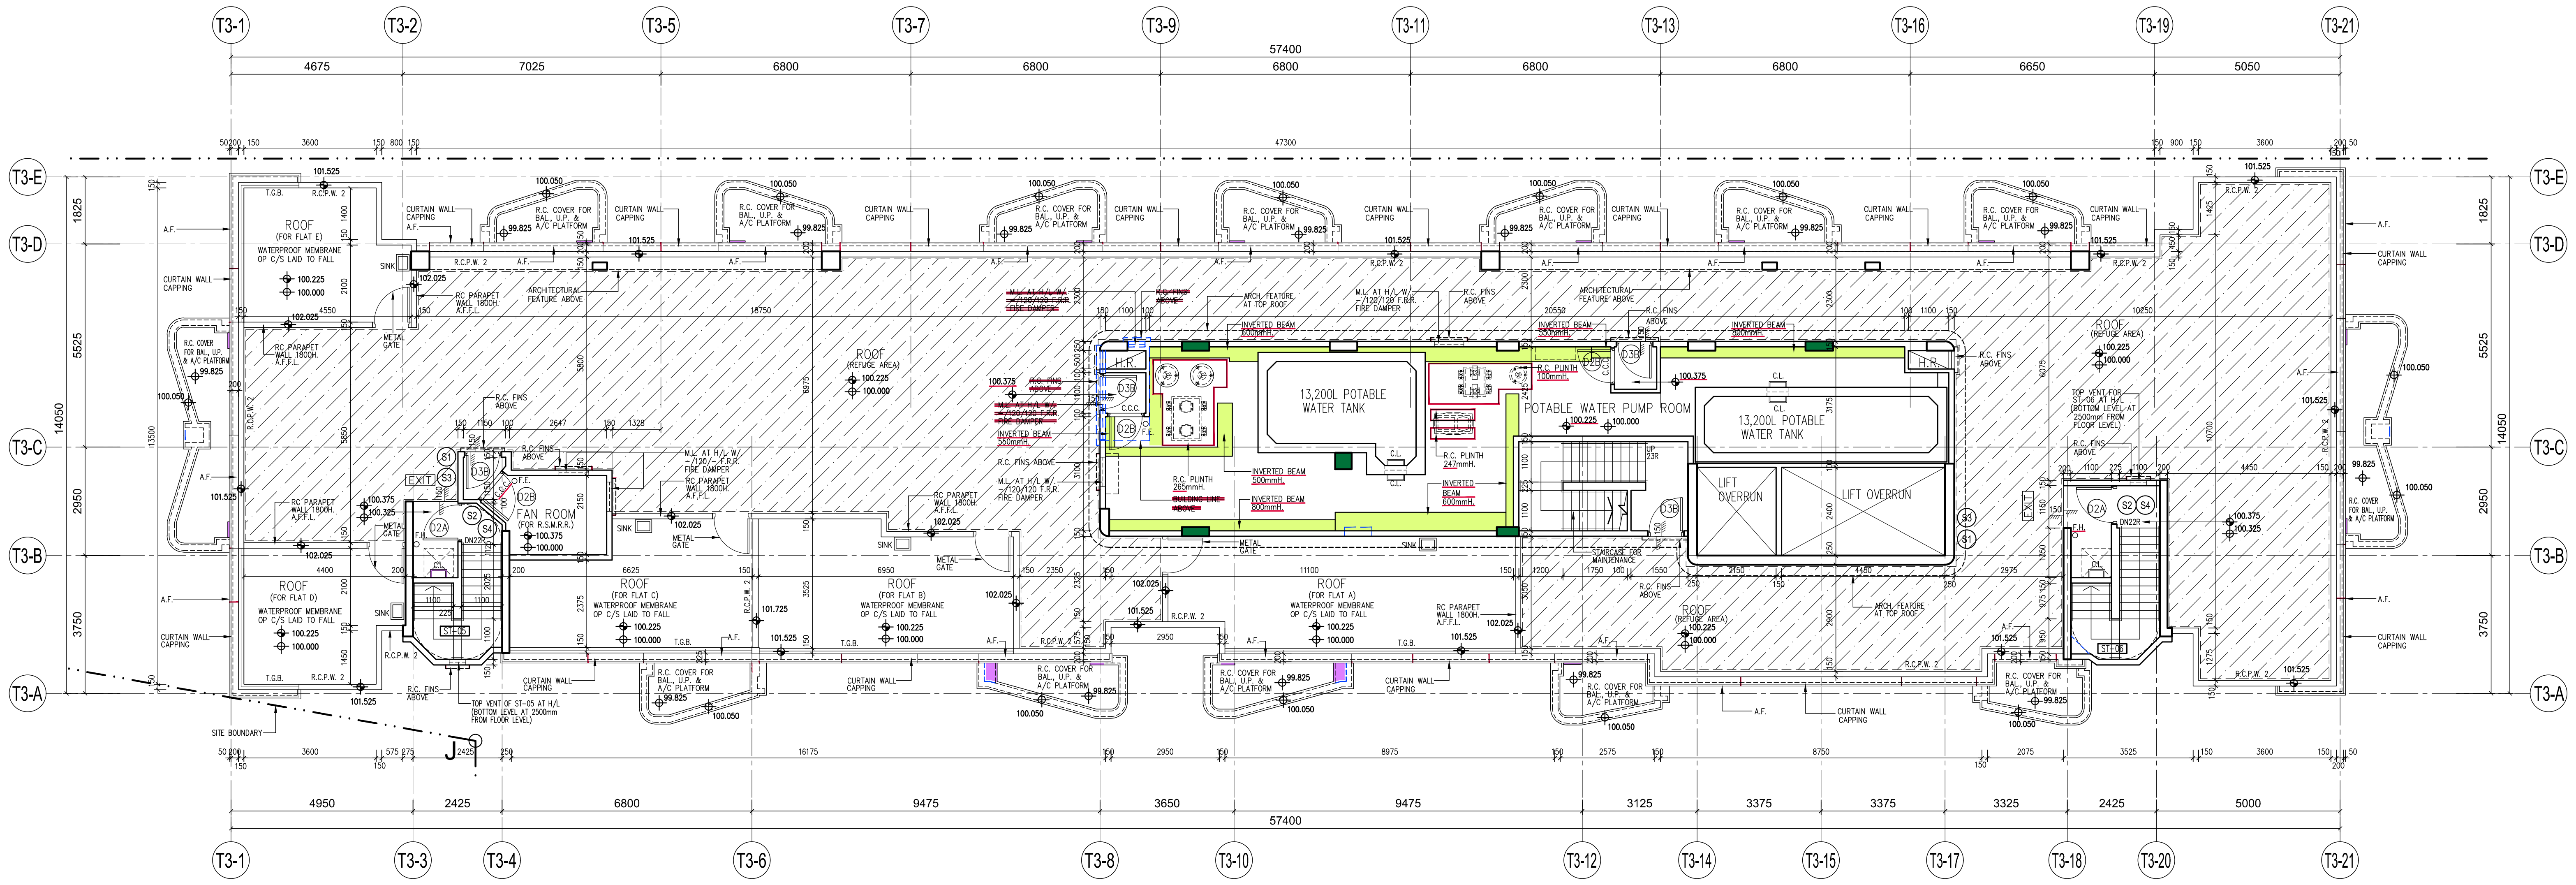
T3-1
T3-2
T3-5
T3-7
T3-9
T3-11
T3-13
T3-16
T3-19
T3-21
57400
T3-E
T3-D
T3-C
T3-B
T3-A
ROOF (FOR FLAT E)
ROOF (FOR FLAT D)
ROOF (REFUGE AREA)
13,200L POTABLE WATER TANK
POTABLE WATER PUMP ROOM
13,200L POTABLE WATER TANK
LIFT OVERRUN
LIFT OVERRUN
FAN ROOM
ROOF (FOR FLAT C)
ROOF (FOR FLAT B)
ROOF (FOR FLAT A)
CURTAIN WALL CAPPING
SITE BOUNDARY
T3-3
T3-4
T3-6
T3-8
T3-10
T3-12
T3-14
T3-15
T3-17
T3-18
T3-20

ROOF PLAN – TOWER 3

LEGEND:

- (S1) REFUGE FLOOR NOTICE
- (S2) STAIR NO. SIGN
- (S3) DIRECTIONAL SIGN TO EXIT STAIRCASE
- (S4) A SIGN INDICATING THE ENTRANCE TO THE REFUGE FLOOR
- ▨ NET REFUGE AREA = 340.816 m²

THE PERCENTAGE OF THE NET REFUGE AREA

THE G.F.A. OF THE LARGEST FLOOR PLATE = 663.064 m²
PERCENTAGE OF REFUGE AREA PROVIDED = 340.816 / 663.064 x 100%
= 51.400 % > 50% (REQUIRED)

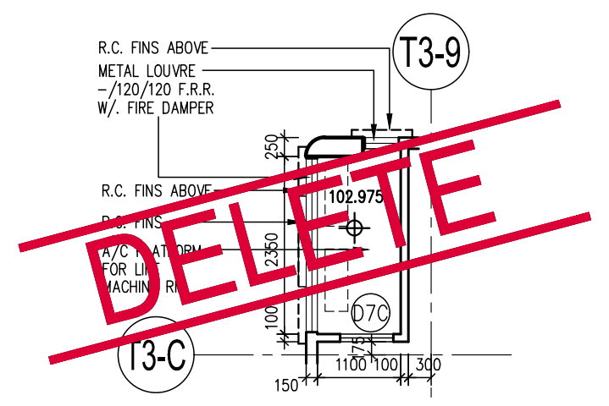
T3-9
T3-C
DELETE

PART PLAN AT LEVEL 102.975

B.D. Ref : BD 2/4024/21
BIM Ref : - --
F.S.D. Ref : - --
D.L.O. Ref : - --

Rev.	Description	Drawn	Checked	Approved	Date
-	1st Submission	WY	AW	AL	07/2022
A	2nd Submission	WY	AW	AL	11/2022
B	1st Amendment	TWM	AW	AL	04/2023
C	2nd Amendment	TWM	AW	AL	12/2023
D	3rd Amendment	TWM	AW	AL	04/2024
D	3rd Amendment (Re-submission)	TWM	AW	AL	05/2024
E	5th Amendment	TWM	AW	AL	12/2024
E	5th Amendment (Re-submission)	TWM	AW	AL	02/2025
F	8th Amendment	TWM	AW	AL	05/2025
G	9th Amendment	TWM	AW	AL	08/2025
G	9th Amendment (Re-submission)	TWM	AW	AL	10/2025
H	10th Amendment	TWM	AW	AL	12/2025
I	11th Amendment	TWM	AW	AL	02/2026

Type II works
The works shown on these plans are Type II works (Building Amendment) in respect of which consent is applied for the purpose of Fast Track consent application under regulation 33 of the Building (Administration) Regulations.

RONALD LU & PARTNERS
呂 元 祥 建 築 師 事 務 所

Check all measurements on site. Do not scale off drawings.
This drawing is to be read in conjunction with the specification and any discrepancies are to be immediately reported to the Architect.
This drawing remains the copyright property of the Architect and is not to be reproduced in whole or in part without permission of the Architect.

Project Title :
PROPOSED DEVELOPMENT
AT BAILEY STREET
& WING KWONG STREET
TO KWA WAN, KOWLOON

Drawing Title :
ROOF FLOOR PLAN
FOR TOWER 3

Drawn By	TWM	Date	08/2025
Checked By	AW	Date	08/2025
Approved By	AL	Date	08/2025
Project No.	21163KL	Issue Date	08/2025

File Path : U:\Studio_B\Proj_Data\2021\21163KL_Bailey Street & Wing Kwong Street\DRAWING\SUB\BD\GBP_13 (Final Amendment)_Hand Amend\PLOT\A_GBP_16.dwg

Scale 1:100 By CAD

Drawing Number : A/GBP/16
Revision Number : I

Drawing Purpose
Buildings Department
Amended Plan

Digitally signed by
LEUNG Kit Man Andy
AP(A) 80/85
16 March 2026

Received on
16 March 2026

Plan Approved
(Digitally Signed)
TSOI Lap-san, Lapson
Senior Building Surveyor
for BUILDING AUTHORITY
17 March 2026

Note: This plan has been processed on a curtailed check basis under the centralized processing system as promulgated in PNAP ADM-19. The duties of the authorized person, registered structural engineer and/or registered geotechnical engineer concerned as specified under section 4(3)(b) and the provision of section 14(2)(c) of the Buildings Ordinance are of particular relevance in this regard.

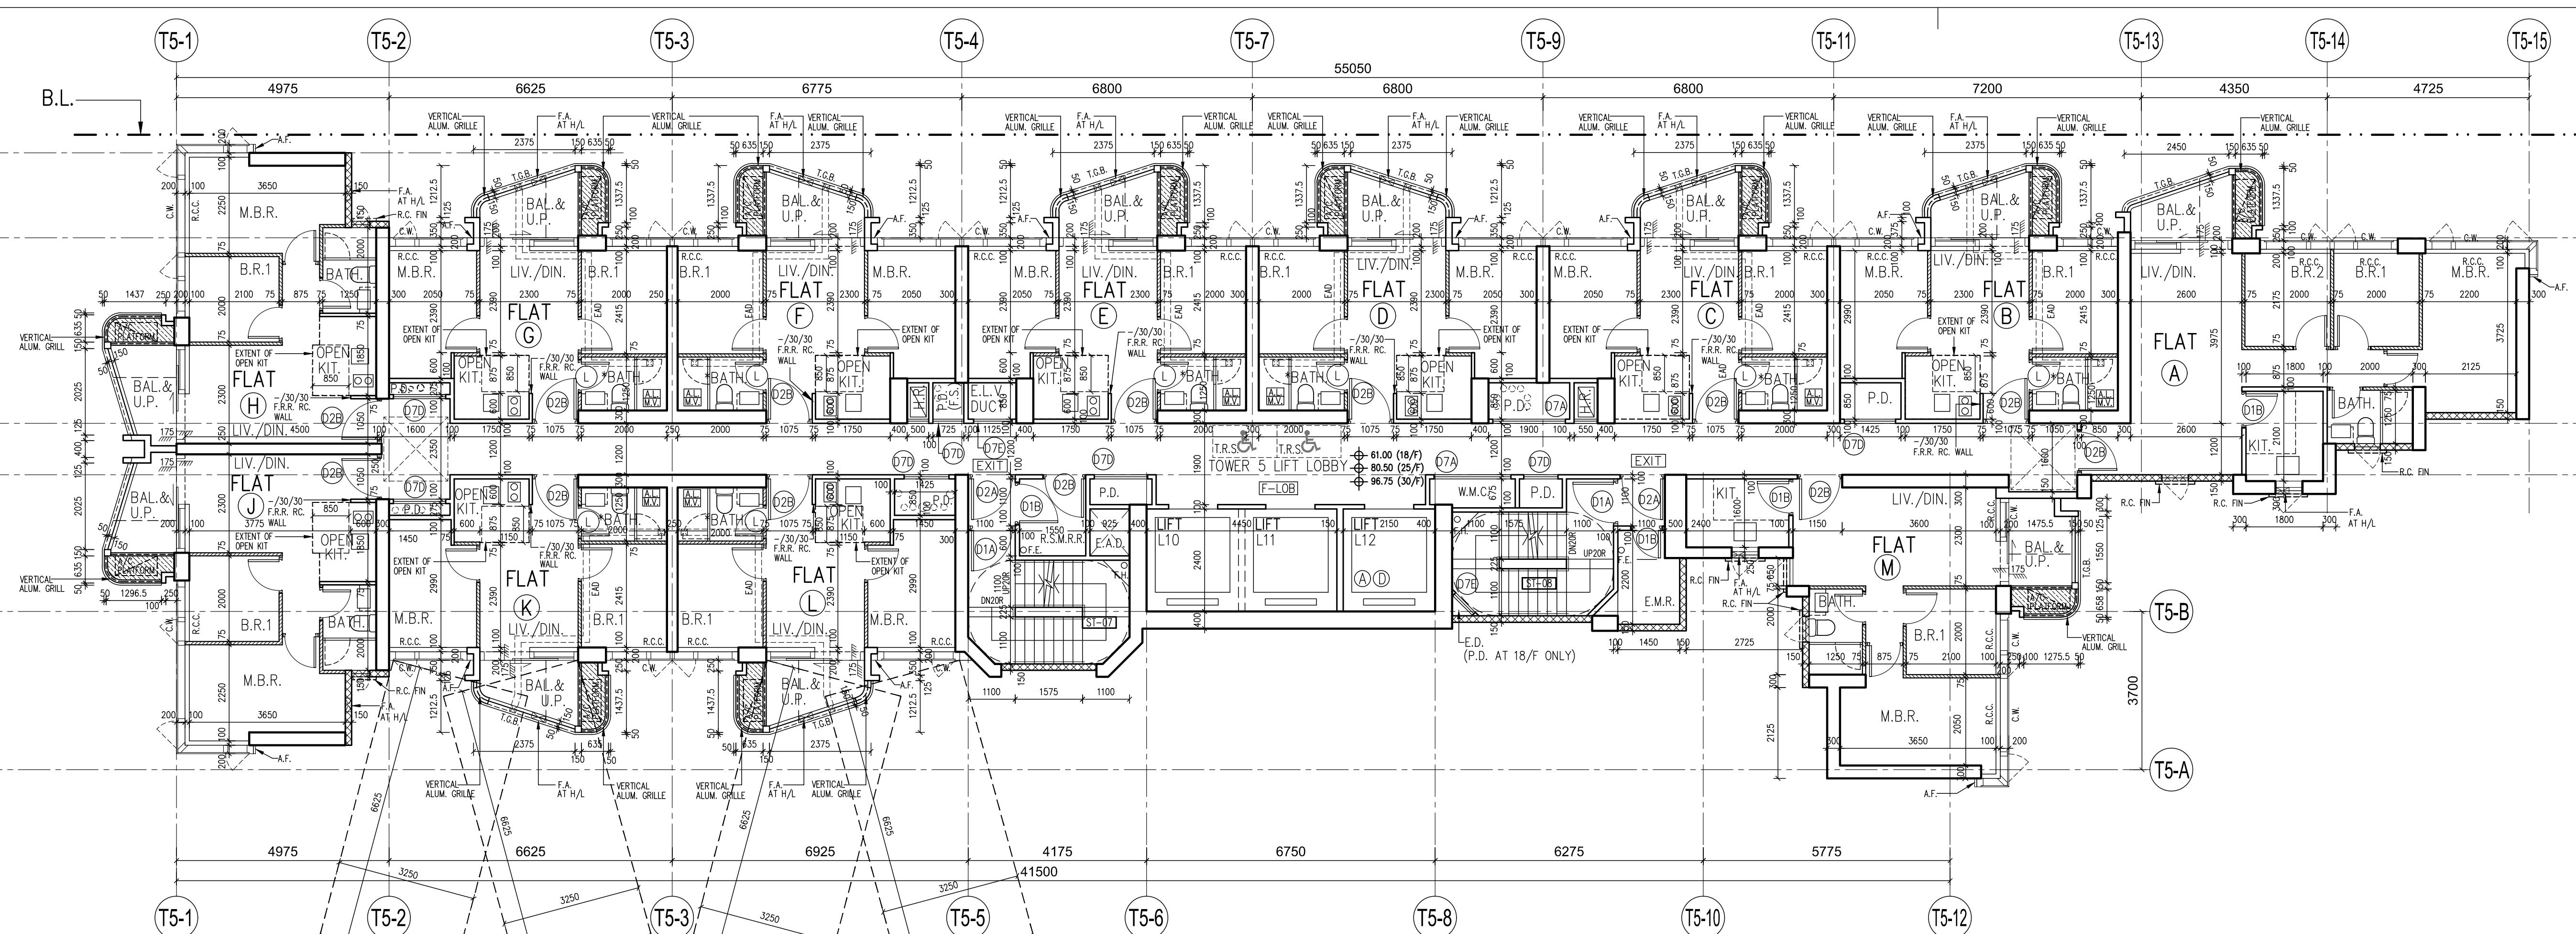

UNDER BUILDING (PLANNING) REG. 31
LEVEL OF MAIN ROOF PARAPET : 101.525
LEVEL OF WINDOW SILL AT 18/F : 62.05
REQUIRED LENGTH OF RECTANGULAR PLANE
= (101.525 − 62.05) / 6 = 6.579
RECTANGULAR HORIZONTAL PLANE AREA PROVIDED
= 6.625 x 3.250 =21.531 > 21 m² (REQUIRED)

18th TO 30th FLOOR PLAN – TOWER 5 (12 STOREYS)

NOTE:
1. MECHANICAL VENTILATION AND ARTIFICIAL LIGHTING WILL BE PROVIDED AT THE BATHROOM/ LAVATORY MARKED WITH " * " FOR OMISSION OF NATURAL LIGHTING AND VENTILATION.
2. THERE WILL BE NO 13/F, 14/F & 24/F IN THE NOMENCLATURE SYSTEM FOR NUMBERING OF FLOORS.

LEGEND:

▨ A/C PLATFORM

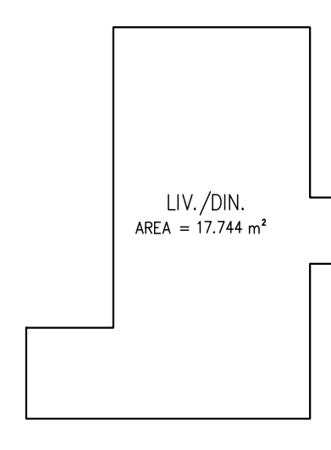
LIV./DIN.
AREA = 17.744 m²

3/F – 30/F FLAT A (LIV./DIN.) ROOM AREA

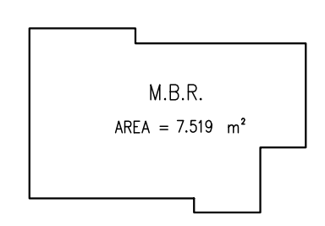
M.B.R.
AREA = 7.519 m²

3/F – 30/F FLAT H (M.B.R.) AREA

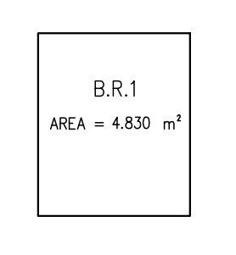
B.R.1
AREA = 4.830 m²

3/F – 30/F FLAT B (B.R.1) ROOM AREA

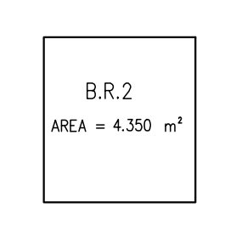
B.R.2
AREA = 4.350 m²

3/F – 30/F FLAT A (B.R.2) ROOM AREA

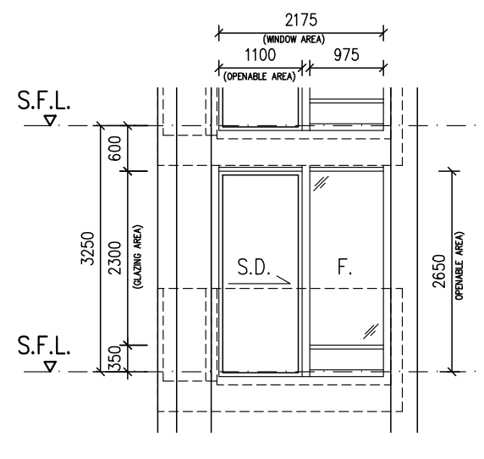
2175
(WINDOW AREA)
1100
975
(OPENABLE AREA)
S.F.L.
600
3250
2300
(GLAZING AREA)
350
S.D.
F.
2650
(OPENABLE AREA)

WINDOW AREA CALCULATION
FOR FLAT A (LIV./DIN.)
(FOR FLAT B TO H, J TO M (LIV./DIN.))

ROOM AREA = 17.744 s.m.

WINDOW AREA REQ'D = 17.744 / 10 = 1.774 s.m.
WINDOW AREA PROV'D = (2.175 x 2.300 x 0.70)
= 3.502 s.m. > 1.774 s.m. (REQUIRED)

OPENABLE WINDOW AREA REQ'D = 17.744 /16 = 1.109 s.m.
OPENABLE WINDOW AREA PROV'D = 1.100 x 2.650 x 0.70
= 2.041 s.m. > 1.109 s.m. (REQUIRED)

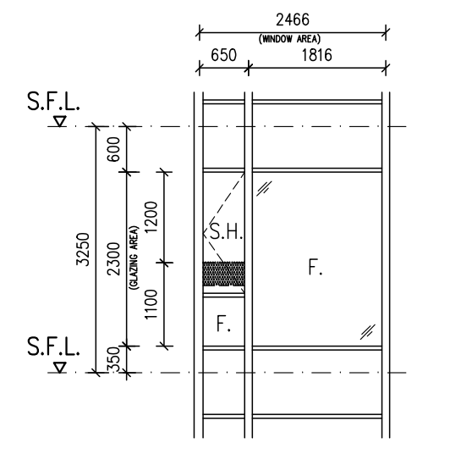
2466
(WINDOW AREA)
650
1816
S.F.L.
600
3250
2300
(GLAZING AREA)
1200
1100
350
S.H.
F.
F.

WINDOW AREA CALCULATION
FOR FLAT H (M.B.R.)
(FOR FLAT A TO G, J TO M (M.B.R.))

ROOM AREA = 7.519 s.m.

WINDOW AREA REQ'D = 7.519 / 10 = 0.752 s.m.
WINDOW AREA PROV'D = 2.466 x 2.300 x 0.70
= 3.970 s.m. > 0.752 s.m. (REQUIRED)

OPENABLE WINDOW AREA REQ'D = 7.519 /16 = 0.470 s.m.
OPENABLE WINDOW AREA PROV'D = 0.65 x 1.200 x 0.70
= 0.546 s.m. > 0.470 s.m. (REQUIRED)

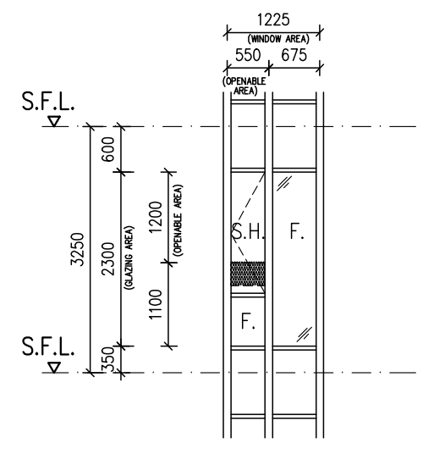
1225
(WINDOW AREA)
550
675
(OPENABLE AREA)
S.F.L.
600
3250
2300
(GLAZING AREA)
1200
(OPENABLE AREA)
1100
350
S.H.
F.
F.

WINDOW AREA CALCULATION
FOR FLAT B (B.R.1)
(FOR FLAT A, C TO G, J TO M (B.R.1))

ROOM AREA = 4.830 s.m.

WINDOW AREA REQ'D = 4.830 / 10 = 0.483 s.m.
WINDOW AREA PROV'D = (1.225 x 2.300 x 0.70)
= 1.972 s.m. > 0.483 s.m. (REQUIRED)

OPENABLE WINDOW AREA REQ'D = 4.830 /16 = 0.302 s.m.
OPENABLE WINDOW AREA PROV'D = (0.550 x 1.200 x 0.70)
= 0.462 s.m. > 0.302 s.m. (REQUIRED)

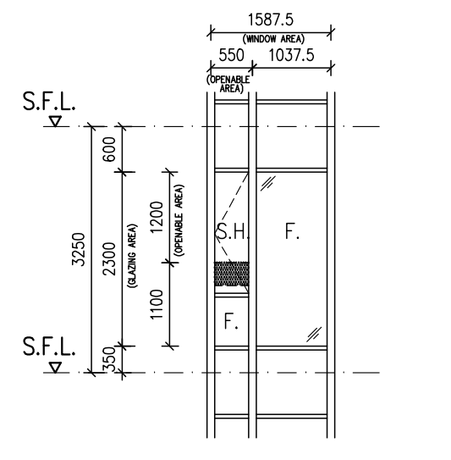
1587.5
(WINDOW AREA)
550
1037.5
(OPENABLE AREA)
S.F.L.
600
3250
2300
(GLAZING AREA)
1200
(OPENABLE AREA)
1100
350
S.H.
F.
F.

WINDOW AREA CALCULATION
FOR FLAT A (B.R.2)

ROOM AREA = 4.350 s.m.

WINDOW AREA REQ'D = 4.350 / 10 = 0.435 s.m.
WINDOW AREA PROV'D = (1.5875 x 2.300 x 0.70)
= 2.556 s.m. > 0.435 s.m. (REQUIRED)

OPENABLE WINDOW AREA REQ'D = 4.350 /16 = 0.272 s.m.
OPENABLE WINDOW AREA PROV'D = (0.550 x 1.200 x 0.70)
= 0.462 s.m. > 0.272 s.m. (REQUIRED)

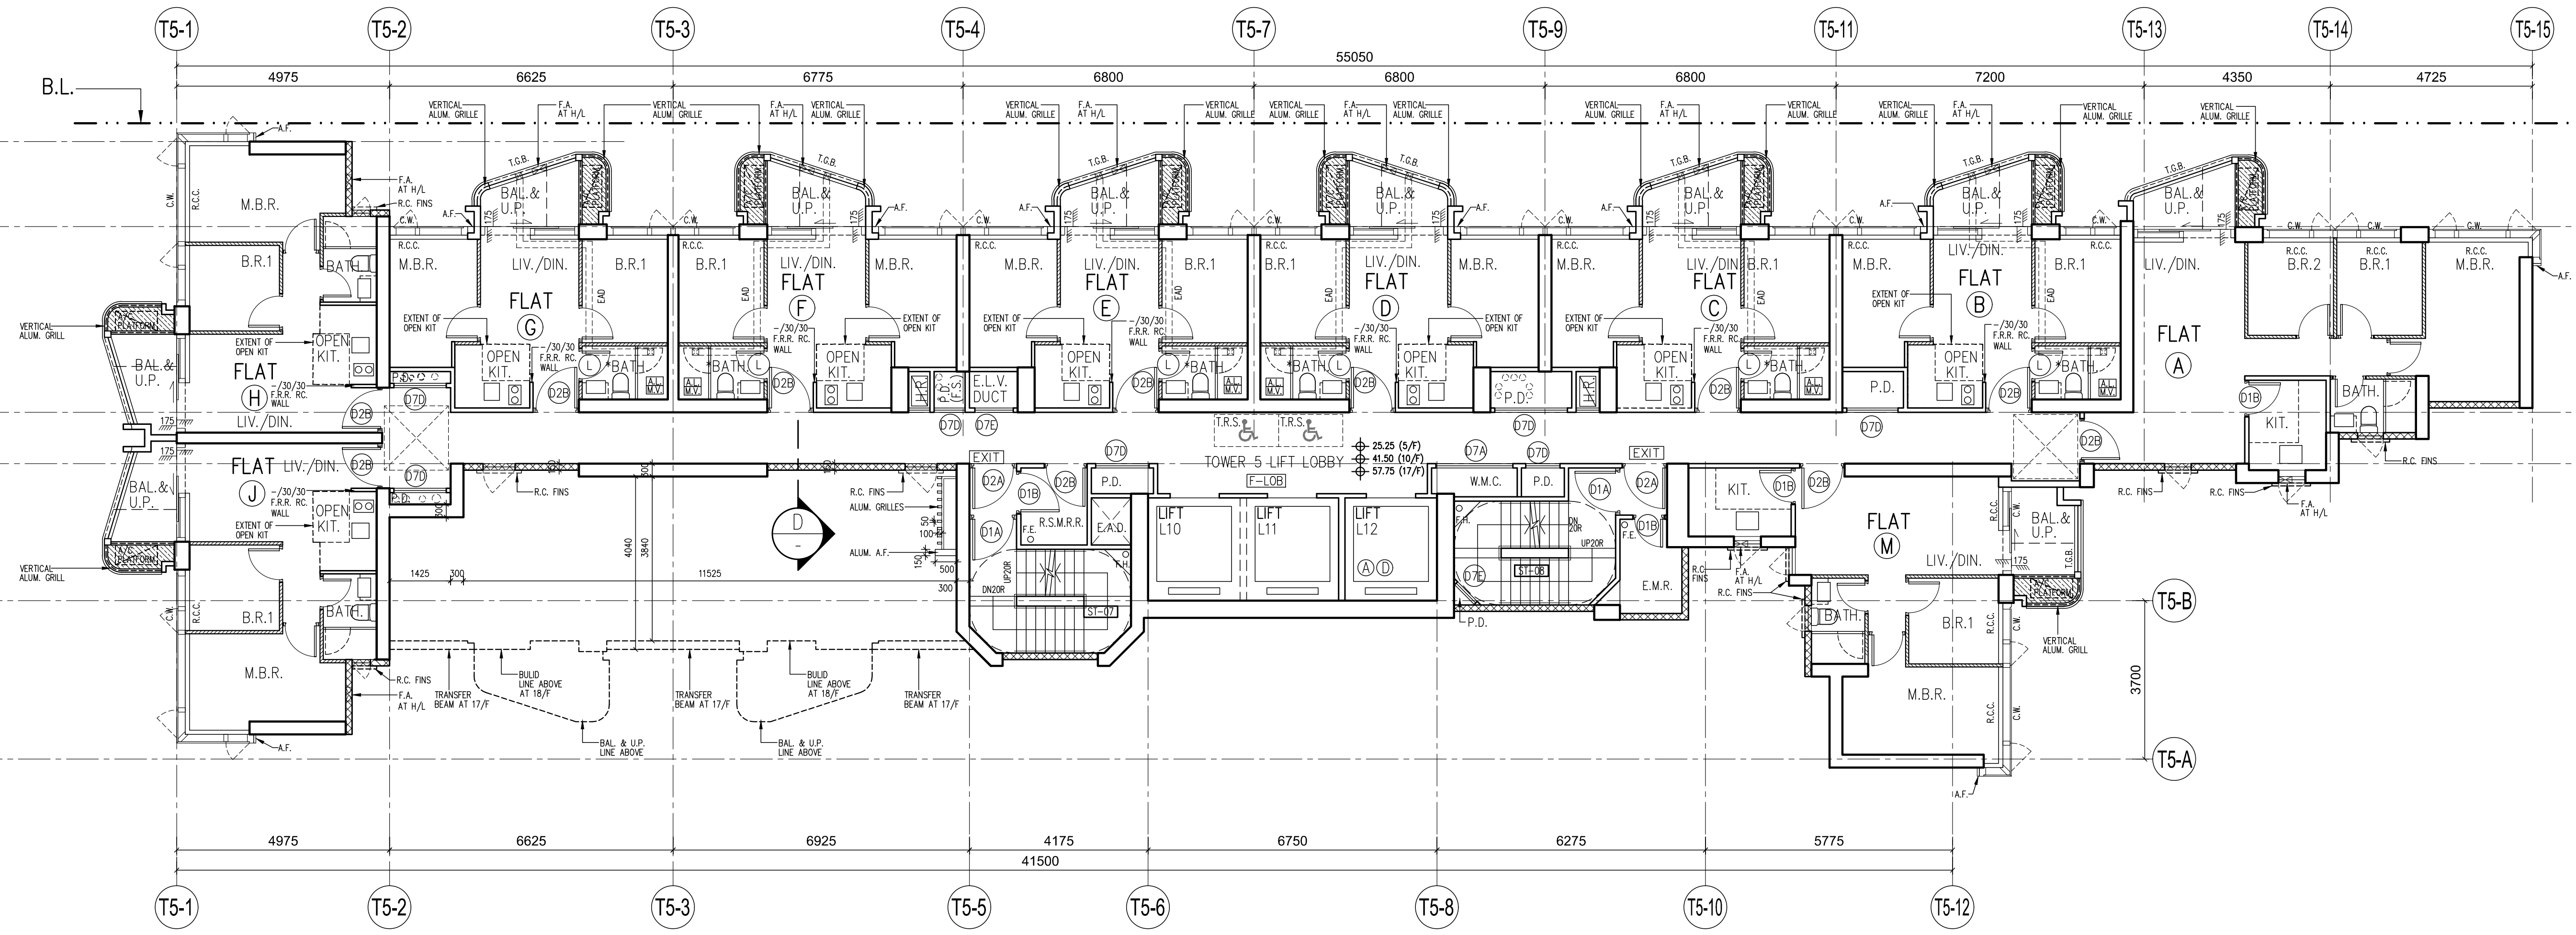

5th TO 17th FLOOR PLAN – TOWER 5 (11 STOREYS)

NOTE:
1. MECHANICAL VENTILATION AND ARTIFICIAL LIGHTING WILL BE PROVIDED AT THE BATHROOM/ LAVATORY MARKED WITH " * " FOR OMISSION OF NATURAL LIGHTING AND VENTILATION.
2. THERE WILL BE NO 13/F, 14/F & 24/F IN THE NOMENCLATURE SYSTEM FOR NUMBERING OF FLOORS.

LEGEND:

▨ A/C PLATFORM

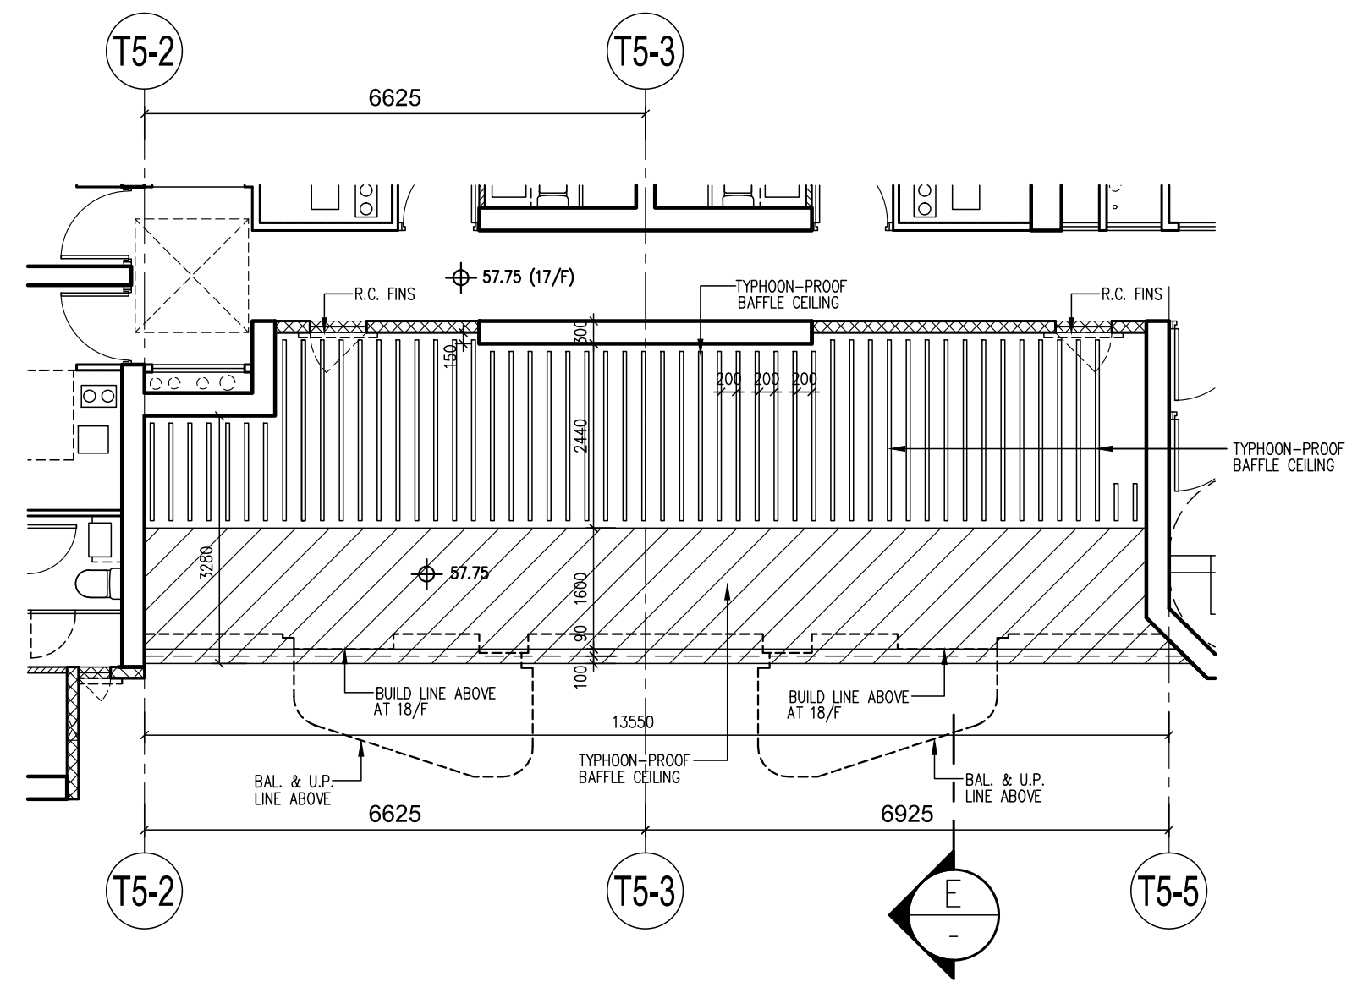

PART PLAN AT 17th FLOOR PLAN – TOWER 5

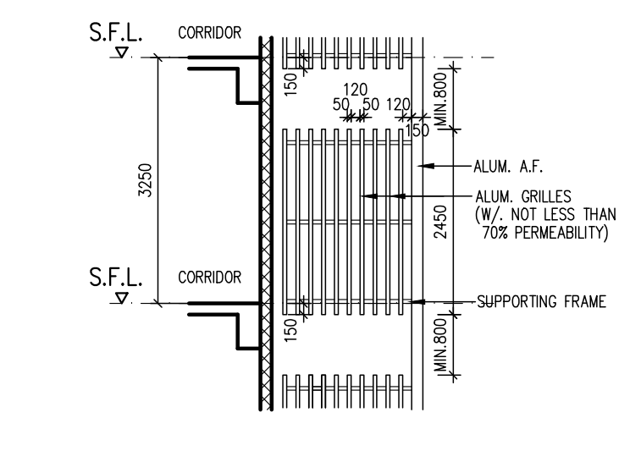

D TYPICAL DETAIL OF ALUM. GRILLES FOR SCREENING OF EXTERNAL PIPES AT T2

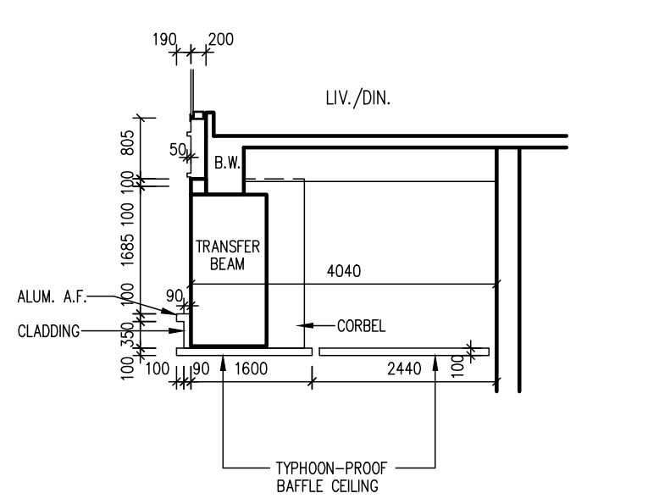
B.W.
TRANSFER BEAM
4040
ALUM. A.F.
CLADDING
CORBEL
1600
2440
TYPHOON-PROOF BAFFLE CEILING

E TYPICAL DETAIL OF CLADDING & TYPHOON-PROOF BAFFLE CEILING
(STRUCTURAL SUBMISSION UNDER SEPARATE SUBMISSION)

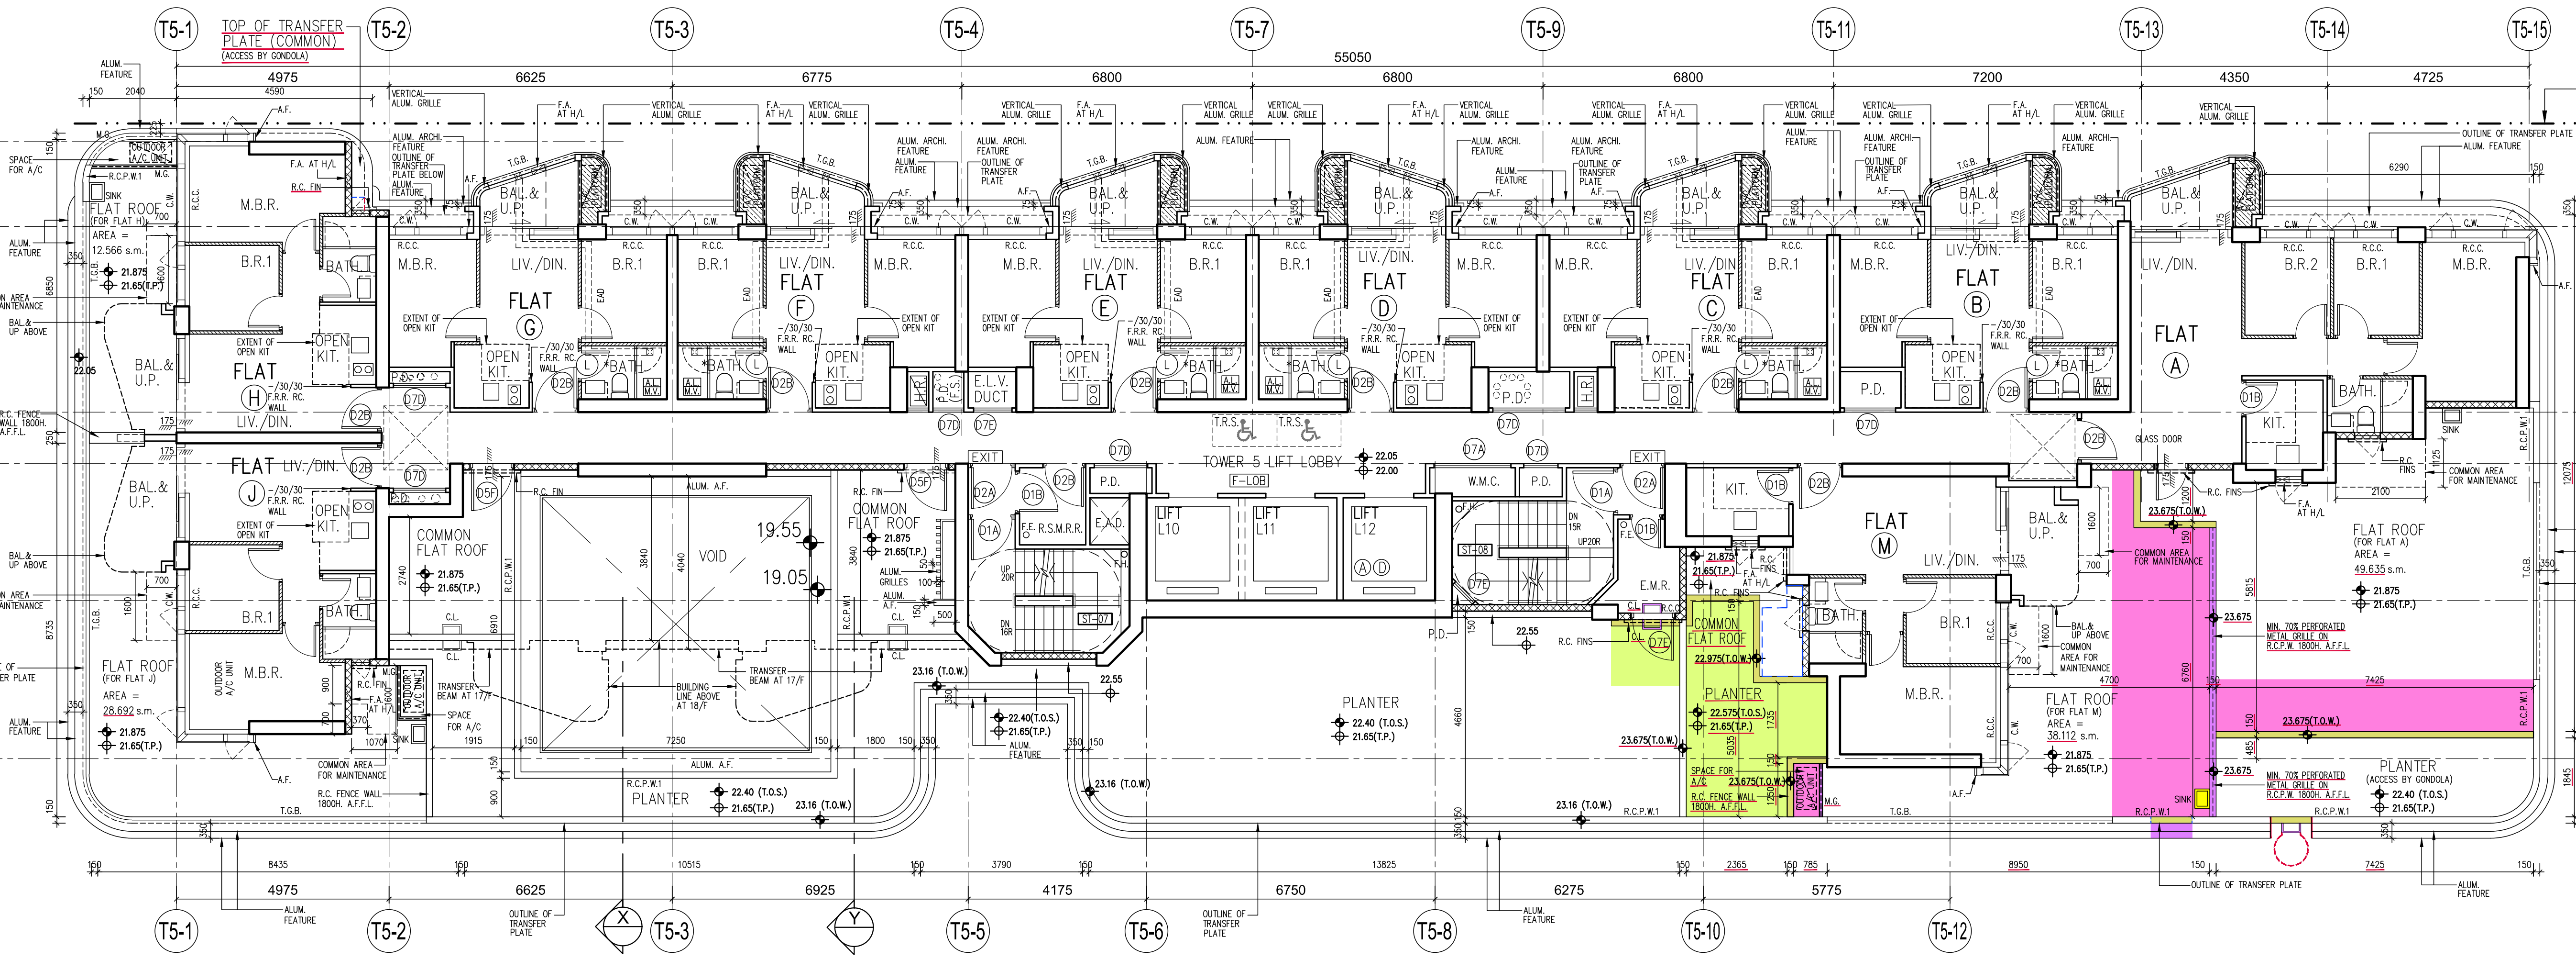

3RD FLOOR PLAN – TOWER 5

NOTE:
1. MECHANICAL VENTILATION AND ARTIFICIAL LIGHTING WILL BE PROVIDED AT THE BATHROOM/ LAVATORY MARKED WITH " * " FOR OMISSION OF NATURAL LIGHTING AND VENTILATION.
2. ALL DIMENSION ARE SAME AS 5/F – 30/F, EXCEPT OTHERWISE NOTED.

LEGEND:

▨ A/C PLATFORM

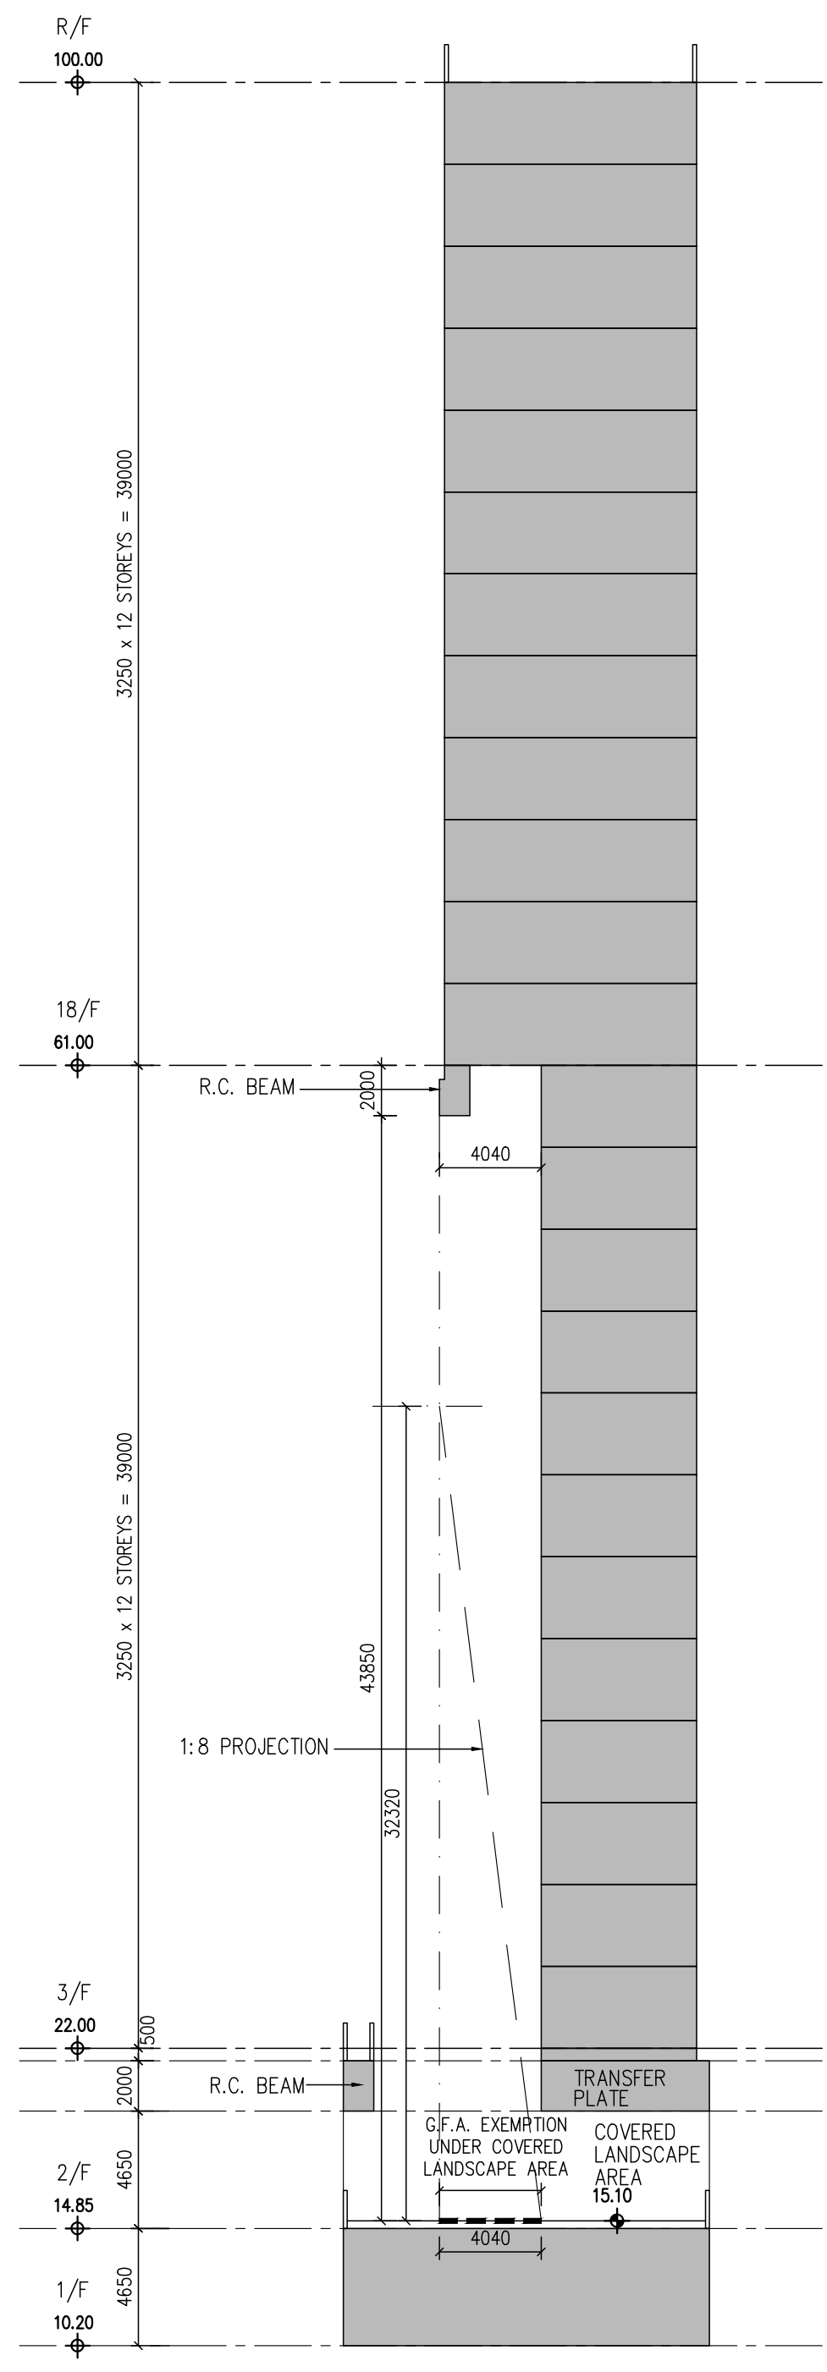
R/F
100.00
18/F
61.00
3/F
22.00
2/F
14.85
1/F
10.00
R.C. BEAM
1:8 PROJECTION
TRANSFER PLATE
G.F.A. EXEMPTION UNDER COVERED LANDSCAPE AREA
COVERED LANDSCAPE AREA
15.10
4040

DIAGRAMMATIC SECTION X
SCALE 1:300

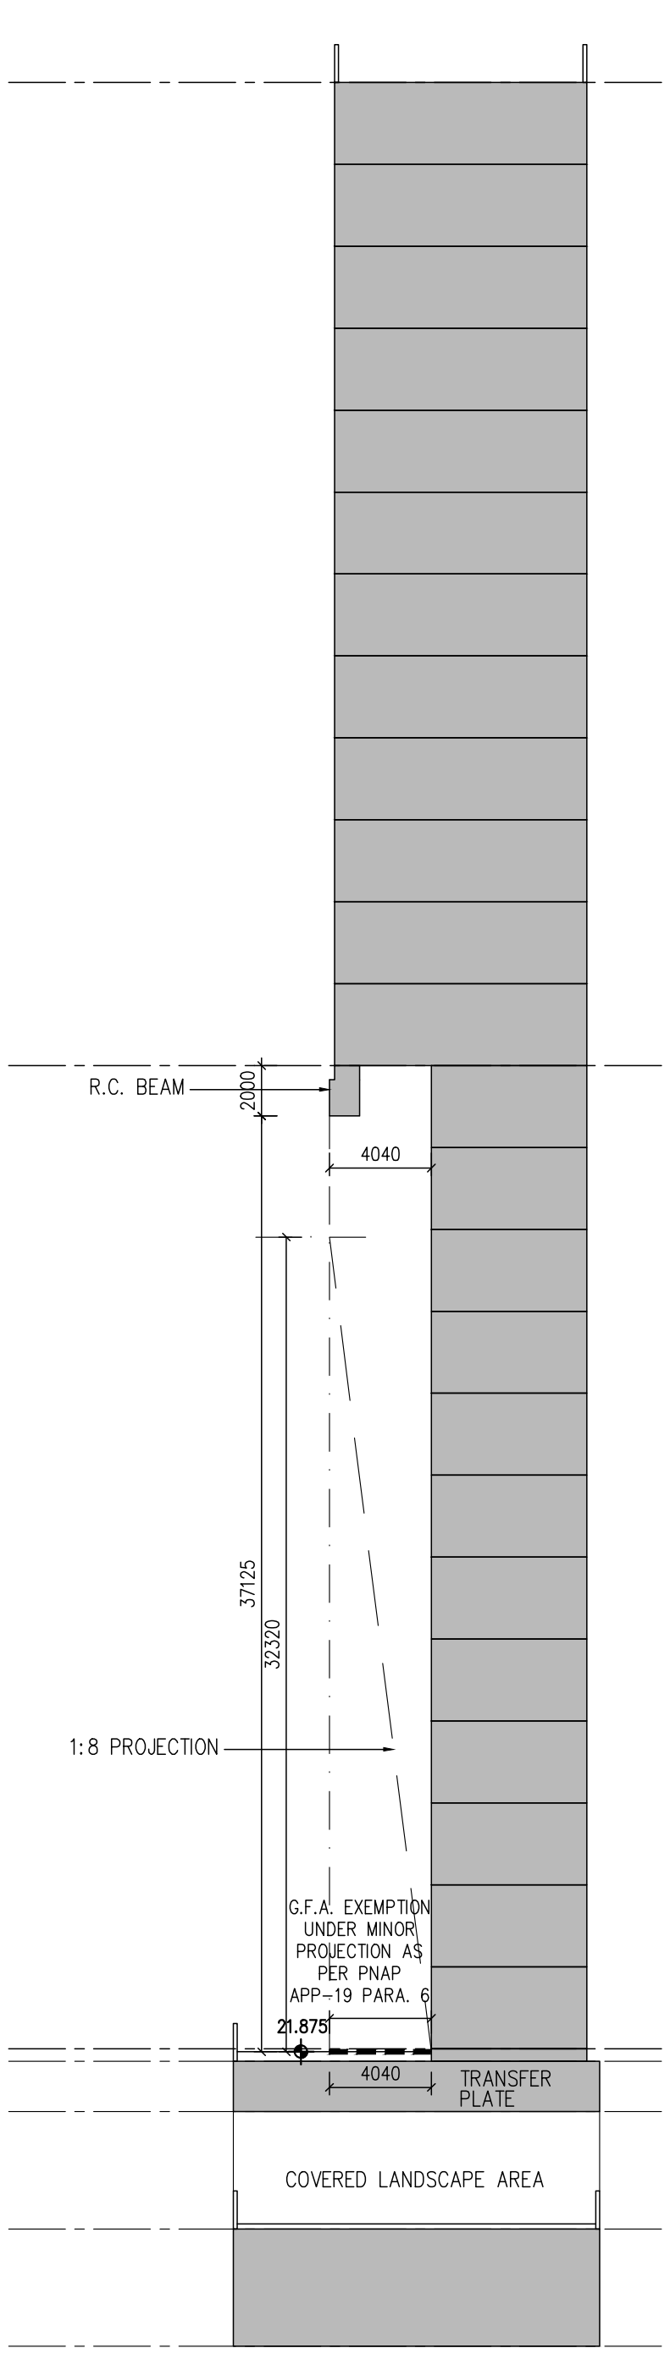
R.C. BEAM
1:8 PROJECTION
G.F.A. EXEMPTION UNDER MINOR PROJECTION AS PER PNAP APP-19 PARA. 6
4040
TRANSFER PLATE
COVERED LANDSCAPE AREA

DIAGRAMMATIC SECTION Y
SCALE 1:300

B.D. Ref : BD 2/4024/21
BIM Ref : - --
F.S.D. Ref : - --
D.L.O. Ref : - --

Rev.	Description	Drawn	Checked	Approved	Date
-	1st Submission	WY	AW	AL	07/2022
A	2nd Submission	WY	AW	AL	11/2022
B	1st Amendment	TWM	AW	AL	04/2023
C	2nd Amendment	TWM	AW	AL	12/2023
D	3rd Amendment	TWM	AW	AL	04/2024
E	4th Amendment	TWM	AW	AL	08/2024
F	5th Amendment	TWM	AW	AL	12/2024
F	5th Amendment (Re-submission)	TWM	AW	AL	02/2025
G	6th Amendment	TWM	AW	AL	02/2025
H	8th Amendment	TWM	AW	AL	05/2025
I	9th Amendment	TWM	AW	AL	08/2025
I	9th Amendment (Re-submission)	TWM	AW	AL	10/2025
J	10th Amendment	TWM	AW	AL	12/2025
K	11th Amendment	TWM	AW	AL	02/2026
L	13th Amendment	TWM	AW	AL	06/2026

Type II works
The works shown on these plans are Type II works (Building Amendment) in respect of which consent is applied for the purpose of Fast Track consent application under regulation 33 of the Building (Administration) Regulations.

RONALD LU & PARTNERS
呂元祥建築師事務所

Project Title :
PROPOSED DEVELOPMENT
AT BAILEY STREET
& WING KWONG STREET
TO KWA WAN, KOWLOON

Drawing Title :
3RD - 30TH FLOOR PLAN
FOR TOWER 5

Drawn By	TWM	Date	08/2025
Checked By	AW	Date	08/2025
Approved By	AL	Date	08/2025
Project No.	21163KL	Issue Date	08/2025

File Path :
U:\Studio_B\Proj_Data\2021\21163KL_Bailey Street & Wing Kwong Street\DRAWING\SUB\BD\GBP_15_Hand Amend\PLOT\A_GBP_17.dwg

Scale 1:100 By CAD

Drawing Number : A/GBP/17
Revision Number : L

Drawing Purpose
Buildings Department
Amended Plan

Digitally signed by
WONG Chi Kin Kenneth
AP(A) 19/95
08 July 2026

Received on
08 July 2026

Plan Approved
(Digitally Signed)
TSOI Lap-san, Lapson
Senior Building Surveyor
for BUILDING AUTHORITY
08 July 2026

Note: This plan has been processed on a curtailed check basis under the centralized processing system as promulgated in PNAP ADM-19. The duties of the authorized person, registered structural engineer and/or registered geotechnical engineer concerned as specified under section 4(3)(b) and the provision of section 14(2)(c) of the Buildings Ordinance are of particular relevance in this regard.

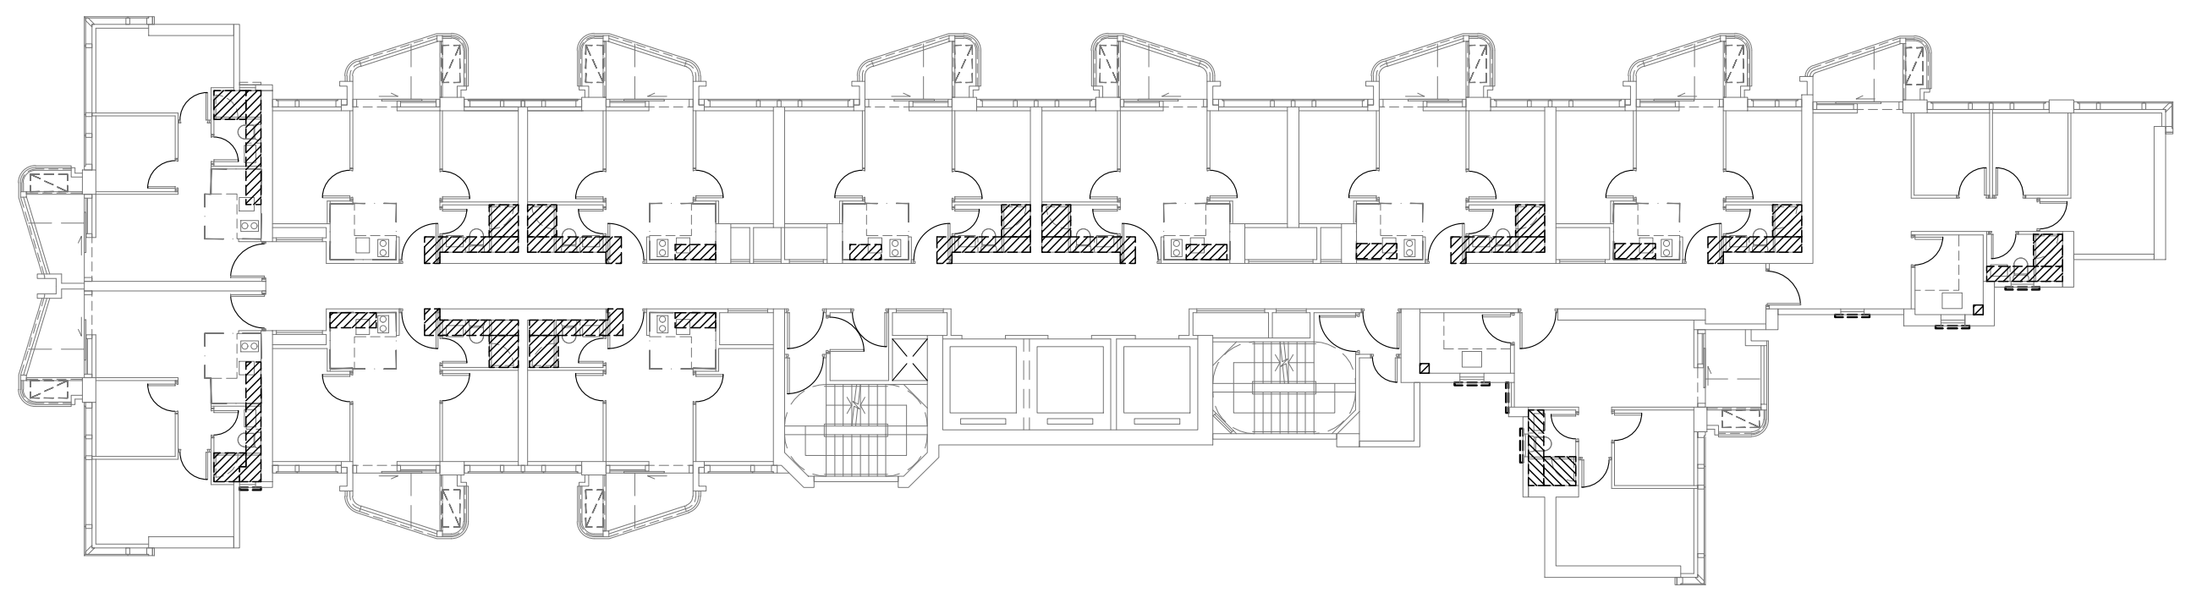

DIAGRAM OF SUNKEN SLAB EXTENT (18th TO 30th FLOOR)

SCALE 1:200

LEGEND:

▨ SUNKEN SLAB

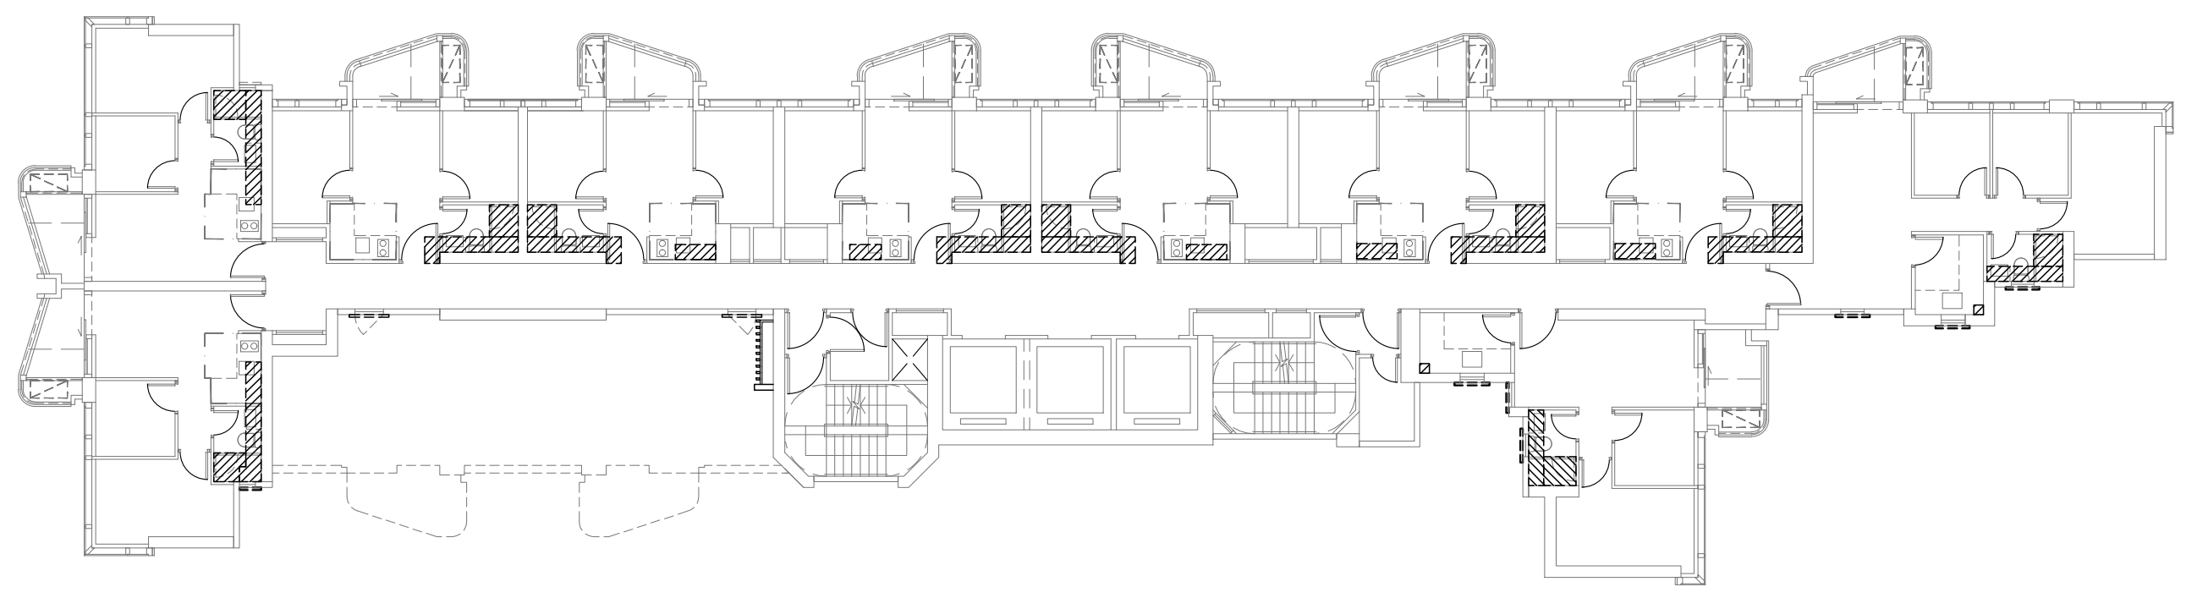

DIAGRAM OF SUNKEN SLAB EXTENT (5th TO 17th FLOOR)

SCALE 1:200

LEGEND:

▨ SUNKEN SLAB

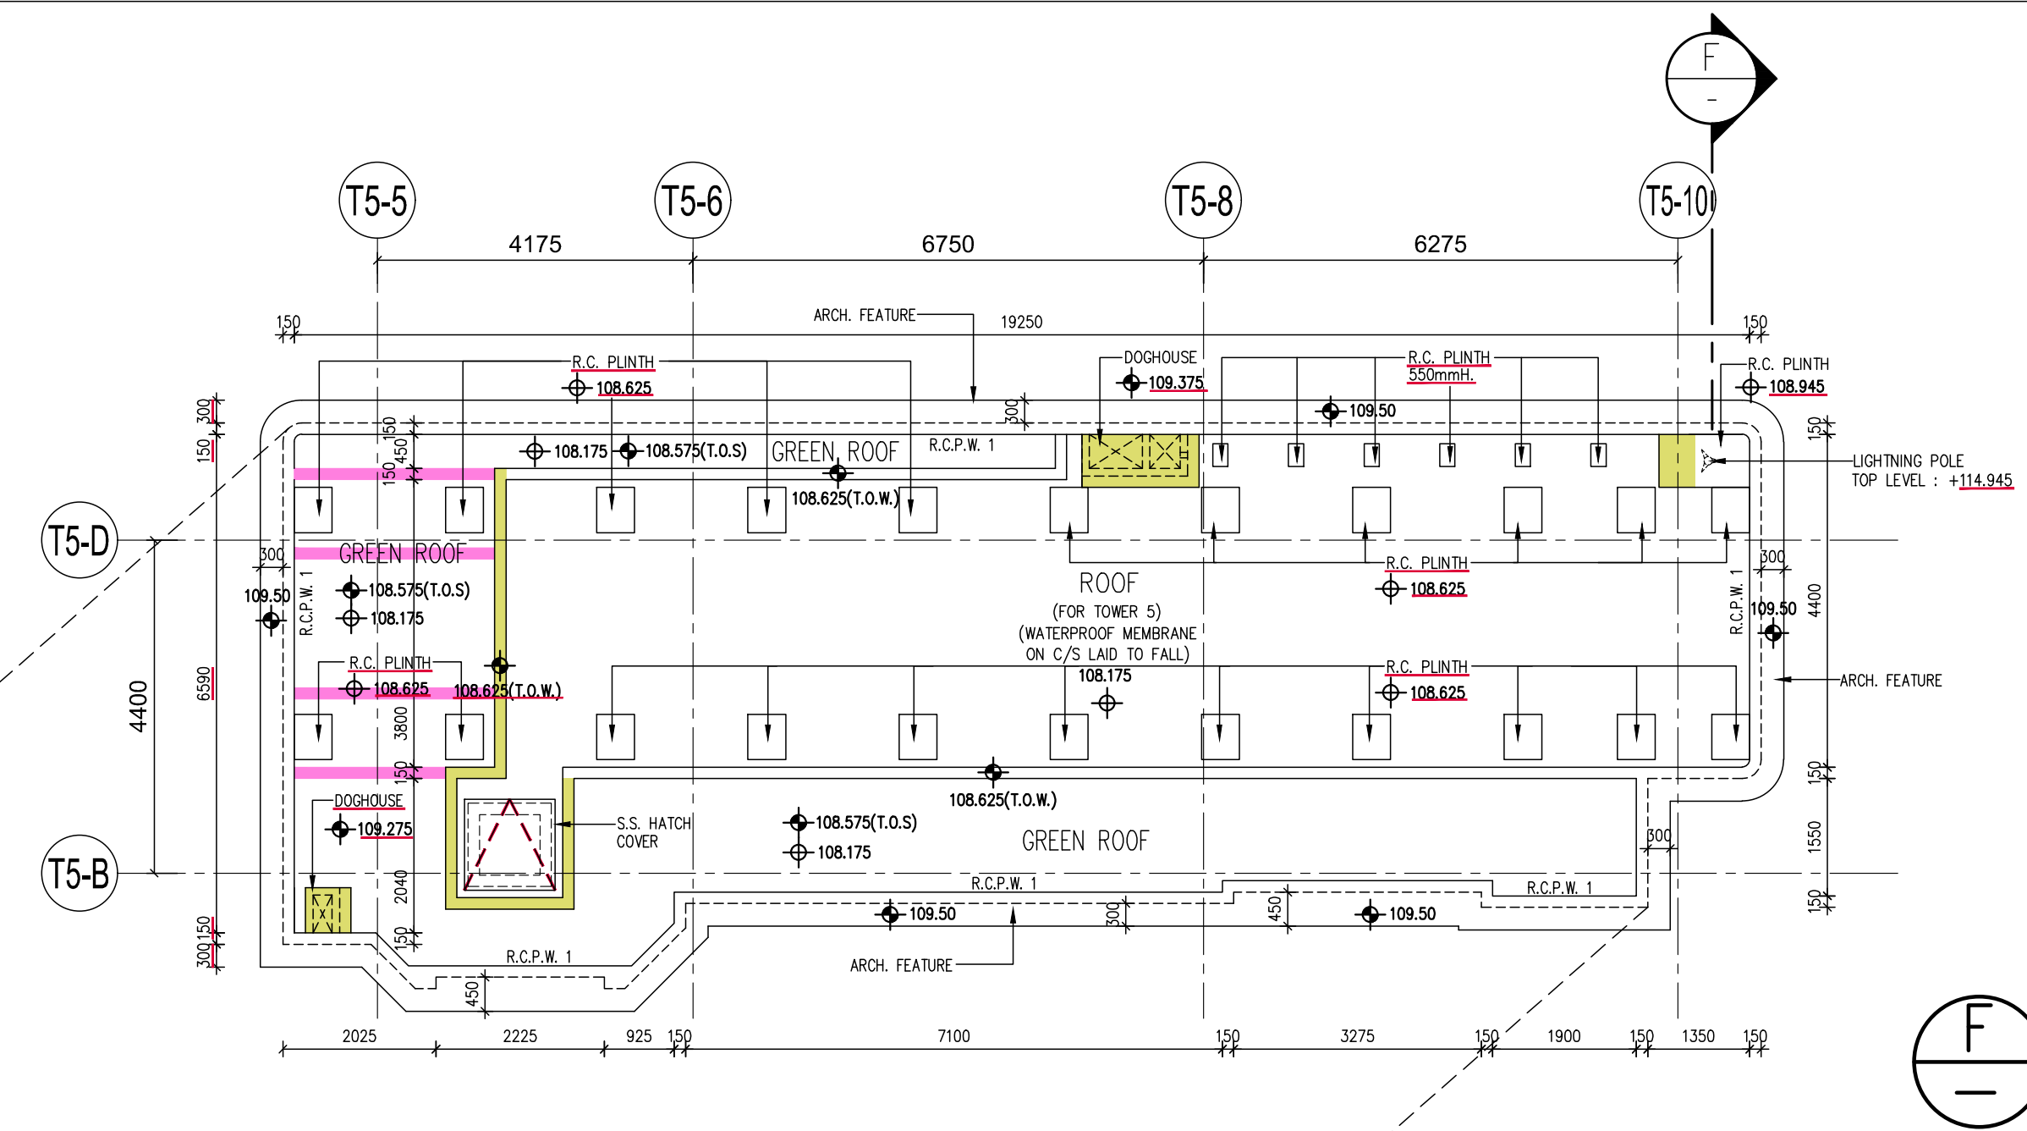
T5-5
T5-6
T5-8
T5-10
T5-D
T5-B
4175
6750
6275
GREEN ROOF
ROOF
DOGHOUSE
R.C. PLINTH
ARCH. FEATURE
S.S. HATCH COVER
LIGHTNING POLE

TOP ROOF PLAN – TOWER 5

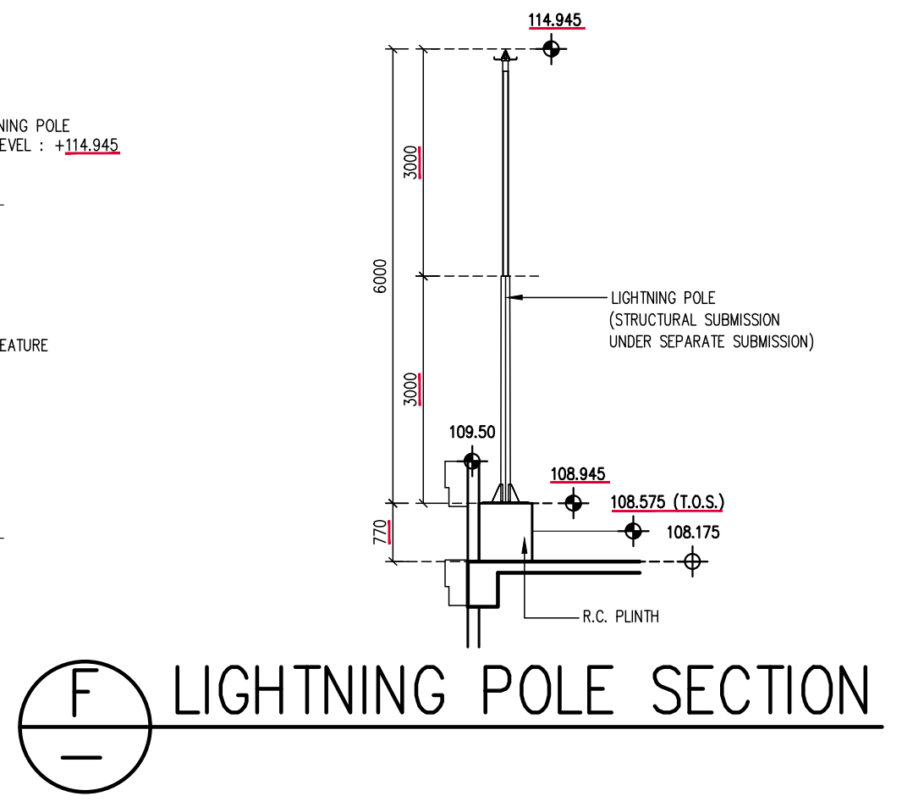
114.845
LIGHTNING POLE (STRUCTURAL SUBMISSION UNDER SEPARATE SUBMISSION)
108.575 (T.O.S)
108.175
R.C. PLINTH

F LIGHTNING POLE SECTION

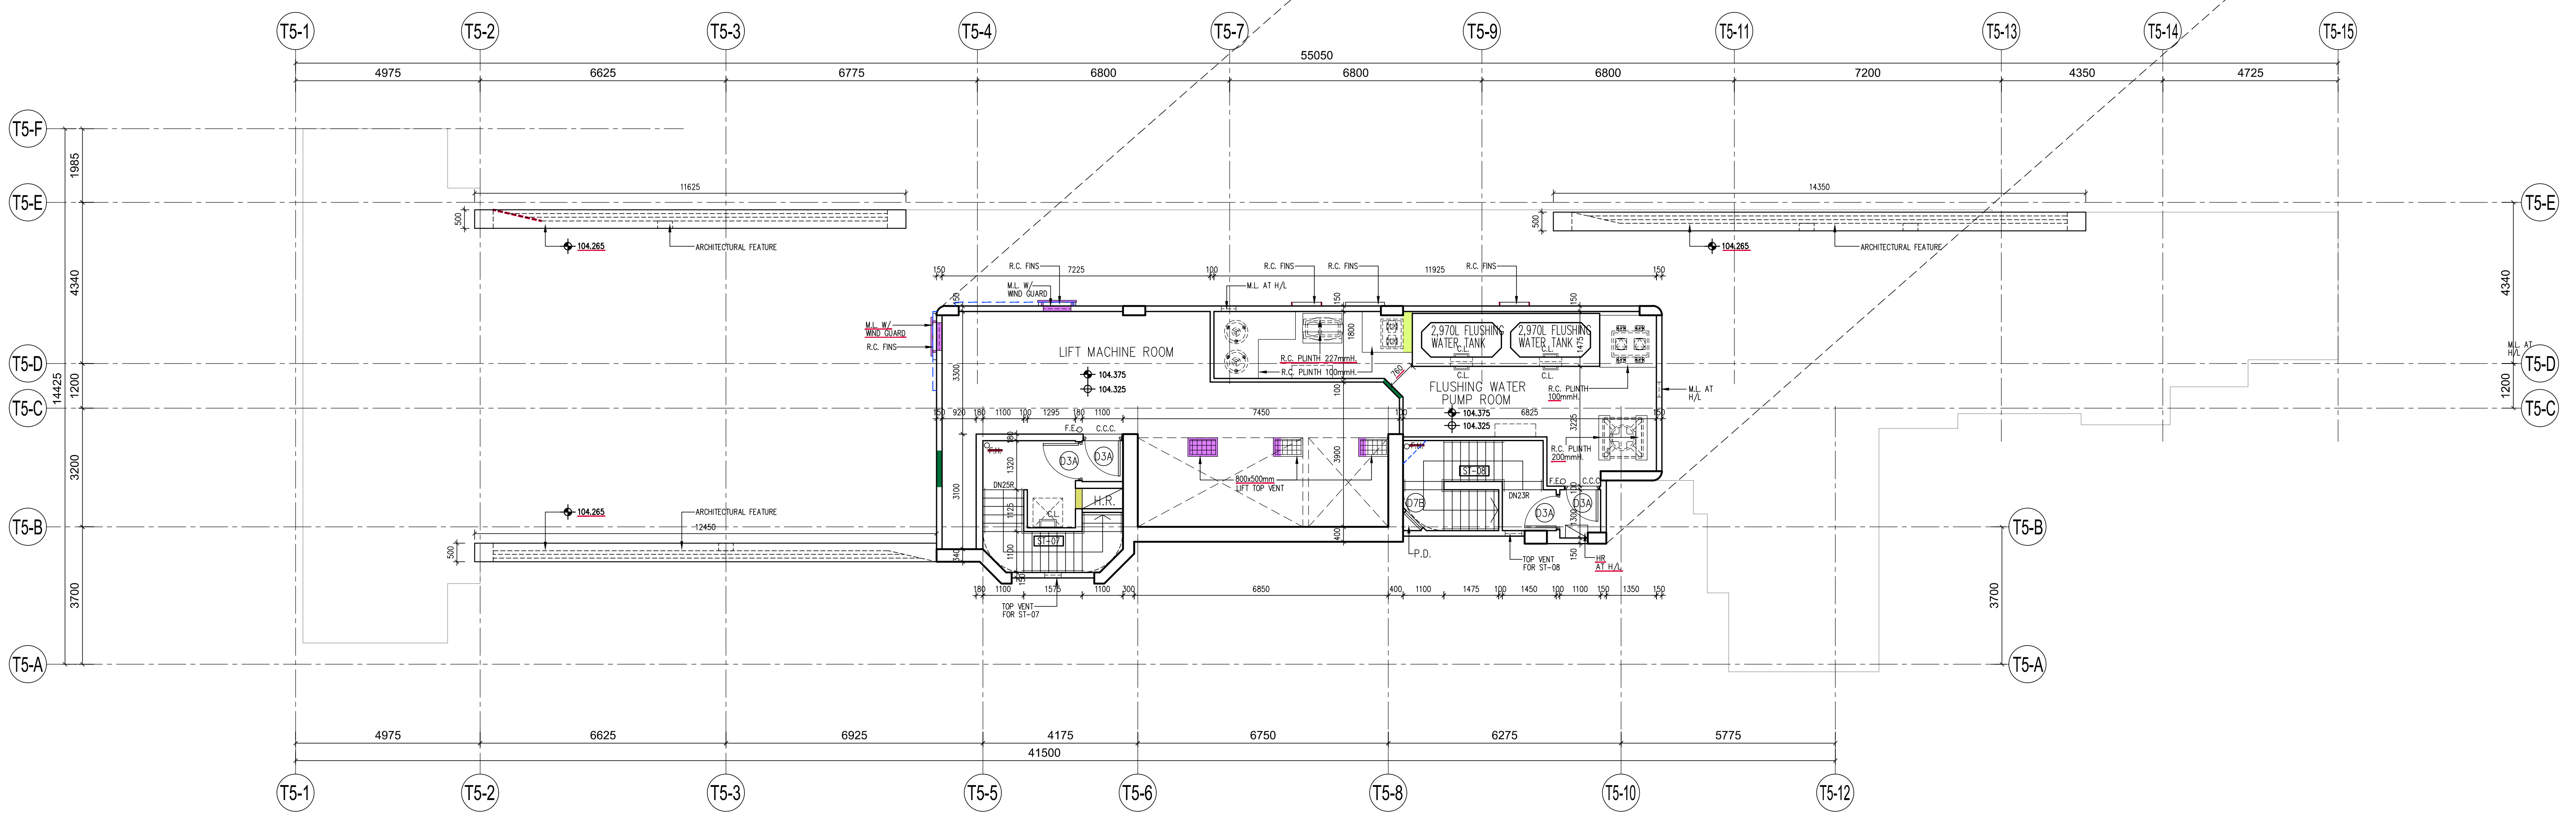
T5-1
T5-2
T5-3
T5-4
T5-7
T5-9
T5-11
T5-13
T5-14
T5-15
T5-F
T5-E
T5-D
T5-C
T5-B
T5-A
T5-5
T5-6
T5-8
T5-10
T5-12
55050
41500
LIFT MACHINE ROOM
FLUSHING WATER PUMP ROOM
2,970L FLUSHING WATER TANK
ARCHITECTURAL FEATURE

UPPER ROOF PLAN – TOWER 5

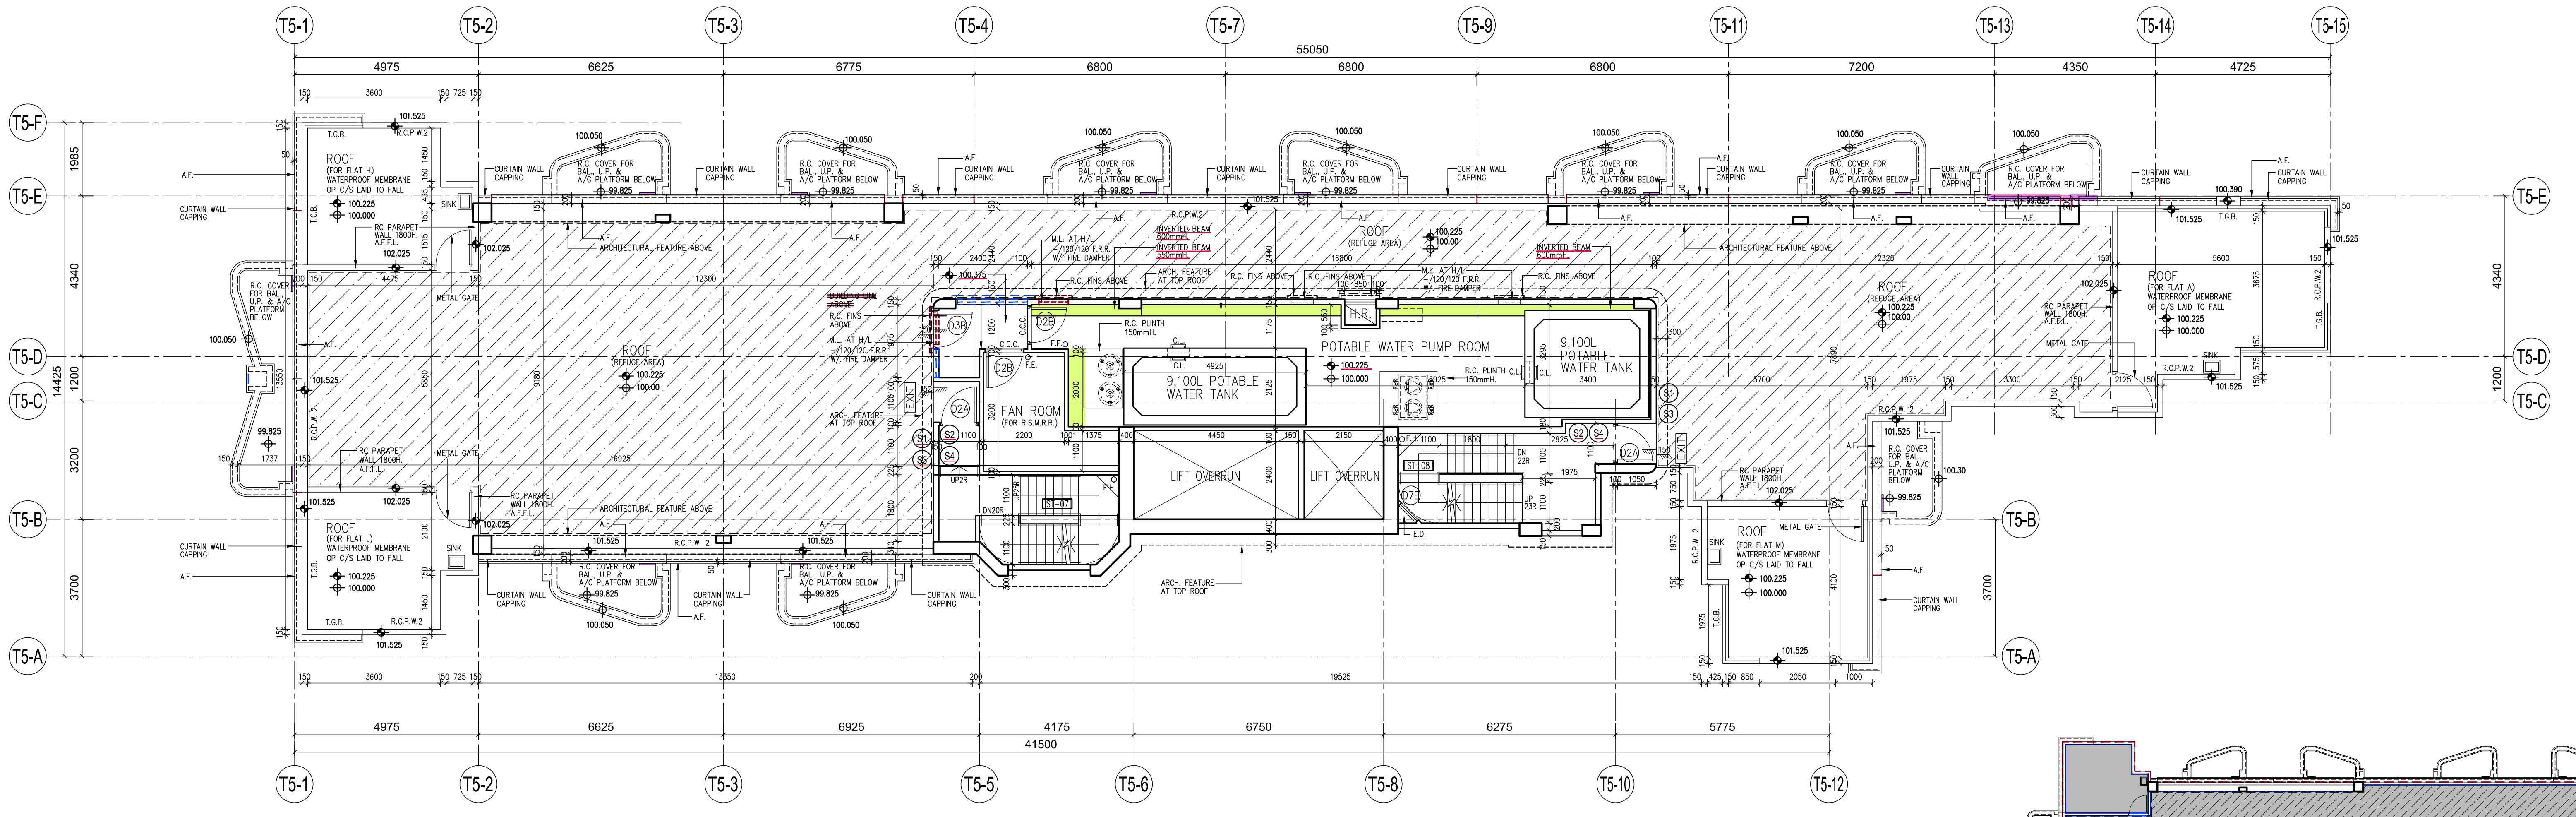
T5-1
T5-2
T5-3
T5-4
T5-7
T5-9
T5-11
T5-13
T5-14
T5-15
T5-F
T5-E
T5-D
T5-C
T5-B
T5-A
T5-5
T5-6
T5-8
T5-10
T5-12
55050
41500
ROOF (REFUGE AREA)
POTABLE WATER PUMP ROOM
9,100L POTABLE WATER TANK
FAN ROOM
LIFT OVERRUN
CURTAIN WALL CAPPING
ARCHITECTURAL FEATURE ABOVE

ROOF PLAN – TOWER 5

LEGEND:

- (S1) REFUGE FLOOR NOTICE
- (S2) STAIR NO. SIGN
- (S3) DIRECTIONAL SIGN TO EXIT STAIRCASE
- (S4) A SIGN INDICATING THE ENTRANCE TO THE REFUGE FLOOR
- ▨ NET REFUGE AREA = 245.916 m^2

THE PERCENTAGE OF THE NET REFUGE AREA

THE G.A. OF THE LARGEST FLOOR PLATE = 490.398 m^2
PERCENTAGE OF REFUGE AREA PROVIDED = 245.916 / 490.398 x 100%
= 50.146 % > 50% (REQUIRED)

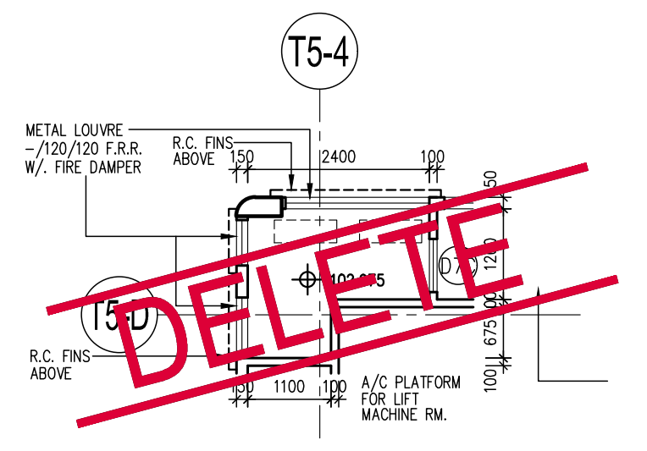
T5-4
DELETE
METAL LOUVRE
R.C. FINS ABOVE
A/C PLATFORM

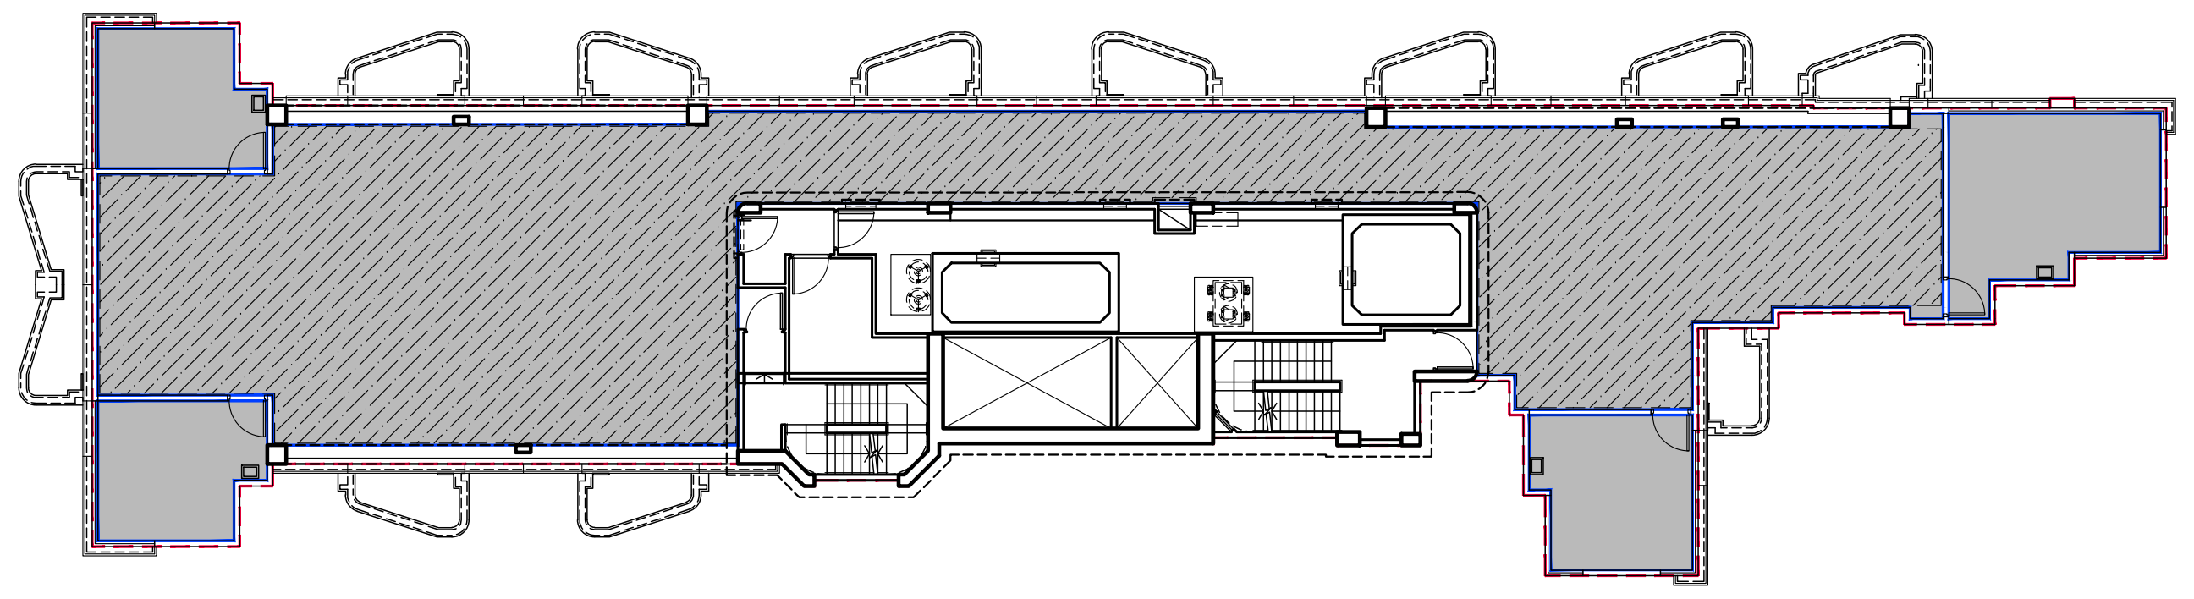

TOWER 5 ROOF FLOOR DIAGRAM

(UNDER PLANNING DEPARTMENT)
SCALE 1:200

– –	AREA OF ROOF	= 485.949 m^2
▨	AREA OF ROOF W/O. ROOF TOP STRUCTURE	= 323.718 m^2 (66.616 % OF ROOF AREA)

B.D. Ref : BD 2/4024/21
BIM Ref : - --
F.S.D. Ref : - --
D.L.O. Ref : - --

Rev.	Description	Drawn	Checked	Approved	Date
-	1st Submission	WY	AW	AL	07/2022
A	2nd Submission	WY	AW	AL	11/2022
B	1st Amendment	TWM	AW	AL	04/2023
C	2nd Amendment	TWM	AW	AL	12/2023
D	3rd Amendment	TWM	AW	AL	04/2024
D	3rd Amendment (Re-submission)	TWM	AW	AL	05/2024
E	5th Amendment	TWM	AW	AL	12/2024
E	5th Amendment (Re-submission)	TWM	AW	AL	02/2025
F	8th Amendment	TWM	AW	AL	05/2025
G	9th Amendment	TWM	AW	AL	08/2025
G	9th Amendment (Re-submission)	TWM	AW	AL	10/2025
H	10th Amendment	TWM	AW	AL	12/2025
I	11th Amendment	TWM	AW	AL	02/2026

Type II works
The works shown on these plans are Type II works (Building Amendment) in respect of which consent is applied for the purpose of Fast Track consent application under regulation 33 of the Building (Administration) Regulations.

RONALD LU & PARTNERS
呂 元 祥 建 築 師 事 務 所

Project Title :
PROPOSED DEVELOPMENT
AT BAILEY STREET
& WING KWONG STREET
TO KWA WAN, KOWLOON

Drawing Title :
ROOF FLOOR PLAN
FOR TOWER 5

Drawn By	TWM	Date	08/2025
Checked By	AW	Date	08/2025
Approved By	AL	Date	08/2025
Project No.	21163KL	Issue Date	08/2025

File Path :
U:\Studio_B\Proj_Data\2021\21163KL_Bailey Street & Wing Kwong Street\DRAWING\SUB\BD\GBP_13 (Final Amendment)_Hand Amend\PLOT\A_GBP_18.dwg

Scale 1:100 By CAD

Drawing Number : A/GBP/18
Revision Number : I

Drawing Purpose
Buildings Department
Amended Plan

Digitally signed by
LEUNG Kit Man Andy
AP(A) 80/85
16 March 2026

Received on
16 March 2026

Plan Approved
(Digitally Signed)
TSOI Lap-san, Lapson
Senior Building Surveyor
for BUILDING AUTHORITY
17 March 2026

Note: This plan has been processed on a curtailed check basis under the centralized processing system as promulgated in PNAP ADM-19. The duties of the authorized person, registered structural engineer and/or registered geotechnical engineer concerned as specified under section 4(3)(b) and the provision of section 14(2)(c) of the Buildings Ordinance are of particular relevance in this regard.